


TITLE BLOCK VERSION: 20210830
MODEL: A:\models\25695.00_Cooper_Miller_Campus_Plan_2023.dwg
PRINT DATE: 11/21/2025 3:25:29 PM
TEMPLATE VERSION: 23.0.3
C:\H1-Tower-A
Exterior: 2023.rvt

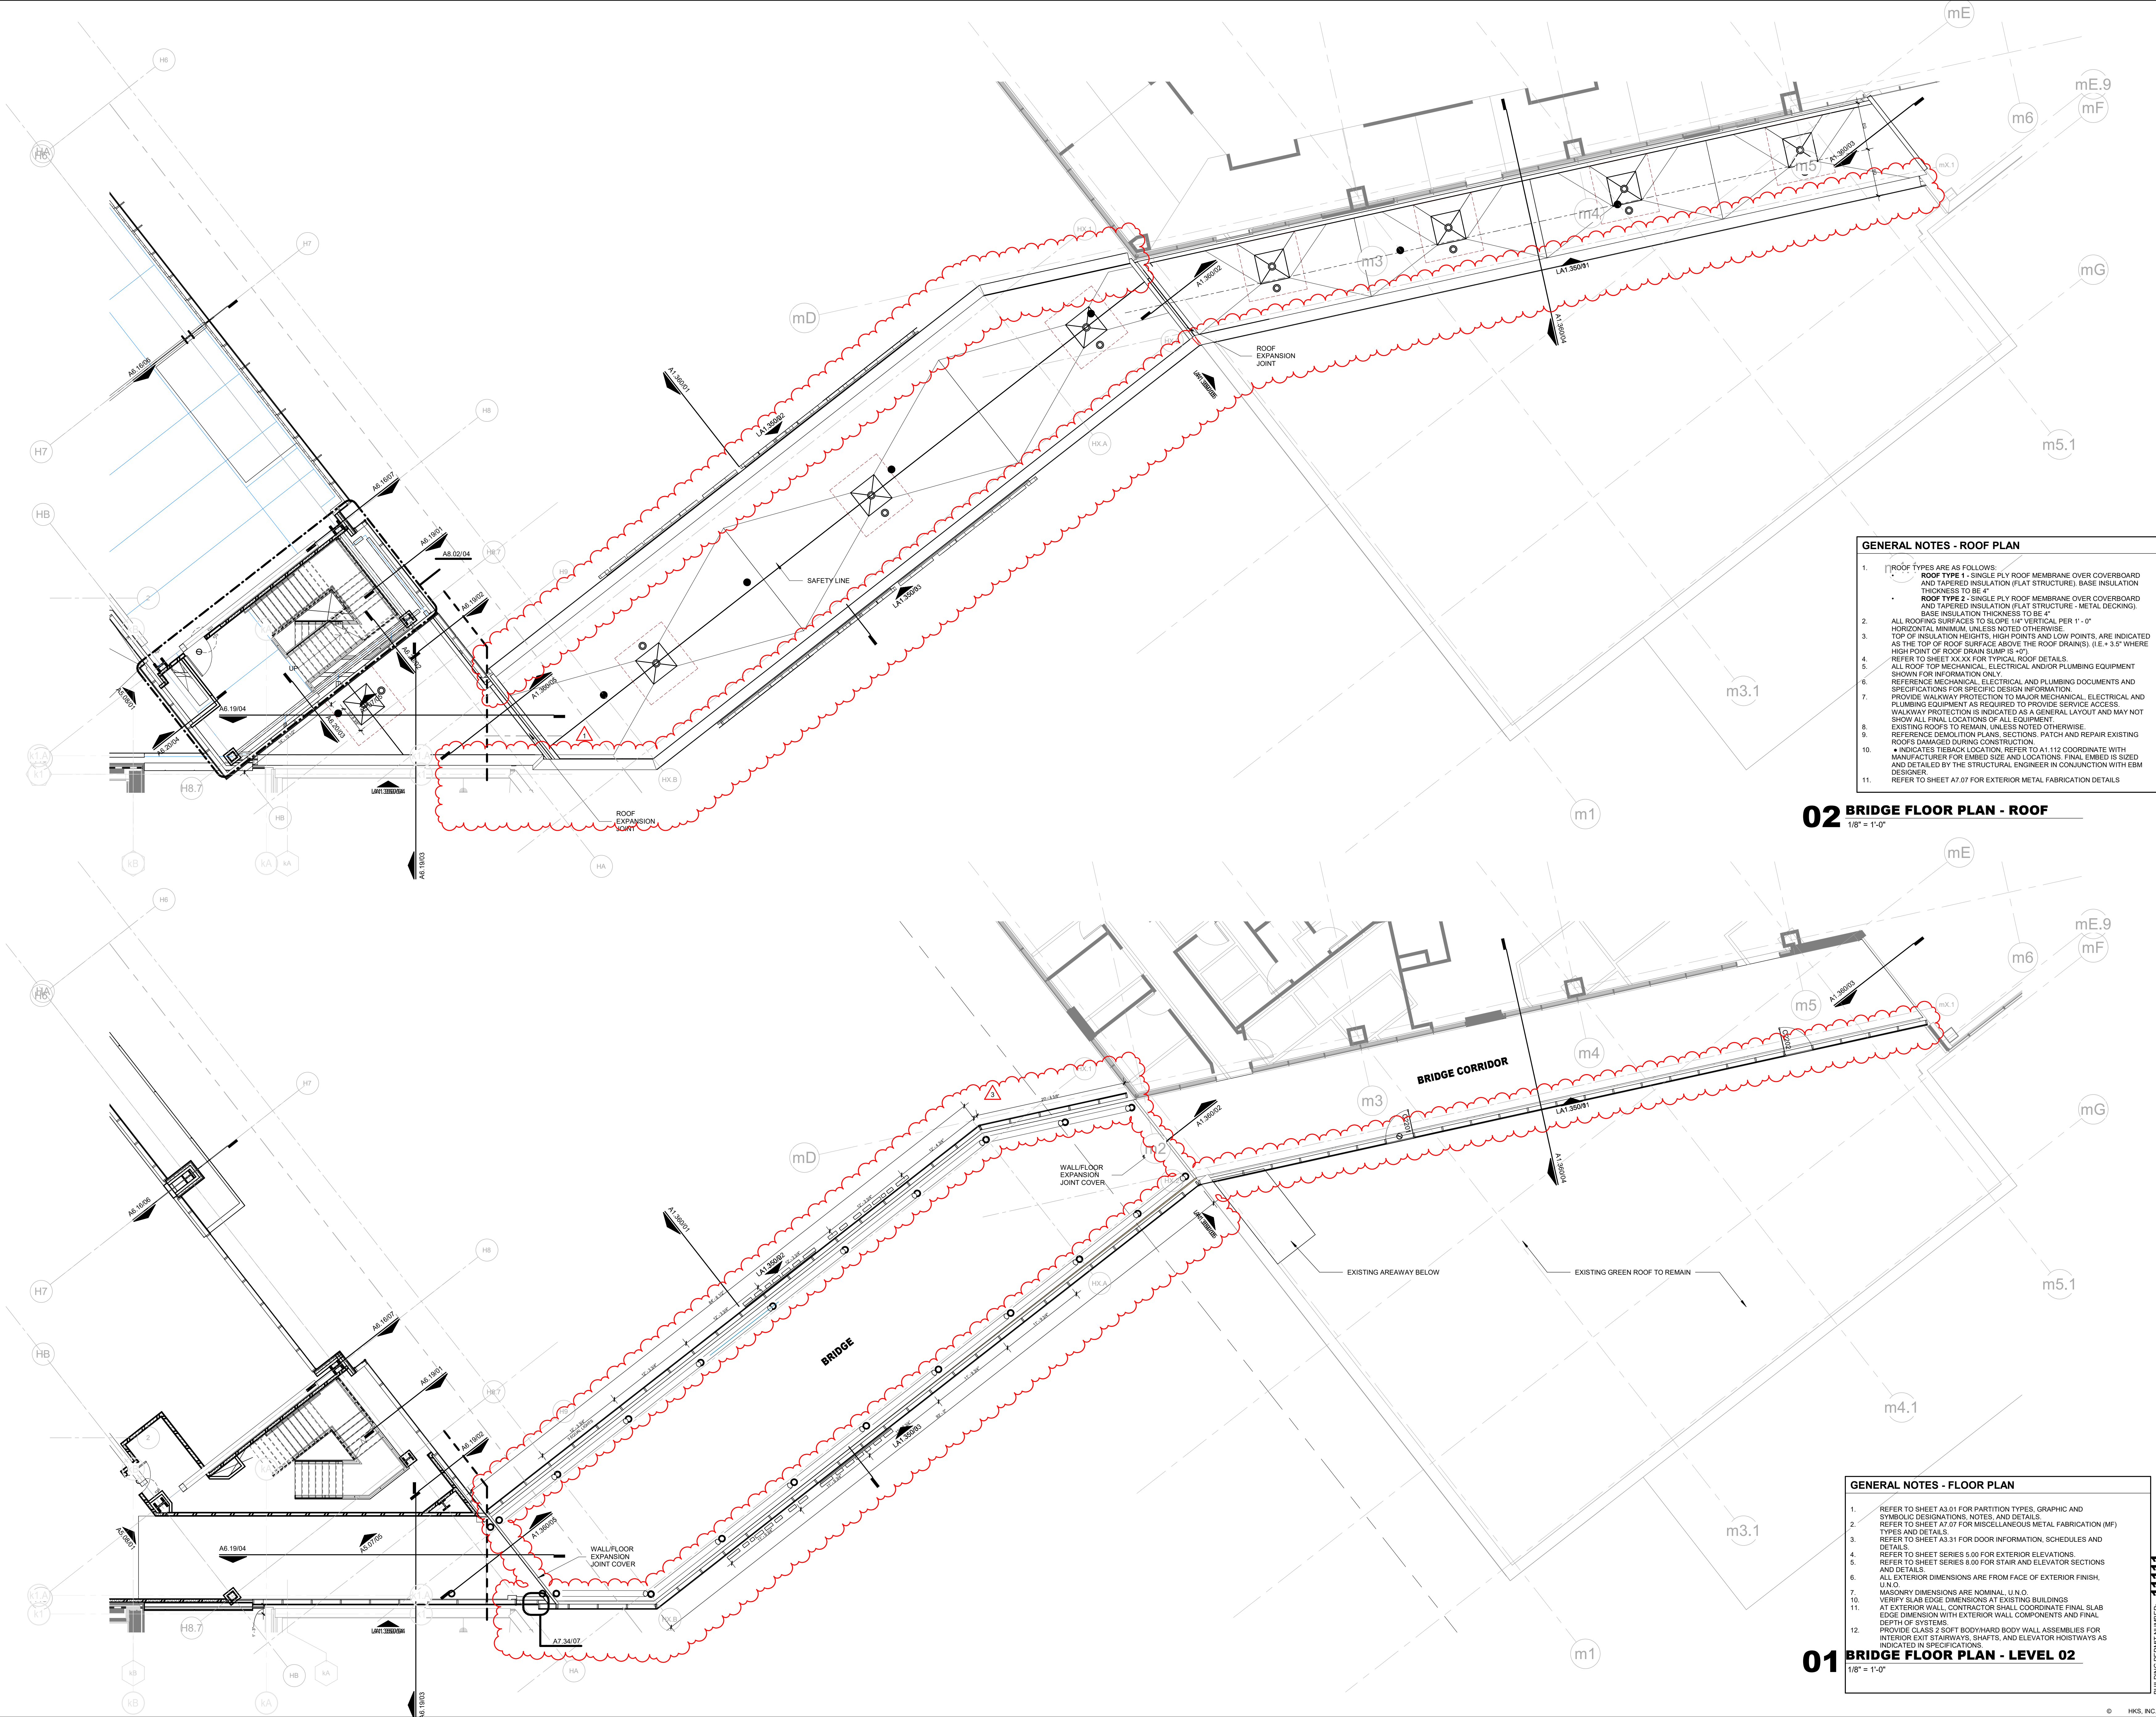

- GENERAL NOTES - ROOF PLAN**
1. ROOF TYPES ARE AS FOLLOWS:
ROOF TYPE 1 - SINGLE PLY ROOF MEMBRANE OVER COVERBOARD AND TAPERED INSULATION (FLAT STRUCTURE); BASE INSULATION THICKNESS TO BE 4".
ROOF TYPE 2 - SINGLE PLY ROOF MEMBRANE OVER COVERBOARD AND TAPERED INSULATION (FLAT STRUCTURE - METAL DECKING); BASE INSULATION THICKNESS TO BE 4".
 2. ALL ROOFING SURFACES TO SLOPE 1/4" VERTICAL PER 1' - 0" HORIZONTAL MINIMUM, UNLESS NOTED OTHERWISE.
 3. TOP OF INSULATION HEIGHTS, HIGH POINTS AND LOW POINTS, ARE INDICATED AS THE TOP OF ROOF SURFACE ABOVE THE ROOF DRAINS). (I.E. + 3.5' WHERE HIGH POINT OF ROOF DRAIN SUMP IS +0').
 4. REFER TO SHEET XX.XX FOR TYPICAL ROOF DETAILS.
 5. ALL ROOF TOP MECHANICAL, ELECTRICAL, AND/OR PLUMBING EQUIPMENT SHOWN FOR INFORMATION ONLY.
 6. PROVIDE WALKWAY PROTECTION TO MAJOR MECHANICAL, ELECTRICAL AND PLUMBING EQUIPMENT AS REQUIRED TO PROVIDE SERVICE ACCESS.
 7. WALKWAY PROTECTION IS INDICATED AS A GENERAL LAYOUT AND MAY NOT SHOW ALL FINAL LOCATIONS OF ALL EQUIPMENT.
 8. EXISTING ROOFS TO REMAIN, UNLESS NOTED OTHERWISE.
 9. REFERENCE DEMOLITION PLANS, SECTIONS, PATCH AND REPAIR EXISTING ROOFS DAMAGED DURING CONSTRUCTION.
 10. * INDICATES TIEBACK LOCATION, REFER TO A1.112 COORDINATE WITH MANUFACTURER FOR EMBED SIZE AND LOCATIONS, FINAL EMBED IS SIZED AND DETAILED BY THE STRUCTURAL ENGINEER IN CONJUNCTION WITH EBM DESIGNER.
 11. REFER TO SHEET A7.07 FOR EXTERIOR METAL FABRICATION DETAILS.

02 BRIDGE FLOOR PLAN - ROOF

1/8" = 1'-0"

- GENERAL NOTES - FLOOR PLAN**
1. REFER TO SHEET A3.01 FOR PARTITION TYPES, GRAPHIC AND SYMBOLIC DESIGNATIONS, NOTES, AND DETAILS.
 2. REFER TO SHEET A7.07 FOR MISCELLANEOUS METAL FABRICATION (MF) TYPES AND DETAILS.
 3. REFER TO SHEET A3.31 FOR DOOR INFORMATION, SCHEDULES AND DETAILS.
 4. REFER TO SHEET SERIES 5.00 FOR EXTERIOR ELEVATIONS.
 5. REFER TO SHEET SERIES 8.00 FOR STAIR AND ELEVATOR SECTIONS AND DETAILS.
 6. ALL EXTERIOR DIMENSIONS ARE FROM FACE OF EXTERIOR FINISH, UNLESS NOTED OTHERWISE.
 7. MASONRY DIMENSIONS ARE NOMINAL, UNLESS NOTED OTHERWISE.
 8. VERIFY SLAB EDGE DIMENSIONS AT EXISTING BUILDINGS.
 9. AT EXTERIOR WALL, CONTRACTOR SHALL COORDINATE FINAL SLAB EDGE DIMENSION WITH EXTERIOR WALL COMPONENTS AND FINAL DEPTH OF SYSTEMS.
 10. PROVIDE CLASS 2 SOFT BODY/HARD BODY WALL ASSEMBLIES FOR INTERIOR EXIT STAIRWAYS, SHAFTS, AND ELEVATOR HOISTWAYS AS INDICATED IN SPECIFICATIONS.
 11. REFER TO SHEET A7.07 FOR EXTERIOR METAL FABRICATION DETAILS.

01 BRIDGE FLOOR PLAN - LEVEL 02

1/8" = 1'-0"

RESERVE FOR DCA STAMP




ARCHITECT
HKS, P.C.
1250 I (EYE) STREET NW, SUITE 600
WASHINGTON, DC 20005
ASSOCIATE ARCHITECT / INTERIOR DESIGNER
ARRAY
1 WEST ELM STREET, SUITE 500
CONSHOHOCKEN, PA 19028
STRUCTURAL ENGINEER
O'DONNELL & NACCARATO
701 MARKET ST., #6000
PHILADELPHIA, PA 19106
MEP-FP / LOW VOLTAGE ENGINEER
BR-A CONSULTING ENGINEERS
2401 WALNUT ST SUITE 701
PHILADELPHIA, PA 19103
HIGHLAND ASSOCIATES
102 HIGHLAND AVE
CLARKS SUMMIT, PA 18411



OWNER
COOPER UNIVERSITY HEALTHCARE
1 COOPER PLAZA
CAMDEN, NJ 08103
PROJECT MANAGER
PURE PM
2026 RICHMOND STREET
PHILADELPHIA, PA 19134
CIVIL ENGINEER / LANDSCAPE
LANGAN
1818 MARKET STREET, SUITE 3300
PHILADELPHIA, PA 19103
SEAL & SINGATURE

KEY PLAN

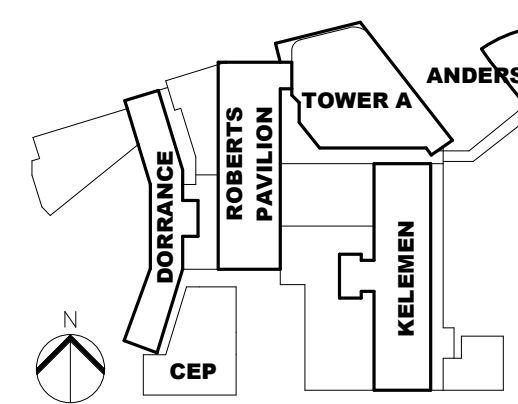

REVISION	DESCRIPTION	DATE
NO. 1	BULLETIN #4	04/28/2025
2	Revision 4 TBD	Date 4
3	RFI 0420	11/14/2025

HKS PROJECT NUMBER
25695.100
DATE
10/15/2024
ISSUE
CORE & SHELL PERMIT SET
SHEET TITLE
BRIDGE FLOOR PLAN


SHEET NO.

A1.301

BUILDING PERMIT NUMBER: 1111

© HKS, INC.

PRINT DATE: 11/21/2023 3:25:40 PM TEMPLATE VERSION: 23.0.3 MODEL: Alameda Docs 25695.000 - Cooper Medical Campus Plan 2023A - CHH Tower A, Exterior 2023.rvt TITLE BLOCK VERSION: 2010B30

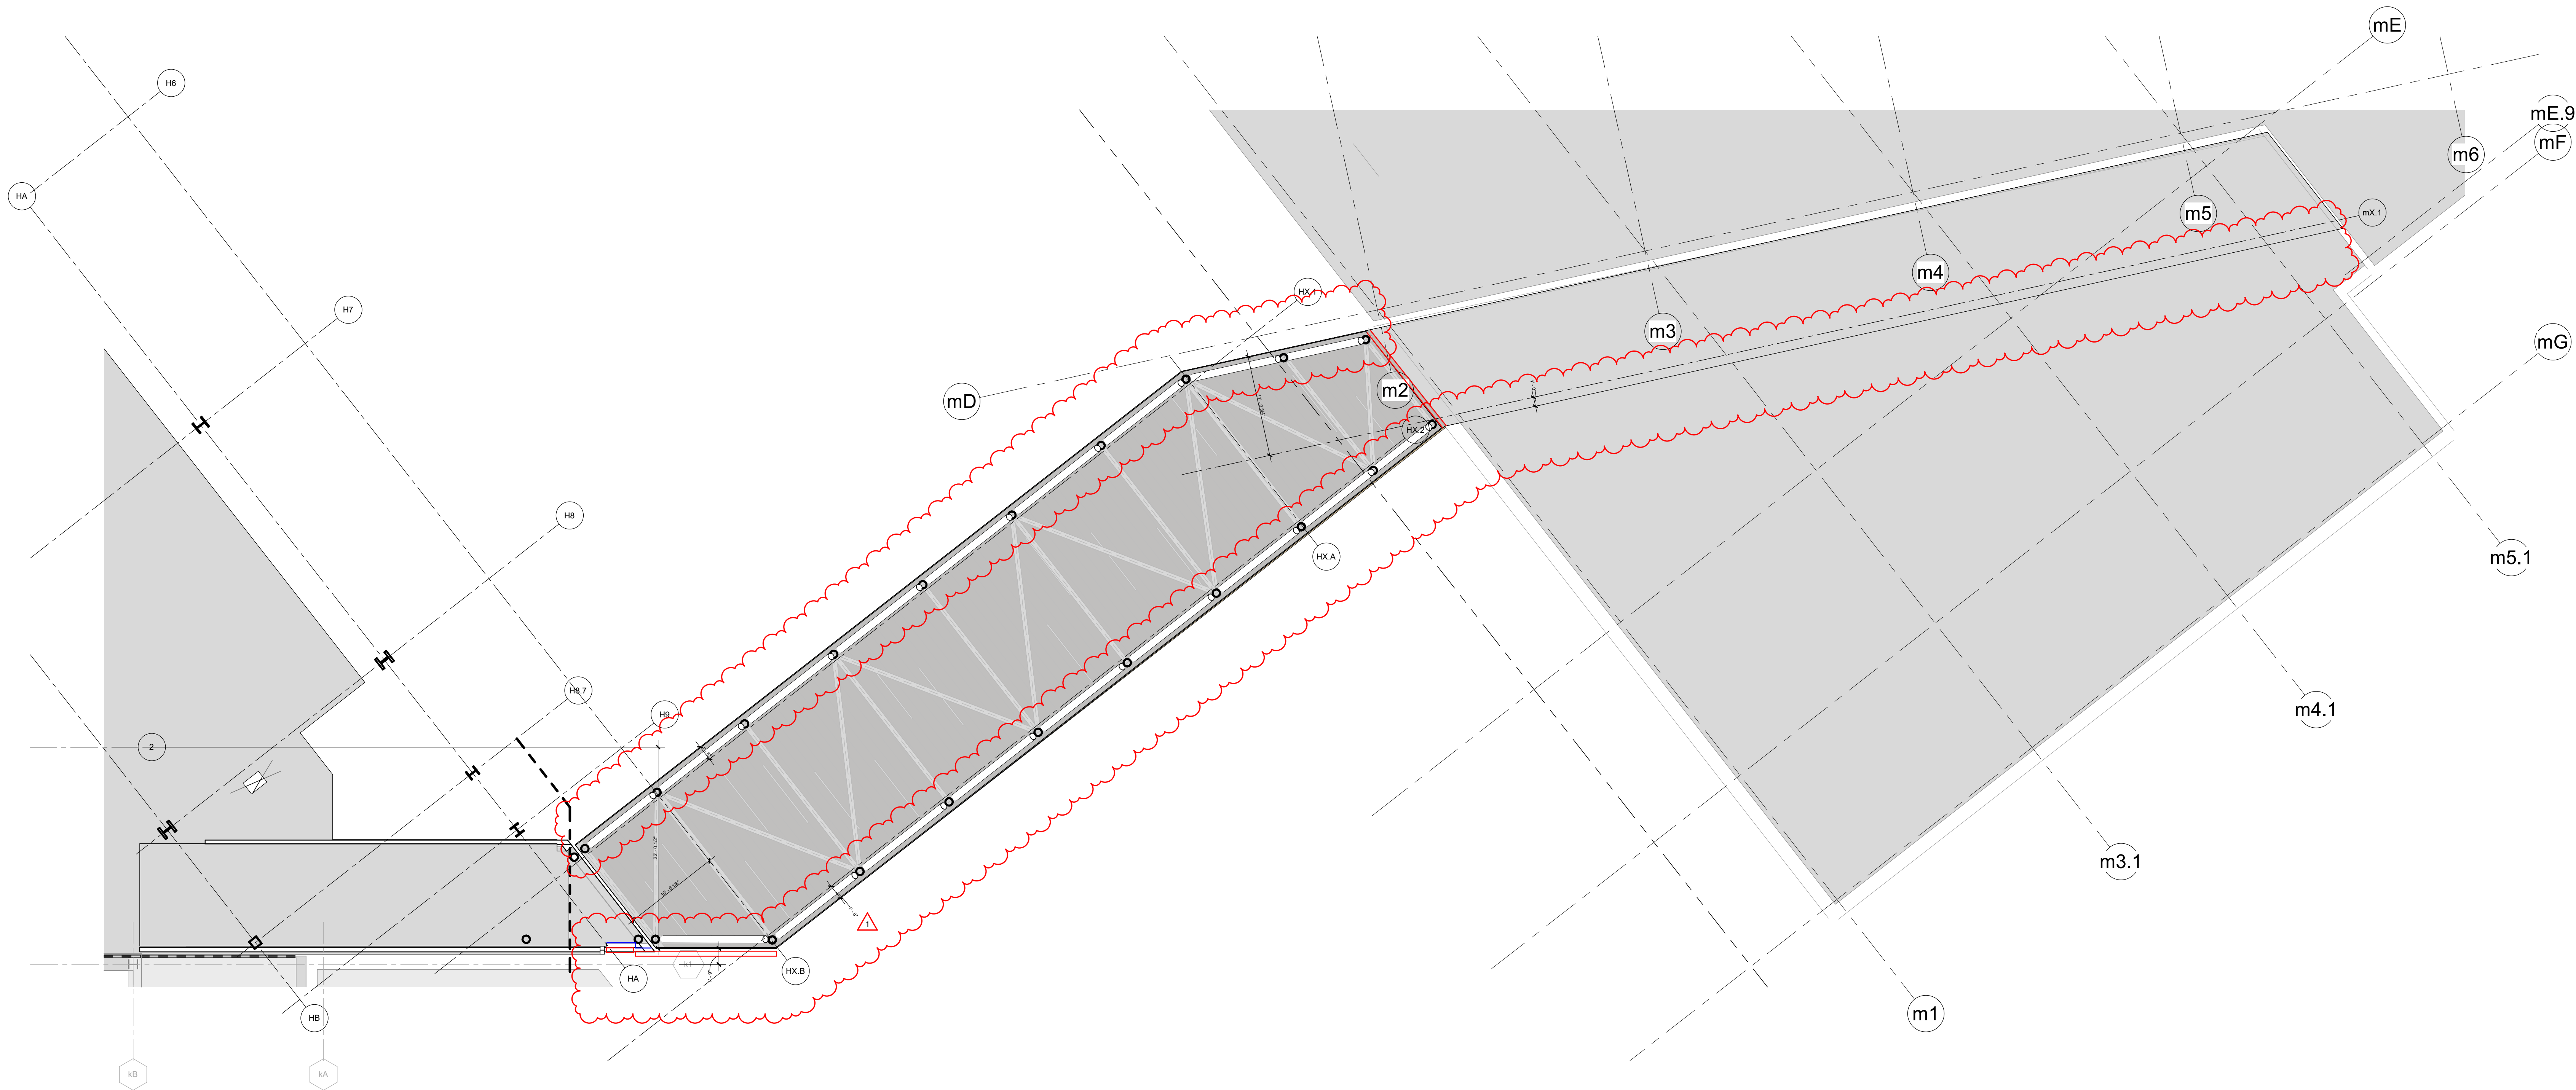

01 EOS PLAN - LEVEL 02
1/8" = 1'-0"


RESERVE FOR DCA STAMP



ARCHITECT
HKS, P.C.
1250 I (EYE) STREET NW, SUITE 600
WASHINGTON, DC 20005
ASSOCIATE ARCHITECT / INTERIOR DESIGNER
ARRAY
1 WEST ELM STREET, SUITE 500
CONSHOHOCKEN, PA 19428
STRUCTURAL ENGINEER
O'DONNELL & NACCARATO
701 MARKET ST, #6000
PHILADELPHIA, PA 19106
MEP-FP / LOW VOLTAGE ENGINEER
BR+A CONSULTING ENGINEERS
2401 WALNUT ST SUITE 701
PHILADELPHIA, PA 19103
HIGHLAND ASSOCIATES
102 HIGHLAND AVE
CLARKS SUMMIT, PA 18411




OWNER
COOPER UNIVERSITY HEALTHCARE
1 COOPER PLAZA
CAMDEN, NJ 08103
PROJECT MANAGER
PURE PM
2026 RICHMOND STREET
PHILADELPHIA, PA 19134
CIVIL ENGINEER / LANDSCAPE
LANGAN
1818 MARKET STREET, SUITE 3300
PHILADELPHIA, PA 19103
SEAL & SIGNATURE

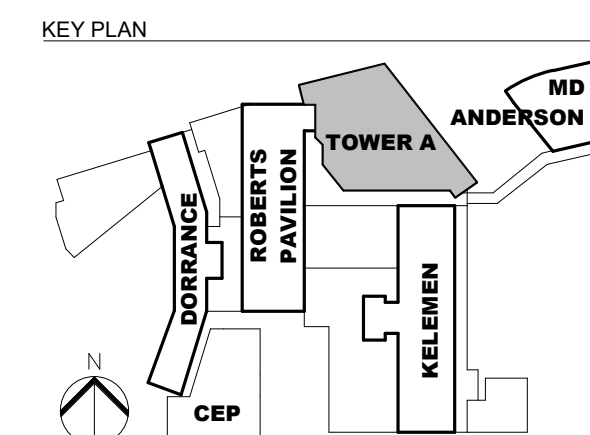

REVISION	NO.	DESCRIPTION	DATE
1	BULLETIN #4		04/28/2025
2	RFI 0420		11/14/2025

HKS PROJECT NUMBER
25695.100
DATE
10/15/2024
ISSUE
CORE & SHELL PERMIT SET
SHEET TITLE
BRIDGE EDGE OF SLAB PLAN

BUILDING PERMIT NUMBER: **1111**
SHEET NO.
A1.320

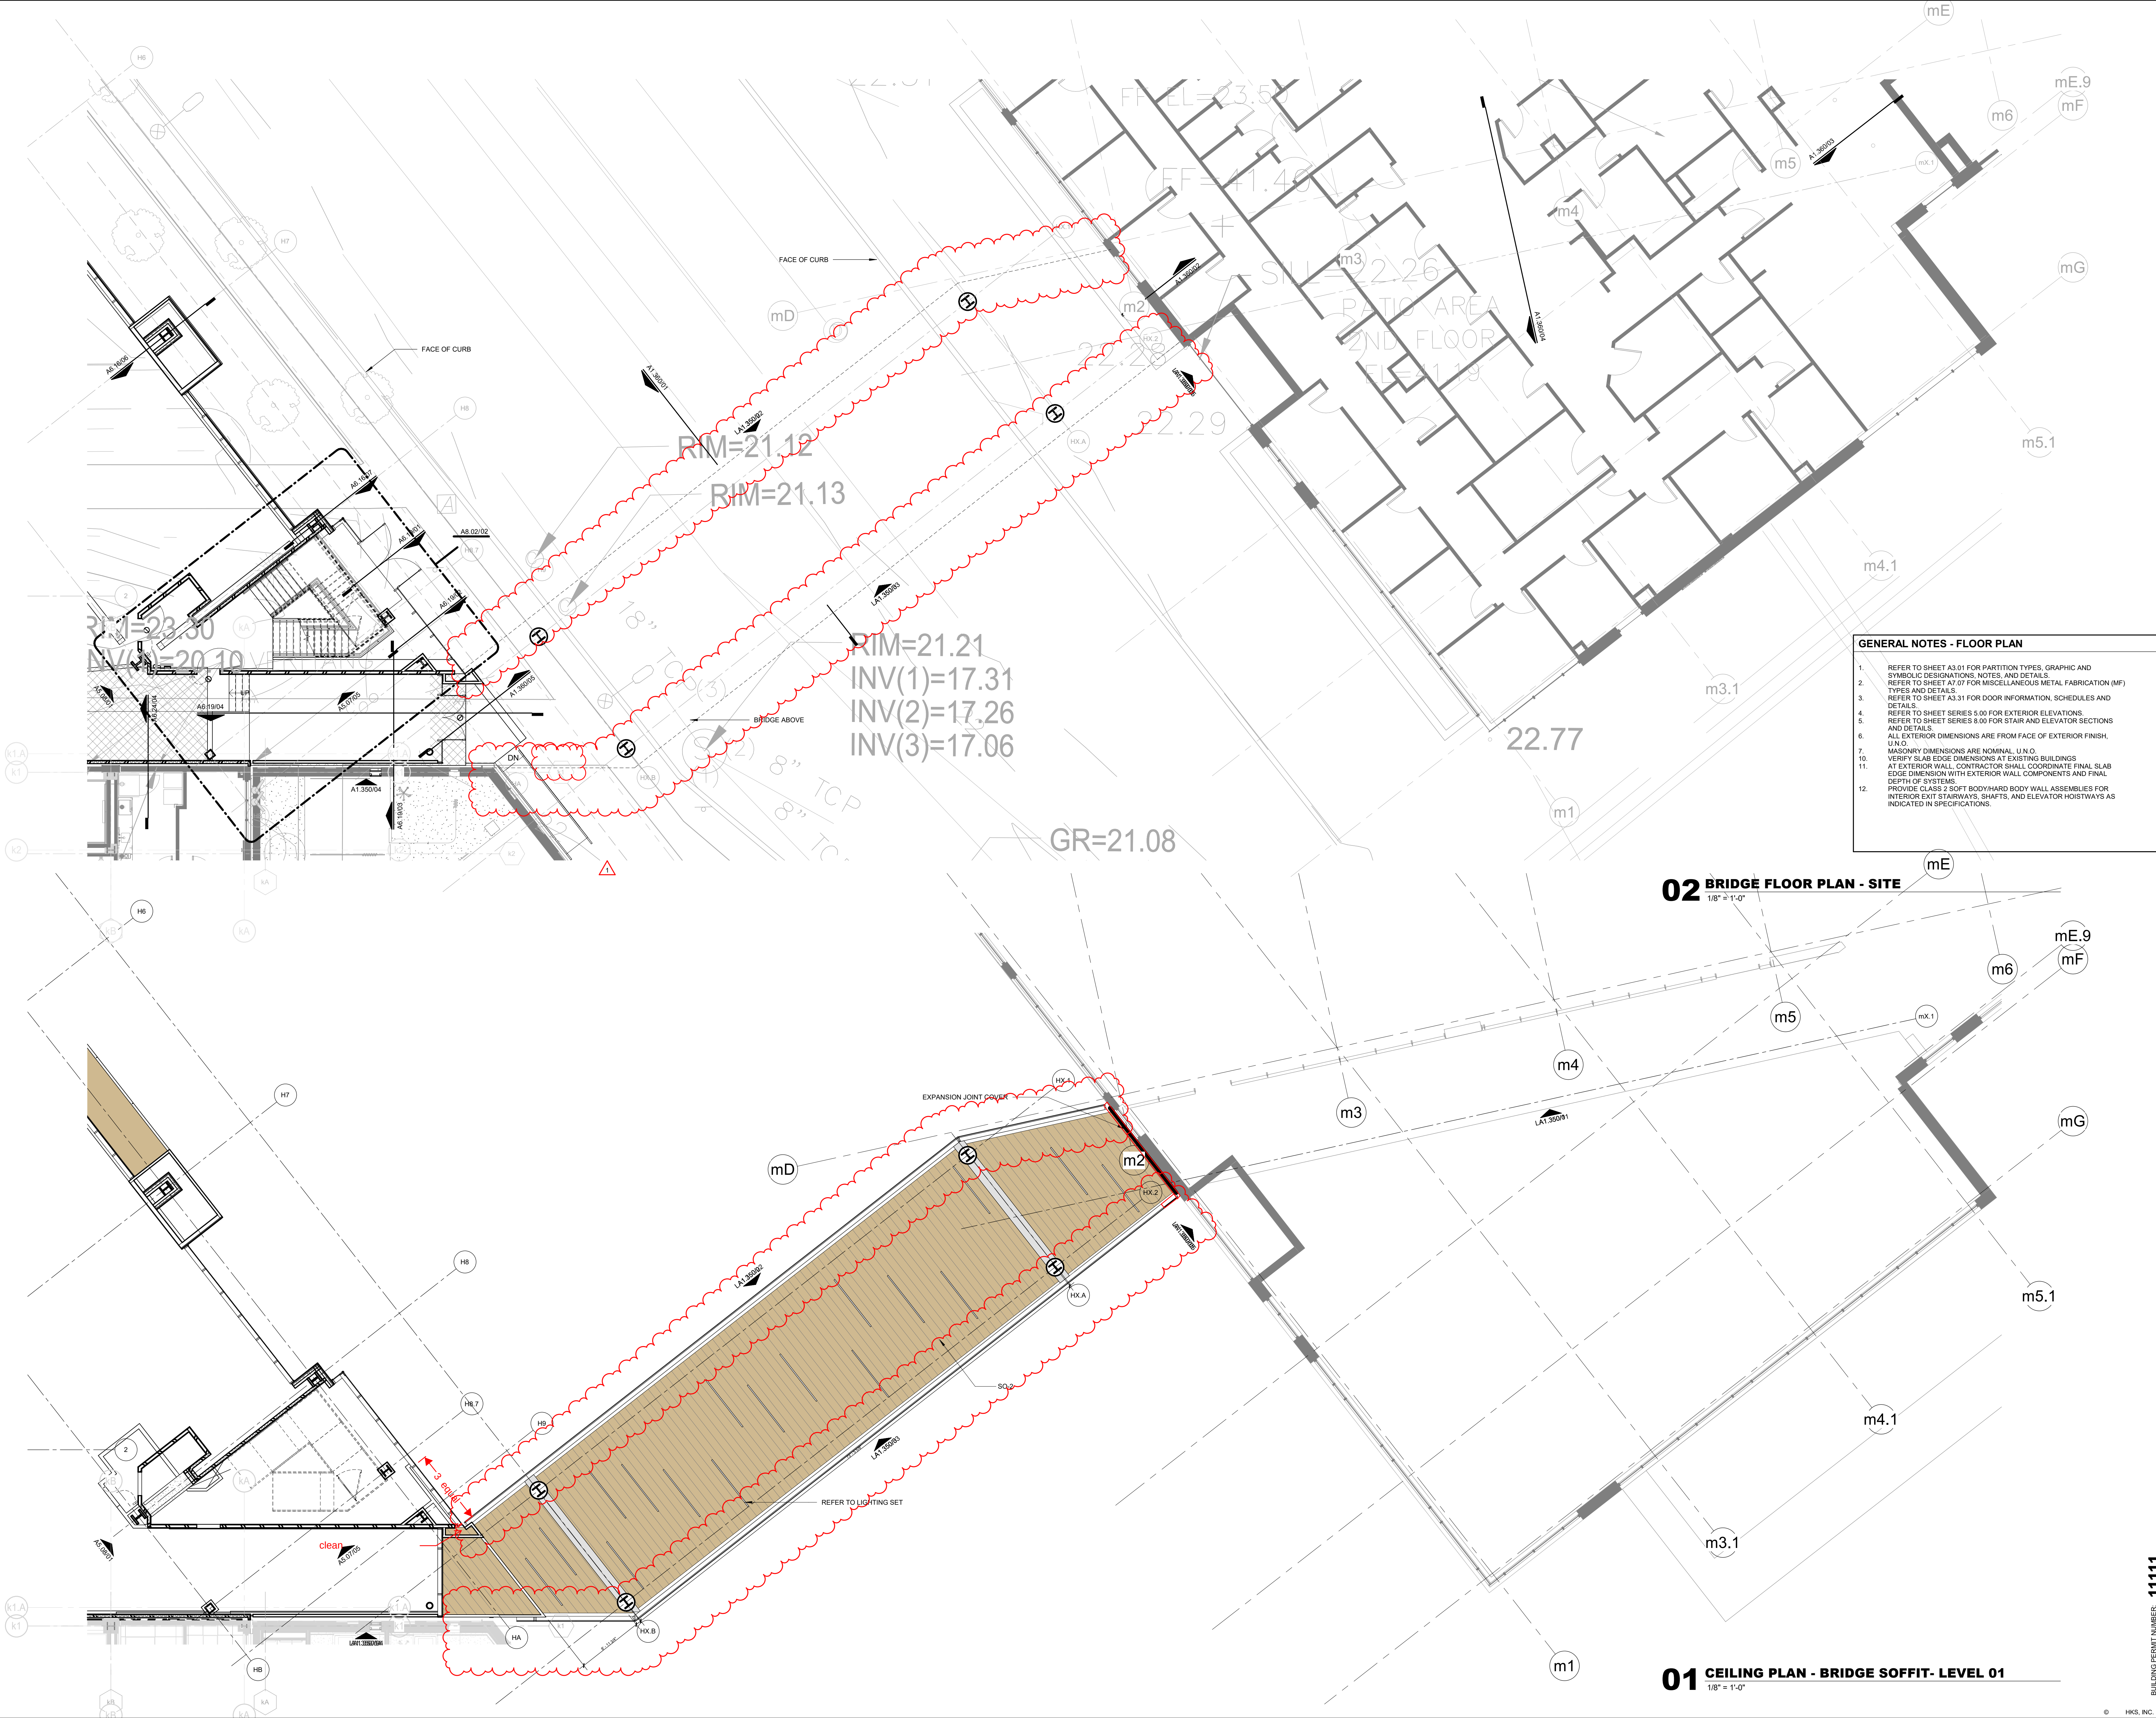

GENERAL NOTES - FLOOR PLAN


- REFER TO SHEET A3.01 FOR PARTITION TYPES, GRAPHIC AND SYMBOLIC DESIGNATIONS, NOTES, AND DETAILS.
- REFER TO SHEET A7.07 FOR MISCELLANEOUS METAL FABRICATION (MF) TYPES AND DETAILS.
- REFER TO SHEET A3.31 FOR DOOR INFORMATION, SCHEDULES AND DETAILS.
- REFER TO SHEET SERIES 5.00 FOR EXTERIOR ELEVATIONS.
- REFER TO SHEET SERIES 8.00 FOR STAIR AND ELEVATOR SECTIONS AND DETAILS.
- ALL EXTERIOR DIMENSIONS ARE FROM FACE OF EXTERIOR FINISH, U.N.O.
- MASSORY DIMENSIONS ARE NOMINAL, U.N.O.
- VERIFY SLAB EDGE DIMENSIONS AT EXISTING BUILDINGS.
- AT EXTERIOR WALL, CONTRACTOR SHALL COORDINATE FINAL SLAB EDGE DIMENSION WITH EXTERIOR WALL COMPONENTS AND FINAL DEPTH OF SYSTEMS.
- PROVIDE CLASS 2 SOFT BODY/HARD BODY WALL ASSEMBLIES FOR INTERIOR EXIT STAIRWAYS, SHAFTS, AND ELEVATOR HOISTWAYS AS INDICATED IN SPECIFICATIONS.

RESERVE FOR DCA STAMP

HKS
ARRAY
ARCHITECT
HKS, P.C.
1250 I (EYE) STREET NW, SUITE 600
WASHINGTON, DC 20005
ASSOCIATE ARCHITECT / INTERIOR DESIGNER
ARRAY
1 WEST ELM STREET, SUITE 500
CONSHOHOCKEN, PA 19428
STRUCTURAL ENGINEER
O'DONNELL & NACCARATO
701 MARKET ST., #6000
PHILADELPHIA, PA 19106
MEP-FP / LOW VOLTAGE ENGINEER
BR-A CONSULTING ENGINEERS
2401 WALNUT ST SUITE 701
PHILADELPHIA, PA 19103
HIGHLAND ASSOCIATES
102 HIGHLAND AVE
CLARKS SUMMIT, PA 18411

Cooper
University Health Care
COOPER UNIVERSITY HOSPITAL - TOWER A
PROJECT ADDRESS: 1 COOPER PLAZA, CAMDEN, NJ 08103

OWNER
COOPER UNIVERSITY HEALTHCARE
1 COOPER PLAZA
CAMDEN, NJ 08103
PROJECT MANAGER
PURE PM
2026 RICHMOND STREET
PHILADELPHIA, PA 19134
CIVIL ENGINEER / LANDSCAPE
LANGAN
1818 MARKET STREET, SUITE 3300
PHILADELPHIA, PA 19103
SEAL & SIGNATURE

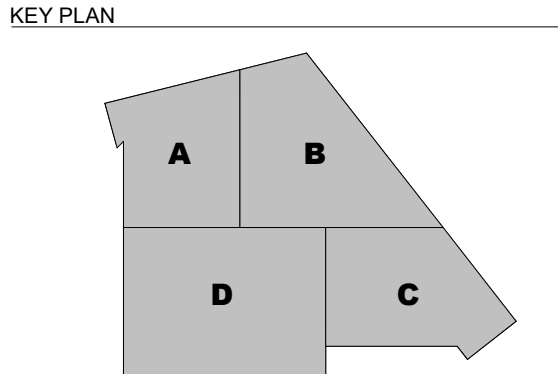


REVISION	NO.	DESCRIPTION	DATE
1	BULLETIN #4		04/28/2025
2	RFI 0420		11/14/2025

HKS PROJECT NUMBER
25695.100
DATE
10/15/2024
ISSUE
CORE & SHELL PERMIT SET
SHEET TITLE
BRIDGE CEILING PLAN & SITE PLAN


SHEET NO.
A1.340

BUILDING PERMIT NUMBER: 1111


TITLE BLOCK VERSION: 20210830
MODEL: Autodesk Docs (25695.00) Cooper Medical Campus Plan 2023A CHAT TowerA Exterior 2023.rvt
PRINT DATE: 1/21/2025 3:25:52 PM TEMPLATE VERSION: 23.0.3
BUILDING PERMIT NUMBER: 1111
© HKS, INC.

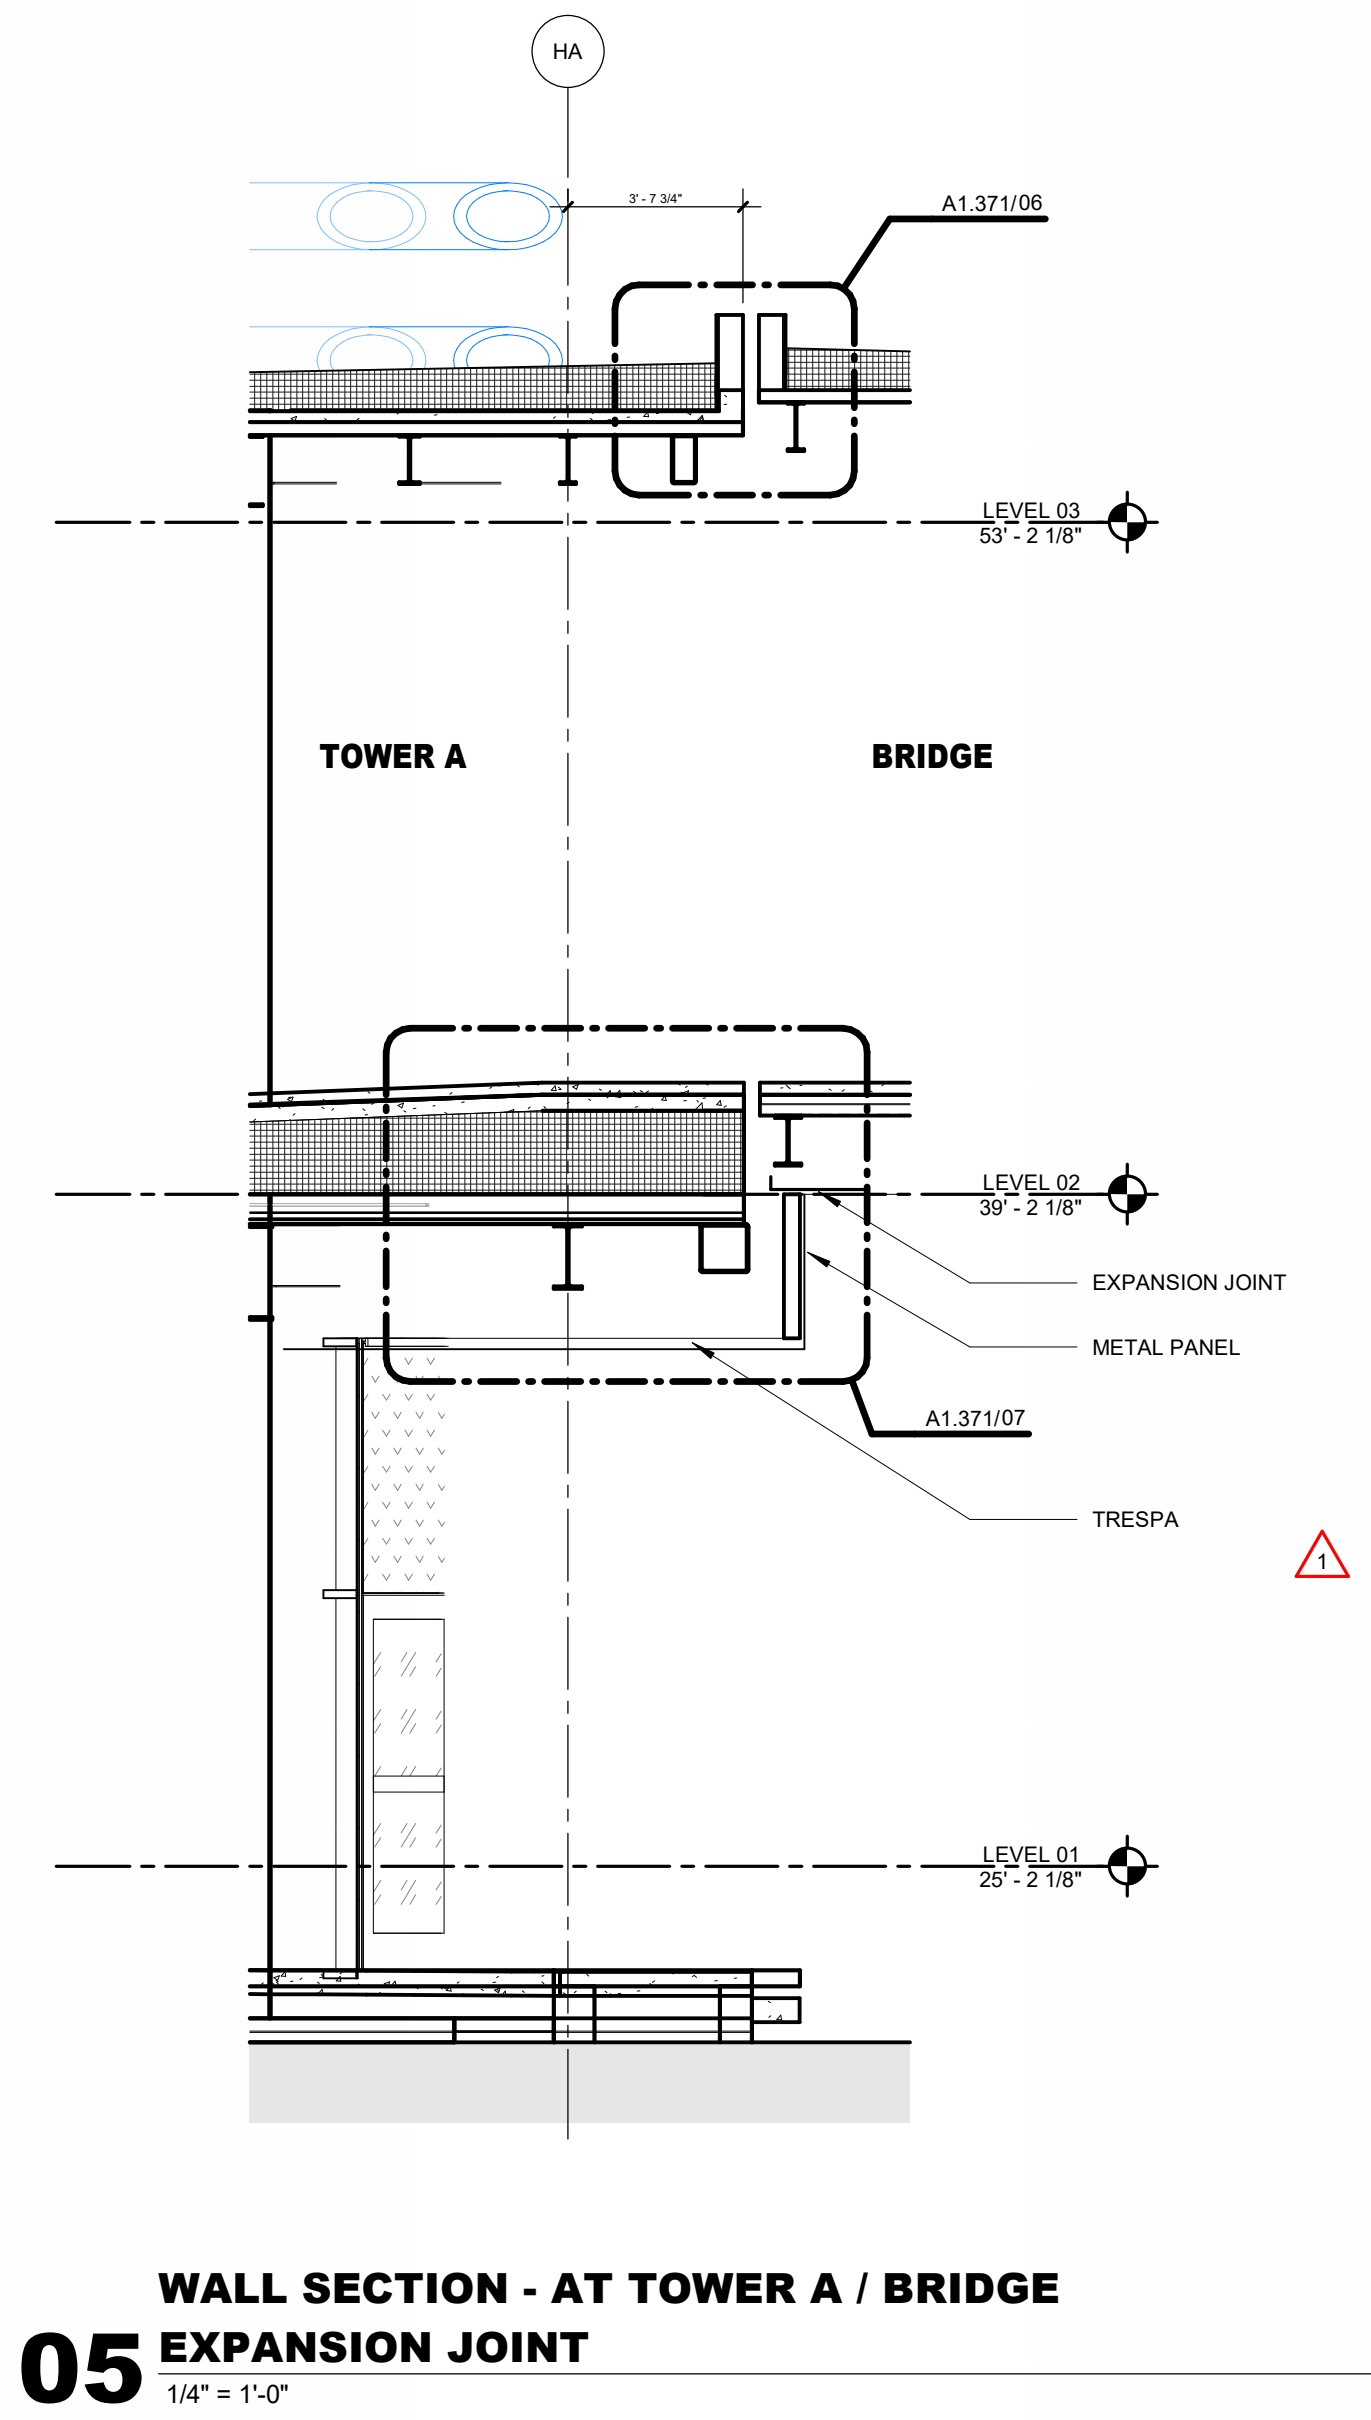


05 WALL SECTION - AT TOWER A / BRIDGE EXPANSION JOINT
1/4" = 1'-0"

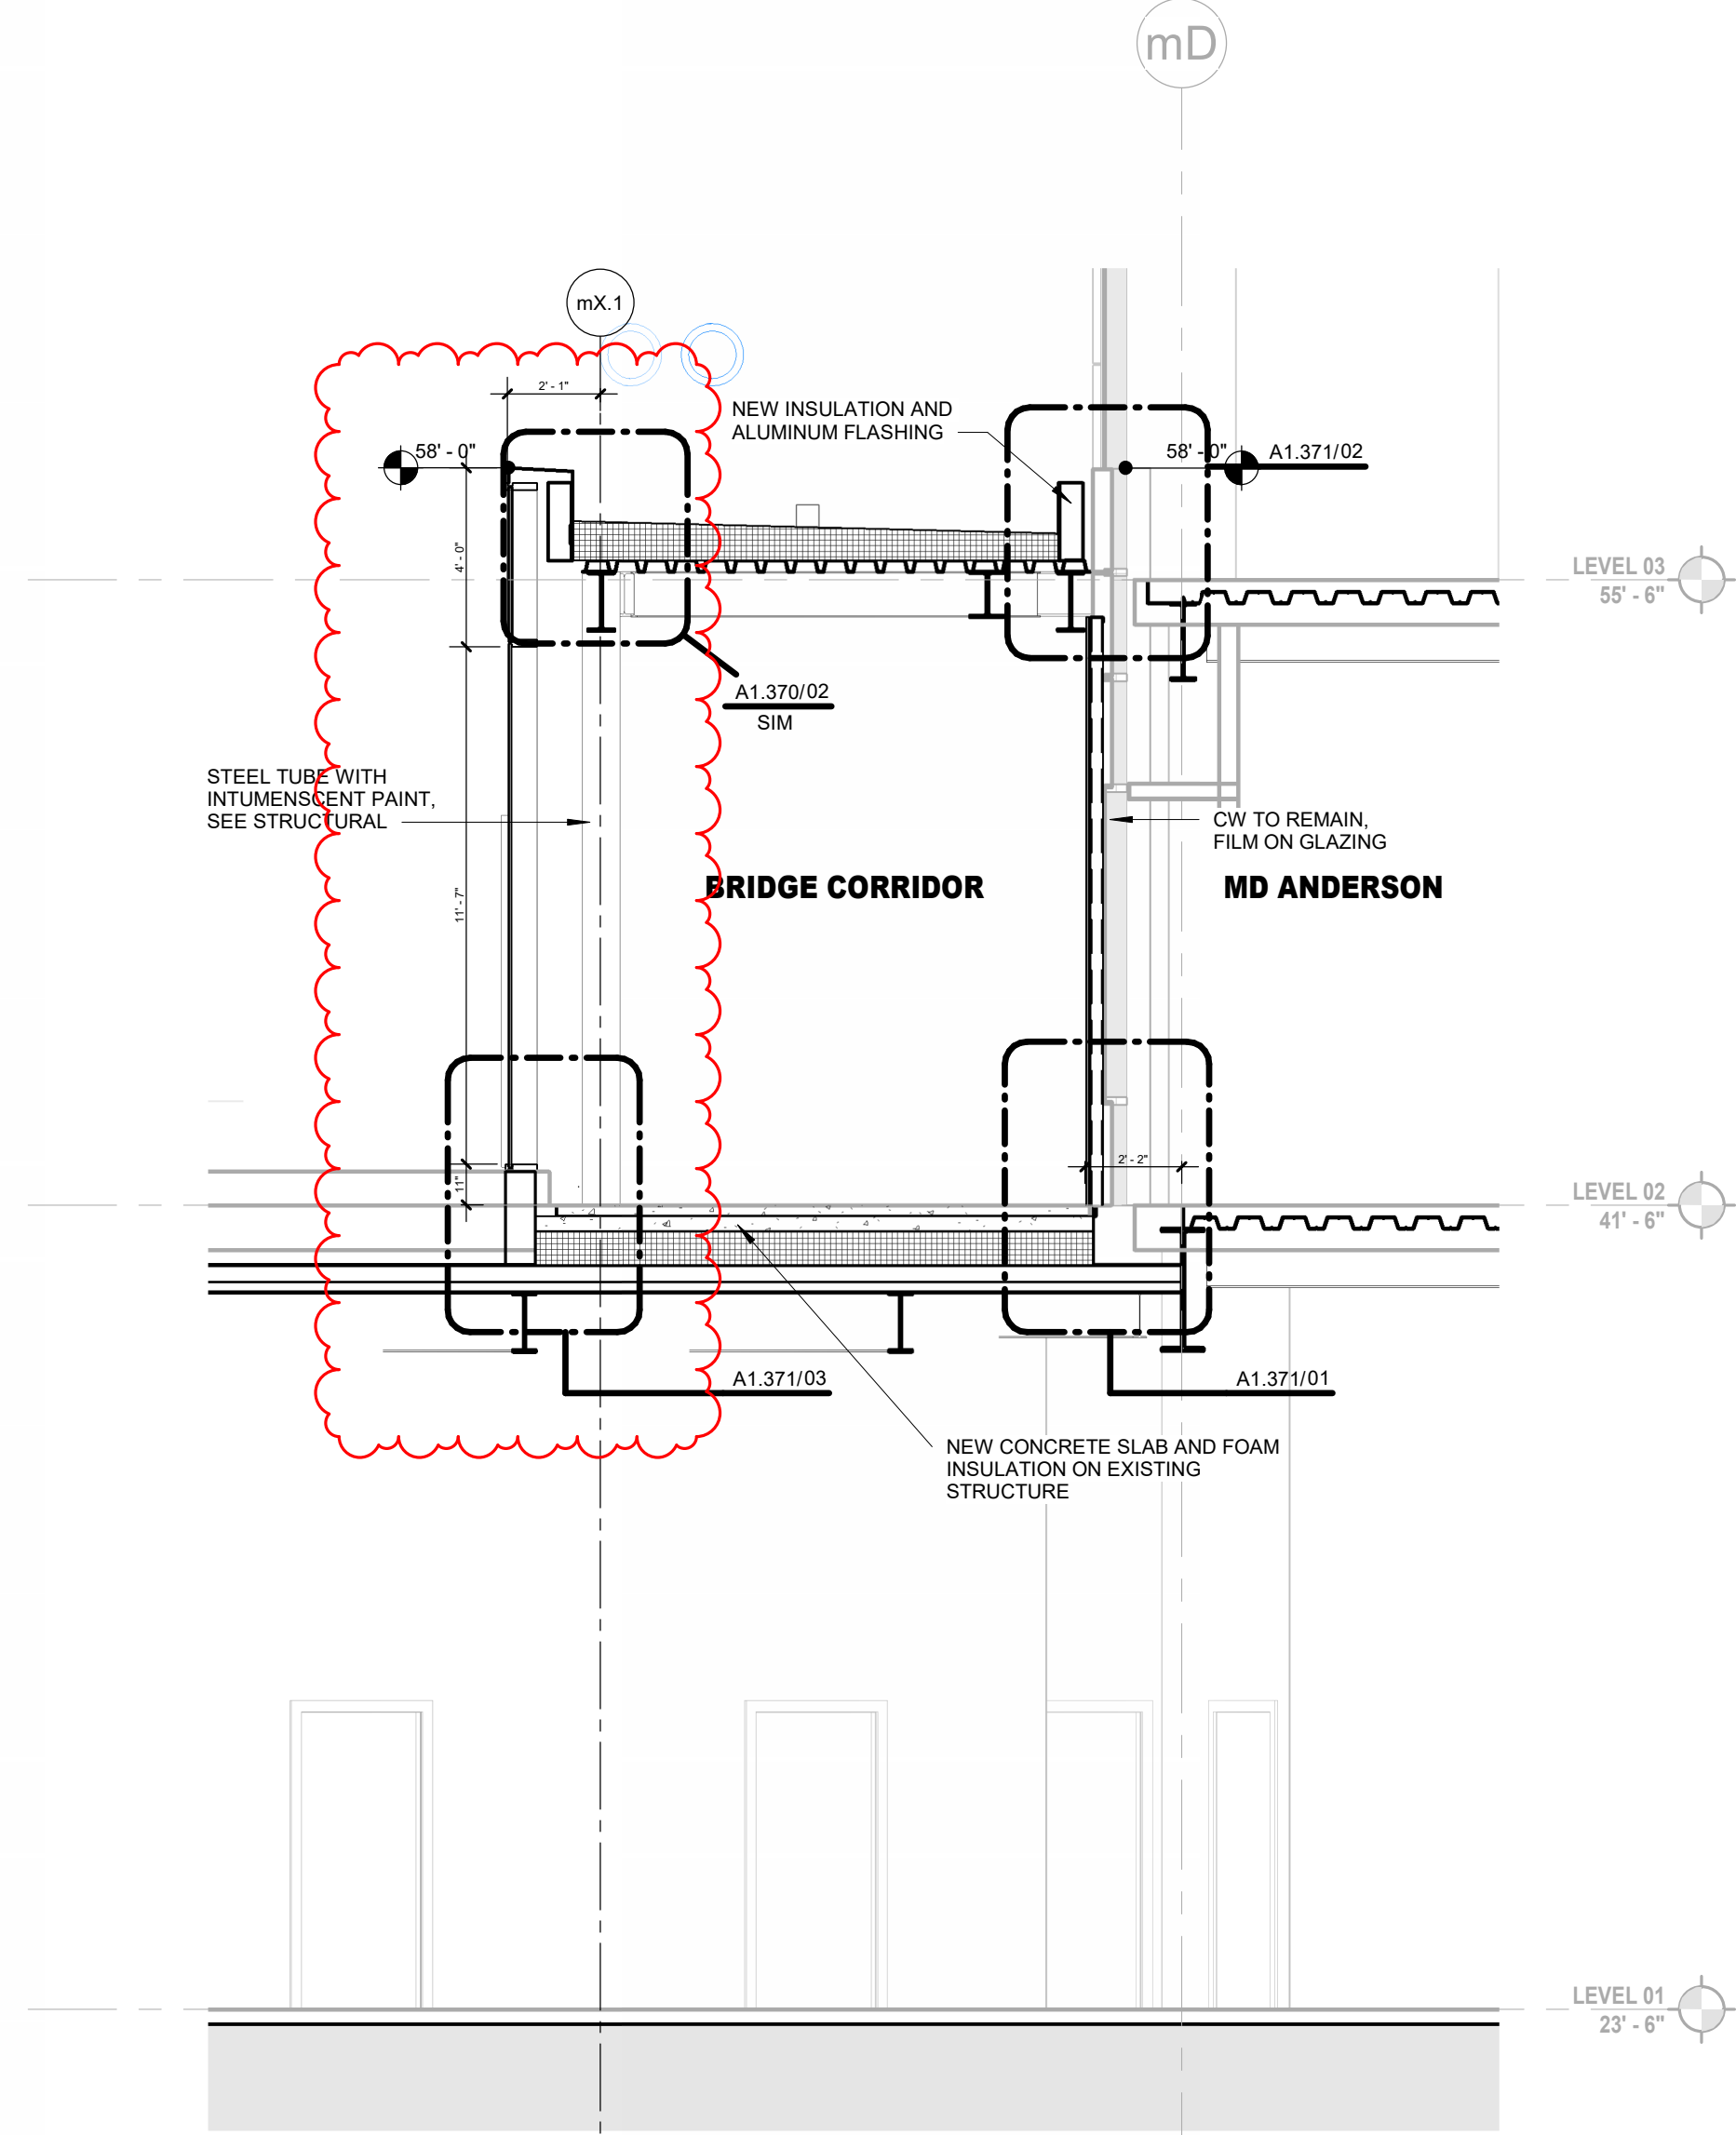


04 CROSS SECTION - THRU CORRIDOR AT MD ANDERSON
1/4" = 1'-0"

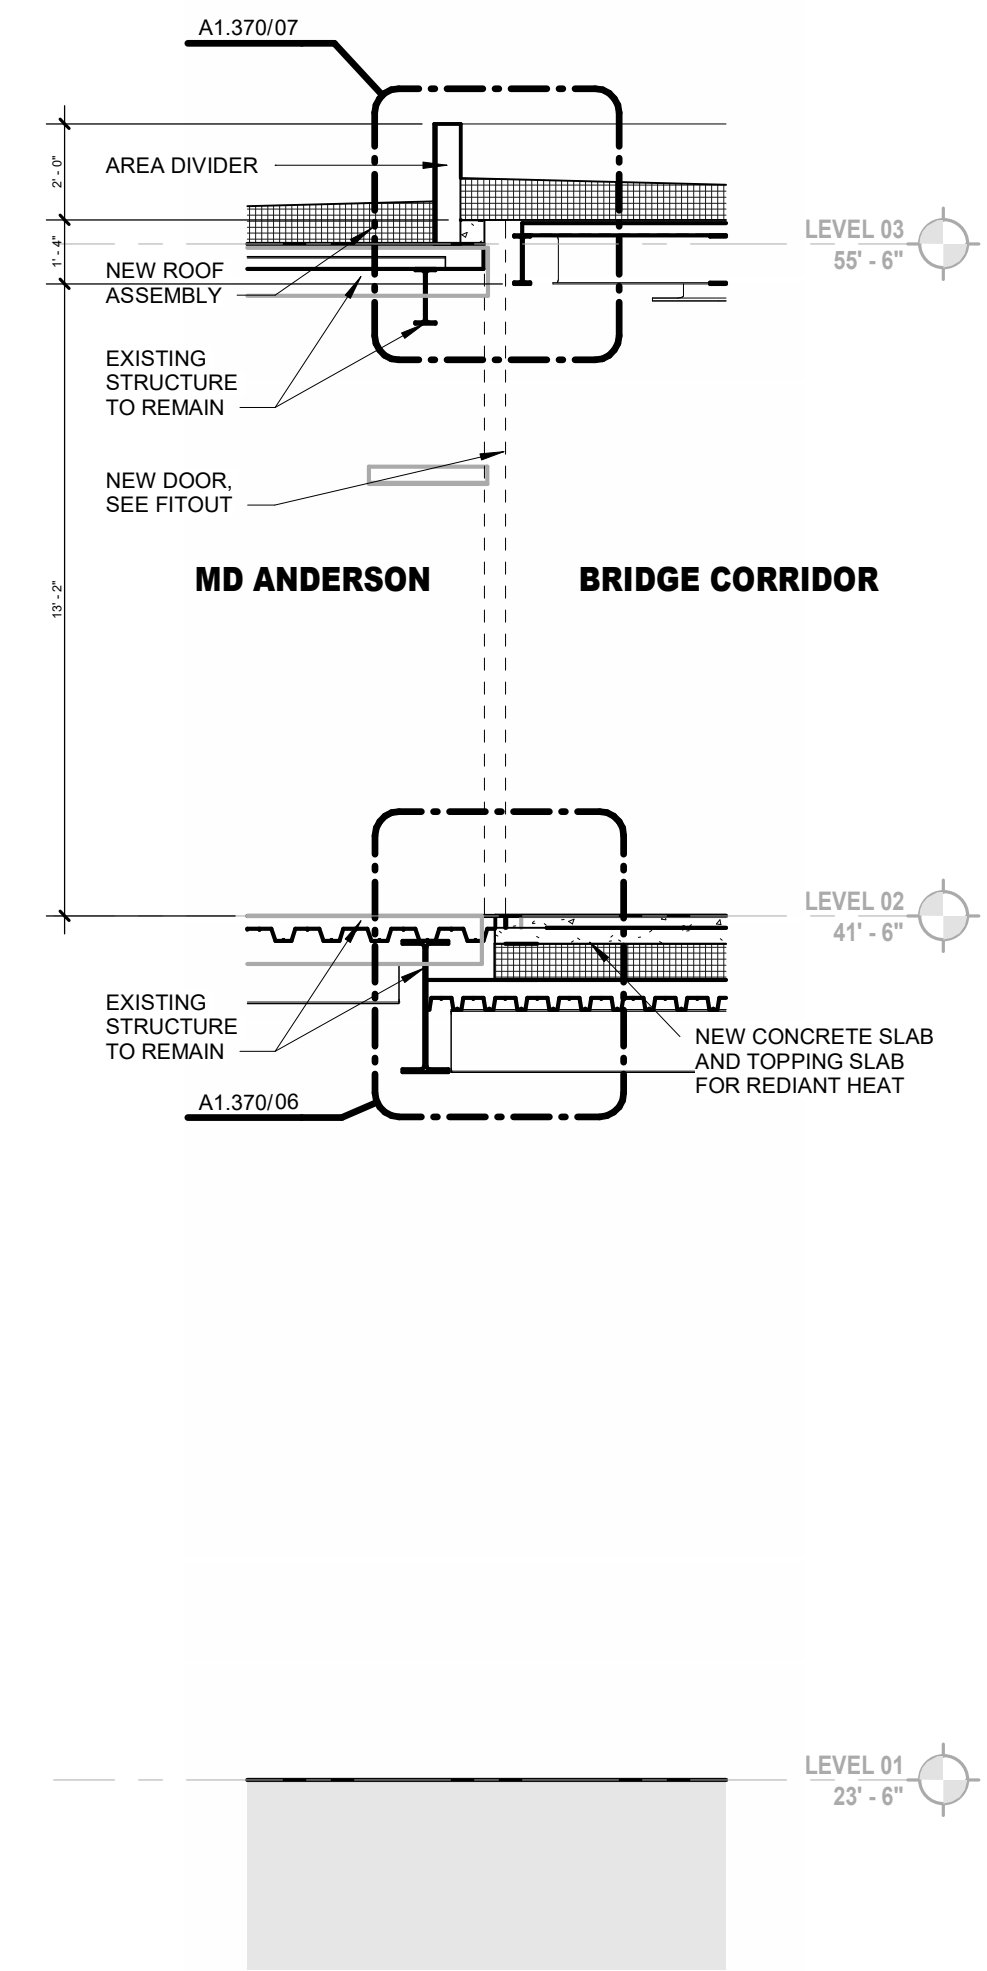

03 WALL SECTION - THRU THE BRIDGE CORRIDOR ENTRY AT MD ANDERSON
1/4" = 1'-0"

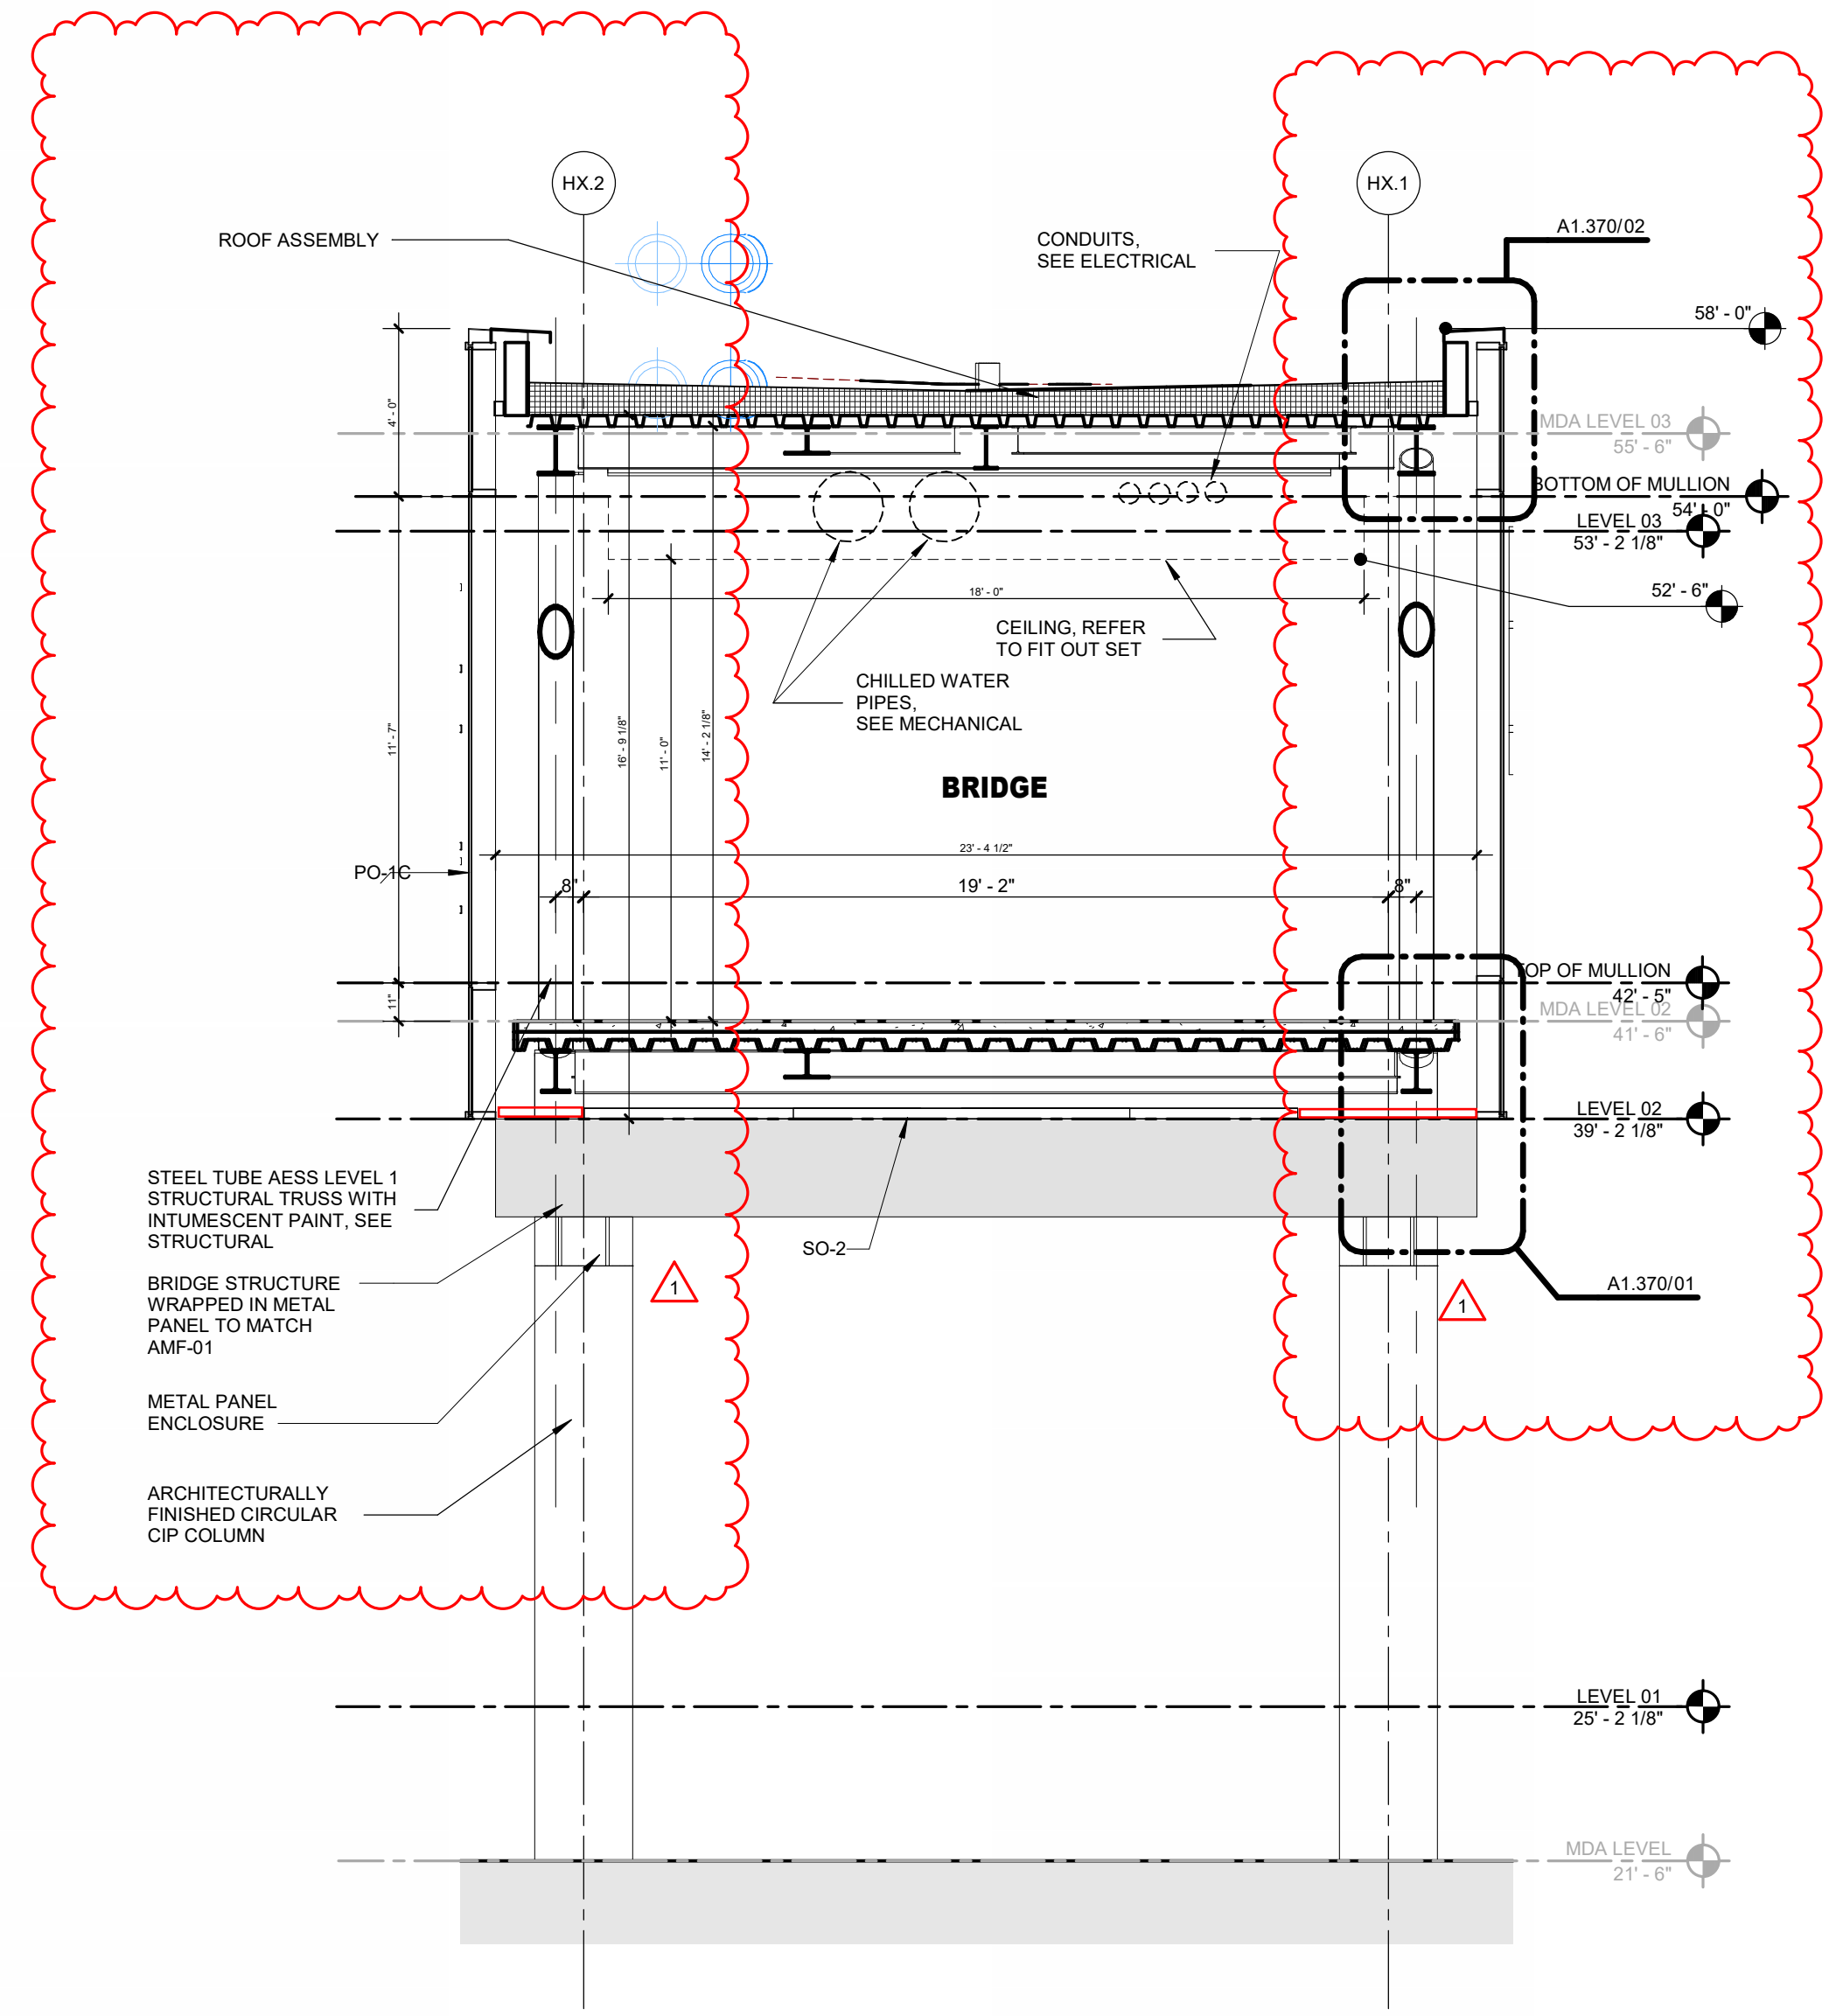

01 CROSS SECTION - THRU BR
1/4" = 1'-0"

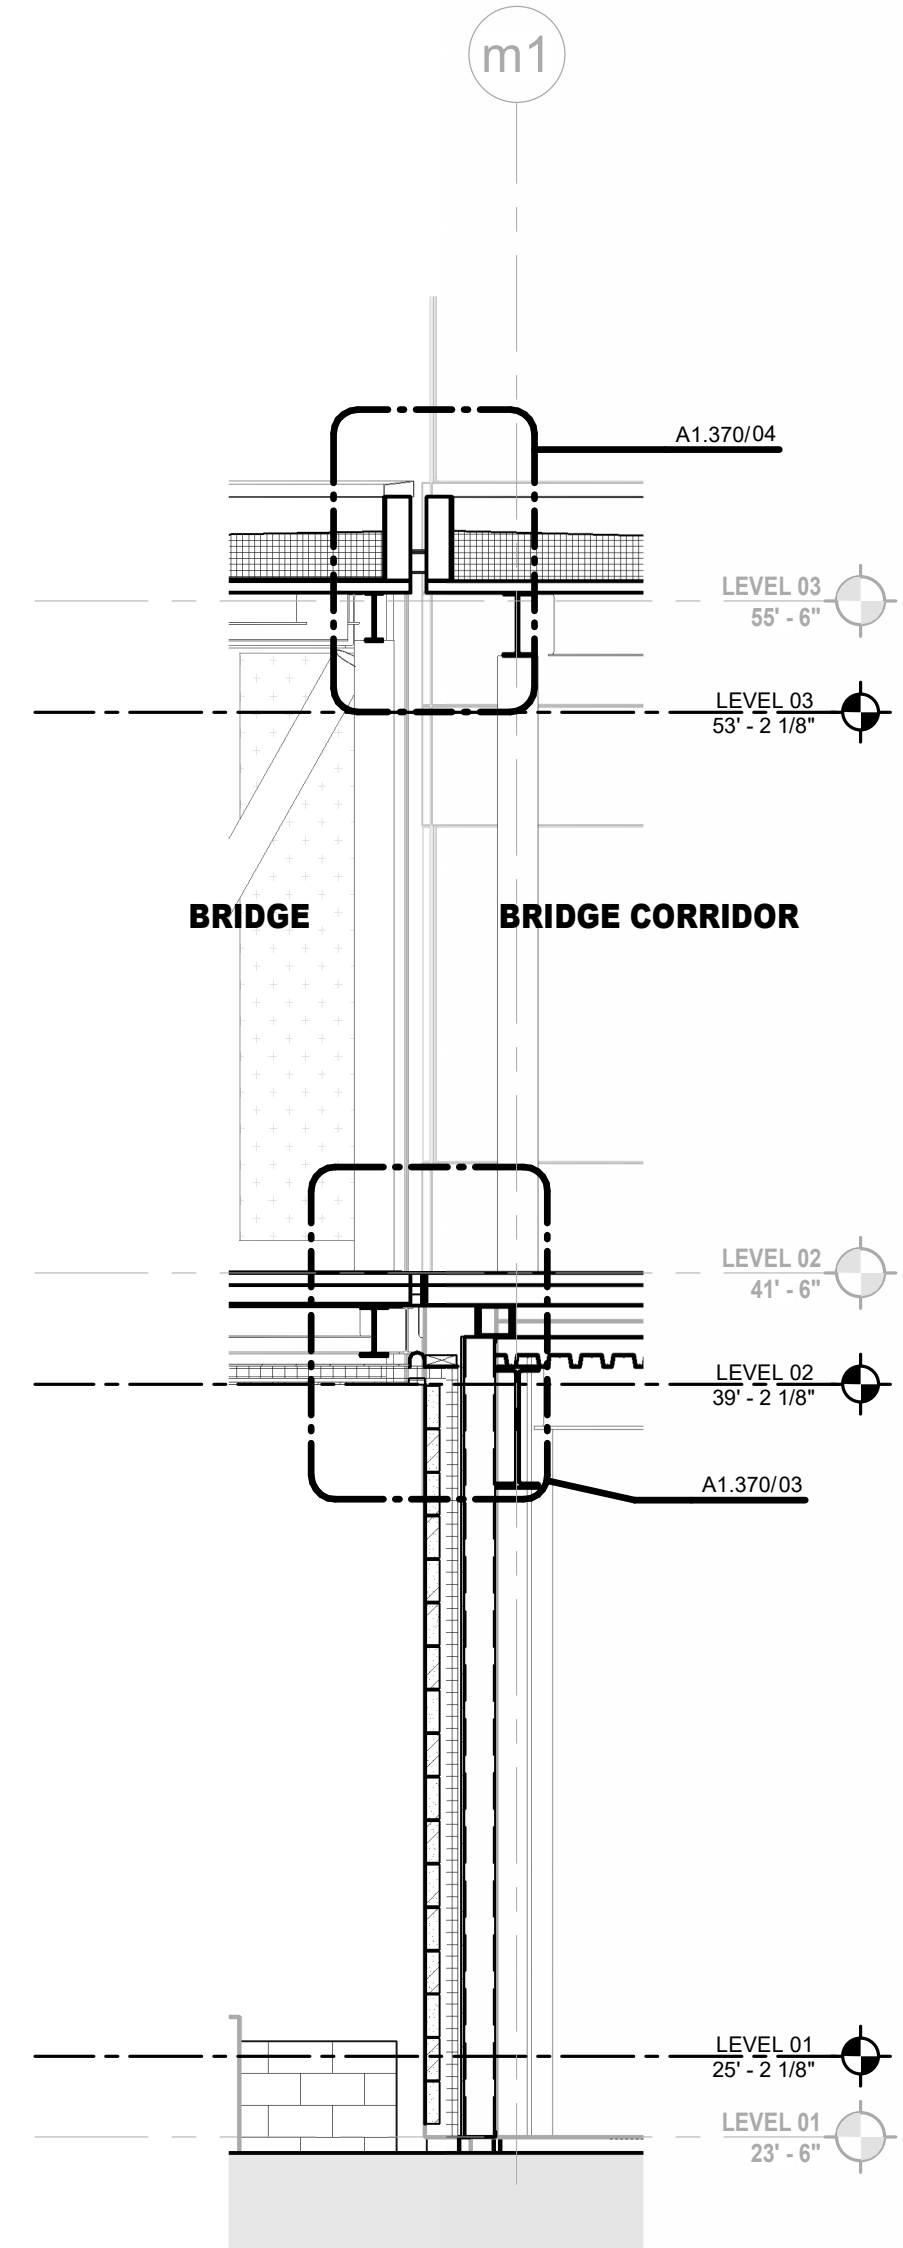

02 WALL SECTION - THRU MD ANDERSON FACADE
1/4" = 1'-0"

RESERVE FOR DCA STAMP




ARCHITECT
HKS, P.C.
1250 I (EYE) STREET NW, SUITE 600
WASHINGTON, DC 20005
ASSOCIATE ARCHITECT / INTERIOR DESIGNER
ARRAY
1 WEST ELM STREET, SUITE 500
CONSHOHOCKEN, PA 19428
STRUCTURAL ENGINEER
O'DONNELL & NACCARATO
701 MARKET ST., #6000
PHILADELPHIA, PA 19106
MEP-FP / LOW VOLTAGE ENGINEER
BR+A CONSULTING ENGINEERS
2401 WALNUT ST SUITE 701
PHILADELPHIA, PA 19103
HIGHLAND ASSOCIATES
102 HIGHLAND AVE
CLARKS SUMMIT, PA 18411



OWNER
COOPER UNIVERSITY HEALTHCARE
1 COOPER PLAZA
CAMDEN, NJ 08103
PROJECT MANAGER
PURE PM
2026 RICHMOND STREET
PHILADELPHIA, PA 19134
CIVIL ENGINEER / LANDSCAPE
LANGAN
1818 MARKET STREET, SUITE 3300
PHILADELPHIA, PA 19103
SEAL & SIGNATURE

KEY PLAN

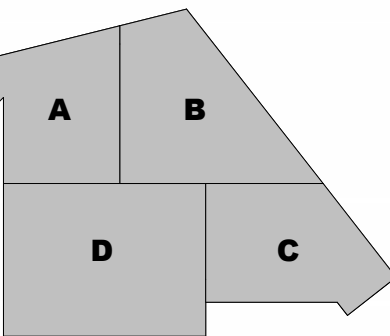


REVISION	NO.	DESCRIPTION	DATE
1	BULLETIN #4		04/28/2025
2	RFI 0420		11/14/2025

HKS PROJECT NUMBER
25695.100
DATE
10/15/2024
ISSUE
CORE & SHELL PERMIT SET
SHEET TITLE
BRIDGE SECTIONS


SHEET NO.

A1.360


TITLE BLOCK VERSION: 20210830
MODEL: Anderson Docs 25695.000 Cooper Master Campus Plan 2023.01 CHAT Tower A, Exterior 2023.rvt
PRINT DATE: 11/21/2023 3:25:56 PM TEMPLATE VERSION: 23.0.3
© HKS, INC.

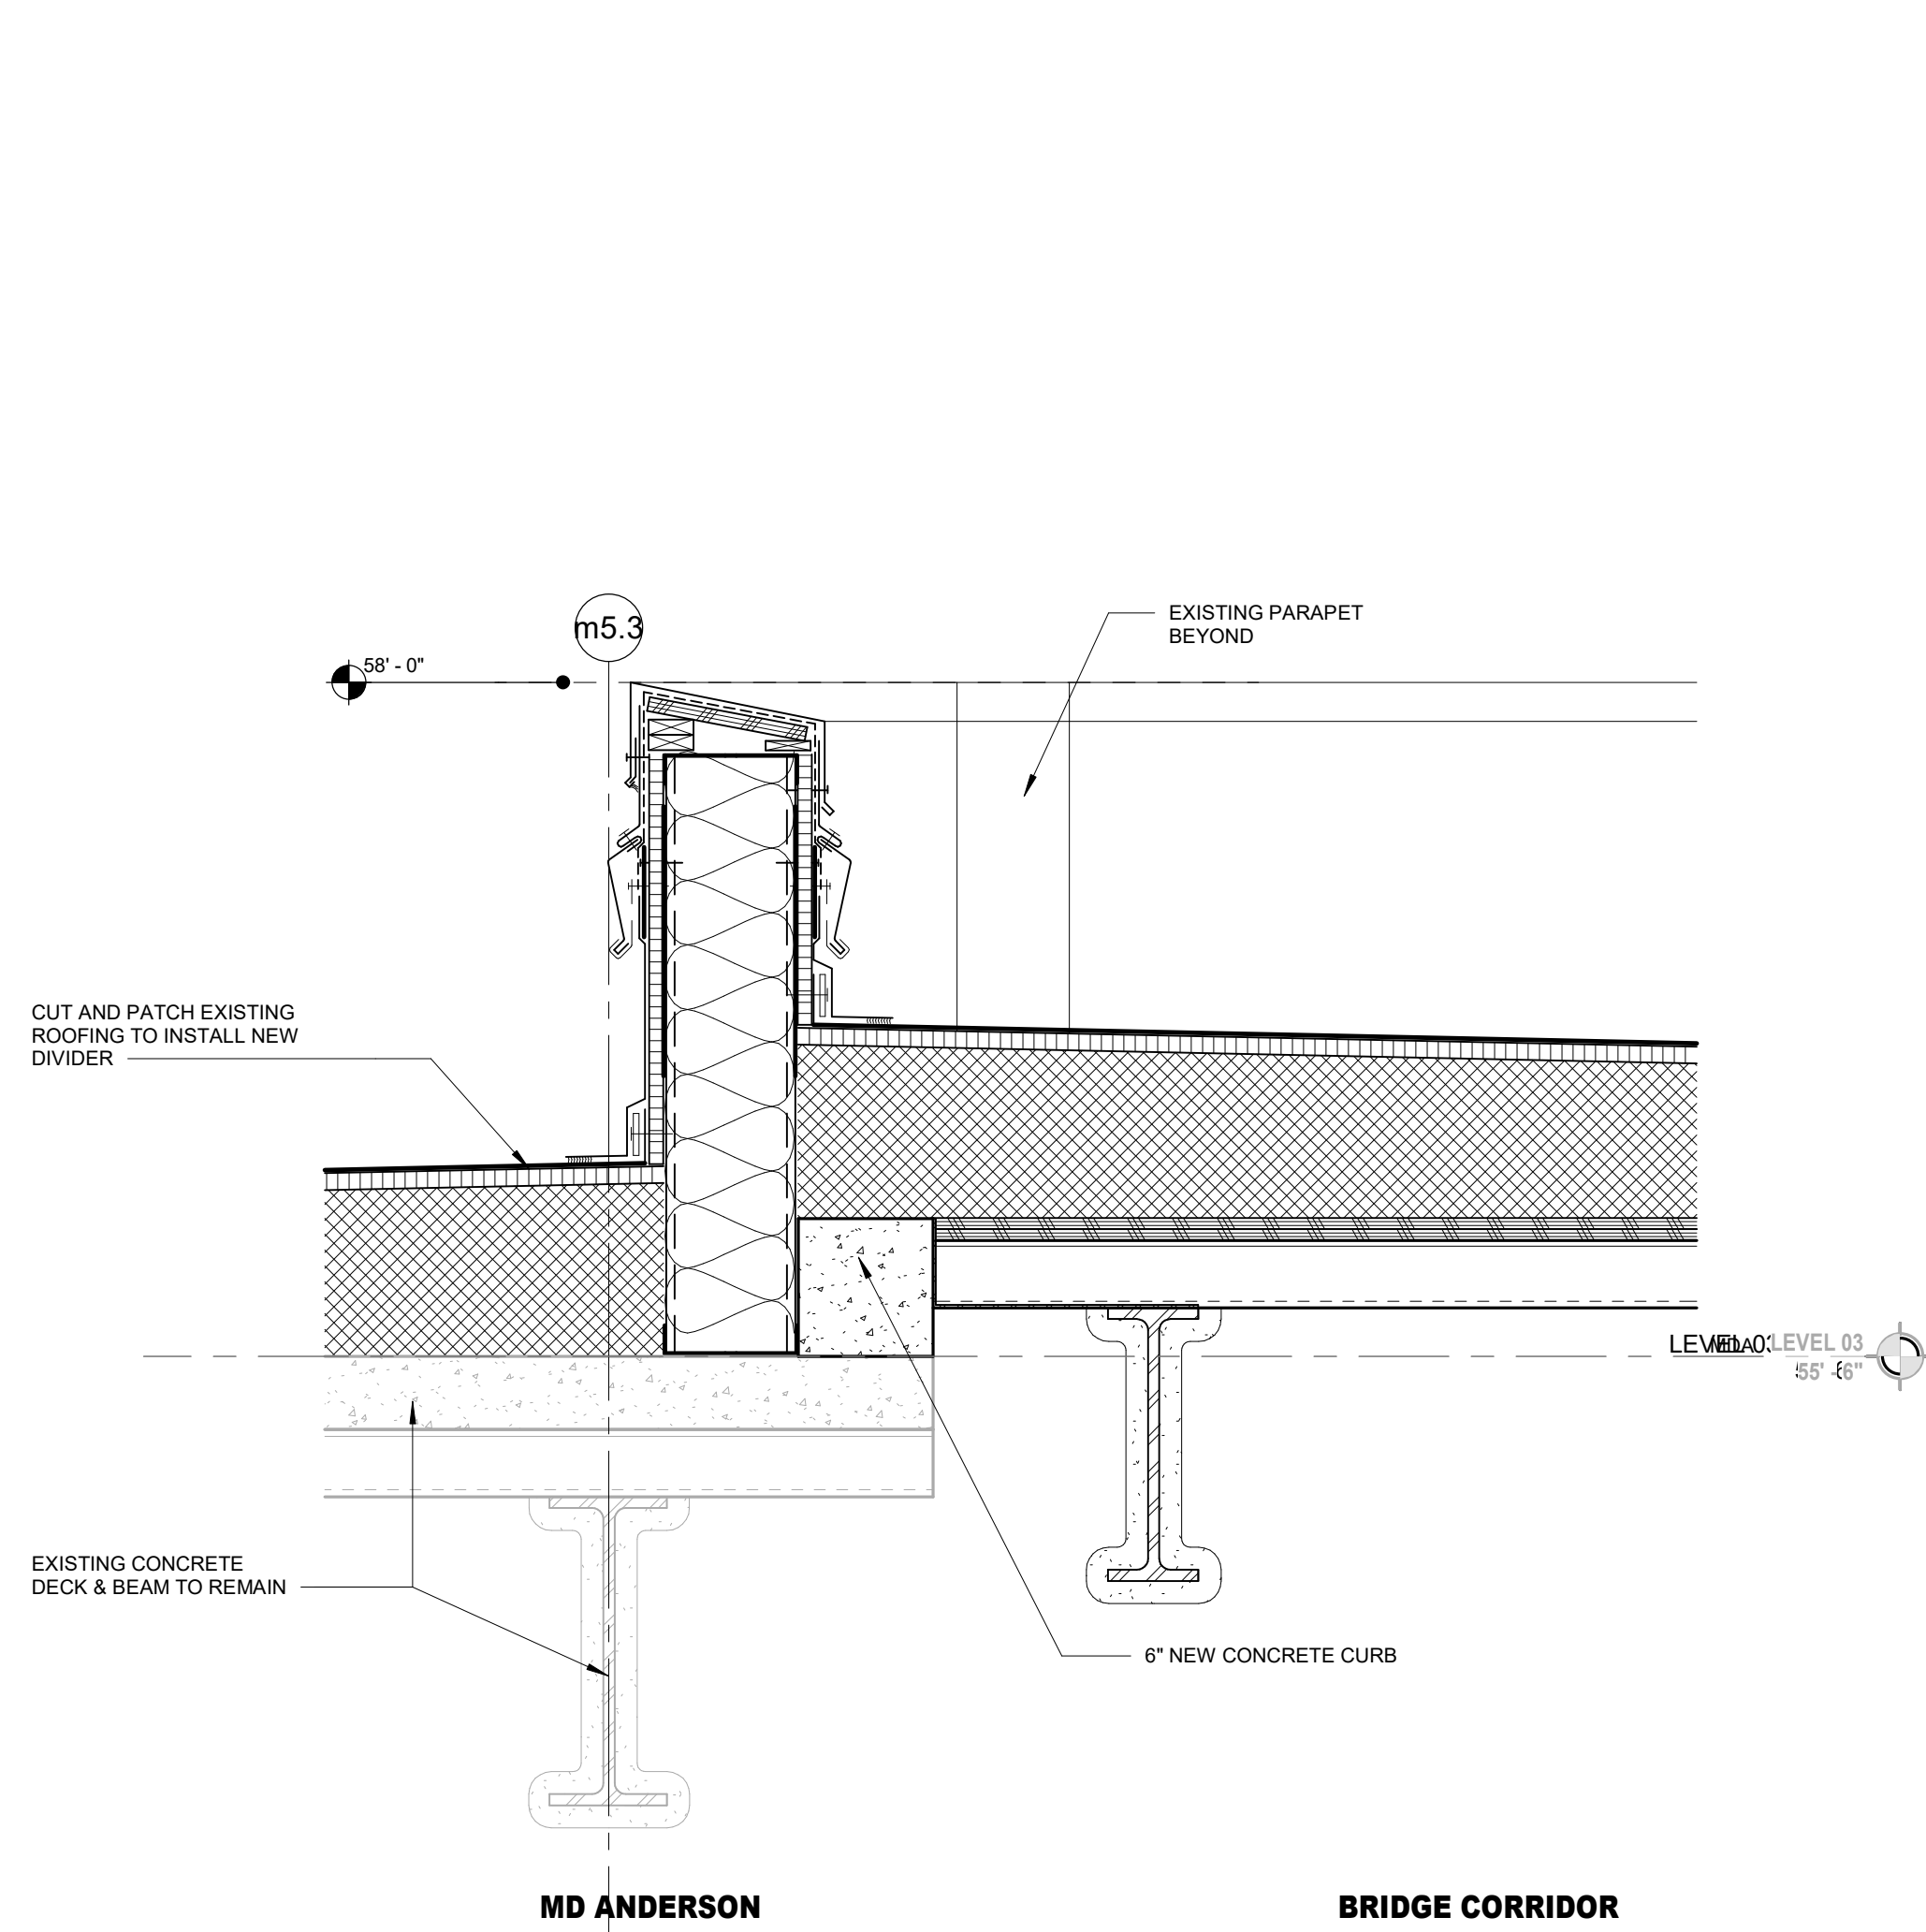


07 SECTION DTL - BRIDGE CORRIDOR ENTRY TO MD ANDERSON LVL 3 ROOF
1 1/2" = 1'-0"

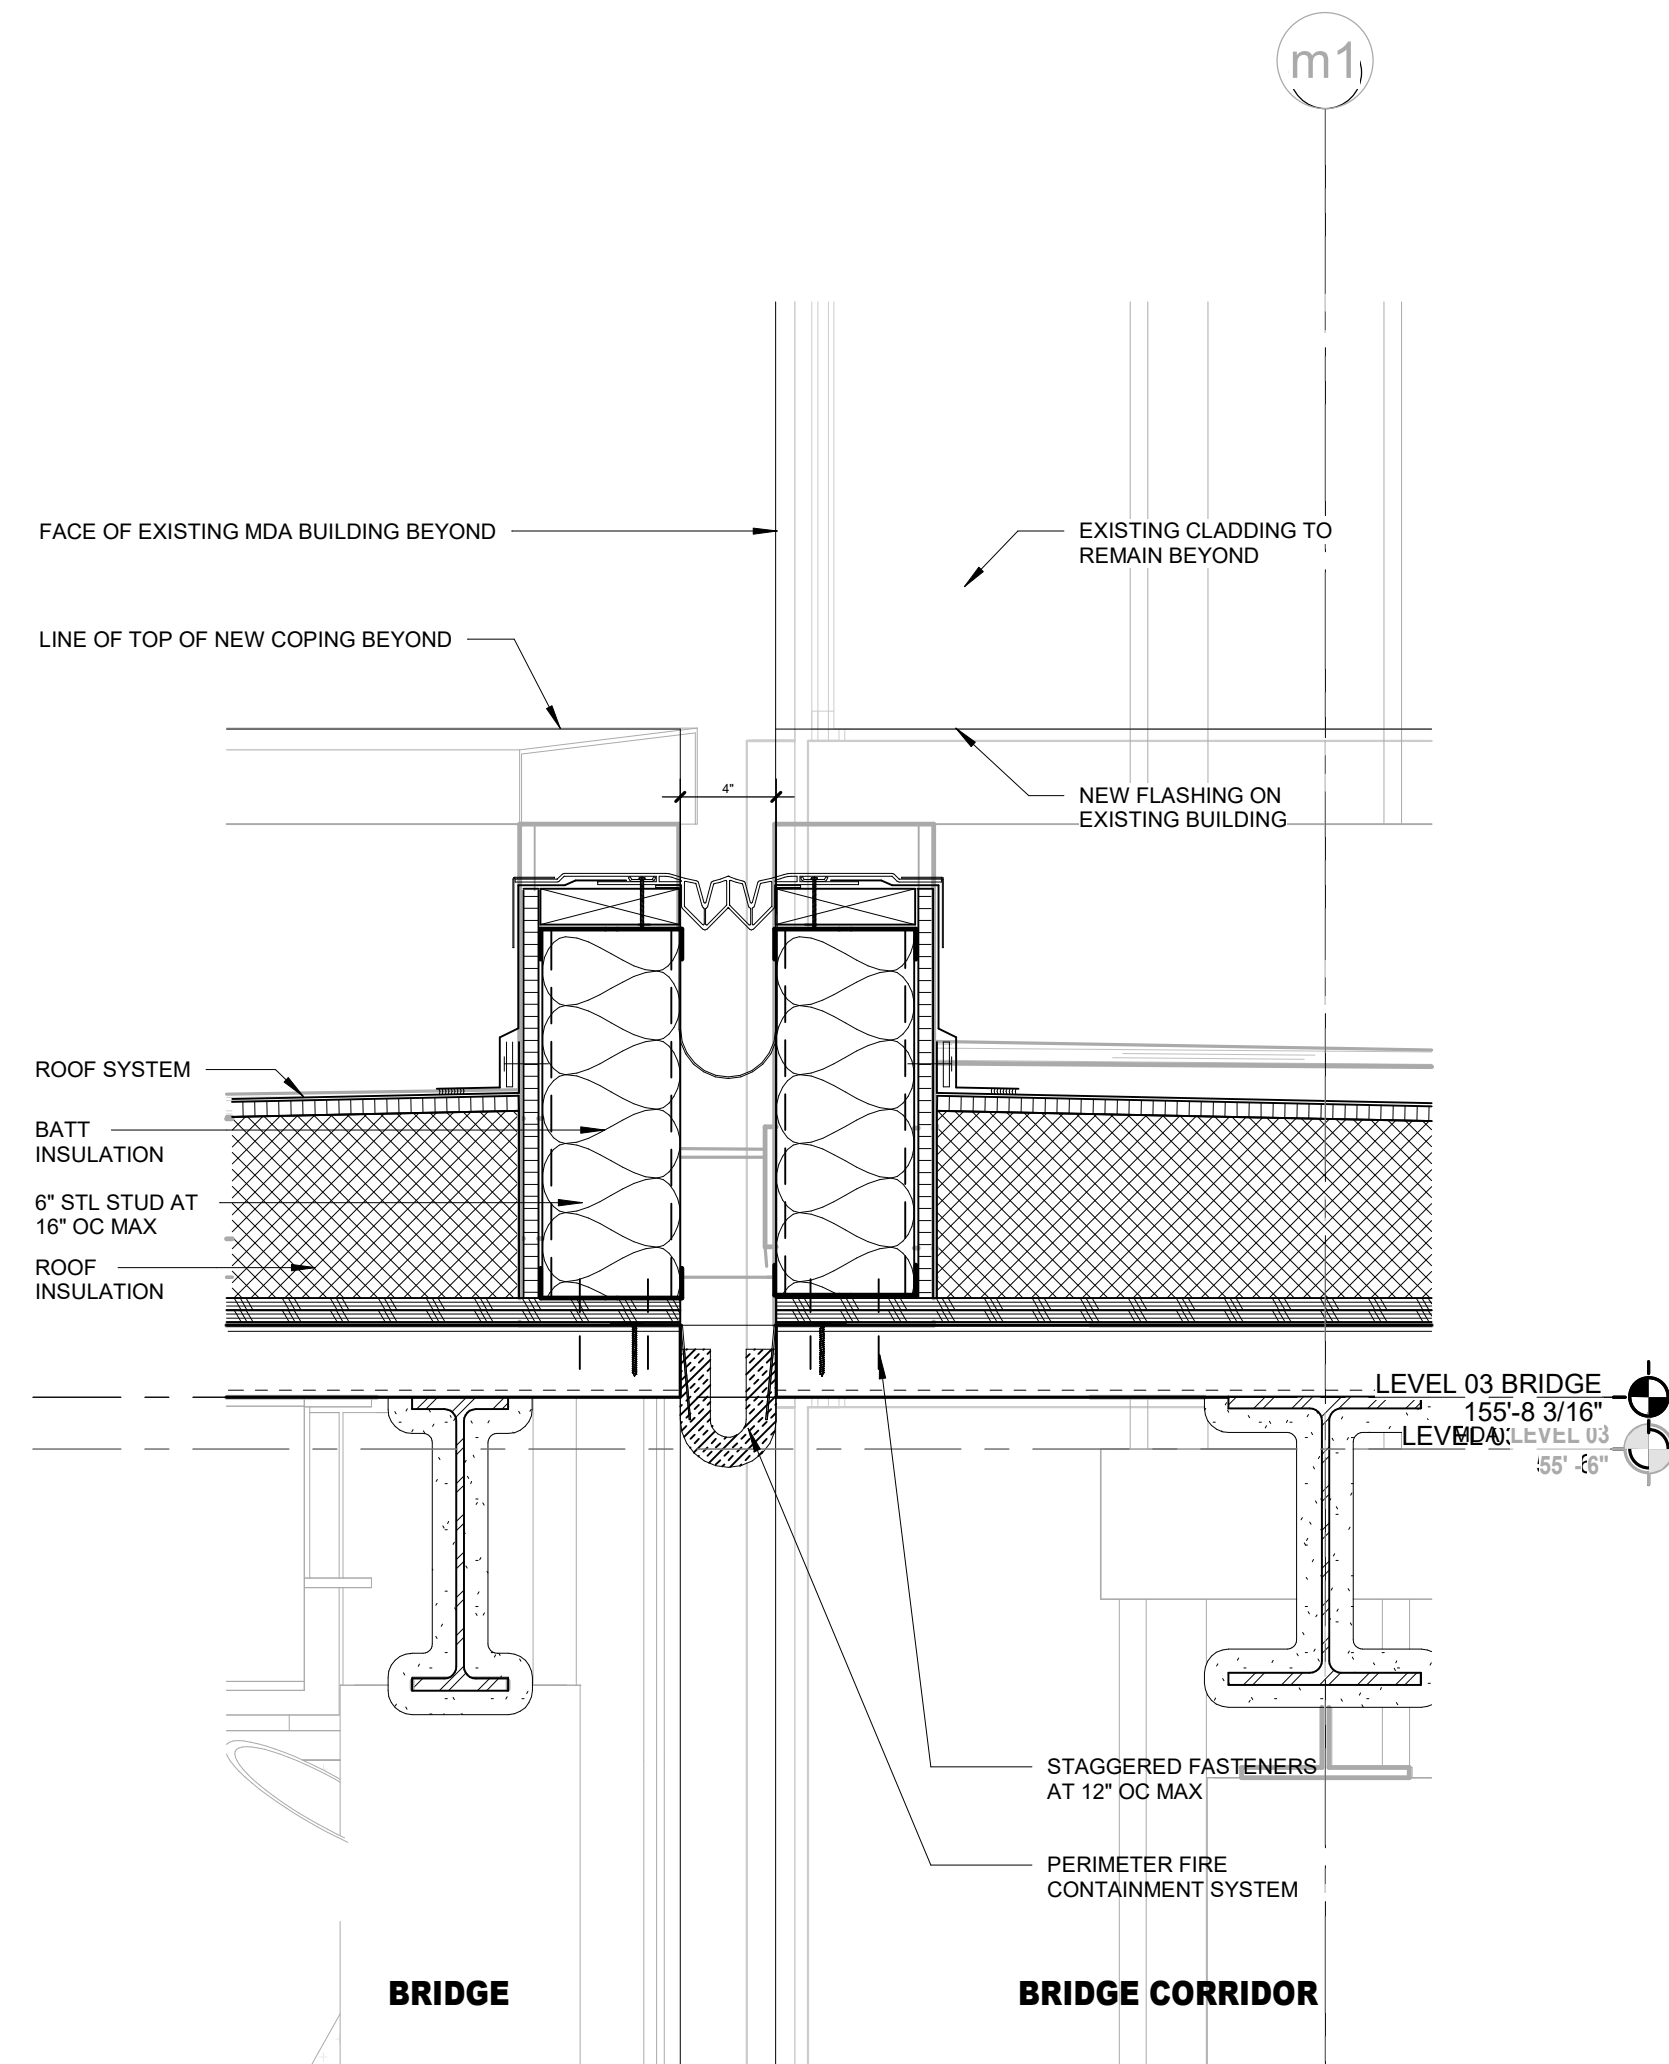


04 SECTION DTL - BRIDGE / BRIDGE CORRIDOR EXPANSION JOINT
1 1/2" = 1'-0"

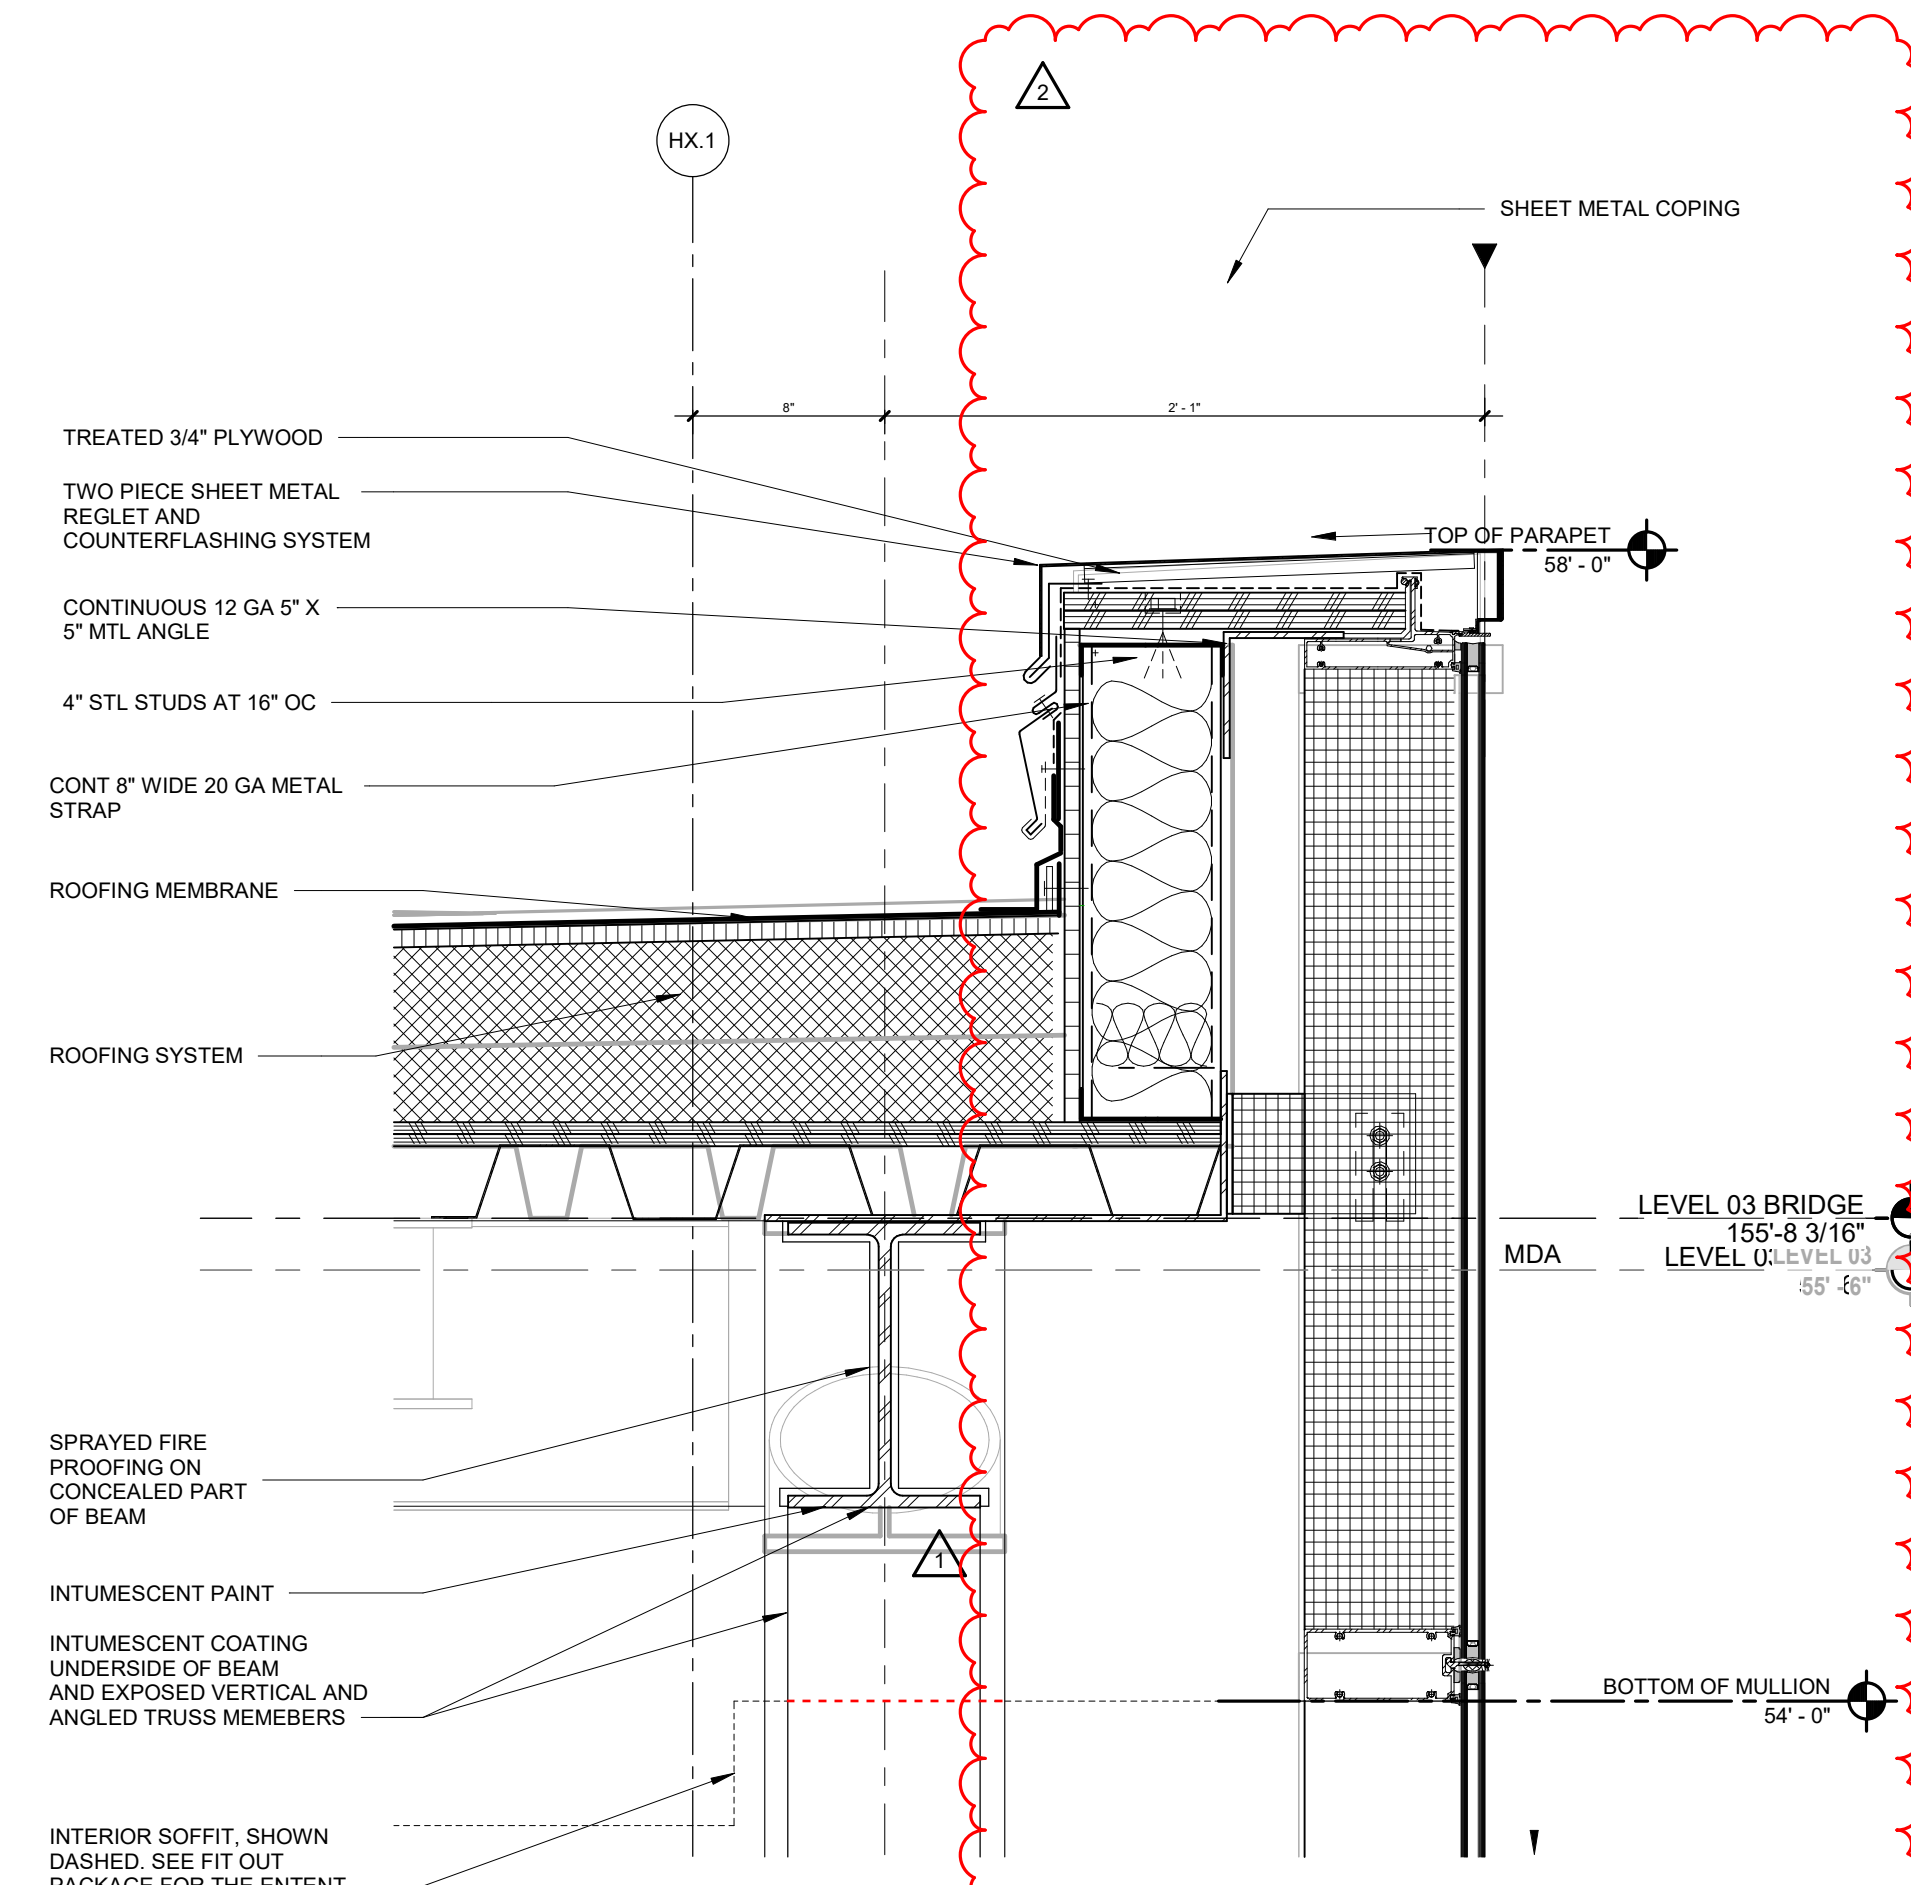


02 SECTION DTL - BRIDGE PARAPET
1 1/2" = 1'-0"

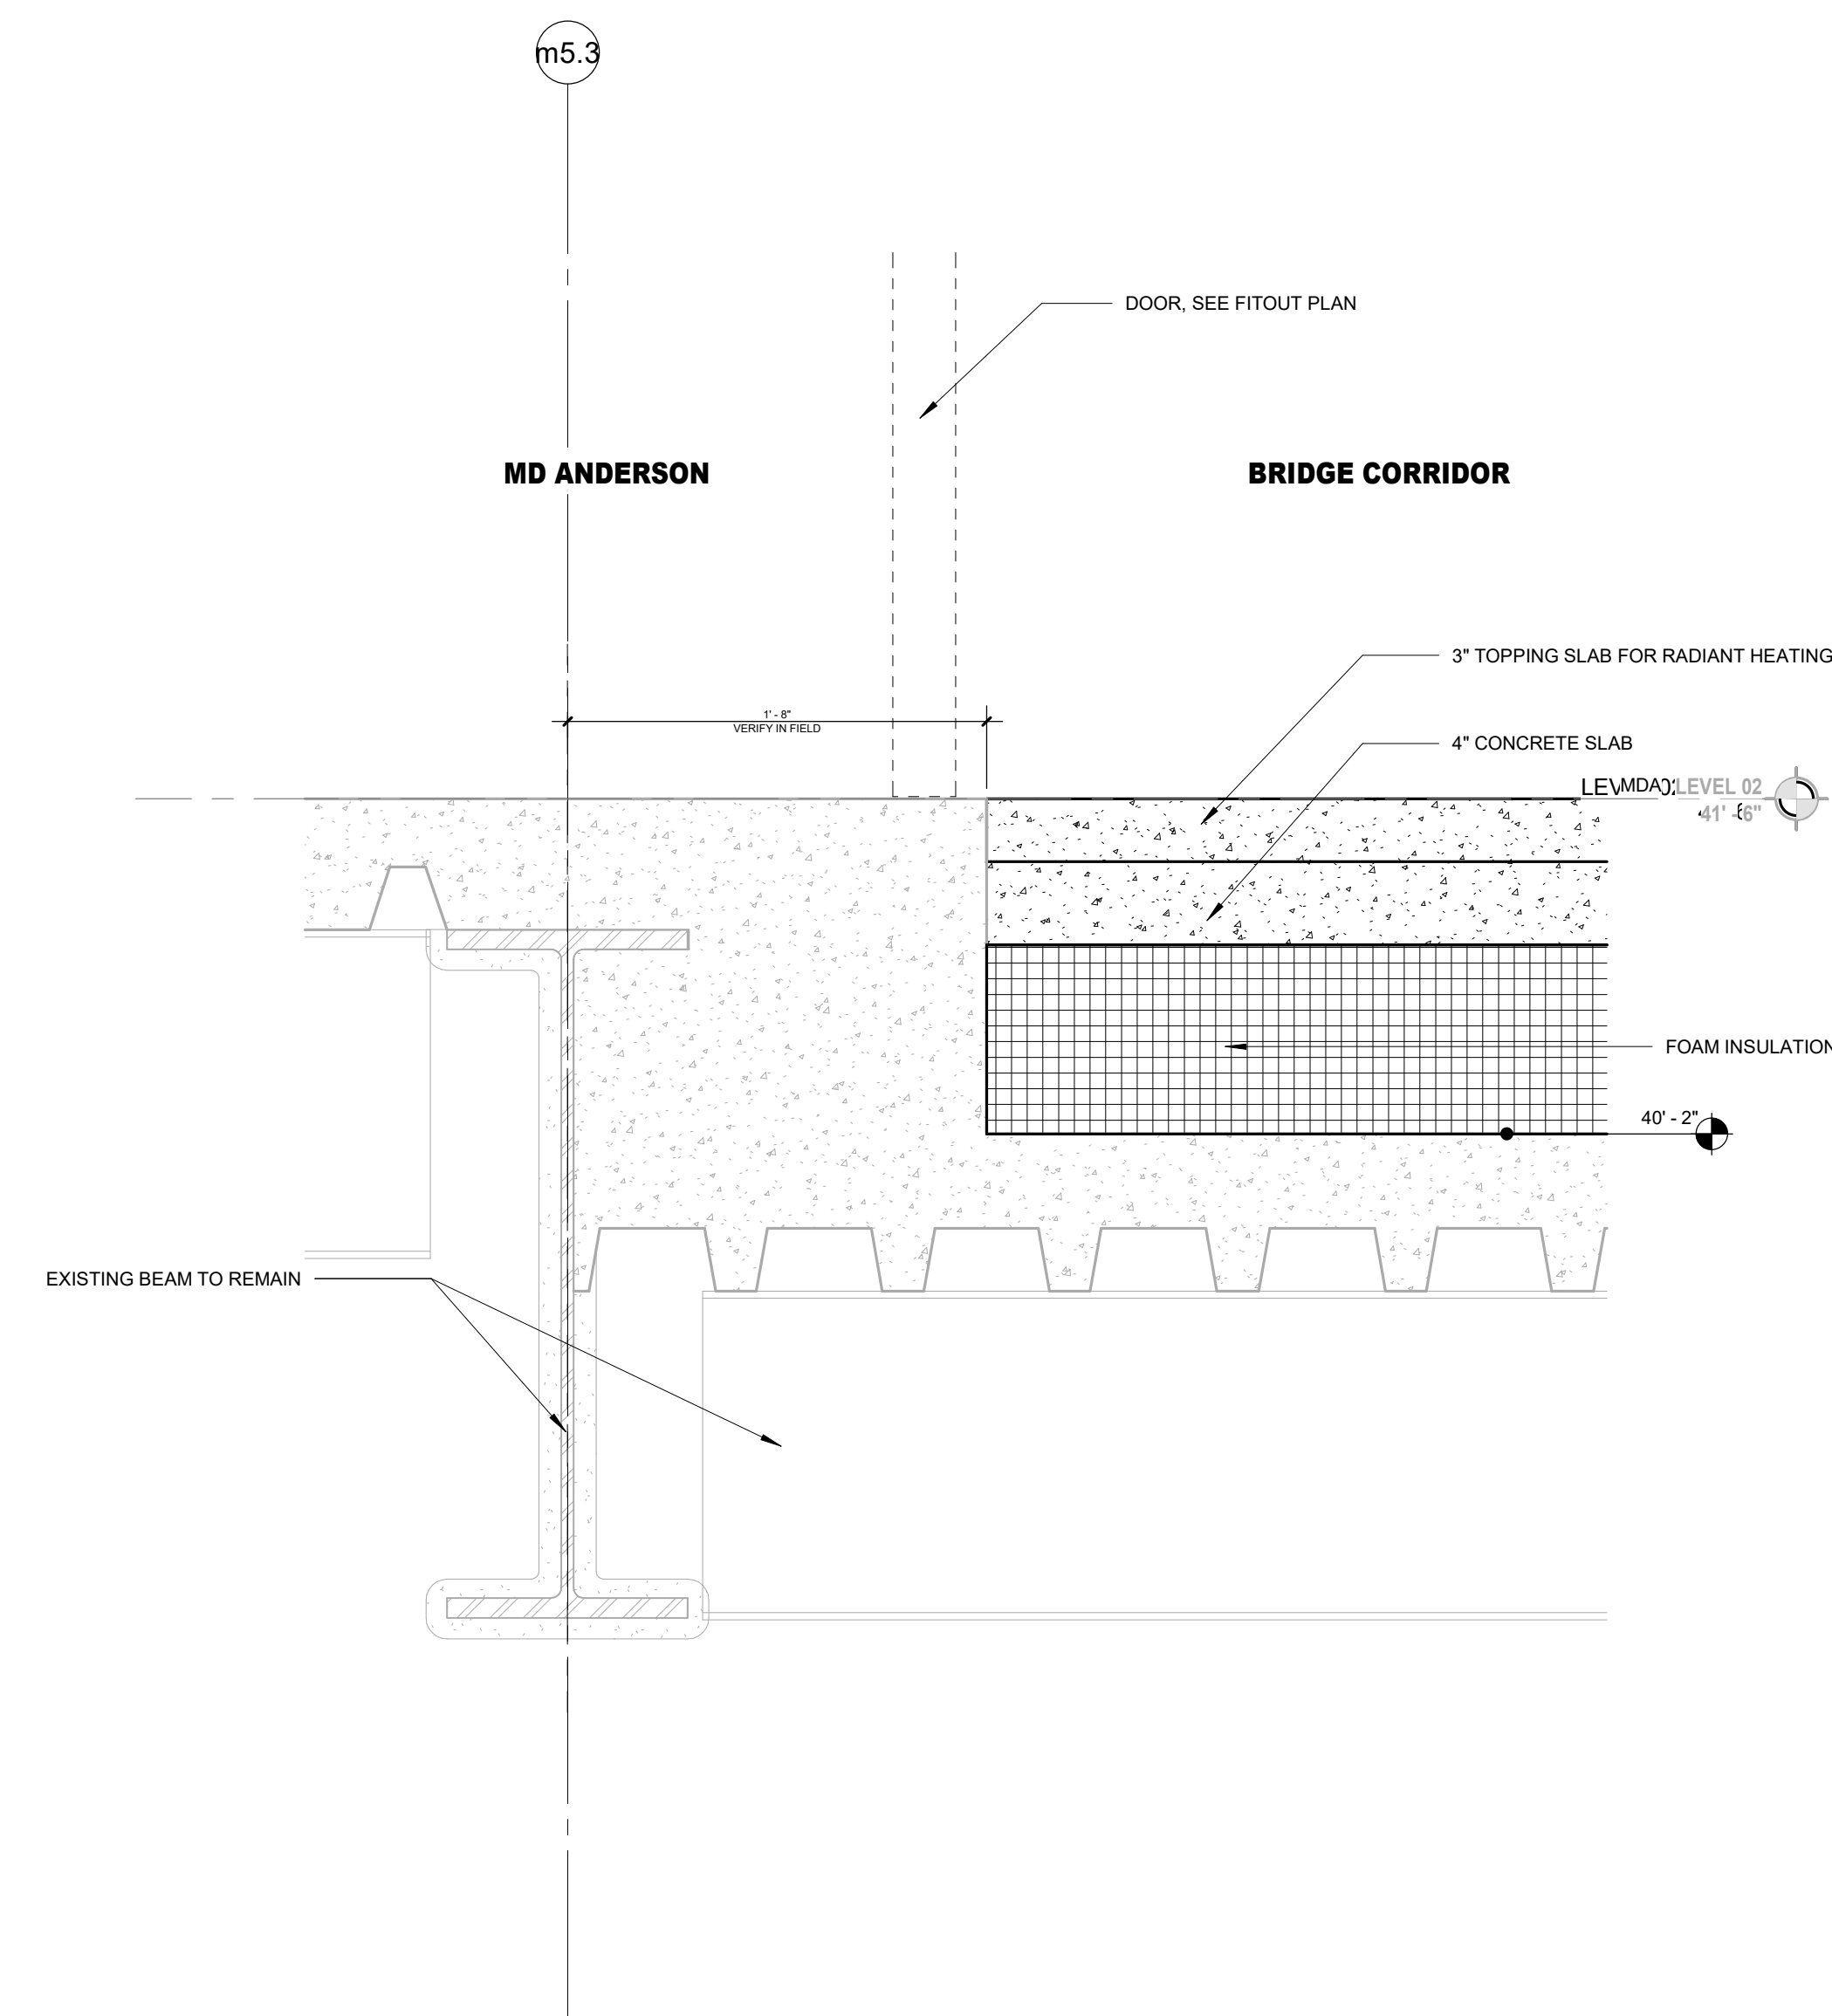

06 SECTION DTL - BRIDGE CORRIDOR ENTRY TO MD ANDERSON LVL 2 ROOF
1 1/2" = 1'-0"

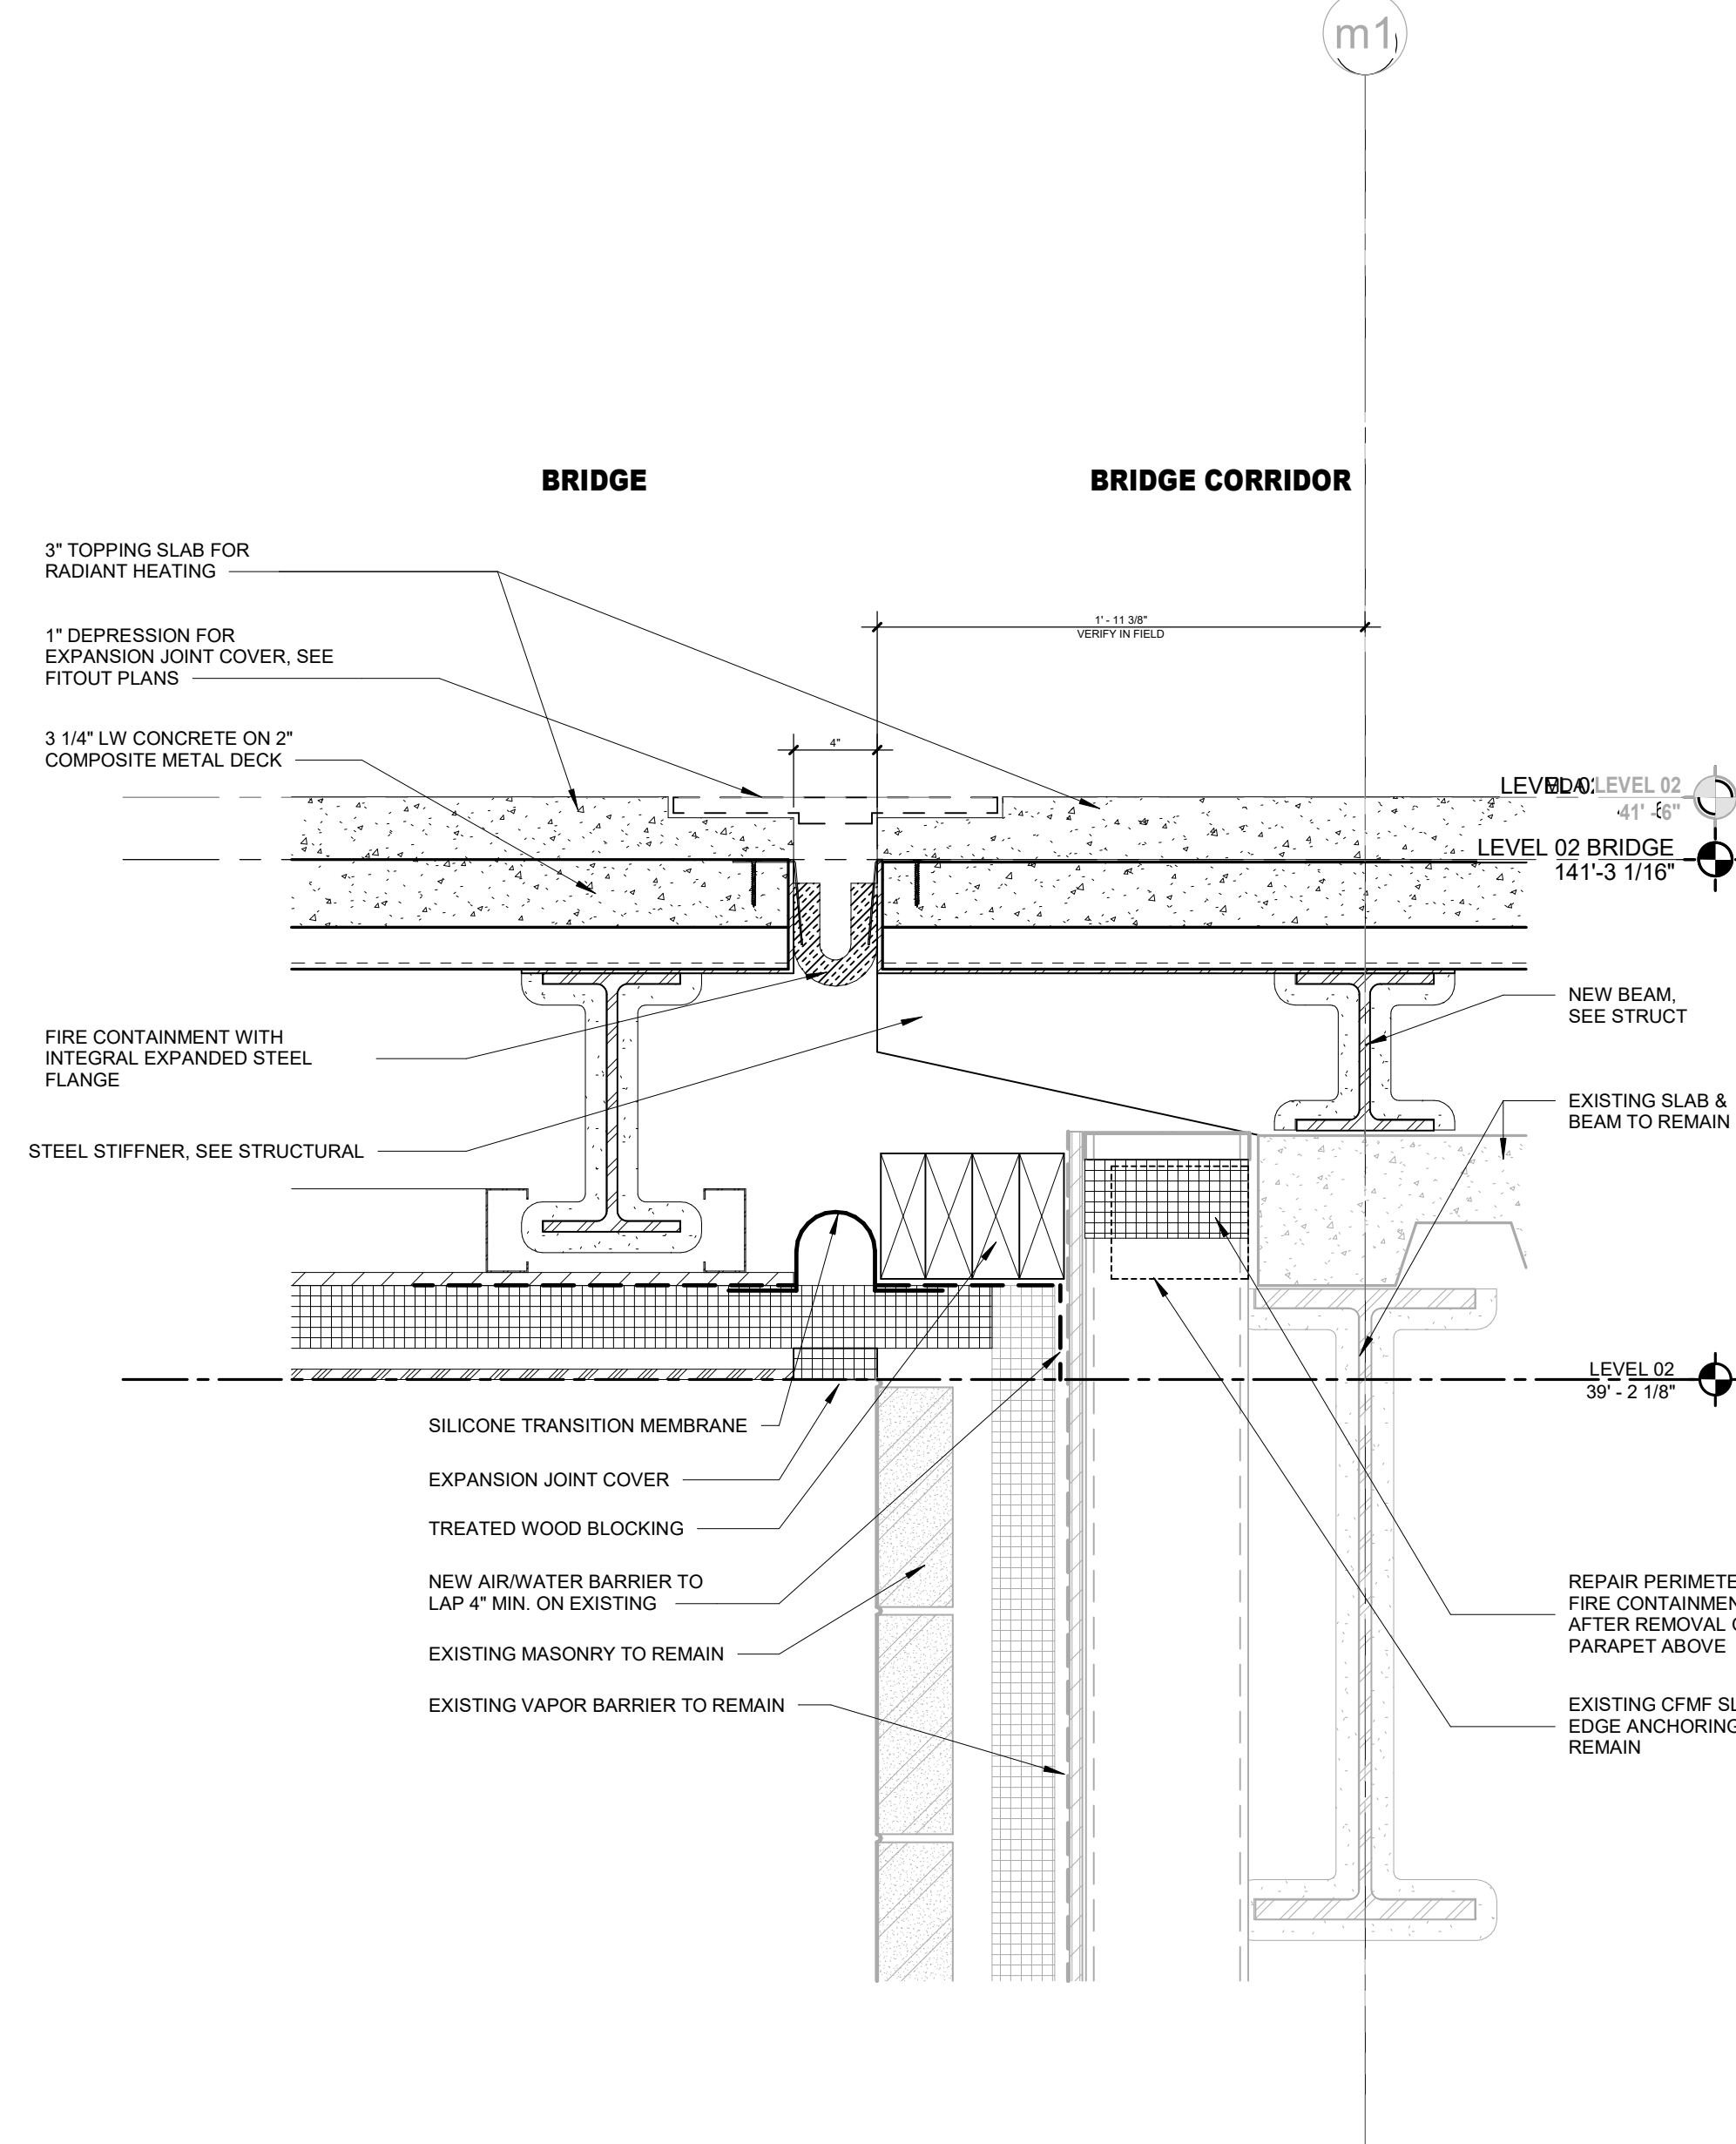

03 SECTION DTL - BRIDGE SLAB TO MD ANDERSON WEST FACADE
1 1/2" = 1'-0"

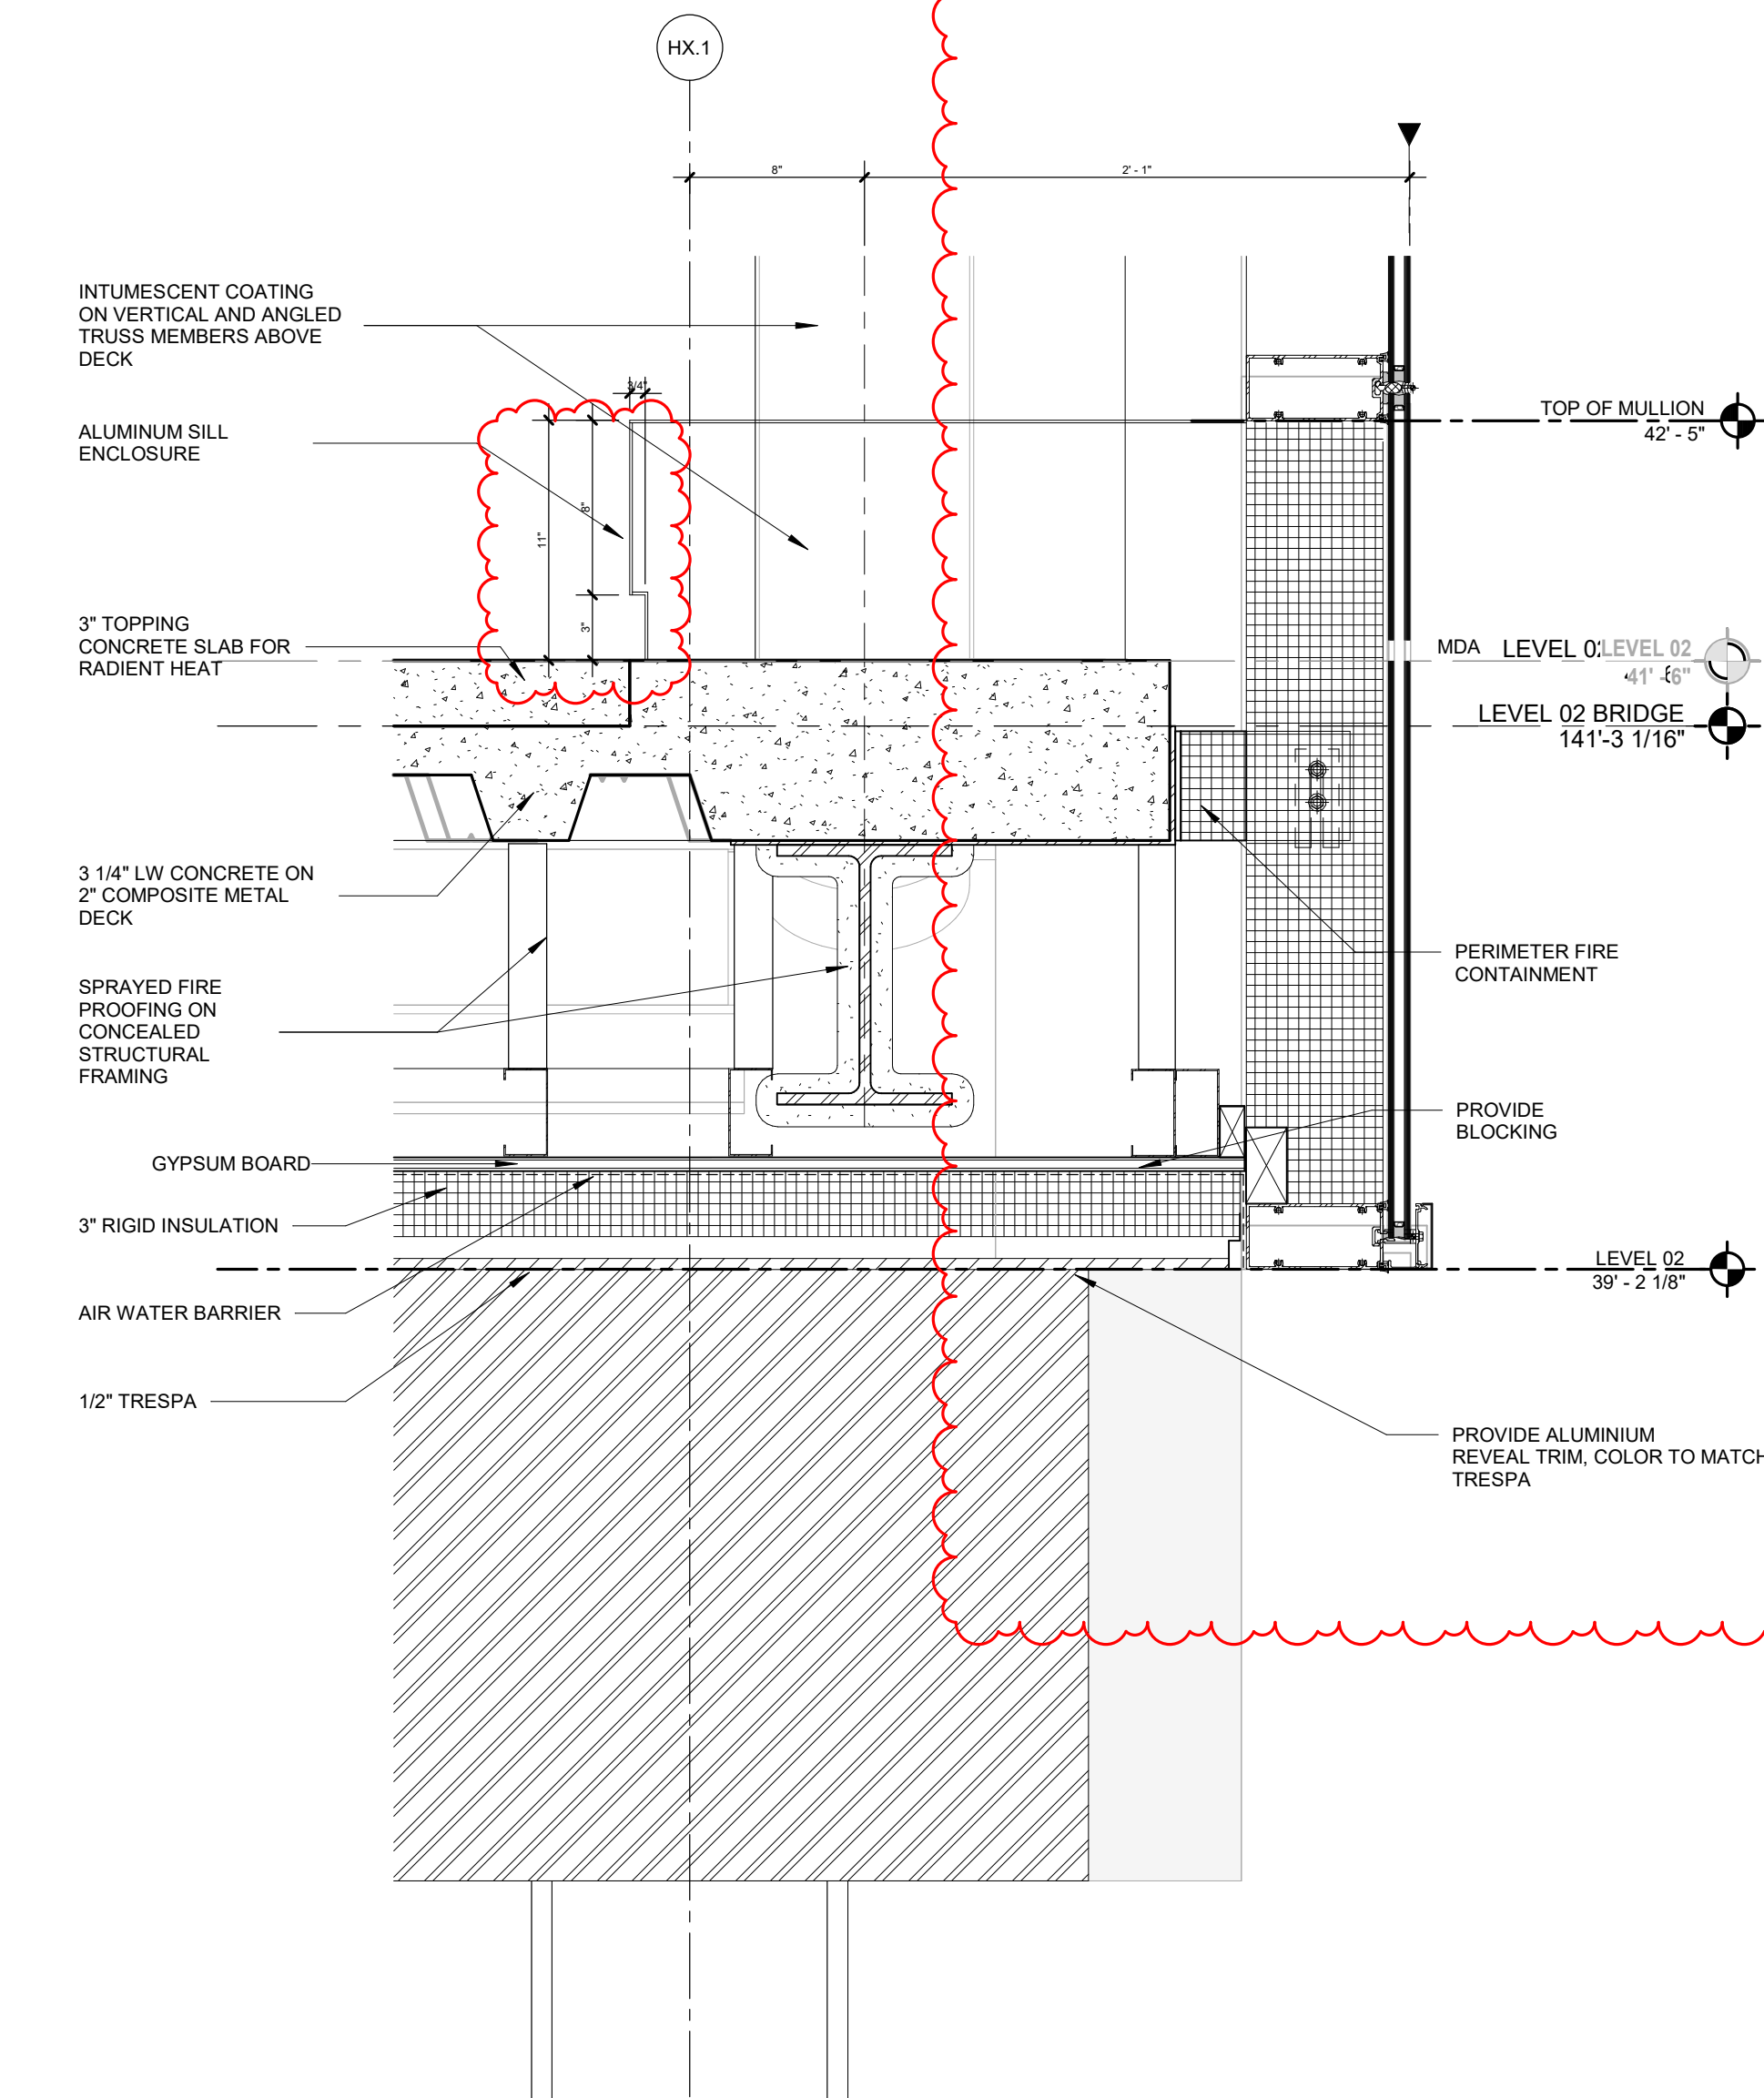

01 SECTION DTL - BRIDGE CW AT SLAB EDGE AND SOFFIT
1 1/2" = 1'-0"

RESERVE FOR DCA STAMP




ARCHITECT
HKS, P.C.
1250 I (EYE) STREET NW, SUITE 600
WASHINGTON, DC 20005
ASSOCIATE ARCHITECT / INTERIOR DESIGNER
ARRAY
1 WEST ELM STREET, SUITE 500
CONSHOHOCKEN, PA 19028
STRUCTURAL ENGINEER
O'DONNELL & NACCARATO
701 MARKET ST., #6000
PHILADELPHIA, PA 19106
MEP-FP / LOW VOLTAGE ENGINEER
BR-A CONSULTING ENGINEERS
2401 WALNUT ST SUITE 701
PHILADELPHIA, PA 19103
HIGHLAND ASSOCIATES
102 HIGHLAND AVE
CLARKS SUMMIT, PA 18411

Cooper University Health Care
COOPER UNIVERSITY HOSPITAL - TOWER A
PROJECT ADDRESS: 1 COOPER PLAZA, CAMDEN, NJ 08103

OWNER
COOPER UNIVERSITY HEALTHCARE
1 COOPER PLAZA
CAMDEN, NJ 08103
PROJECT MANAGER
PURE PM
2026 RICHMOND STREET
PHILADELPHIA, PA 19134
CIVIL ENGINEER / LANDSCAPE
LANGAN
1818 MARKET STREET, SUITE 3300
PHILADELPHIA, PA 19103
SEAL & SIGNATURE

KEY PLAN


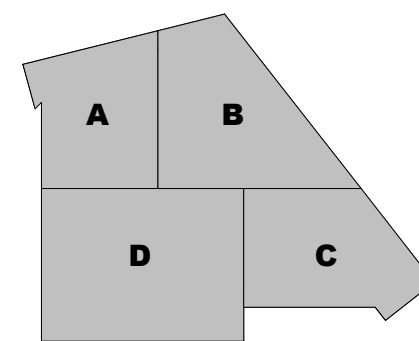


REVISION	NO.	DESCRIPTION	DATE
1	BULLETIN #4		04/28/2025
2	RFI 0420		11/14/2025

HKS PROJECT NUMBER
25695.100
DATE
10/15/2024
ISSUE
CORE & SHELL PERMIT SET
SHEET TITLE
BRIDGE DETAILS

SHEET NO.


A1.370

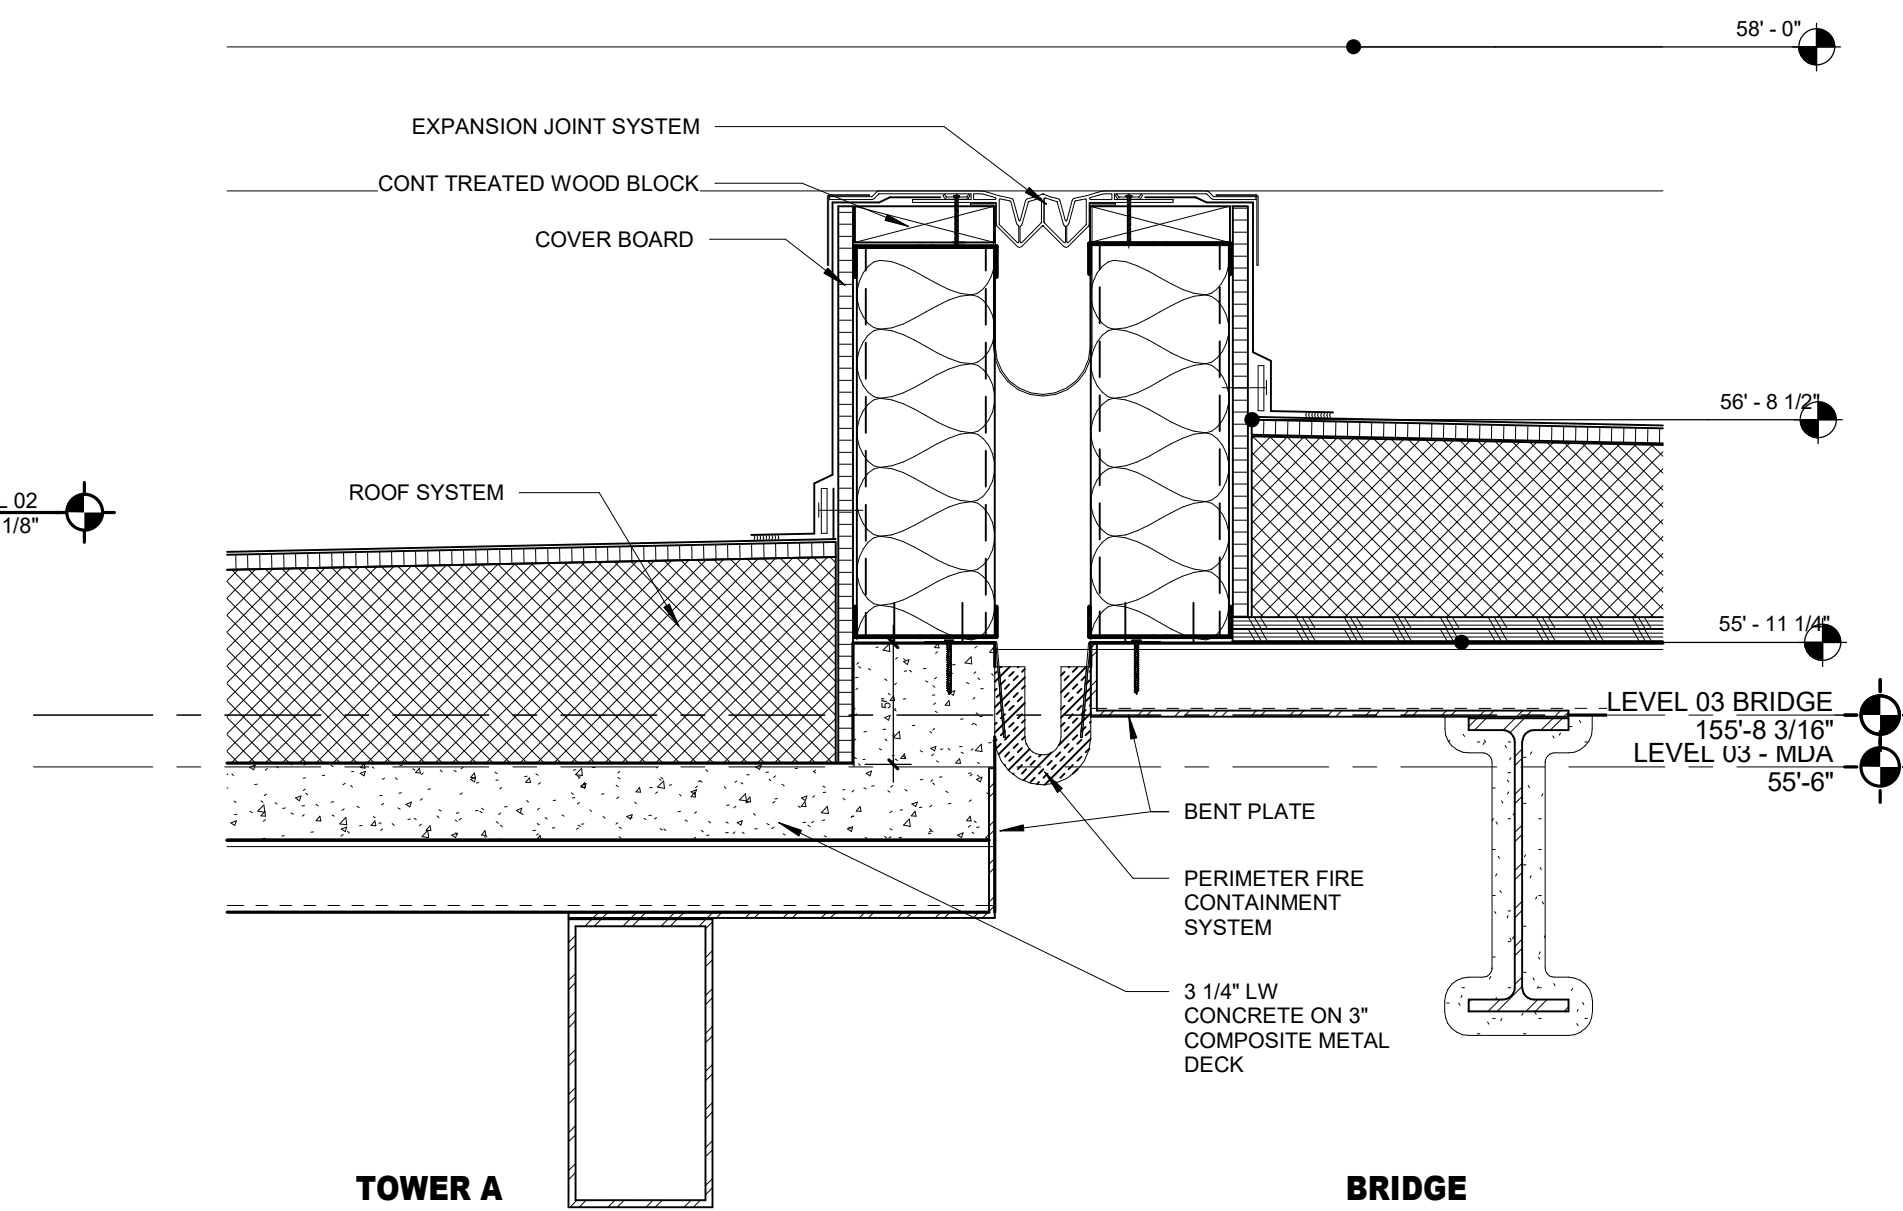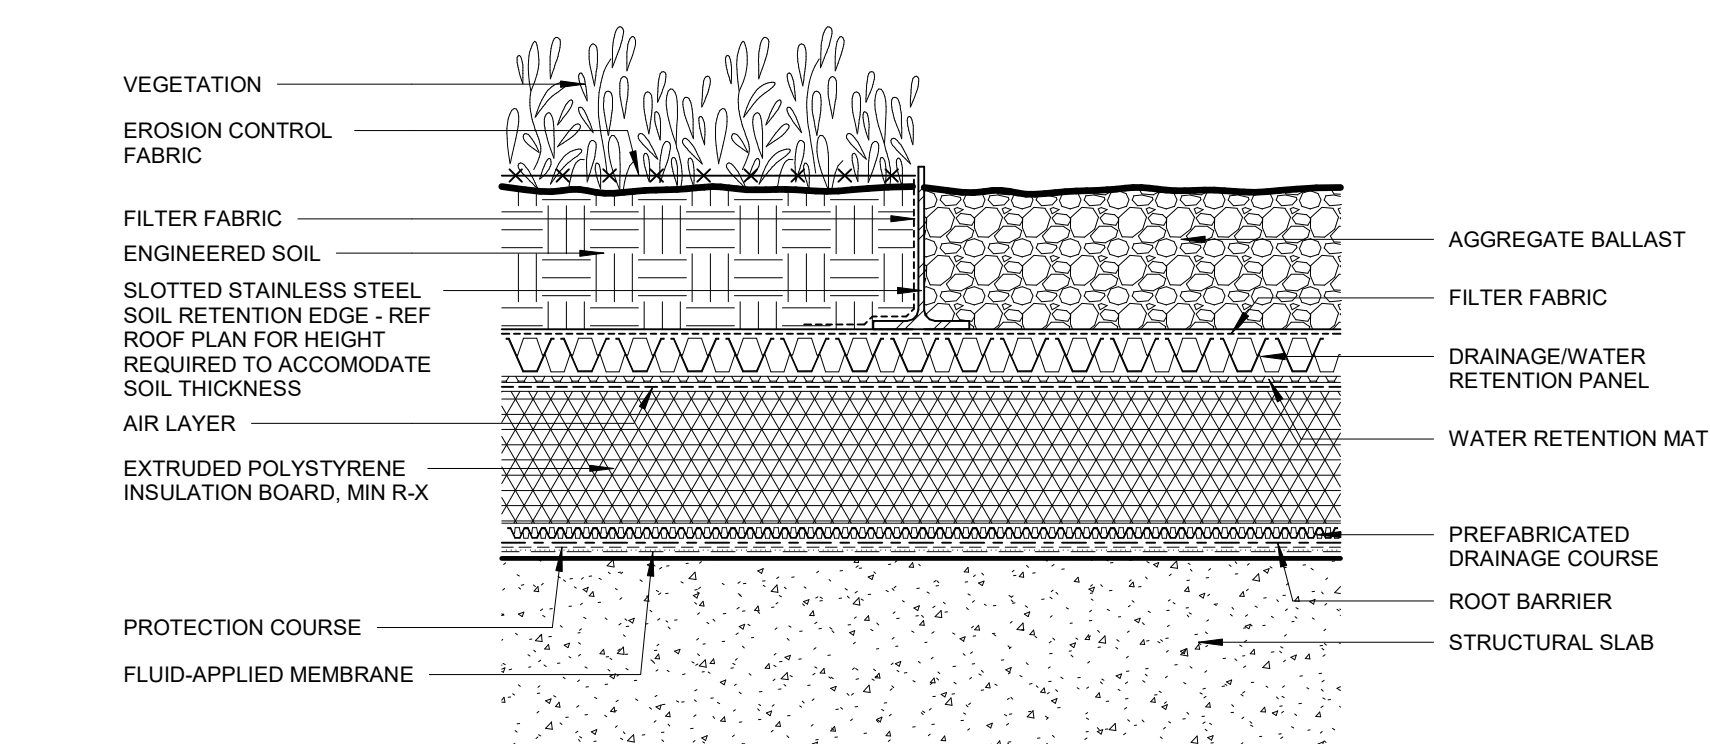


06 **SECTION DTL - TOWER A / BRIDGE PARAPET EXPANSION JOINT**
1 1/2" = 1'-0"




A1.371

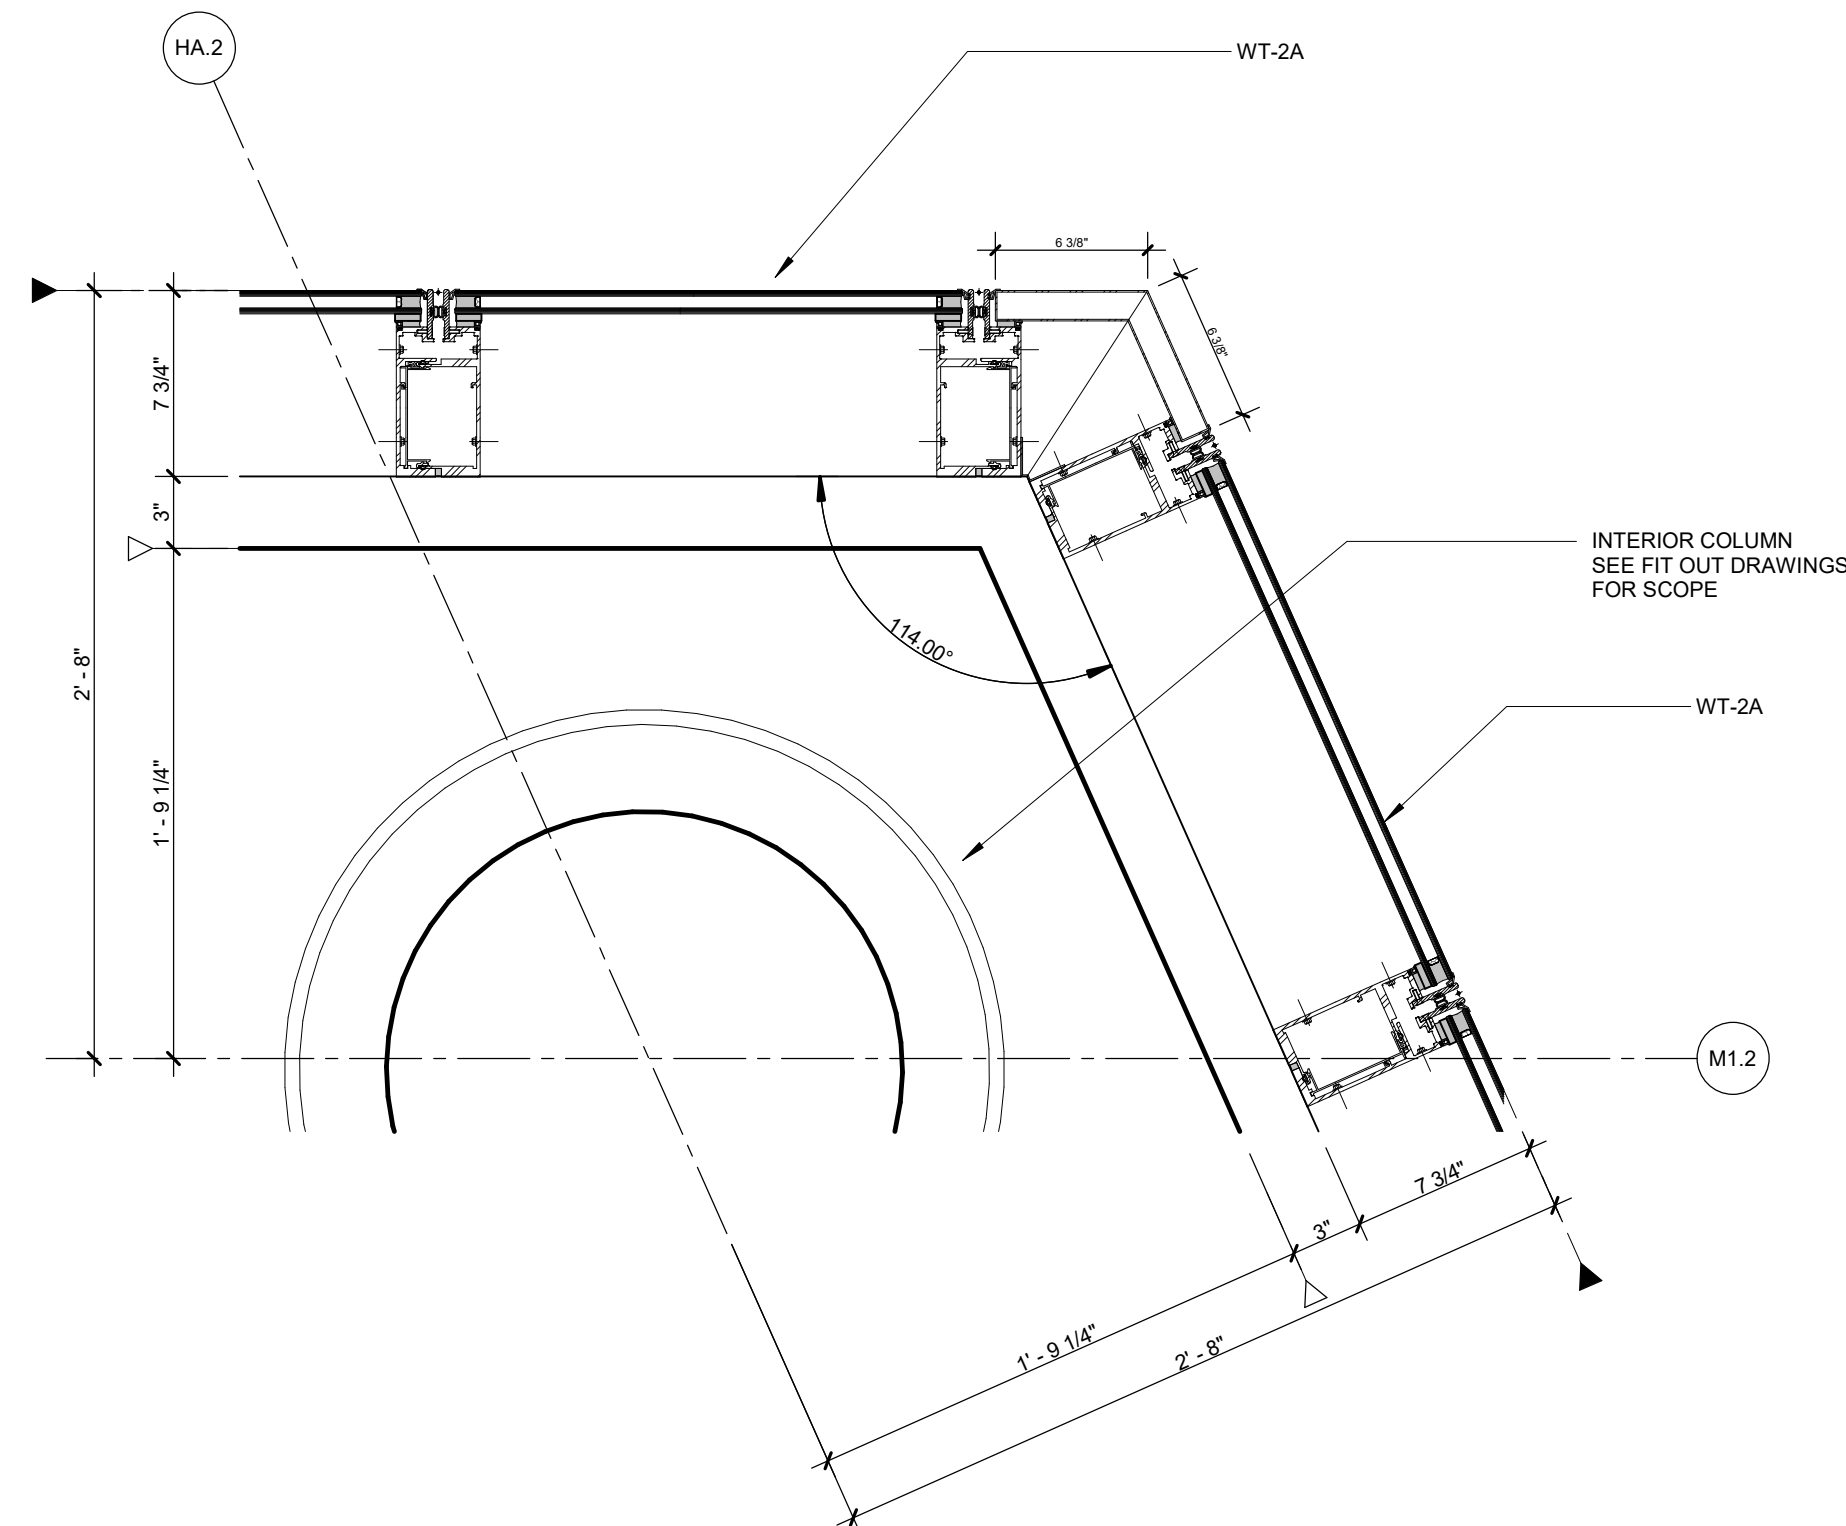


06 PLAN DETAIL - AT NE CORNER

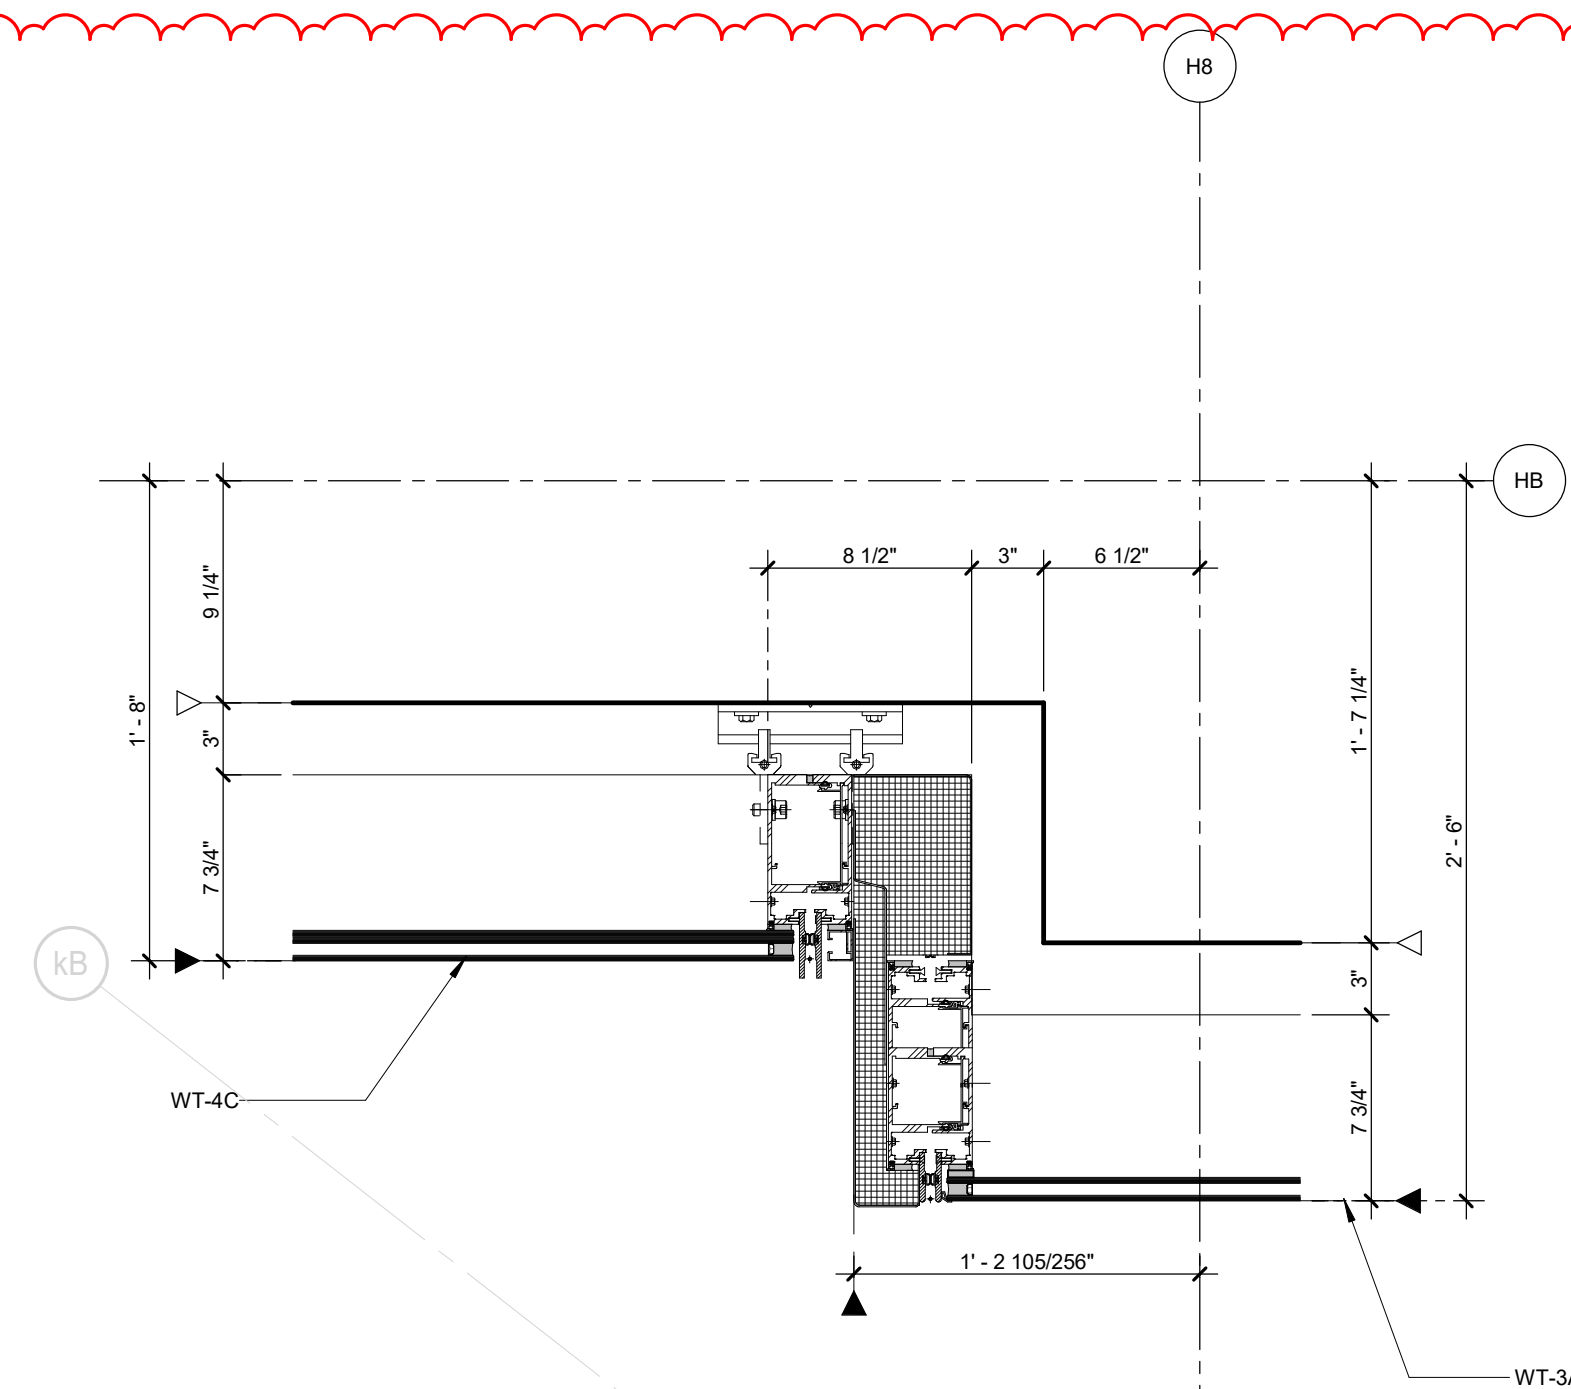


04 PLAN DETAIL - AT SE STAIR TOWER STACKED CW
MULLION
1 1/2" = 1'-0"

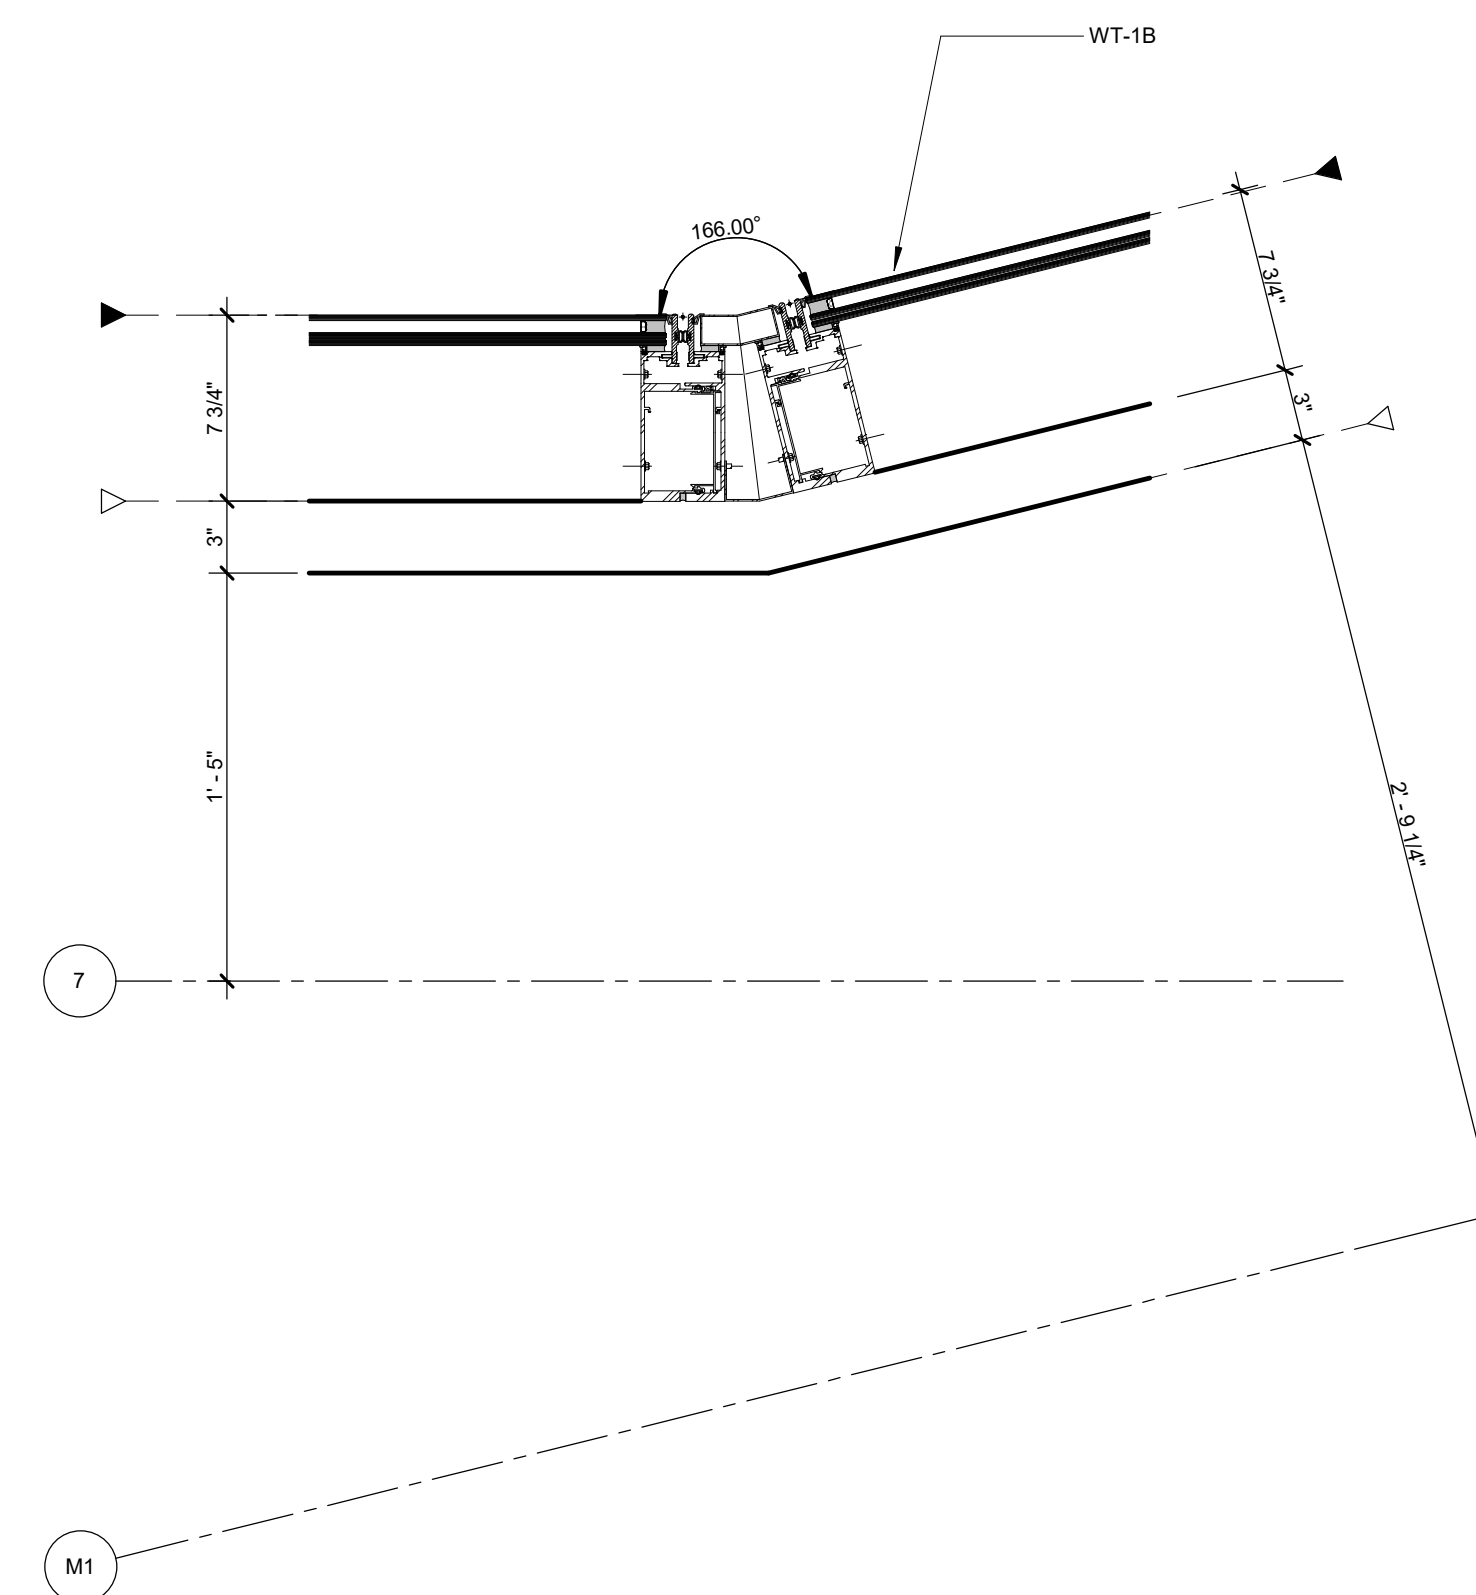


02 PLAN DETAIL - ANGLED CW AT NORTH FACADE

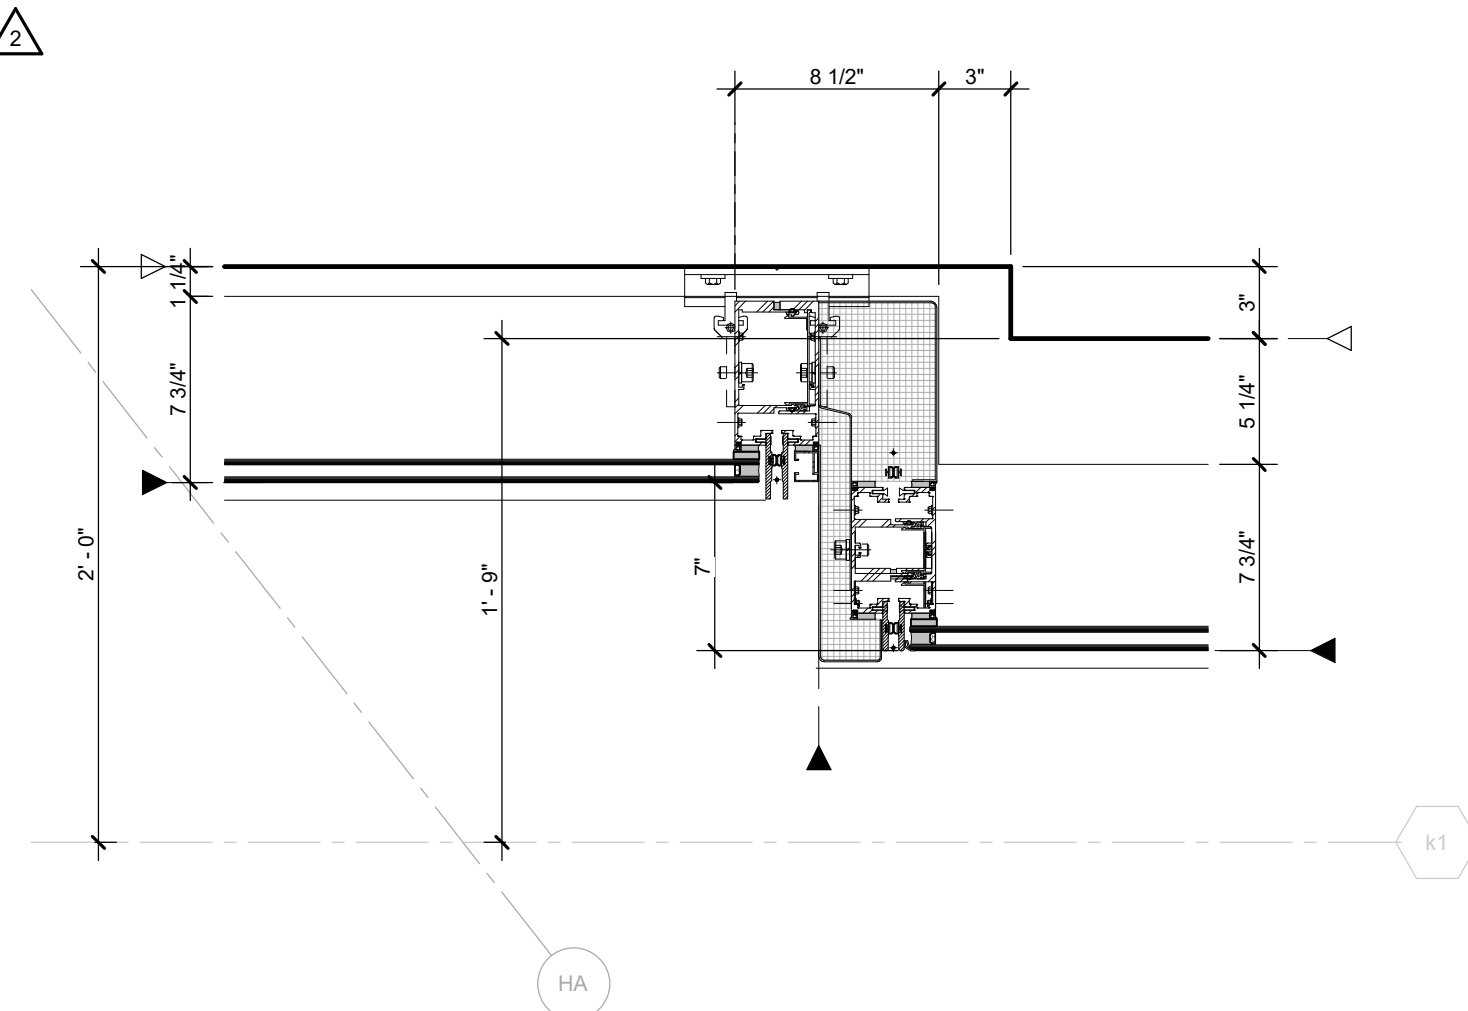


07 PLAN DETAIL - AT BRIDGE
1 1/2" = 1'-0"

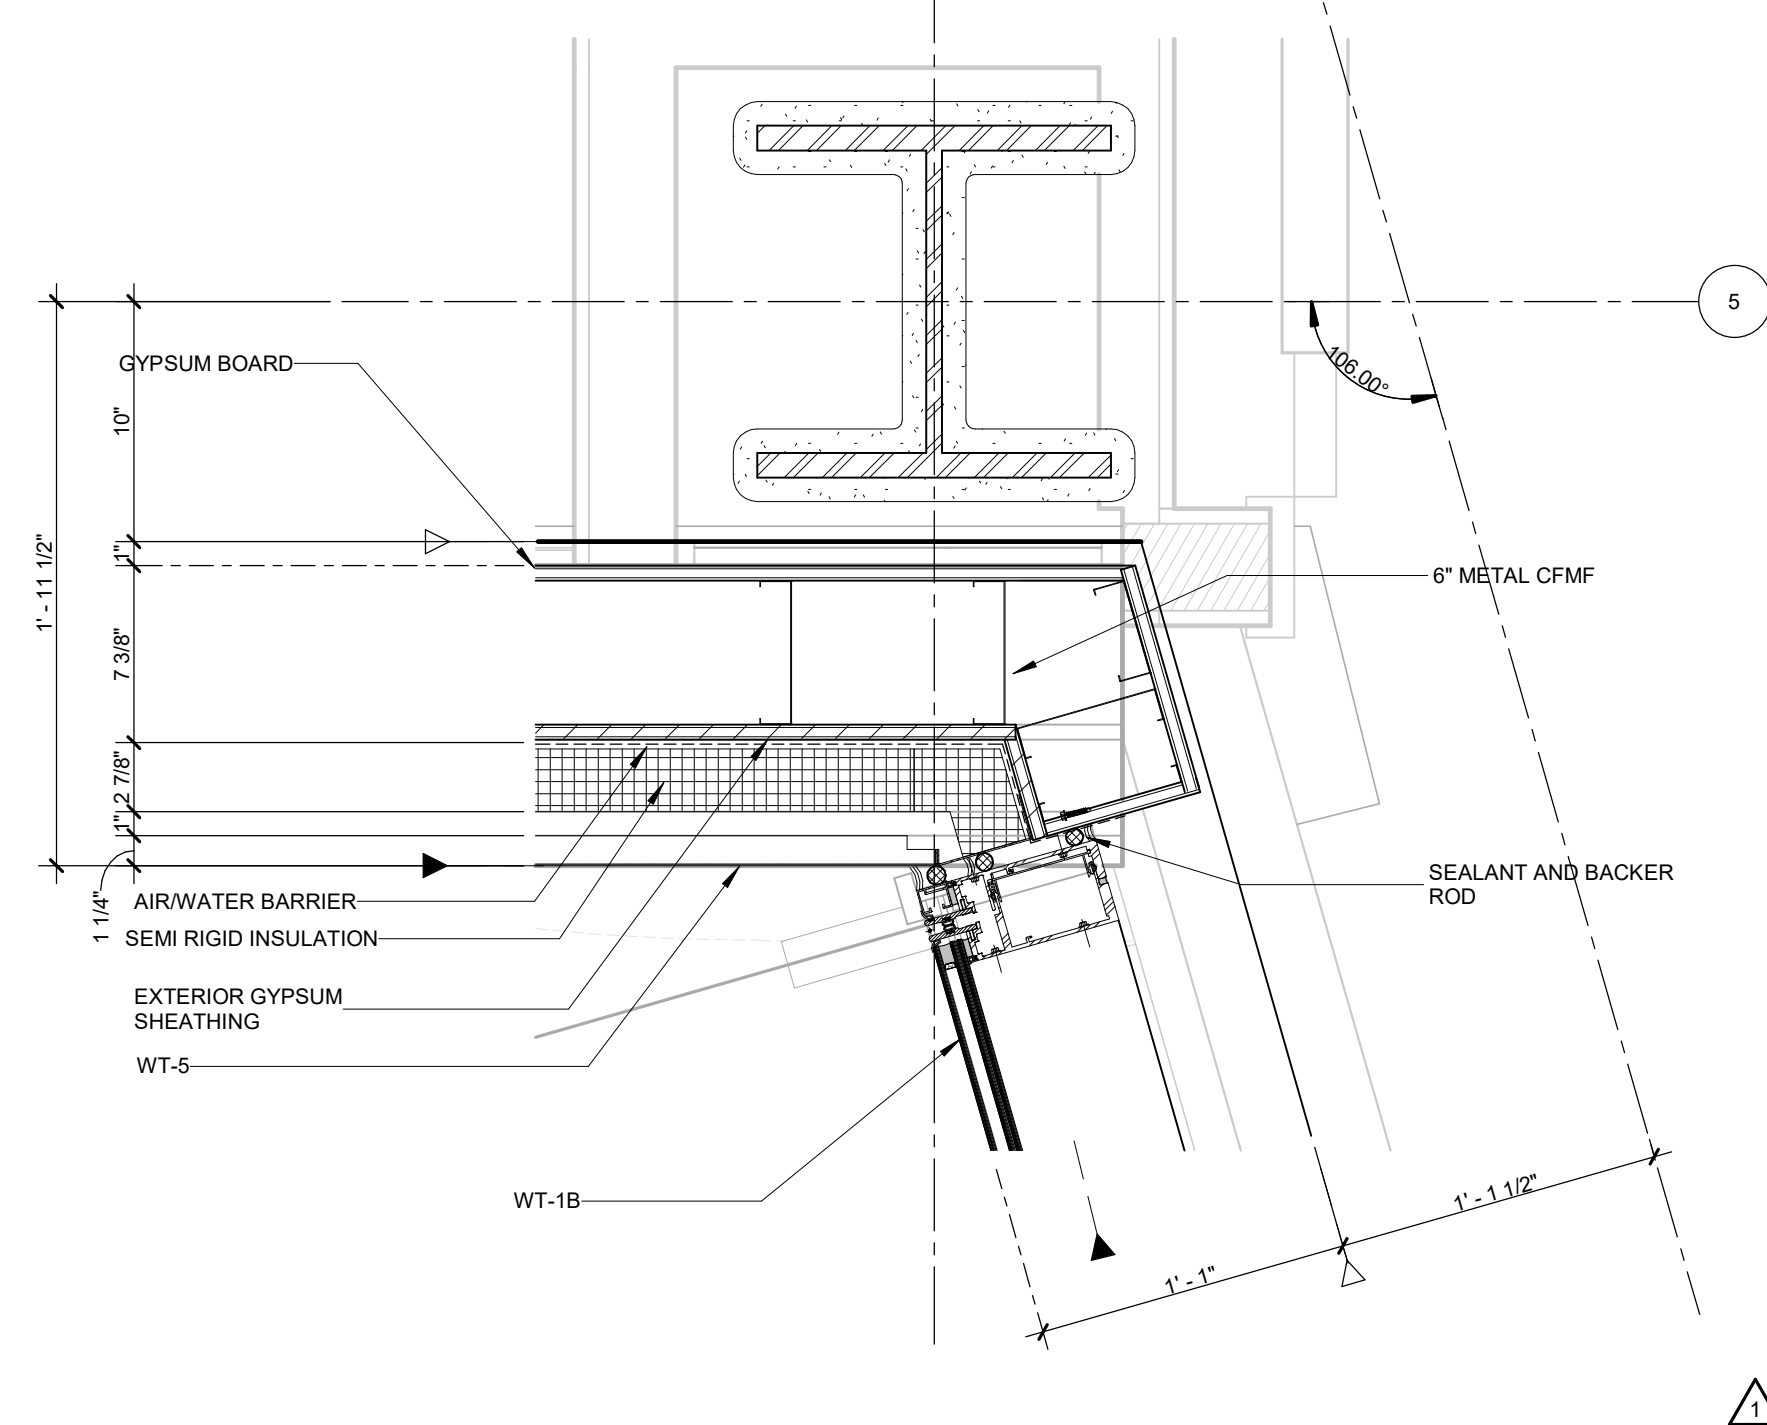

05 **PLAN DETAIL - AT NW FACADE MP WALL TO CW CORNER**
1 1/2" = 1'-0"

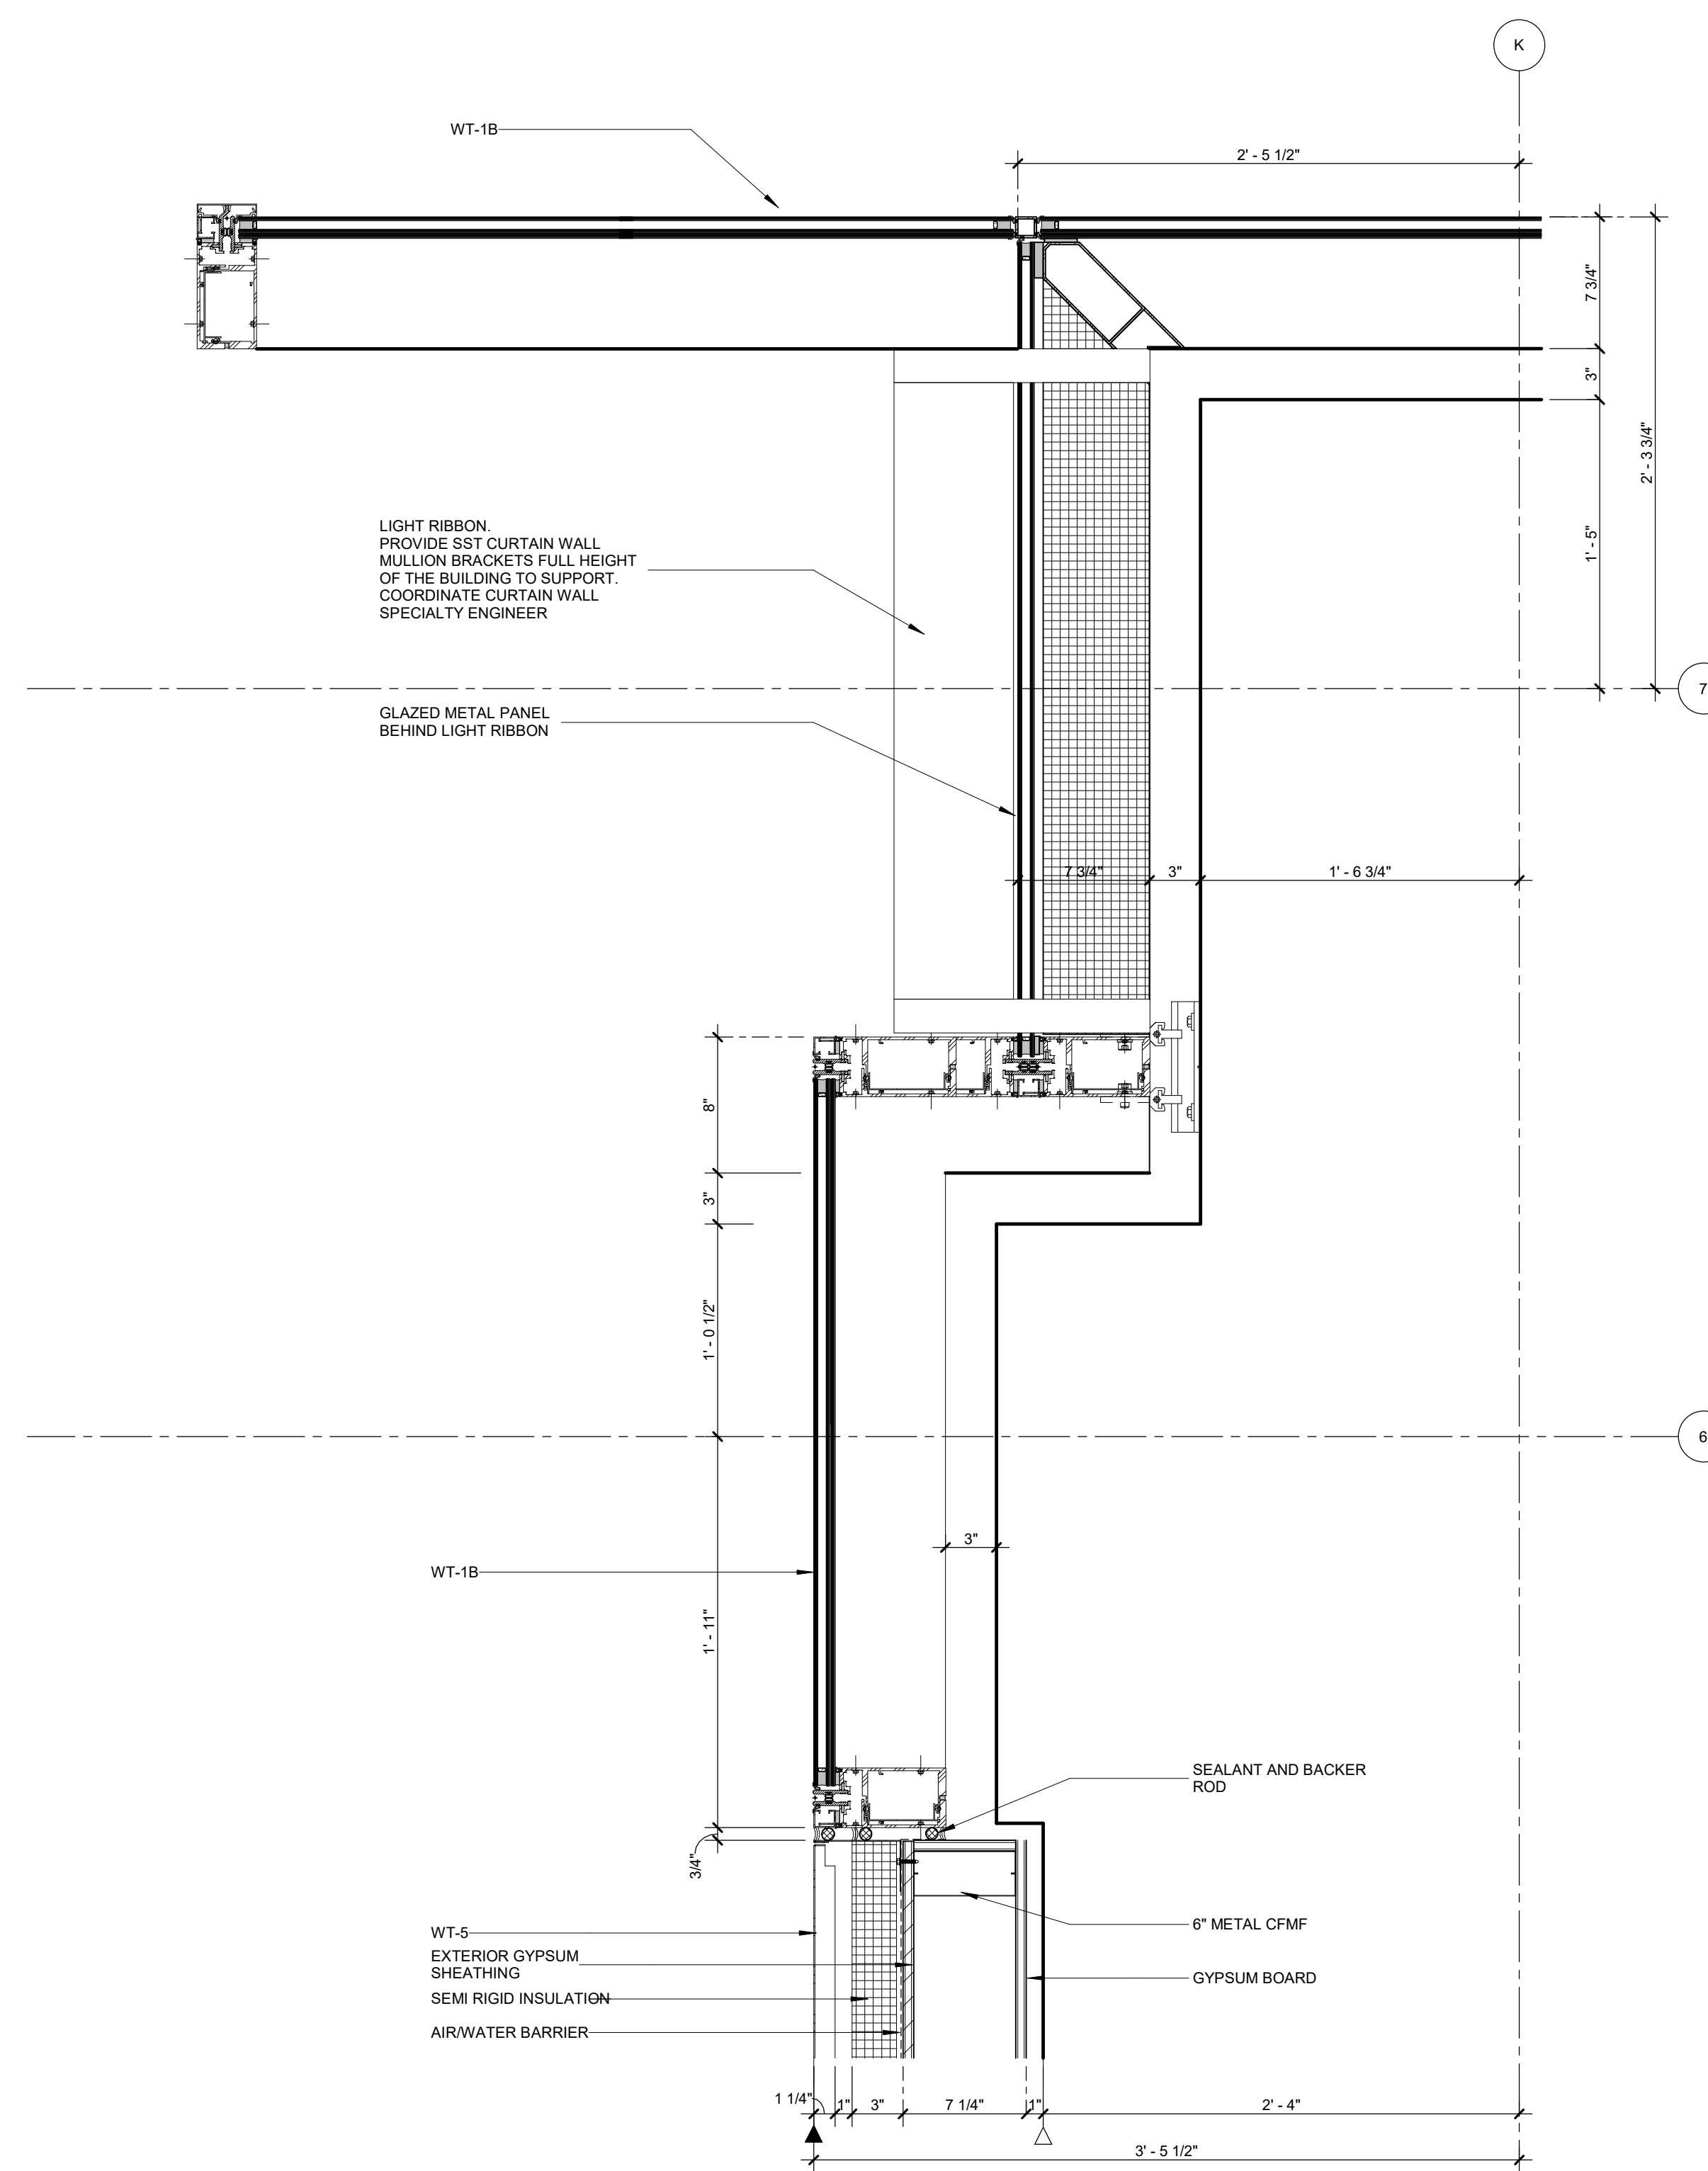

03 PLAN DETAIL - AT NW CORNER

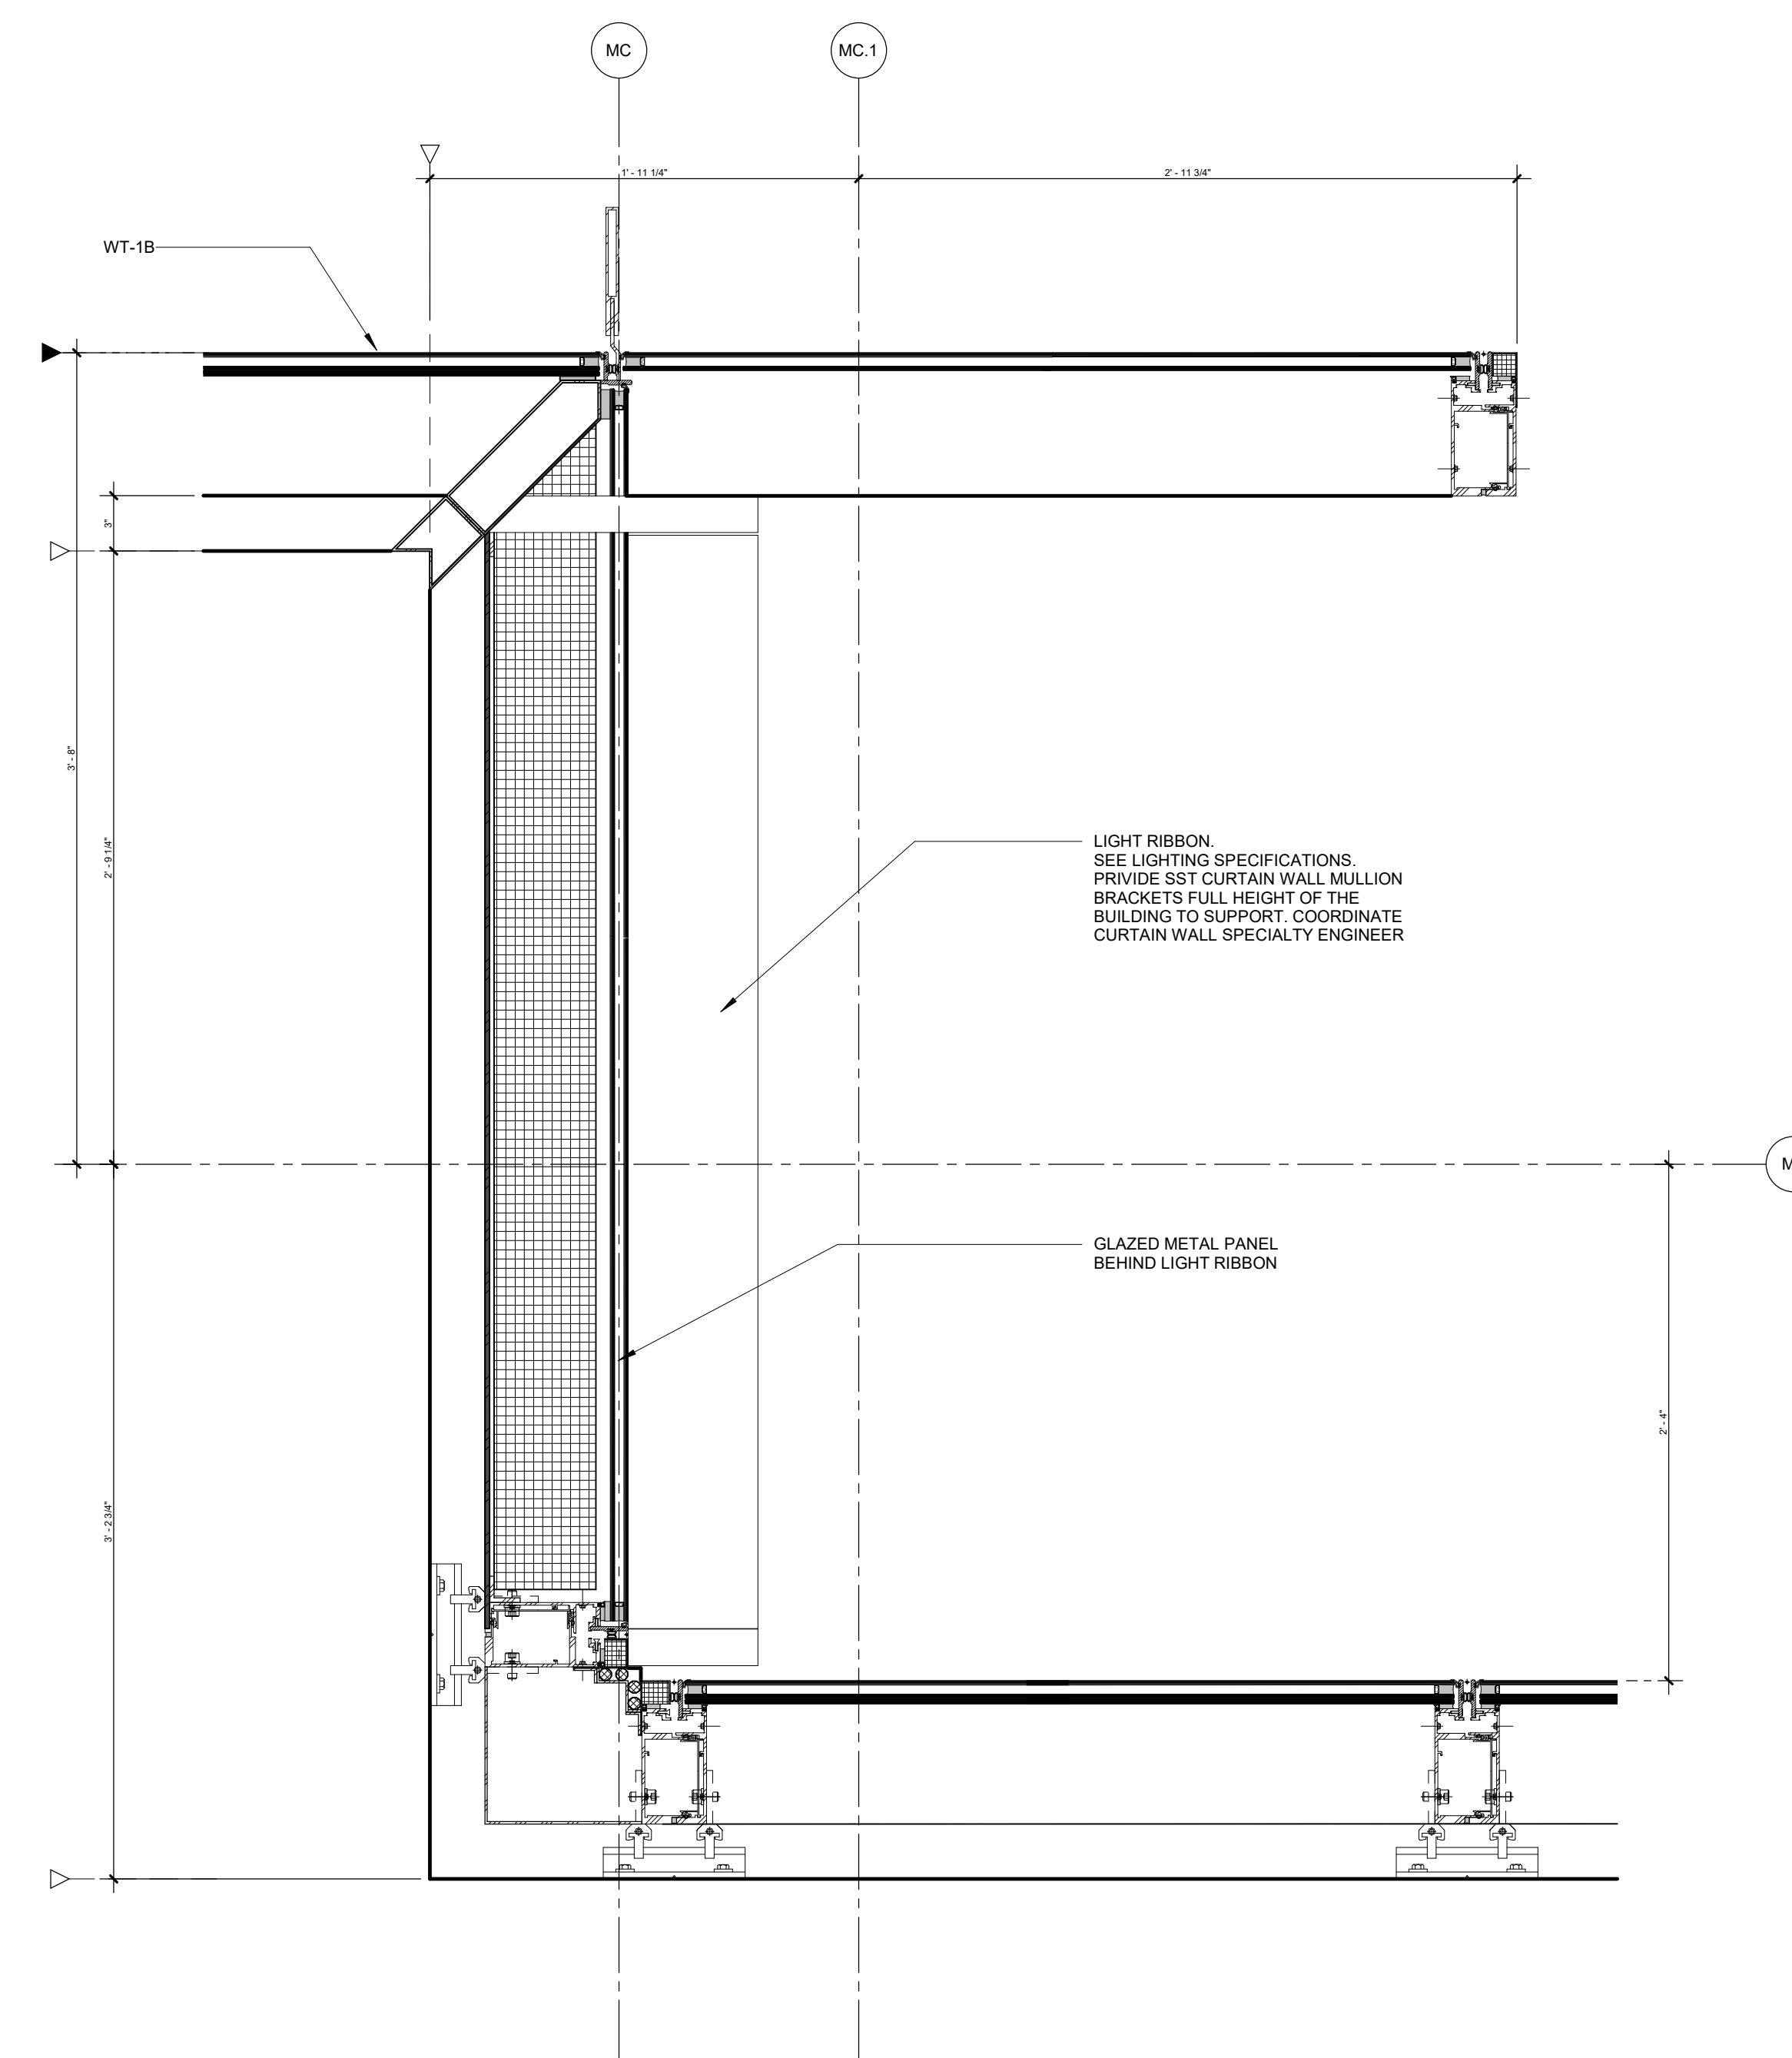

01 PLAN DETAIL - CW AT FLYBY LIGHTING RIBBON
1 1/2" = 1'-0"