


INDEX OF DRAWINGS - CORE SHELL						
SHEET NO.	SHEET NAME		CORE AND SHELL CONST. DOCS - 10/15/24	CORE AND SHELL BULLETIN #1 - 1/22/24	CORE AND SHELL BULLETIN #2 - 10/23/25	CORE AND SHELL BULLETIN #4 - 10/29/2025
ARCHITECTURAL						
A0.00	COVER SHEET					
A0.01	DRAWING INDEX					
A0.02	DRAWING INDEX					
A0.03	INDEX OF DRAWINGS					
A0.04	PROJECT INFORMATION					
APH1-00	TOWER A PHASING PLAN					
AS1.00	OVERALL CAMPUS PLAN					
AS1.01	ARCHITECTURAL SITE PLAN - OVERALL					
AS1.02	ARCHITECTURAL SITE PLAN - STREET LEVEL					
A02.00	DEMOLITION PLAN - BASEMENT					
A02.01	DEMOLITION PLAN - LEVEL 00 OVERBUILD					
A02.01	DEMOLITION PLAN - LEVEL 01					
A02.02	DEMOLITION PLAN - LEVEL 02					
A02.03	DEMOLITION PLAN - LEVEL 03					
A02.04	DEMOLITION PLAN - LEVELS 04-10					
A02.05	DEMOLITION PLAN - LEVEL ROOF					
A03.02	DEMOLITION PLAN - LEVEL 2 KELEMEN + ROBERTS					
A03.02.1	DEMOLITION PLAN - LEVEL 2 MDA					
A03.03	DEMOLITION PLANS - BASEMENT, LEVELS 1, 3-10					
A05.01	SELECTIVE DEMOLITION					
A05.02	SELECTIVE DEMOLITION					
A05.03	SELECTIVE DEMOLITION					
A05.04	SELECTIVE DEMOLITION					
A05.05	SELECTIVE DEMOLITION - DETAILS					
A05.06	SELECTIVE DEMOLITION - DETAILS					
A06.00	DEMOLITION SECTION - STAIRS					
ALS.00	OCCUPANCY + BUILDING SEPARATION DIAGRAMS					
ALS.01	LIFE SAFETY PLAN - BASEMENT					
ALS.02	LIFE SAFETY PLAN - LEVEL 01					
ALS.03	LIFE SAFETY PLAN - LEVEL 02					
ALS.04	LIFE SAFETY PLAN - BRIDGE + MD ANDERSON					
ALS.05	LIFE SAFETY PLAN - LEVEL 03					
ALS.06	IP PERIMETER PLAN - LEVEL 03					
ALS.07	LIFE SAFETY PLAN - LEVEL 04					
ALS.08	LIFE SAFETY PLAN - LEVEL 05					
ALS.09	IP PERIMETER PLAN - LEVEL 06					
ALS.10	LIFE SAFETY PLAN - LEVEL 07					
ALS.11	LIFE SAFETY PLAN - LEVEL 08					
ALS.12	LIFE SAFETY PLAN - LEVEL 09					
ALS.13	LIFE SAFETY PLAN - LEVEL 10					
ALS.14	LIFE SAFETY PLAN - PENTHOUSE					
ALS.15	DIMENSION CONTROL PLAN					
AT.100	CORE & SHELL FLOOR PLAN - LEVEL 00					
AT.100.1	CORE & SHELL FLOOR PLAN - LEVEL 00 - OVERBUILD					
AT.101	CORE & SHELL FLOOR PLAN - LEVEL 01					
AT.101.1	CORE & SHELL FLOOR PLAN - LEVEL 01 - OVERBUILD					
AT.102	CORE & SHELL FLOOR PLAN - LEVEL 02					
AT.102.1	CORE & SHELL FLOOR PLAN - LEVEL 02 - OVERBUILD					
AT.103	CORE & SHELL FLOOR PLAN - LEVEL 03					
AT.104	CORE & SHELL FLOOR PLAN - LEVEL 04					
AT.105	CORE & SHELL FLOOR PLAN - LEVEL 05					
AT.106	CORE & SHELL FLOOR PLAN - LEVEL 06					
AT.107	CORE & SHELL FLOOR PLAN - LEVEL 07					
AT.108	CORE & SHELL FLOOR PLAN - LEVEL 08					
AT.109	CORE & SHELL FLOOR PLAN - LEVEL 09					
AT.110	CORE & SHELL FLOOR PLAN - LEVEL 10					
AT.111	CORE & SHELL FLOOR PLAN - ROOF					
AT.112	CORE & SHELL FLOOR PLAN - LEVEL PH ROOF					
AT.113	ENLARGED PLANS - LEVEL 01					
AT.120	EDGE OF SLAB PLAN - LEVEL 00					
AT.201	EDGE OF SLAB PLAN - LEVEL 01					
AT.202	EDGE OF SLAB PLAN - LEVEL 02					
AT.203	EDGE OF SLAB PLAN - LEVEL 03					
AT.204	EDGE OF SLAB PLAN - LEVEL 04					
AT.205	EDGE OF SLAB PLAN - LEVEL 05					
AT.206	EDGE OF SLAB PLAN - LEVEL 06					
AT.207	EDGE OF SLAB PLAN - LEVEL 07					
AT.208	EDGE OF SLAB PLAN - LEVEL 08					
AT.209	EDGE OF SLAB PLAN - LEVEL 09					
AT.210	EDGE OF SLAB PLAN - LEVEL 10					
AT.211	EDGE OF SLAB PLAN - LEVEL ROOF					
AT.301	BRIDGE FLOOR PLAN					
AT.340	BRIDGE CEILING PLAN & SITE PLAN					
AT.350	BRIDGE ELEVATIONS					
AT.360	BRIDGE SECTIONS					
AT.370	BRIDGE DETAILS					
AT.371	BRIDGE DETAILS					
AT.501	KELEMEN ELEVATIONS AND DETAILS					
LA1.300	COVER PAGE					
LA1.301	BRIDGE FLOOR PLAN					
LA1.302	BRIDGE CEILING PLAN & SITE PLAN					
LA1.350	BRIDGE ELEVATIONS					
LA1.360	BRIDGE SECTIONS					
A2.202	FIT OUT FLOOR PLAN - LEVEL 02					
A2.202.1	FIT OUT FLOOR PLAN - LEVEL 02 KELEMEN					
A2.202.2	FIT OUT FLOOR PLAN - LEVEL 02 BRIDGE + PITS RENOVATIONS					
A2.203	FIT OUT FLOOR PLAN - LEVEL 03					
A2.205	FIT OUT FLOOR PLAN - LEVEL 05					
A2.207	FIT OUT FLOOR PLAN - LEVEL 06					
A2.208	FIT OUT FLOOR PLAN - LEVEL 08					
A2.209	FIT OUT FLOOR PLAN - LEVEL 09					
A2.210	FIT OUT FLOOR PLAN - LEVEL 10					
A2.211	FIT OUT FLOOR PLAN - PENTHOUSE					
A2.320	LEVEL 02 - OR #0, HYBRID					
A2.320.1	LEVEL 02 - OR #0, HYBRID CTRL					
A2.321	LEVEL 02 - OR #2, CARDIAC					
A2.322	LEVEL 02 - OR #4, CARDIAC					
A2.323	LEVEL 02 - OR #5, CARDIAC					
A2.324	LEVEL 02 - HYBRID OR #7					
A2.324.1	LEVEL 02 - HYBRID OR #1					
A2.325	LEVEL 02 - HYBRID OR #6					
A2.326	LEVEL 02 - HYBRID OR SUPPORT					
A2.327	LEVEL 02 - TYPICAL PERIOP BAYS					
A2.328	LEVEL 02 - PERIOP WORKSTATION					
A2.329	LEVEL 02 - PERIOP CLINIC SUPPORT					
A2.330	LEVEL 02 - PUMP ROOM					
A2.331	LEVEL 03 - TYPICAL ANTEPARTUM ROOM					
A2.332	LEVEL 03 - C-SECTION - NORTH					
A2.333	LEVEL 03 - C-SECTION - SOUTH					
A2.334	LEVEL 03 - TYPICAL TRIAGE ROOM & PREP / RECOVERY ROOM					
A2.335	LEVEL 03 - TYPICAL LABOR & DELIVERY ROOM					
A2.336	LEVEL 03 - TRIAGE TEAM WORKSTATION					
A2.337	LEVEL 03 - CLINICAL TRIAGE ROOMS					
A2.338	LEVEL 03 - SOUTH TEAM WORKSTATION					
A2.339	LEVEL 03 - NORTH TEAM WORKSTATION					
A2.340	LEVEL 05 - NURSERY & INFANT EXAM					
A2.341	LEVEL 05 - TYPICAL POSTPARTUM ROOM					
A2.342	LEVEL 05 - SOUTH TEAM WORKSTATION					
A2.343	LEVEL 06 - TYPICAL UNIVERNAL PATIENT ROOM					
A2.344	LEVEL 06 - UNIVERNAL CLINICAL CORE					
A2.345	LEVEL 08 - SOUTH TEAM WORKSTATION					
A2.346	LEVEL 08 - NORTH TEAM WORKSTATION					
A2.347	LEVEL 10 - TYPICAL LEVEL 10 PATIENT ROOM					
A3.01	PARTITION TYPES					
A3.02	PARTITION HEAD DETAILS					
A3.04	PARTITION FRAMING DETAILS					
A3.05	TYPICAL GYP BD DETAILS					
A3.06	TYPICAL GYP BD DETAILS					
A3.10	METAL FABRICATIONS					
A3.11	INTERIOR EXPANSION JOINTS					
A3.12	LOCKERS, ACCESSORIES, AND EQUIPMENT					
A3.20	TYPICAL TOILET LAYOUTS AND STD ACCESSORIES					
A3.22	ENLARGED TOILET TYPES - LEVEL 02 & ABOVE					
A3.23	ENLARGED TOILET ROOMS - MULTI-OCCUPANT - LEVEL 02					
A3.26	ENLARGED PATIENT TOILET TYPES					
A3.27	TYPICAL SHOWER DETAILS					
A3.30	DOOR SAFETY GLAZING AND LOUVER INFORMATION					
A3.31	DOOR INFORMATION - CORE + SHELL					
A3.32	DOOR SCHEDULE AND INFORMATION - LEVELS BASEMENT .01, + 02					
A3.33	DOOR SCHEDULE AND INFORMATION - LEVELS 03, 04					
A3.34	DOOR SCHEDULE AND INFORMATION - LEVELS 05, 06, 07					
A3.35	DOOR SCHEDULE AND INFORMATION - LEVELS 08, 09, 10					
A3.36	DOOR AND LEAD LINED DETAILS					
A3.44	INTERIOR DETAILS - PLANS LEVEL 02					
A3.45	INTERIOR DETAILS - PLANS LEVEL 03					
A3.46	INTERIOR DETAILS - PLANS LEVEL 04					
A3.47	INTERIOR DETAILS - SECTIONS					
A3.48	INTERIOR DETAILS - SYSTEM DETAILS					
A3.49	INTERIOR DETAILS - SYSTEM DETAILS					
A3.50	CABINET DETAILS					
A3.52	CABINET DETAILS					
A3.53	CABINET DETAILS					
A3.63	LEVEL 02 INTERIOR ELEVATIONS					
A3.63.1	LEVEL 02 INTERIOR ELEVATIONS - BRIDGE					
A3.65	LEVELS 03 + 05 INTERIOR ELEVATIONS					
A3.69	LEVEL 06 INTERIOR ELEVATIONS					

INDEX OF DRAWINGS - CORE SHELL		CORE AND SHELL CONST. DOCS - 10/15/24	CORE AND SHELL BULLETIN #1 - 1/22/24	CORE AND SHELL BULLETIN #2 - 10/23/25	CORE AND SHELL BULLETIN #4 - 04/28/2026	CORE AND SHELL BULLETIN #6 - 07/03/2026	CORE AND SHELL BULLETIN #8 - 03/26/2026
SHEET NO.	SHEET NAME						
A3.90	LINEN / WASTE CHUTES - TYP LAYOUT AND DETAILS						
A4.02	REFLECTED CEILING PLAN - LEVEL 02						
A4.02.1	REFLECTED CEILING PLAN - LEVEL 02 KELEMEN						
A4.02.2	REFLECTED CEILING PLAN - LEVEL 02 BRIDGE						
A4.03	REFLECTED CEILING PLAN - LEVEL 03						
A4.05	REFLECTED CEILING PLAN - LEVEL 05						
A4.06	REFLECTED CEILING PLAN - LEVEL 06						
A4.07	REFLECTED CEILING PLAN - LEVEL 07						
A4.08	REFLECTED CEILING PLAN - LEVEL 08						
A4.09	REFLECTED CEILING PLAN - LEVEL 09						
A4.10	REFLECTED CEILING PLAN - LEVEL 10						
A4.20	CEILING DETAILS, TYPICAL						
A4.25	CEILING DETAILS						
A5.00	ARCHITECTURAL RENDERINGS						
A5.01	OVERALL BUILDING ELEVATIONS						
A5.02	OVERALL BUILDING ELEVATIONS						
A5.03	PARTIAL BUILDING ELEVATIONS						
A5.04	PARTIAL BUILDING ELEVATIONS						
A5.05	PARTIAL BUILDING ELEVATIONS						
A5.06	PARTIAL BUILDING ELEVATIONS						
A5.07	PARTIAL BUILDING ELEVATIONS						
A5.08	PARTIAL BUILDING ELEVATIONS						
A5.09	PARTIAL BUILDING ELEVATIONS						
A5.10	PARTIAL BUILDING ELEVATIONS						
A6.00	BUILDING AXONOMETRICS AND SECTIONS INDEX						
A6.01	BUILDING SECTIONS						
A6.02	BUILDING SECTIONS						
A6.10	WALL SECTIONS - PAVILION						
A6.12	WALL SECTIONS - MLK FOUNDATION						
A6.13	WALL SECTIONS - MLK FOUNDATION						
A6.14	WALL SECTIONS - MLK CURTAIN WALL						
A6.16	WALL SECTIONS - HADSON FOUNDATION						
A6.17	WALL SECTIONS - HADSON CURTAIN WALL						
A6.19	WALL SECTIONS - SE STAIR + BRIDGE						
A6.20	WALL SECTIONS - SE STAIR						
A6.24	WALL SECTIONS - KELEMEN BASE						
A6.25	WALL SECTIONS - KELEMEN						
A6.26	WALL SECTIONS - KELEMEN						
A6.27	WALL SECTIONS - ROBERTS BASE						
A6.28	WALL SECTIONS - ROBERTS BASE						
A6.29	WALL SECTIONS - ROBERTS						
A6.30	WALL SECTIONS - ROBERTS						
A6.31	WALL SECTIONS - PAVILION TO TOWER						
A6.33	WALL SECTIONS - ROOF						
A7.01	GLAZED ALUM FRAMING SYSTEMS						
A7.04	SINGLE PLY ROOFING DETAILS 01						
A7.05	SINGLE PLY ROOFING DETAILS 02						
A7.06	BELOW GRADE WATERPROOFING DETAILS 01						
A7.07	METAL FABRICATIONS 02						
A7.10	EXTERIOR SECTION DETAILS						
A7.11	EXTERIOR SECTION DETAILS						
A7.12	EXTERIOR SECTION DETAILS						
A7.13	EXTERIOR SECTION DETAILS						
A7.14	EXTERIOR SECTION DETAILS						
A7.15	EXTERIOR SECTION DETAILS						
A7.16	EXTERIOR SECTION DETAILS						
A7.17	EXTERIOR SECTION DETAILS						
A7.18	EXTERIOR SECTION DETAILS						
A7.19	EXTERIOR SECTION DETAILS						
A7.20	EXTERIOR SECTION DETAILS						
A7.21	EXTERIOR SECTION DETAILS						
A7.22	EXTERIOR SECTION DETAILS						
A7.23	EXTERIOR SECTION DETAILS						
A7.24	EXTERIOR SECTION DETAILS						
A7.25	EXTERIOR SECTION DETAILS						
A7.26	EXTERIOR SECTION DETAILS						
A7.30	EXTERIOR PLAN DETAILS						
A7.32	EXTERIOR PLAN DETAILS						
A7.34	EXTERIOR PLAN DETAILS						
A7.35	EXTERIOR PLAN DETAILS						
A7.36	EXTERIOR PLAN DETAILS						
A7.37	EXTERIOR PLAN DETAILS						
A7.38	EXTERIOR PLAN DETAILS						
A8.00	STEEL STAIR PLANS, SECTIONS, AND DETAILS						
A8.01	STAIR PLANS AND SECTIONS						
A8.02	STAIR PLANS AND SECTIONS						
A8.03	STAIR PLANS AND SECTIONS						
A8.04	STAIR PLANS AND SECTIONS						
A8.05	RAMP PLANS AND SECTIONS						
A8.06	STEEL STAIR WITH CABLE RAILING SECTIONS, AND DETAILS						
A8.20	ELEVATOR PLANS						
A8.22	ELEVATOR PLANS						
A8.23	WALL SECTIONS - ELEV R1 + R8						
A8.24	WALL SECTIONS - ELEV R7 + R8						
A8.31	ELEVATOR DETAILS						
MEDICAL EQUIPMENT							
EQ.200	RESPONSIBILITY MATRIX - EQUIPMENT						
EQ.202	EQUIPMENT PLAN - LEVEL 02						
EQ.202.1	EQUIPMENT PLAN - LEVEL 02 KELEMEN						
EQ.203	EQUIPMENT PLAN - LEVEL 03						
EQ.205	EQUIPMENT PLAN - LEVEL 05						
EQ.206	EQUIPMENT PLAN - LEVELS 06 TO 10						
STRUCTURAL							
S-000	COVER SHEET						
S-001	GENERAL NOTES						
S-002	SCHEDULES						
S-003	COLUMN SCHEDULE						
S-004	SPECIAL INSPECTIONS						
S-010	DESIGN LOAD MAPS						
S-011	DESIGN LOAD MAPS						
S-012	DESIGN LOAD MAPS						
S-013	DESIGN LOAD MAPS						
S-100	FOUNDATION PLAN						
S-101	FIRST FLOOR FRAMING PLAN						
S-102	SECOND FLOOR FRAMING PLAN						
S-102A	SECOND FLOOR FRAMING PLAN						
S-103	THIRD FLOOR FRAMING PLAN						
S-104	FOURTH FLOOR FRAMING PLAN						
S-107	FIFTH FLOOR FRAMING PLAN						
S-108	SIXTH FLOOR FRAMING PLAN						
S-107	SEVENTH FLOOR FRAMING PLAN						
S-108	EIGHTH FLOOR FRAMING PLAN						
S-109	NINTH FLOOR FRAMING PLAN						
S-110	TENTH FLOOR FRAMING PLAN						
S-111	ROOF FRAMING PLAN						
S-112	DUNNAGE FRAMING PLAN						
S-113	PENTHOUSE ROOF FRAMING PLAN						
S-114	SCREENWALL CATWALK FRAMING PLAN						
S-115	SCREENWALL FRAMING PLAN						
S-116	SCREENWALL ELEVATIONS & SECTIONS						
S-120	ROBERTS OVERBUILD PLANS						
S-121	ROBERTS MECHANICAL MEZZANINE PLANS						
S-130	MAT FOUNDATION PLANS						
S-131	MAT FOUNDATION PLANS						
S-132	MAT FOUNDATION PLANS						
S-140	BRIDGE FOUNDATION (FIRST FLOOR) PLAN						
S-141	BRIDGE FLOOR (SECOND FLOOR) FRAMING PLAN						
S-142	BRIDGE ROOF (THIRD FLOOR) FRAMING PLAN						
S-143	BRIDGE TRUSS ELEVATIONS						
S-144	BRIDGE SECTIONS & DETAILS						
S-145	BRIDGE SECTIONS & DETAILS						
S-200	PILE CAP DETAILS						
S-201	TYPICAL FOUNDATION DETAILS						
S-202	TYPICAL FOUNDATION DETAILS						
S-203	TYPICAL CONCRETE DETAILS						
S-204	TYPICAL CONCRETE DETAILS						
S-205	FOUNDATION SECTIONS						
S-206	FOUNDATION SECTIONS						
S-207	FOUNDATION SECTIONS						
S-208	FOUNDATION SECTIONS						
S-300	TYPICAL FRAMING DETAILS						
S-301	TYPICAL FRAMING DETAILS						
S-302	TYPICAL FRAMING DETAILS						
S-303	FRAMING SECTIONS						
S-304	FRAMING SECTIONS						
S-305	FRAMING SECTIONS						
S-306	FRAMING SECTIONS						
S-307	FRAMING SECTIONS						
S-308	FRAMING SECTIONS						
S-309	FRAMING SECTIONS						
S-310	FRAMING SECTIONS						
S-311	FRAMING SECTIONS						
S-312	FRAMING SECTIONS						
S-313	FRAMING SECTIONS						
S-314	FRAMING SECTIONS						
S-315	FRAMING SECTIONS						
S-316	FRAMING SECTIONS						
S-400	BRACING ELEVATIONS & DETAILS						
S-401	BRACING ELEVATIONS						
S-500	MEDICAL EQUIPMENT DETAILS						
S-501	MEDICAL EQUIPMENT DETAILS						
S-502	MEDICAL EQUIPMENT FRAMING PLANS						
S-503	MEDICAL EQUIPMENT FRAMING PLANS						
S-600	SITE COMMODITY PARTIAL PLANS						
S-601	ROBERTS EX. SITE RETAINING WALL DETAILS						

INDEX OF DRAWINGS - CORE SHELL		
SHEET NO.	SHEET NAME	CORE AND SHELL CONST. DOCS - 10/15/24 CORE AND SHELL BULLETIN #1 - 1/23/2024 CORE AND SHELL BULLETIN #2 - 1/23/2025 CORE AND SHELL BULLETIN #4 - 1/24/202025 CORE AND SHELL BULLETIN #8 - 1/10/202025 CORE AND SHELL BULLETIN #9 - 1/24/202026
P3.10-CS	MED GAS PLAN - CORE & SHELL - LEVEL 10	
P3.11-CS	MED GAS PLAN - CORE & SHELL - PENTHOUSE	
P3.12-CS	MED GAS PLAN - CORE & SHELL - PENTHOUSE ROOF	
P4.01	PLUMBING DETAILS	
P4.01-CS	PLUMBING DETAILS	
P4.02-CS	PLUMBING DETAILS	
P5.01	DOMESTIC WATER RISER DIAGRAM	
P5.02	DOMESTIC WATER RISER DIAGRAM	
P5.03	DOMESTIC WATER RISER DIAGRAM	
P6.04	MEDICAL GAS RISER DIAGRAM	
P7.01	SANITARY WASTE AND VENT RISER DIAGRAM	
P7.02	SANITARY WASTE AND VENT RISER DIAGRAM	
P7.03	SANITARY WASTE AND VENT RISER DIAGRAM	
P8.01-CS	RAINWATER RISER DIAGRAM	
P1.1	PLUMBING PLAN, NOTES, SPECIFICATIONS, AND DETAILS	
P1.02.K1	FIT OUT FLOOR PLAN - LEVEL 0201 KELEMEN DEMOLITION	
P1.02.K1	LEVEL 02 KELEMEN PLUMBING NOTES, SCHEDULES, AND DETAILS	
P2.02.K1	FIT OUT FLOOR PLAN - LEVEL 0201 KELEMEN DOMESTIC	
P3.02.K2	FIT OUT FLOOR PLAN - LEVEL 0201 KELEMEN SANITARY	
ELECTRICAL	ELECTRICAL SYMBOLS & LEGEND	
E0.00	ELECTRICAL SYMBOLS & LEGEND	
E0.00-CS	ELECTRICAL SYMBOLS & LEGEND	
E0.01	ELECTRICAL SCHEDULES - SCOPE OF WORK ASSIGNMENTS	
E0.01-CS	ELECTRICAL SCHEDULES - SCOPE OF WORK ASSIGNMENTS	
E0.02-CS	ELECTRICAL SCHEDULES - SCOPE OF WORK ASSIGNMENTS	
E1.1	SYMBOLS, ABBREVIATIONS, AND GENERAL NOTES	
E2.00-CS	LEVEL 00 BASEMENT OVERALL - POWER PLAN - CORE & SHELL	
E2.00.1-CS	LEVEL 00 BASEMENT TOWER A - POWER PLAN - CORE & SHELL	
E2.00.2-CS	LEVEL 00 BASEMENT TOWER A EXTENSION - POWER PLAN - CORE & SHELL	
E2.01	POWER PLAN - LEVEL 02	
E2.01.0	POWER PLAN - LEVEL 1 OVERALL	
E2.01.0-CS	POWER PLAN - LEVEL 1 OVERALL	
E2.01.1	POWER PLAN - LEVEL 1	
E2.01.1-CS	POWER PLAN - LEVEL 1	
E2.01.2	POWER PLAN - LEVEL 1 EXTENSION	
E2.01.2-CS	POWER PLAN - LEVEL 1 EXTENSION	
E2.02	POWER PLAN - LEVEL 2 OVERALL	
E2.02.1	POWER PLAN - LEVEL 2	
E2.02.2	POWER PLAN - LEVEL 2 EXTENSION	
E2.03	POWER PLAN - LEVEL 03	
E2.03-CS	POWER PLAN - LEVEL 03	
E2.04	POWER PLAN - LEVEL 04	
E2.04-CS	POWER PLAN - LEVEL 04	
E2.05	POWER PLAN - LEVEL 05	
E2.05-CS	POWER PLAN - LEVEL 05	
E2.06	POWER PLAN - LEVEL 06	
E2.06-CS	POWER PLAN - LEVEL 06	
E2.07	POWER PLAN - LEVEL 07	
E2.07-CS	POWER PLAN - LEVEL 07	
E2.08	POWER PLAN - LEVEL 08	
E2.08-CS	POWER PLAN - LEVEL 08	
E2.09	POWER PLAN - LEVEL 09	
E2.09-CS	POWER PLAN - LEVEL 09	
E2.10	POWER PLAN - LEVEL 10	
E2.10-CS	POWER PLAN - LEVEL 10	
E2.11	POWER PLAN - LEVEL 11	
E2.11-CS	POWER PLAN - LEVEL 11	
E2.12	POWER PLAN - LEVEL 12	
E2.12-CS	POWER PLAN - LEVEL 12	
E2.13	POWER PLAN - LEVEL 13	
E2.13-CS	POWER PLAN - LEVEL 13	
E2.14	POWER PLAN - LEVEL 14	
E2.14-CS	POWER PLAN - LEVEL 14	
E2.15	POWER PLAN - LEVEL 15	
E2.15-CS	POWER PLAN - LEVEL 15	
E2.16	POWER PLAN - LEVEL 16	
E2.16-CS	POWER PLAN - LEVEL 16	
E2.17	POWER PLAN - LEVEL 17	
E2.17-CS	POWER PLAN - LEVEL 17	
E2.18	POWER PLAN - LEVEL 18	
E2.18-CS	POWER PLAN - LEVEL 18	
E2.19	POWER PLAN - LEVEL 19	
E2.19-CS	POWER PLAN - LEVEL 19	
E2.20	POWER PLAN - LEVEL 20	
E2.20-CS	POWER PLAN - LEVEL 20	
E2.21	POWER PLAN - LEVEL 21	
E2.21-CS	POWER PLAN - LEVEL 21	
E2.22	POWER PLAN - LEVEL 22	
E2.22-CS	POWER PLAN - LEVEL 22	
E2.23	POWER PLAN - LEVEL 23	
E2.23-CS	POWER PLAN - LEVEL 23	
E2.24	POWER PLAN - LEVEL 24	
E2.24-CS	POWER PLAN - LEVEL 24	
E2.25	POWER PLAN - LEVEL 25	
E2.25-CS	POWER PLAN - LEVEL 25	
E2.26	POWER PLAN - LEVEL 26	
E2.26-CS	POWER PLAN - LEVEL 26	
E2.27	POWER PLAN - LEVEL 27	
E2.27-CS	POWER PLAN - LEVEL 27	
E2.28	POWER PLAN - LEVEL 28	
E2.28-CS	POWER PLAN - LEVEL 28	
E2.29	POWER PLAN - LEVEL 29	
E2.29-CS	POWER PLAN - LEVEL 29	
E2.30	POWER PLAN - LEVEL 30	
E2.30-CS	POWER PLAN - LEVEL 30	
E2.31	POWER PLAN - LEVEL 31	
E2.31-CS	POWER PLAN - LEVEL 31	
E2.32	POWER PLAN - LEVEL 32	
E2.32-CS	POWER PLAN - LEVEL 32	
E2.33	POWER PLAN - LEVEL 33	
E2.33-CS	POWER PLAN - LEVEL 33	
E2.34	POWER PLAN - LEVEL 34	
E2.34-CS	POWER PLAN - LEVEL 34	
E2.35	POWER PLAN - LEVEL 35	
E2.35-CS	POWER PLAN - LEVEL 35	
E2.36	POWER PLAN - LEVEL 36	
E2.36-CS	POWER PLAN - LEVEL 36	
E2.37	POWER PLAN - LEVEL 37	
E2.37-CS	POWER PLAN - LEVEL 37	
E2.38	POWER PLAN - LEVEL 38	
E2.38-CS	POWER PLAN - LEVEL 38	
E2.39	POWER PLAN - LEVEL 39	
E2.39-CS	POWER PLAN - LEVEL 39	
E2.40	POWER PLAN - LEVEL 40	
E2.40-CS	POWER PLAN - LEVEL 40	
E2.41	POWER PLAN - LEVEL 41	
E2.41-CS	POWER PLAN - LEVEL 41	
E2.42	POWER PLAN - LEVEL 42	
E2.42-CS	POWER PLAN - LEVEL 42	
E2.43	POWER PLAN - LEVEL 43	
E2.43-CS	POWER PLAN - LEVEL 43	
E2.44	POWER PLAN - LEVEL 44	
E2.44-CS	POWER PLAN - LEVEL 44	
E2.45	POWER PLAN - LEVEL 45	
E2.45-CS	POWER PLAN - LEVEL 45	
E2.46	POWER PLAN - LEVEL 46	
E2.46-CS	POWER PLAN - LEVEL 46	
E2.47	POWER PLAN - LEVEL 47	
E2.47-CS	POWER PLAN - LEVEL 47	
E2.48	POWER PLAN - LEVEL 48	
E2.48-CS	POWER PLAN - LEVEL 48	
E2.49	POWER PLAN - LEVEL 49	
E2.49-CS	POWER PLAN - LEVEL 49	
E2.50	POWER PLAN - LEVEL 50	
E2.50-CS	POWER PLAN - LEVEL 50	
E2.51	POWER PLAN - LEVEL 51	
E2.51-CS	POWER PLAN - LEVEL 51	
E2.52	POWER PLAN - LEVEL 52	
E2.52-CS	POWER PLAN - LEVEL 52	
E2.53	POWER PLAN - LEVEL 53	
E2.53-CS	POWER PLAN - LEVEL 53	
E2.54	POWER PLAN - LEVEL 54	
E2.54-CS	POWER PLAN - LEVEL 54	
E2.55	POWER PLAN - LEVEL 55	
E2.55-CS	POWER PLAN - LEVEL 55	
E2.56	POWER PLAN - LEVEL 56	
E2.56-CS	POWER PLAN - LEVEL 56	
E2.57	POWER PLAN - LEVEL 57	
E2.57-CS	POWER PLAN - LEVEL 57	
E2.58	POWER PLAN - LEVEL 58	
E2.58-CS	POWER PLAN - LEVEL 58	
E2.59	POWER PLAN - LEVEL 59	
E2.59-CS	POWER PLAN - LEVEL 59	
E2.60	POWER PLAN - LEVEL 60	
E2.60-CS	POWER PLAN - LEVEL 60	
E2.61	POWER PLAN - LEVEL 61	
E2.61-CS	POWER PLAN - LEVEL 61	
E2.62	POWER PLAN - LEVEL 62	
E2.62-CS	POWER PLAN - LEVEL 62	
E2.63	POWER PLAN - LEVEL 63	
E2.63-CS	POWER PLAN - LEVEL 63	
E2.64	POWER PLAN - LEVEL 64	
E2.64-CS	POWER PLAN - LEVEL 64	
E2.65	POWER PLAN - LEVEL 65	
E2.65-CS	POWER PLAN - LEVEL 65	
E2.66	POWER PLAN - LEVEL 66	
E2.66-CS	POWER PLAN - LEVEL 66	
E2.67	POWER PLAN - LEVEL 67	
E2.67-CS	POWER PLAN - LEVEL 67	
E2.68	POWER PLAN - LEVEL 68	
E2.68-CS	POWER PLAN - LEVEL 68	
E2.69	POWER PLAN - LEVEL 69	
E2.69-CS	POWER PLAN - LEVEL 69	
E2.70	POWER PLAN - LEVEL 70	
E2.70-CS	POWER PLAN - LEVEL 70	
E2.71	POWER PLAN - LEVEL 71	
E2.71-CS	POWER PLAN - LEVEL 71	
E2.72	POWER PLAN - LEVEL 72	
E2.72-CS	POWER PLAN - LEVEL 72	
E2.73	POWER PLAN - LEVEL 73	
E2.73-CS	POWER PLAN - LEVEL 73	


INDEX OF DRAWINGS - CORE SHELL		
SHEET NO.	SHEET NAME	CORE AND SHELL CONST. DOCS - 10/15/24 CORE AND SHELL BULLETIN #1 - 1/23/2024 CORE AND SHELL BULLETIN #2 - 01/23/2025 CORE AND SHELL BULLETIN #4 - 04/26/2025 CORE AND SHELL BULLETIN #8 - 01/30/2026 CORE AND SHELL BULLETIN #9 - 03/26/2026
E3.75	LIGHTING COMCHECK	
E3.76	LIGHTING COMCHECK	
E3.77	LIGHTING COMCHECK	
E3.78	LIGHTING COMCHECK	
E3.79	LIGHTING FIXTURE SCHEDULE - LEVEL 2 ONLY	
E4.00-CS	LEVEL 0 BASEMENT - CONDUIT PLAN - CORE & SHELL	
E4.1	ONE LINE DIAGRAM	
E4.2	PANELBOARD SCHEDULES	
E4.11-CS	LEVEL ROOF - CONDUIT PLAN - CORE & SHELL	
E5.1	DETAILS	
E5.01	ELECTRICAL PANEL SCHEDULES - LVL B NORMAL	
E5.01-CS	ELECTRICAL PANEL SCHEDULES - LVL B NORMAL - CORE & SHELL	
E5.02	ELECTRICAL PANEL SCHEDULES - LVL B EMERGENCY	
E5.02-CS	ELECTRICAL PANEL SCHEDULES - LVL B EMERGENCY - CORE & SHELL	
E5.03	ELECTRICAL PANEL SCHEDULES - LVL 1 NORMAL	
E5.03-CS	ELECTRICAL PANEL SCHEDULES - LVL 1 NORMAL - CORE & SHELL	
E5.04	ELECTRICAL PANEL SCHEDULES - LVL 1 EMERGENCY	
E5.04-CS	ELECTRICAL PANEL SCHEDULES - LVL 1 EMERGENCY - CORE & SHELL	
E5.05	ELECTRICAL PANEL SCHEDULES - LVL 23 NORMAL	
E5.05-CS	ELECTRICAL PANEL SCHEDULES - LVL 23 NORMAL - CORE & SHELL	
E5.06	ELECTRICAL PANEL SCHEDULES - LVL 2 EMERGENCY	
E5.06-CS	ELECTRICAL PANEL SCHEDULES - LVL 2 EMERGENCY - CORE & SHELL	
E5.07	ELECTRICAL PANEL SCHEDULES - LVL 45 NORMAL/EM - CORE & SHELL	
E5.07-CS	ELECTRICAL PANEL SCHEDULES - LVL 45 NORMAL/EM - CORE & SHELL	
E5.08	ELECTRICAL PANEL SCHEDULES - LVL 45 EMERGENCY	
E5.08-CS	ELECTRICAL PANEL SCHEDULES - LVL 45 EMERGENCY - CORE & SHELL	
E5.09	ELECTRICAL PANEL SCHEDULES - LVL 4 EMERGENCY	
E5.09-CS	ELECTRICAL PANEL SCHEDULES - LVL 4 EMERGENCY - CORE & SHELL	
E5.10	ELECTRICAL PANEL SCHEDULES - LVL 5 EMERGENCY	
E5.10-CS	ELECTRICAL PANEL SCHEDULES - LVL 5 EMERGENCY - CORE & SHELL	
E5.11	ELECTRICAL PANEL SCHEDULES - LVL 89 EMERGENCY - CORE & SHELL	
E5.11-CS	ELECTRICAL PANEL SCHEDULES - LVL 89 NORMAL - CORE & SHELL	
E5.12	ELECTRICAL PANEL SCHEDULES - LVL 6 EMERGENCY	
E5.12-CS	ELECTRICAL PANEL SCHEDULES - LVL 6 EMERGENCY - CORE & SHELL	
E5.13	ELECTRICAL PANEL SCHEDULES - LVL 7 EMERGENCY	
E5.13-CS	ELECTRICAL PANEL SCHEDULES - LVL 10PH NORMAL - CORE & SHELL	
E5.14	ELECTRICAL PANEL SCHEDULES - LVL 10PH EM - CORE & SHELL	
E5.14-CS	ELECTRICAL PANEL SCHEDULES - LVL 10PH EM - CORE & SHELL	
E5.15	ELECTRICAL PANEL SCHEDULES - LVL 8 EMERGENCY	
E5.15-CS	ELECTRICAL PANEL SCHEDULES - LVL 2 EMERGENCY	
E5.16	ELECTRICAL PANEL SCHEDULES - LVL 10PH NORMAL	
E5.17	ELECTRICAL PANEL SCHEDULES - LVL 10PH NORMAL	
E5.18	ELECTRICAL PANEL SCHEDULES - LVL 10PH EMERGENCY	
E5.18-CS	ELECTRICAL PANEL SCHEDULES - LVL 3 ISOLATED PANELS	
E5.19	ELECTRICAL PANEL SCHEDULES - LVL 2 ISOLATED PANELS	
E5.20	ELECTRICAL PANEL SCHEDULES - LVL 2 ISOLATED PANELS	
E5.21	ELECTRICAL NORMAL POWER RISER DIAGRAM	
E5.21-CS	NORMAL POWER ONE LINE DIAGRAM	
E6.02	ELECTRICAL ESSENTIAL POWER RISER DIAGRAM	
E6.02-CS	EMERGENCY POWER ONE LINE DIAGRAM	
E6.02-CS	ELECTRICAL NORMAL POWER RISER DIAGRAM	
E6.04-CS	ELECTRICAL ESSENTIAL POWER RISER DIAGRAM	
E7.01	ELECTRICAL DETAILS 1	
E7.01-CS	ELECTRICAL DETAILS 1	
E7.02-CS	ELECTRICAL DETAILS 2 LIGHTNING PROTECTION	
E7.03-CS	ELECTRICAL DETAILS 3	
E7.04-CS	ELECTRICAL DETAILS 4	
E7.05-CS	ELECTRICAL DETAILS 5	
E9.01	ELECTRICAL CLOSETS ENLARGED PLANS BASEMENT	
E9.01-CS	ENLARGED ELECTRICAL ROOMS - MAIN NORMAL & EMERGENCY	
E9.02	NORMAL ELECTRICAL CLOSETS ENLARGED PLANS	
E9.02-CS	ENLARGED ELECTRICAL ROOMS	
E9.03	EMERGENCY ELECTRICAL CLOSETS ENLARGED PLANS	
E9.03-CS	ENLARGED ELECTRICAL ROOMS	
E9.04	ELECTRICAL TDR ENLARGED PLANS	
E9.04-CS	ENLARGED ELECTRICAL ROOMS	
E9.05	ELECTRICAL LOCKERS ENLARGED PLANS	
E9.05-CS	ENLARGED ELECTRICAL ROOMS	
E9.06	ELECTRICAL NORMAL, EMERGENCY AND TDR ROOMS ENLARGED PLANS - 2ND FL.	
E9.07	ELECTRICAL HYBRID OR EQUIPMENT ENLARGED PLAN	
E9.08	ELECTRICAL HYBRID ROOMS ENLARGED PLANS	
E9.09	ELECTRICAL HYBRID OR ENLARGED POWER PLANS	
E9.10	ELECTRICAL OR ROOM ENLARGED POWER PLANS	
E9.11	ELECTRICAL DEMOLITION PLAN - LEVEL 02	
E9.11	FIRE ALARM PLAN - LEVEL 02	
E9.11	COMMUNICATIONS PLAN - LEVEL 02	
ELECTRICAL - KELEMEN		
EED1.02-K1	ELECTRICAL DEMOLITION PLAN - LEVEL 02 KELEMEN	
EED2.02-K1	POWER PLAN - LEVEL 02 KELEMEN	
EED3.02-K1	LIGHTING RCP - LEVEL 02 KELEMEN	
EED4.02-K1	ELECTRICAL PANELBOARD SCHEDULES - KELEMEN LVL 2	
FIRE ALARM		
FAD.00	FIRE ALARM LEGEND	
FAD.00-CS	FIRE ALARM LEGEND CORE & SHELL	
FAD.02-CS	FIRE FEIGHTERS SMOKE CONTROL PANEL	
FAD.01	FIRE ALARM PLAN - LEVEL 0 - BASEMENT	
FAD.01.00-CS	BASMT - FIRE ALARM PLAN - CORE & SHELL	
FAD.01.01-CS	BASMT - FIRE ALARM PLAN - CORE & SHELL	
FAD.01.02-CS	BASMT - FIRE ALARM PLAN - TOWER A - EXPANSION - CORE & SHELL	
FAD.01.01	FIRE ALARM PLAN - LEVEL 01 OVERALL	
FAD.01.01-CS	LEVEL 01 - FIRE ALARM PLAN - TOWER A - CORE & SHELL	
FAD.01.01.01	FIRE ALARM PLAN - LEVEL 01 TOWER A	
FAD.01.01.1-CS	LEVEL 01 - FIRE ALARM PLAN - TOWER A - CORE & SHELL	
FAD.01.01.1	FIRE ALARM PLAN - LEVEL 01 TOWER A EXTENSION	
FAD.01.01.2-CS	FIRE ALARM PLAN - LEVEL 1 - Tower A - Extension - CORE & SHELL	
FAD.01.02-CS	LEVEL 02 - FIRE ALARM PLAN - CORE & SHELL	
FAD.01.02.1	FIRE ALARM PLAN - LEVEL 02 TOWER A EXTENSION	
FAD.01.02.1	FIRE ALARM PLAN - LEVEL 02 TOWER A	
FAD.01.02.1	FIRE ALARM PLAN - LEVEL 02 TOWER A	
FAD.01.02.1		

MODEL: A:\models\Draw\25695.000_Cooper_Miller_Campus_Plan_2023.dwg, CHIT: TowerA, Extndr: 2023.rvt, PRINT DATE: 3/27/2026 5:32:59 PM, TEMPLATE VERSION: 23.3.3, TITLE BLOCK VERSION: 20210630

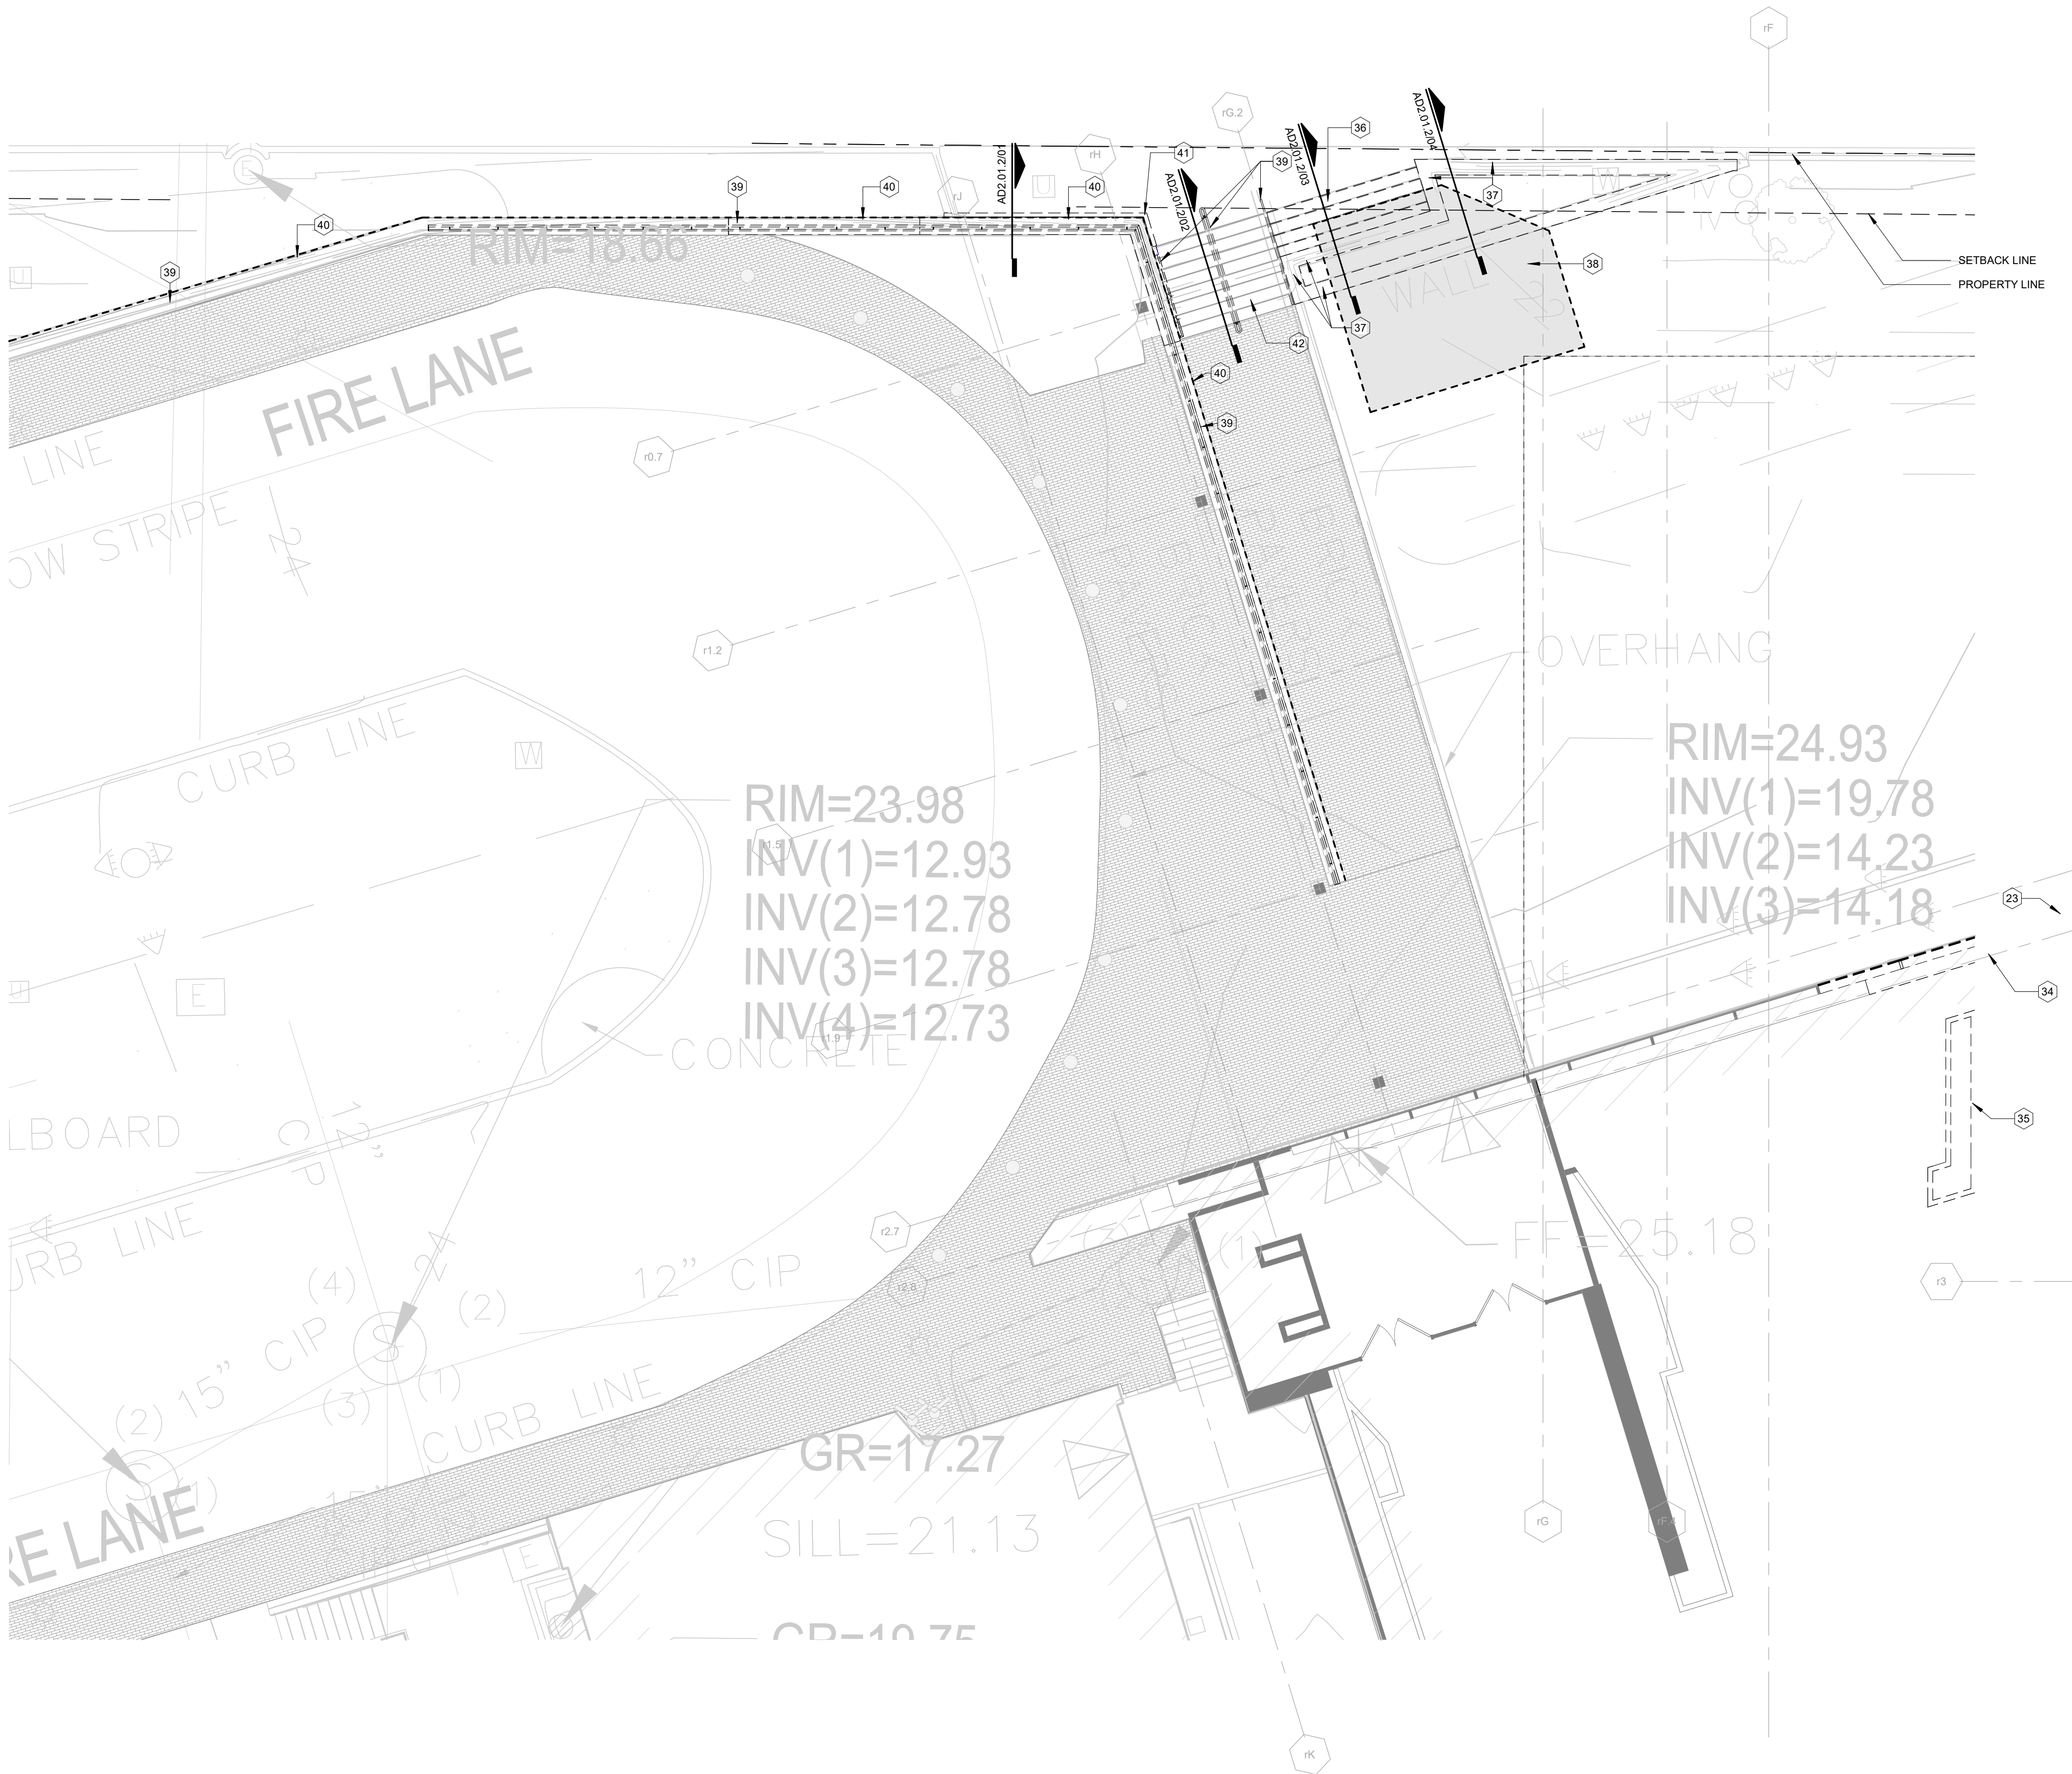


05 DEMOLITION PLAN - LEVEL 01

1/8" = 1'-0"

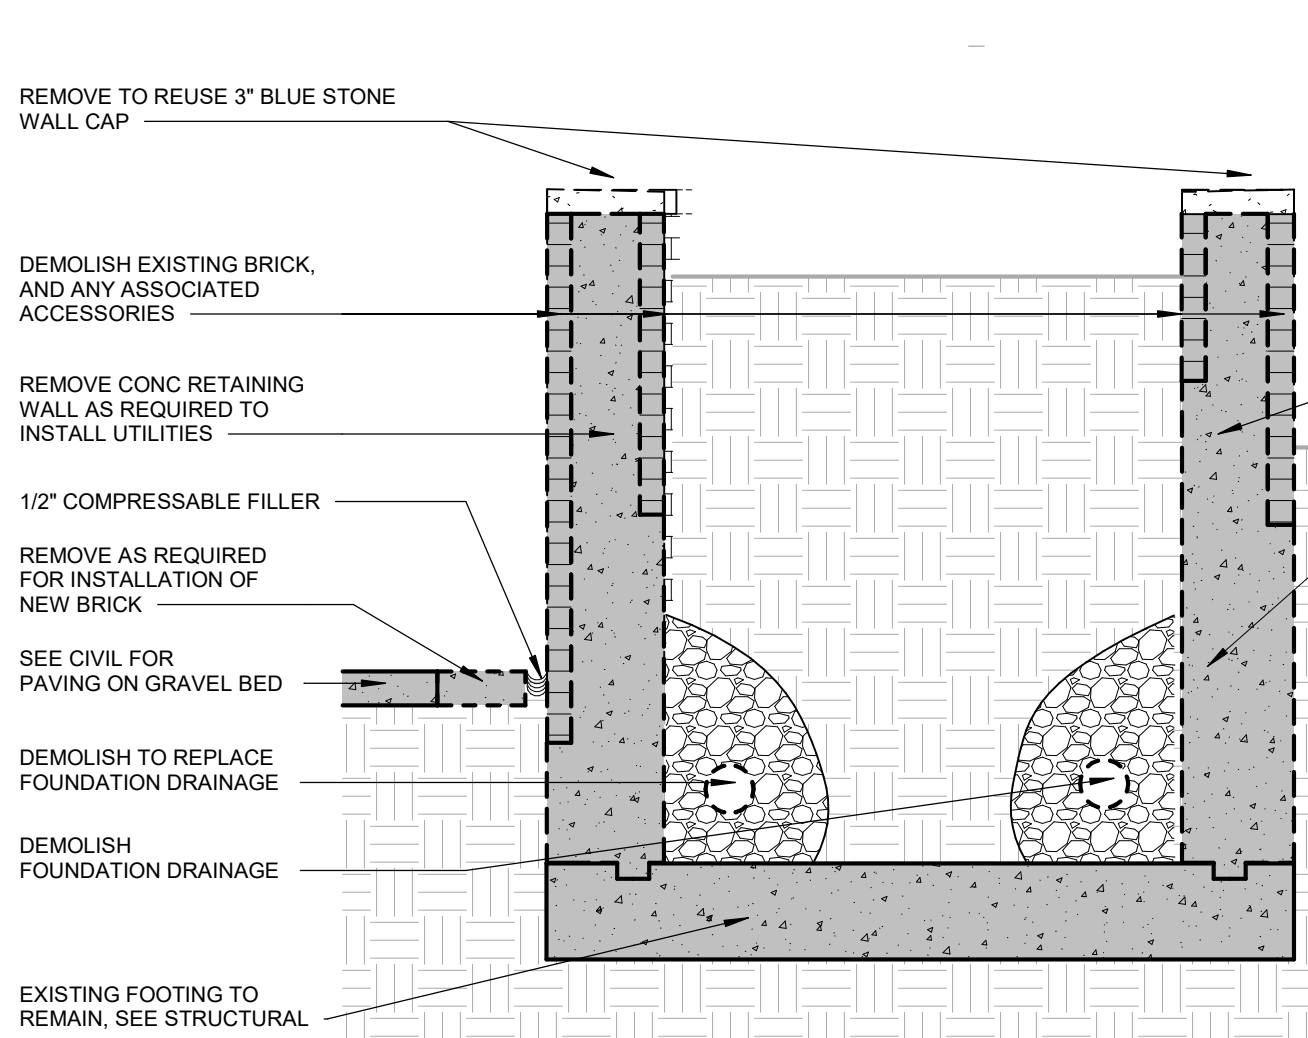


04 RETAINING WALL SECTION

1/2" = 1'-0"

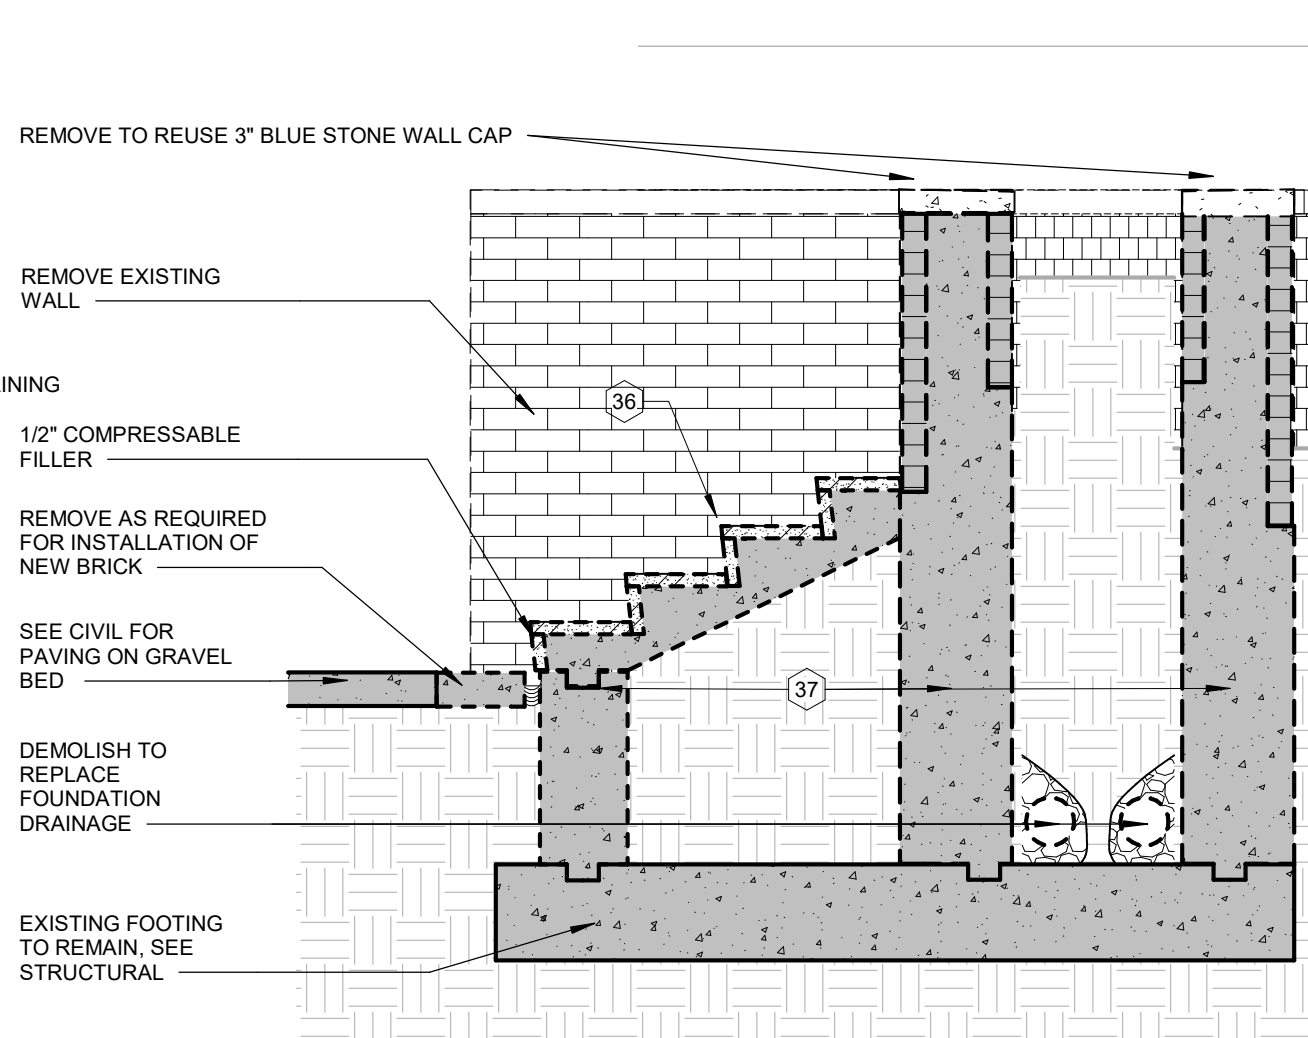


03 DECORATIVE STEPS SECTION

1/2" = 1'-0"

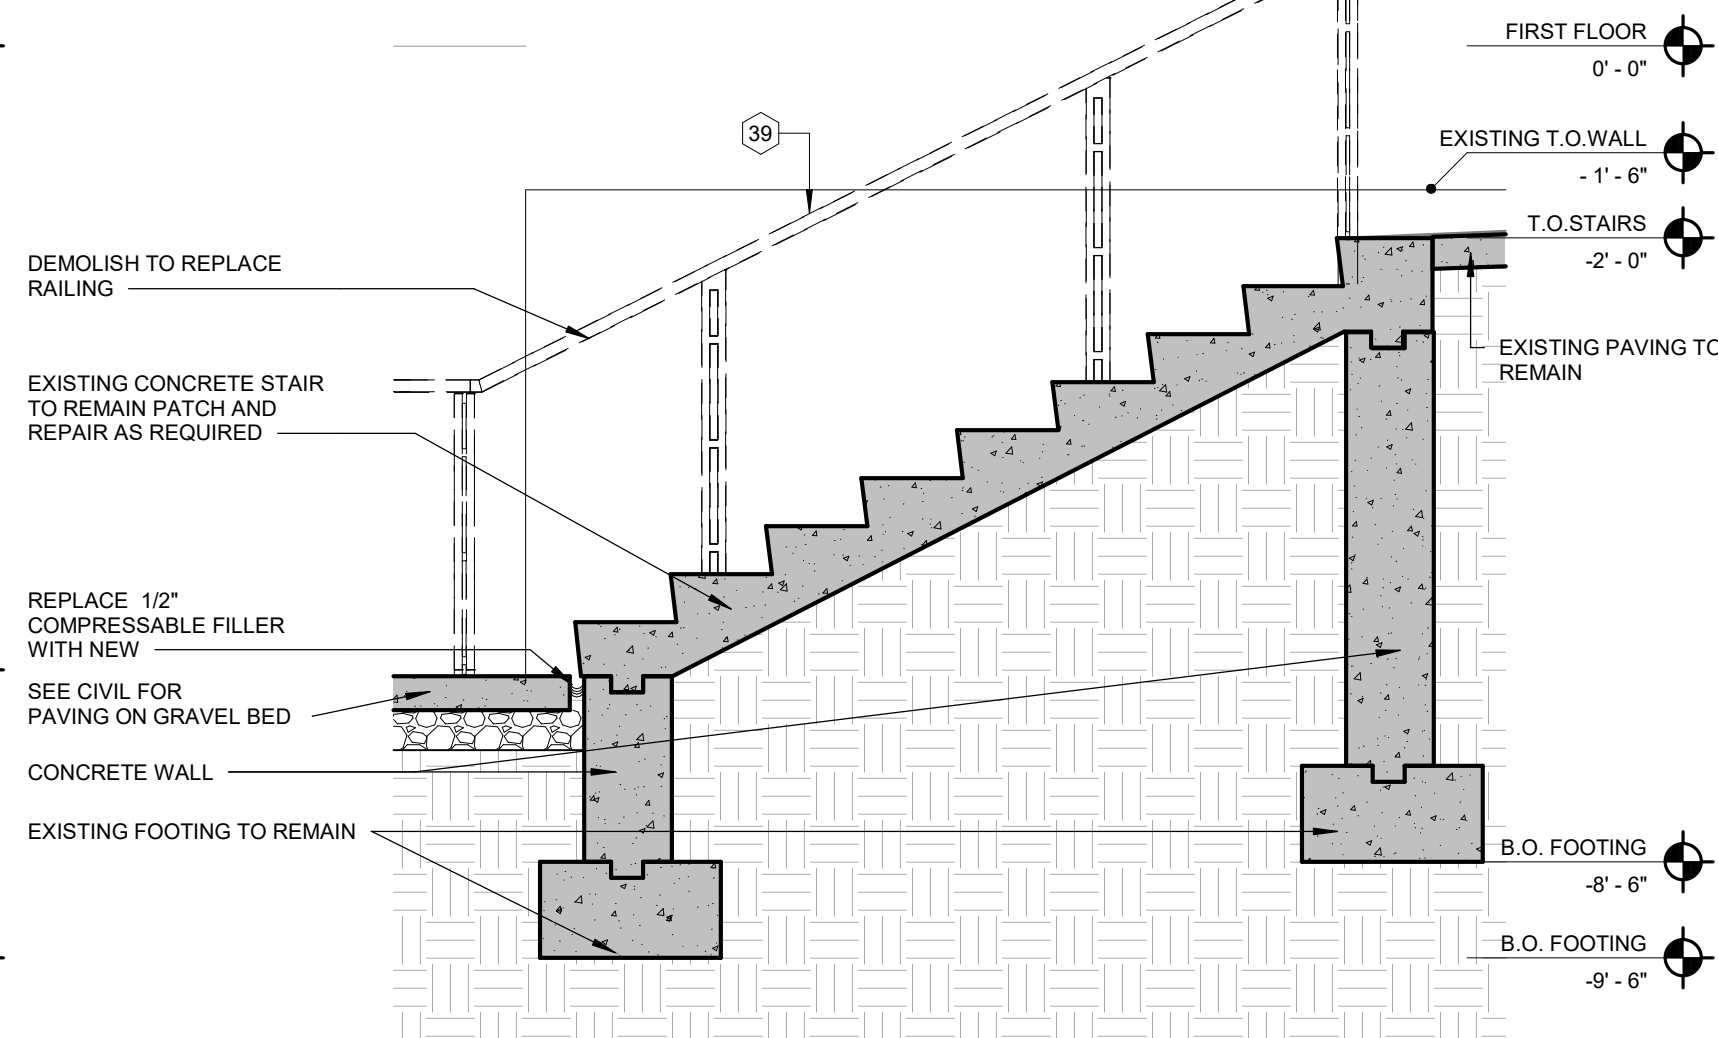

02 STAIR SECTION

1/2" = 1'-0"

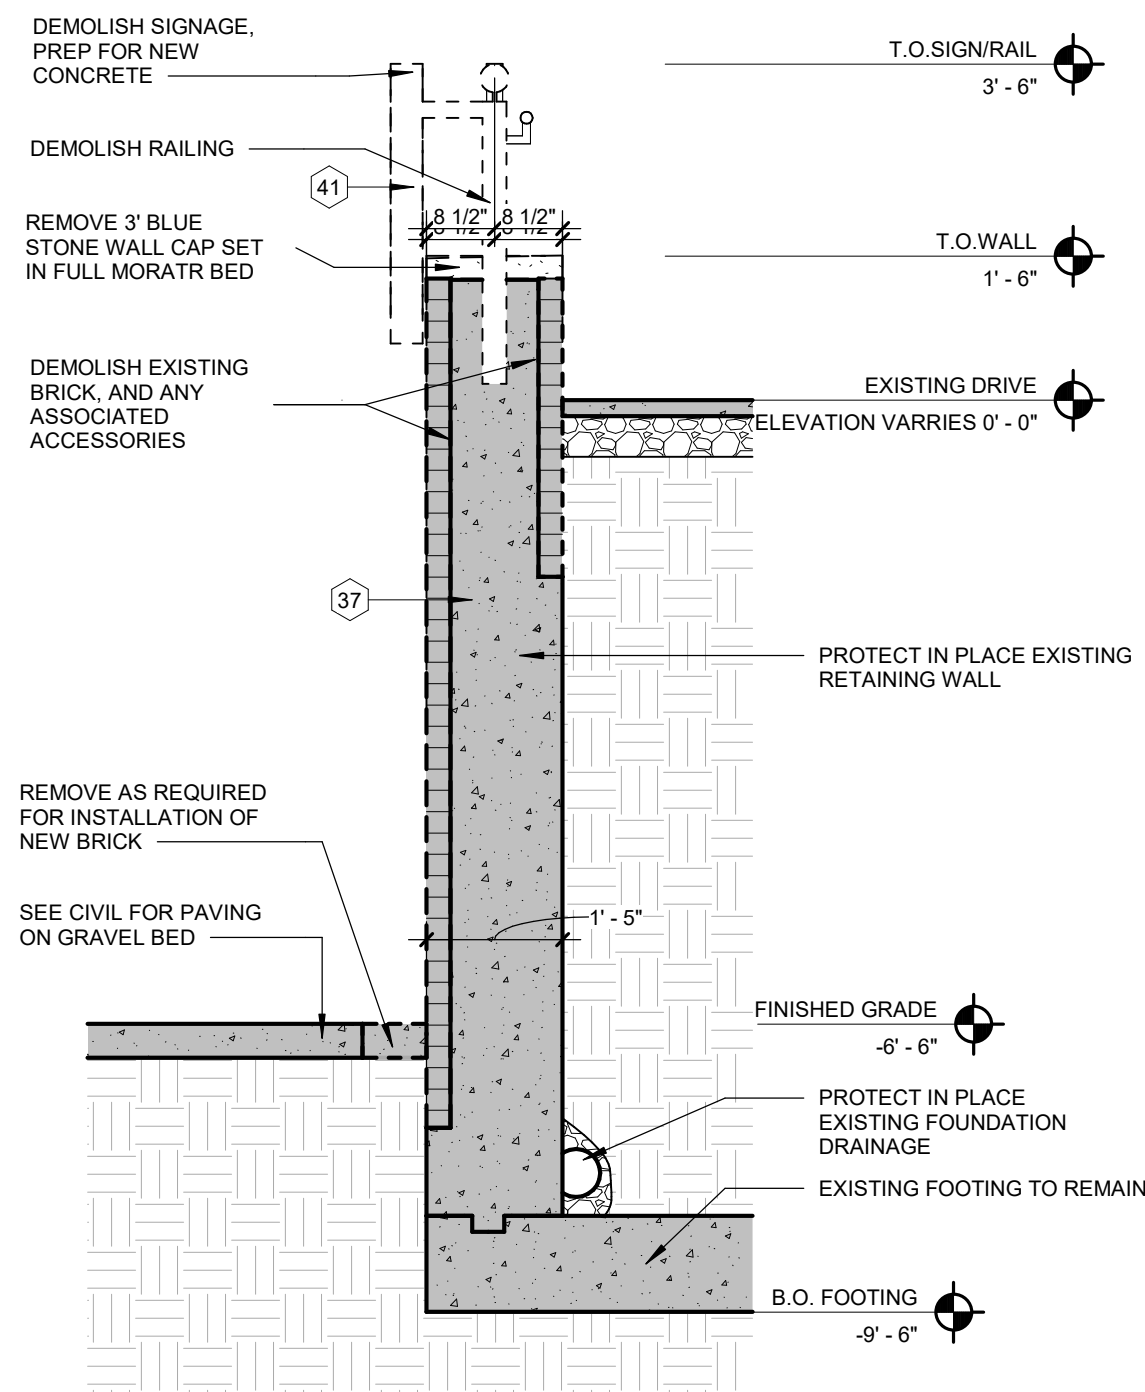

01 RETAINING WALL SECTION

1/2" = 1'-0"

GENERAL NOTES - DEMOLITION

- REFER TO SPECIFICATION SECTION 02.4110 - SELECTIVE DEMOLITION FOR SPECIFIC PROJECT REQUIREMENTS.
- REFER TO DEMOLITION SYMBOL LEGEND ON DRAWINGS.
- CONTRACTOR TO COORDINATE DEMOLITION WORK SEQUENCE.
- REFERENCE PHASING DRAWINGS WHERE APPLICABLE.
- DEMOLITION DRAWINGS REPRESENT EXISTING CONDITIONS BASED ON LIMITED EXISTING DRAWINGS AND SITE OBSERVATIONS. CONTRACTOR SHALL FIELD VERIFY ALL EXISTING BUILDING AND SITE CONDITIONS.
- DEMOLITION DRAWINGS GENERALLY INDICATE EXISTING SCOPE OF WORK TO BE DEMOLISHED AND ARE NOT INTENDED TO LIMIT OR FULLY DEFINE THE SCOPE OF WORK TO BE REMOVED IN ORDER TO ACCOMPLISH SCOPE OF NEW CONSTRUCTION. WHERE THESE CONDITIONS OCCUR OUTSIDE OF THE DEMOLITION LIMITS, AREAS SHALL BE RETURNED TO THEIR ORIGINAL CONDITION AS PART OF THE NEW CONSTRUCTION SCOPE OF WORK.
- CONTRACTOR SHALL NOTIFY ARCHITECT OF ANY CONFLICTS BETWEEN EXISTING CONSTRUCTION AND CONSTRUCTION DOCUMENTS.
- REFERENCE STRUCTURAL, CIVIL, AND MEP DRAWINGS FOR OTHER DISCIPLINE DEMOLITION SCOPE OF WORK.
- WHERE EXISTING WALL MOUNTED DEVICES, FIXTURES OR OTHER WALL MOUNTED ITEMS ARE SCHEDULED TO BE SALVAGED, REFERENCE CONSTRUCTION DRAWINGS FOR NEW LOCATIONS OR COORDINATE WITH OWNER FOR STORAGE LOCATION.
- PARTITIONS SCHEDULED TO BE REMOVED, DEMOLITION SHOULD INCLUDE MISCELLANEOUS BRACINGS, TRACK, ETC. TO BOTTOM OF STRUCTURE.
- CONTRACTOR SHALL MAINTAIN ALL REQUIRED EXITS UNOBSERVED, ILLUMINATED AND PROTECTED FROM CONSTRUCTION ACTIVITIES. CONTRACTOR TO CLEAN AREAS ADJACENT TO DEMOLITION AREA OF DUST, DIRT AND DEBRIS CAUSED BY DEMOLITION OPERATIONS.
- PROMPTLY DISPOSE OF DEMOLISHED MATERIALS. DO NOT ALLOW DEMOLISHED MATERIALS TO ACCUMULATE ON SITE. TRANSPORT DEMOLISHED MATERIALS AND LEGALLY DISPOSE OF THEM.
- KEEP BUILDING ENCLOSURE WATER TIGHT AT ALL TIMES THROUGHOUT DEMOLITION AND CONSTRUCTION PHASES.


DEMOLITION SYMBOLS

- ITEMS SHOWN DASHED ARE TO BE REMOVED.
- ITEMS SHOWN SCREENED ARE TO REMAIN.
- ITEMS SHOWN SOLID ARE NEW CONSTRUCTION.
- DEMOLITION KEYNOTE

DEMOLITION KEYNOTES

- REMOVE METAL PANEL CLADDING, CURTAIN WALL AND ASSOCIATED SUPPORT FRAMING
- REMOVE SIDEWALK IN ITS ENTIRETY. SEE CIVIL DRAWINGS, TYP.
- REMOVE STAIRS IN ITS ENTIRETY
- REMOVE METAL PANEL, CATWALK, AND SUPPORTING STRUCTURE IN ITS ENTIRETY
- REMOVE GRADE BEAM SUPPORTING KELEMEN FACADE. SEE STRUCTURAL DRAWINGS, TYP.
- REMOVE METAL PANEL SYSTEM, CURTAINWALL SYSTEM AND BACKUP WALL IN ITS ENTIRETY. REMOVE AIR/WATER BARRIER SYSTEMS IN THEIR ENTIRETY
- REMOVE SECTION OF RETAINING WALL AS SHOWN
- REMOVE EXISTING AREAWAY PARTITIONS. SEE STRUCTURAL, TYP.
- REMOVE CLEERSTORY WINDOWS AND INFILL OPENING
- REMOVE WALLS IN THEIR ENTIRETY AS SHOWN
- REMOVE WATER PROOFING AND ASSOCIATED SYSTEMS ON EXISTING BASEMENT WALL
- REMOVE LOUVERS IN ITS ENTIRETY AND INFILL OPENING PROVIDE AIR AND WATERPROOFING CONTINUITY
- REMOVE METAL GRATING ABOVE AREAWAY IN ITS ENTIRETY
- REMOVE STEEL FRAMING AND DECK IN ITS ENTIRETY
- REMOVE LANDSCAPE AND PLAZA SYSTEM
- REMOVE EXISTING DOOR AND FRAME AND INFILL OPENING
- REMOVE PLASTER SYSTEM OVER EXISTING BACK UP WALL
- REMOVE EXISTING DOOR IN ITS ENTIRETY
- REMOVE CURTAIN WALL SYSTEM IN ITS ENTIRETY
- REMOVE STAIR IN ITS ENTIRETY FROM LEVEL 02 UP
- REMOVE METAL PANEL SYSTEM, BACK UP WALL TO REMAIN
- REMOVE CONCRETE CURB TO ALLOW CORRIDOR CONNECTION
- REMOVE EXISTING FACADE/METAL PANEL, CURTAINWALL, AND BACKUP WALL IN ITS ENTIRETY. PROTECT AIR/WATER BARRIER SYSTEM AND PROVIDE NEW WATERPROOFING AS PART OF DEMOLITION. REFER TO STRUCTURAL DRAWINGS. EXISTING ROBERTS SLAB TO REMAIN. PROVIDE PROTECTION PARTITION INSTALLED FROM EXTERIOR SIDE TO PROVIDE CLOSURE OF THIS LEVEL. LEVEL 1 EXISTING FACADE TO REMAIN IN PLACE UNTIL TOWER A LEVEL 1 IS WEATHER TIGHT
- REMOVE CANTILEVERED FACADE (METAL PANEL, CURTAINWALL, AND BACKUP WALL) IN ITS ENTIRETY. PROTECT AIR/WATER BARRIER SYSTEM AND PROVIDE NEW WATERPROOFING AS PART OF DEMOLITION. REFER TO STRUCTURAL DRAWINGS. EXISTING ROBERTS SLAB TO REMAIN. PROVIDE PROTECTION PARTITION INSTALLED FROM EXTERIOR SIDE TO PROVIDE CLOSURE OF THIS LEVEL.
- REMOVE METAL BASE FOR NEW PORTAL OPENING
- REMOVE STEEL CURTAINWALL SUPPORT FRAMING POST FOR NEW PORTAL OPENING
- REMOVE PLANTER
- DEMOLISH DECORATIVE STEPS
- DEMOLISH WALL AS REQUIRED TO INSTALL UTILITIES. MAINTAIN AND PROTECT EXISTING FOUNDATION. PROVIDE TEMPORARY SHORING AND SOIL STABILIZATION AS REQUIRED. REFER TO STRUCTURAL AND CIVIL FOR THE EXTENT OF DEMOLITION. REMOVE AND REPLACE EXISTING WALL CAP IN NEW CONSTRUCTION.
- PREPARE AREA FOR NEW UTILITY INSTALLATION, INCLUDING SELECTIVE DEMOLITION AND EXCAVATION. PROTECT EXISTING FOUNDATION AND SITE FEATURES. PROVIDE SHORING AS REQUIRED. BACKFILL AND COMPACT AFTER INSTALLATION.
- REMOVE RAILINGS GUARD RAIL IN ITS ENTIRETY. EXISTING CONCEALED BASE PLATES MAY BE REUSED IF VERIFIED TO BE IN GOOD CONDITION
- REMOVE EXISTING BRICK AND STEP LIGHTS ON BOTH SIDES OF WALL. INSTALL NEW BRICK VENEER PER SPECIFICATIONS, INCLUDING NEW WATERPROOFING, DRAINAGE CAVITY DRAINAGE MAT, WEEP HOLES, AND VENTS. REMOVE AND REPLACE EXISTING WALL CAP IN NEW CONSTRUCTION.
- REMOVE EXISTING METAL SIGNAGE PANEL AND ASSOCIATED MOUNTING BRACKETS IN THEIR ENTIRETY. REMOVE ALL FASTENERS AND ANCHORS.
- CLEAN AND PATCH STAMPED CONCRETE AT STAIRS AS NECESSARY.
- NOT IN SCOPE. RENOVATION TO BE ISSUED AS PART OF FUTURE FIT OUT SUBMISSION.

RESERVE FOR DCA STAMP

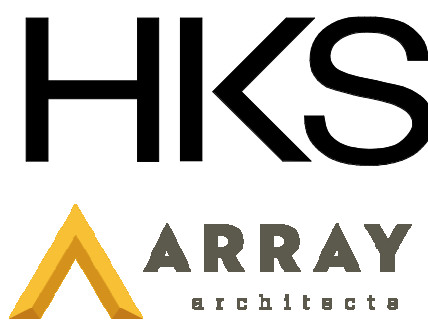


ARCHITECT
HKS, P.C.
1250 (EYE) STREET NW, SUITE 600
WASHINGTON, DC 20005
ASSOCIATE ARCHITECT / INTERIOR DESIGNER
ARRAY
1 WEST ELM STREET, SUITE 500
CONSHOHOCKEN, PA 19428
STRUCTURAL ENGINEER
O'DONNELL & NACCARATO
701 MARKET ST., #6000
PHILADELPHIA, PA 19106
MEP-FP / LOW VOLTAGE ENGINEER
BR+A CONSULTING ENGINEERS
2401 WALNUT ST SUITE 701
PHILADELPHIA, PA 19103
HIGHLAND ASSOCIATES
102 HIGHLAND AVE
CLARKS SUMMIT, PA 18411



OWNER
COOPER UNIVERSITY HEALTHCARE
1 COOPER PLAZA
CAMDEN, NJ 08103
PROJECT MANAGER
PURE PM
2026 RICHMOND STREET
PHILADELPHIA, PA 19134
CIVIL ENGINEER / LANDSCAPE
LANGAN
1818 MARKET STREET, SUITE 3300
PHILADELPHIA, PA 19103
SEAL & SIGNATURE


KEY PLAN

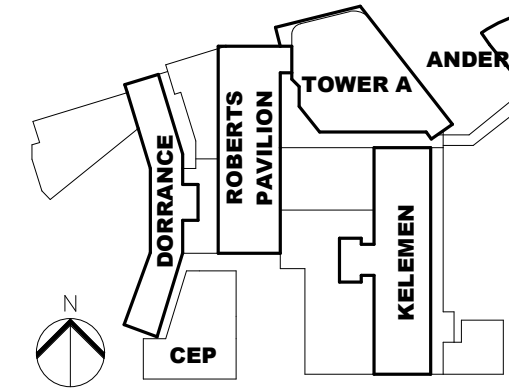

REVISION	DESCRIPTION	DATE
1	Revision 4 T&D	Date 4
2	BULLETIN #9	03/27/2026

HKS PROJECT NUMBER
25695.100
DATE
10/15/2024
ISSUE
CORE & SHELL PERMIT SET
SHEET TITLE
DEMOLITION PLAN - LEVEL 01 OVERBUILD

BUILDING PERMIT NUMBER: 1111
SHEET NO.
AD2.01.2

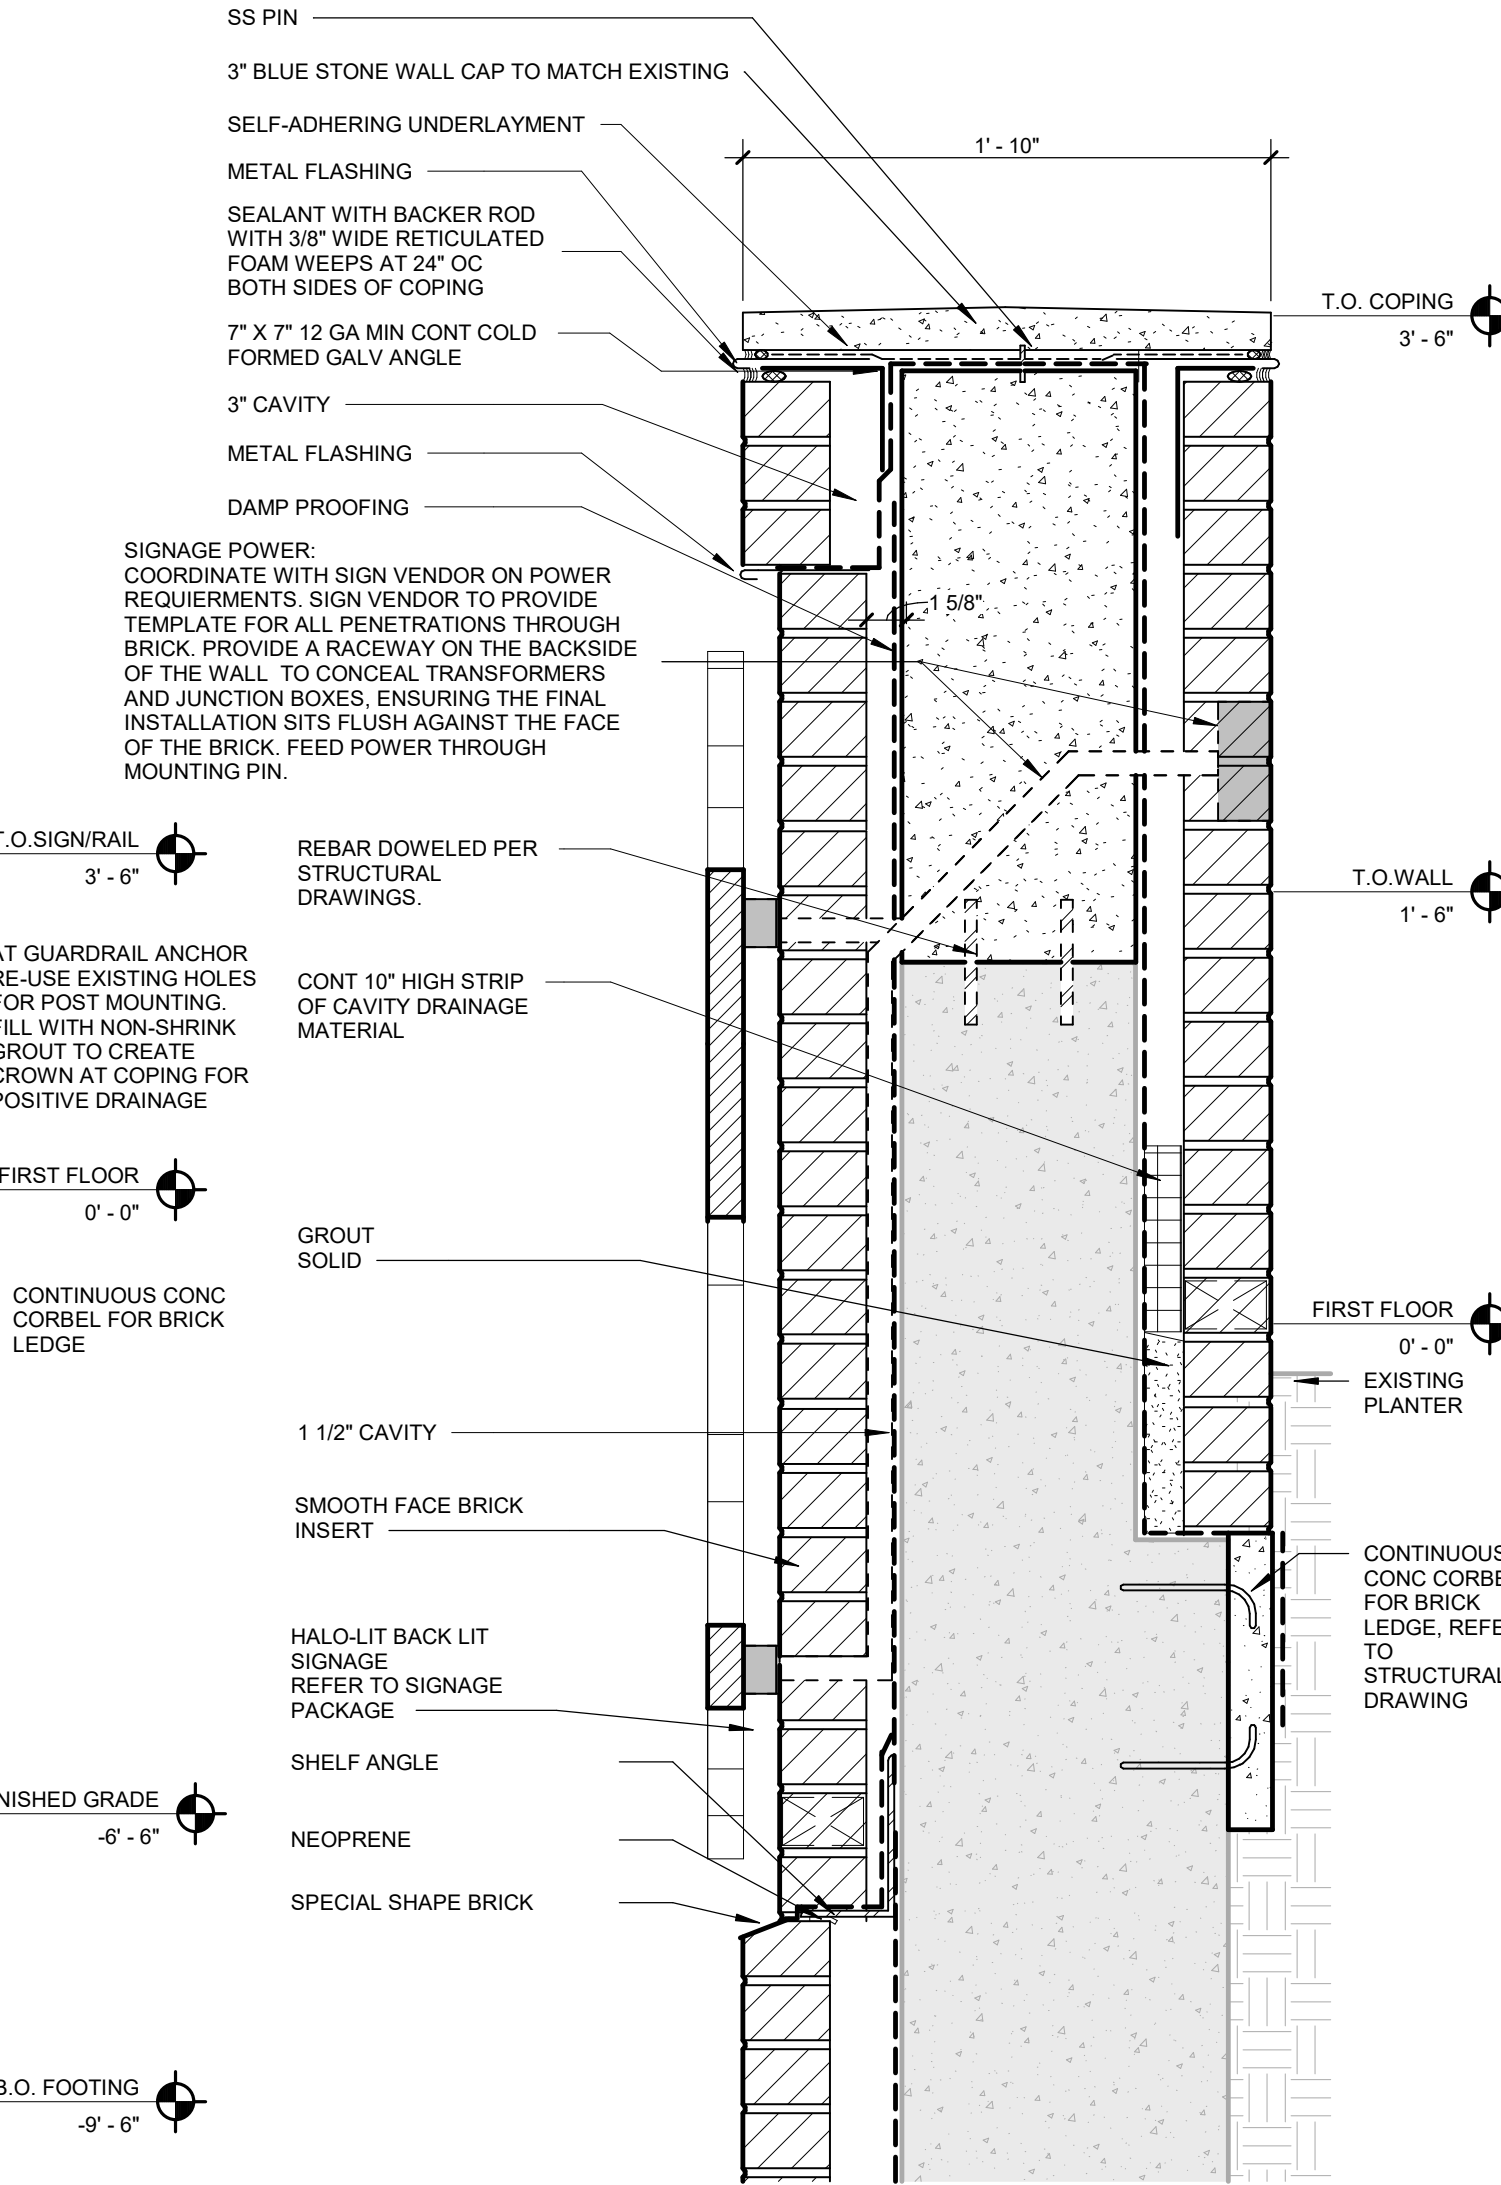

- | GENERAL NOTES - FLOOR PLAN | |
|----------------------------|---|
| 1. | REFER TO SHEET A3.01 FOR PARTITION TYPES, GRAPHIC AND SYMBOLIC DESIGNATIONS, NOTES, AND DETAILS. |
| 2. | REFER TO SHEET A3.02 FOR MISCELLANEOUS MEAL FABRICATION (MF) TYPES AND DETAILS. |
| 3. | REFER TO SHEET A3.31 FOR FOOD INFORMATION, SCHEDULES AND DETAILS. |
| 4. | REFER TO SHEET SERIES 5.00 FOR EXTERIOR ELEVATIONS. |
| 5. | REFER TO SHEET SERIES 8.00 FOR STAIR AND ELEVATOR SECTIONS AND DETAILS. |
| 6. | ALL EXTERIOR DIMENSIONS ARE FROM FACE OF EXTERIOR FINISH, U.N.O. |
| 7. | MASSORY DIMENSIONS ARE NOMINAL, U.N.O. |
| 8. | VERIFY SLAB EDGE DIMENSIONS AT EXISTING BUILDINGS |
| 9. | EXTERIOR WALL, CONTAINMENT WALL, AND COORDINATE SLAB EDGE DIMENSION WITH EXTERIOR WALL COMPONENTS AND FINAL DEPTH OF SYSTEMS. |
| 10. | REMOVE SLAB SUPPORT BODY/HARD BODY WALL ASSEMBLIES FOR INTERIOR EXIST STAIRWAYS, SHEDS, AND ELEVATOR HOISTWAYS AS |

RESERVE FOR DCA STAMP

HKS
ARRAY
architects

ARCHITECT
HKS, P.C.
12501 (I)EYE STREET NW, SUITE 800
WASHINGTON, DC 20005

**ASSOCIATE ARCHITECT /
INTERIOR DESIGNER**
ARRAY
1 WEST ELM STREET, SUITE 500
CONSHOHOCKEN, PA 19428

STRUCTURAL ENGINEER
O'DONNELL & NACCARATO
701 MARKET ST, #6000
PHILADELPHIA, PA 19106

**MEP-FP / LOW VOLTAGE
ENGINEER**
BRA+ CONSULTING ENGINEERS
2401 WALNUT ST SUITE 701
PHILADELPHIA, PA 19103

HIGHLAND ASSOCIATES
102 HIGHLAND AVE
CLARKS SUMMIT, PA 18411

Cooper
University Health Care


**COOPER UNIVERSITY
HOSPITAL - TOWER A**

OWNER
COOPER UNIVERSITY HEALTHCARE
1 COOPER PLAZA
CAMDEN, NJ 08103

PROJECT MANAGER
PURE PM
2926 RICHMOND STREET
PHILADELPHIA, PA 19134

CIVIL ENGINEER / LANDSCAPE
LANGAN
1818 MARKET STREET, SUITE 3300
PHILADELPHIA, PA 19103

SEAL & SINGATURE

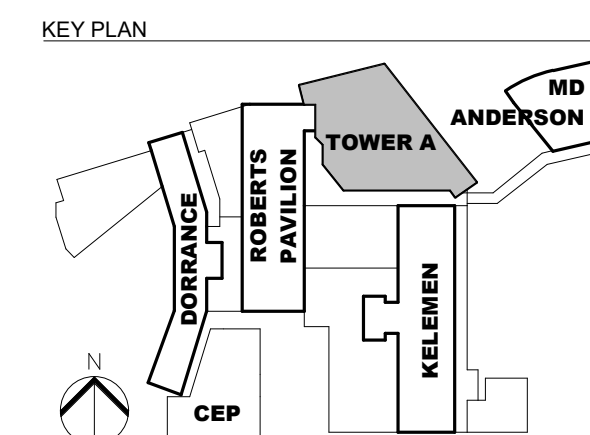

REVISION		
NO.	DESCRIPTION	DATE
1	BULLETIN #9	03/27/2026

HKS PROJECT NUMBER
25695.100
DATE
12/15/2024








**CORE & SHELL PERMIT
SET**
SHEET TITLE
**CORE & SHELL FLOOR
PLAN - LEVEL 01 -
OVERBUILD**

SHEET NO. 1

A1.101.2

TITLE BLOCK VERSION: 20210830
MODEL: A510.dwg 25695.000 Cooper Medical Campus Plan 2023.04 CHAT Tower A, Exterior 2023.rvt
PRINT DATE: 3/27/2026 4:41:54 PM TEMPLATE VERSION: 23.0.3

FACADE MATERIAL LEGEND

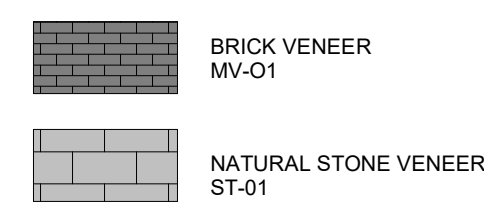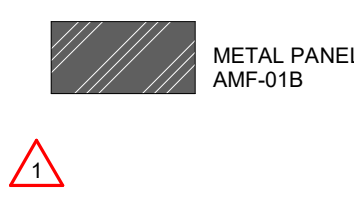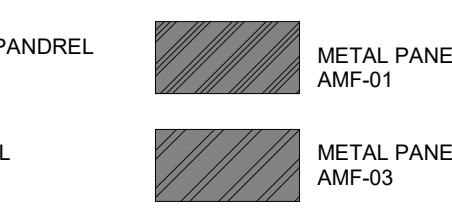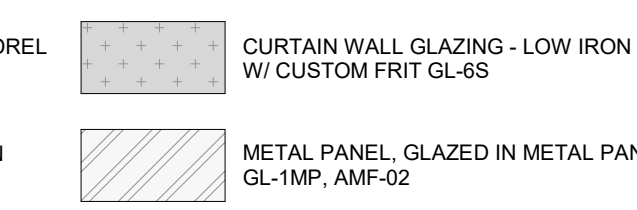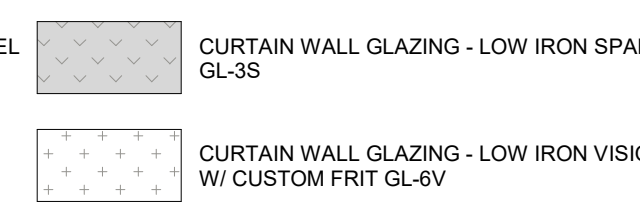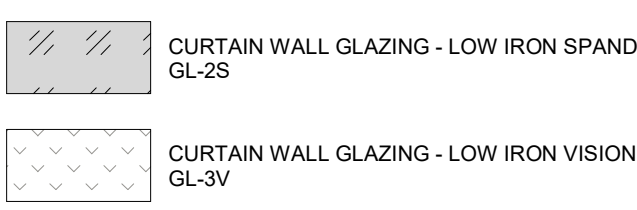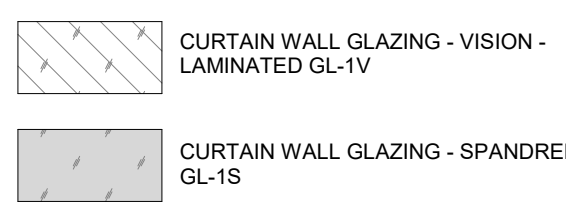

GENERAL NOTES

1. REFER TO SPECIFICATION SECTION XX.XX.XX FOR DETAILED EXTERIOR DESIGN SELECTIONS.
2. SEE NOTES ON ELEVATIONS FOR LOUVER LOCATIONS.
3. SEE NOTES ON ELEVATIONS AND DETAILS FOR PARAPET CORING AND CAP TYPES. ALL CORING AND CAP FINISHES TO MATCH CARVED MATERIAL UNO.
4. PROVIDE SIGNAGE SUPPORT THROUGH CURTAIN WALL FRAMING.
5. SEE LIGHTING DRAWINGS FOR EXTERIOR LIGHTING.

RESERVE FOR DCA STAMP



ARCHITECT
HKS, P.C.
1250 I (EVE) STREET NW, SUITE 600
WASHINGTON, DC 20005
ASSOCIATE ARCHITECT / INTERIOR DESIGNER
ARRAY
1 WEST ELM STREET, SUITE 500
CONSHOHOCKEN, PA 19028
STRUCTURAL ENGINEER
O'DONNELL & NACCARATO
701 MARKET ST., #6000
PHILADELPHIA, PA 19106
MEP-FP / LOW VOLTAGE ENGINEER
BR+A CONSULTING ENGINEERS
2401 WALNUT ST SUITE 701
PHILADELPHIA, PA 19103
HIGHLAND ASSOCIATES
102 HIGHLAND AVE
CLARKS SUMMIT, PA 18411



OWNER
COOPER UNIVERSITY HEALTHCARE
1 COOPER PLAZA
CAMDEN, NJ 08103
PROJECT MANAGER
PURE PM
2026 RICHMOND STREET
PHILADELPHIA, PA 19134
CIVIL ENGINEER / LANDSCAPE
LANGAN
1818 MARKET STREET, SUITE 3300
PHILADELPHIA, PA 19103
SEAL & SIGNATURE

KEY PLAN

NO.	REVISION	DESCRIPTION	DATE
1	BULLETIN #4		04/28/2025
2	RFI 0085		11/11/2024
3	RFI 336		09/29/2025
4	BULLETIN #9		03/27/2026

HKS PROJECT NUMBER
25695.100
DATE
10/15/2024
ISSUE
CORE & SHELL PERMIT SET
SHEET TITLE
PARTIAL BUILDING ELEVATIONS

SHEET NO.

A5.10

BUILDING PERMIT NUMBER: 1111

© HKS, INC.

09 ENTRY GUARD RAIL

1/4" = 1'-0"

03 EL-BLDG-PARTIAL-PH-MACHINE ROOM SE

1/8" = 1'-0"

07 ENTRY SITE SIGNAGE

1/8" = 1'-0"

06 EL-BLDG-PARTIAL-SE STAIR-NORTH

1/8" = 1'-0"

02 EL-BLDG-PARTIAL-PH-NE

1/8" = 1'-0"

08 ENTRY SITE STAIR ELEVATION

1/8" = 1'-0"

05 EL-BLDG-PARTIAL-SE STAIR-NORTH

1/8" = 1'-0"

04 EL-BLDG-PARTIAL-PH-SE

1/8" = 1'-0"

01 EL-BLDG-PARTIAL-PH-NW

1/8" = 1'-0"