


TITLE BLOCK VERSION: 20210830
MODEL: A:\models\25695.000_Cooper_Miller_Campus_Plan_2023\A_Cooper_TowerA_Estimate_2023.rvt
PRINT DATE: 11/21/2025 9:24:38 PM
TEMPLATE VERSION: 23.0.3

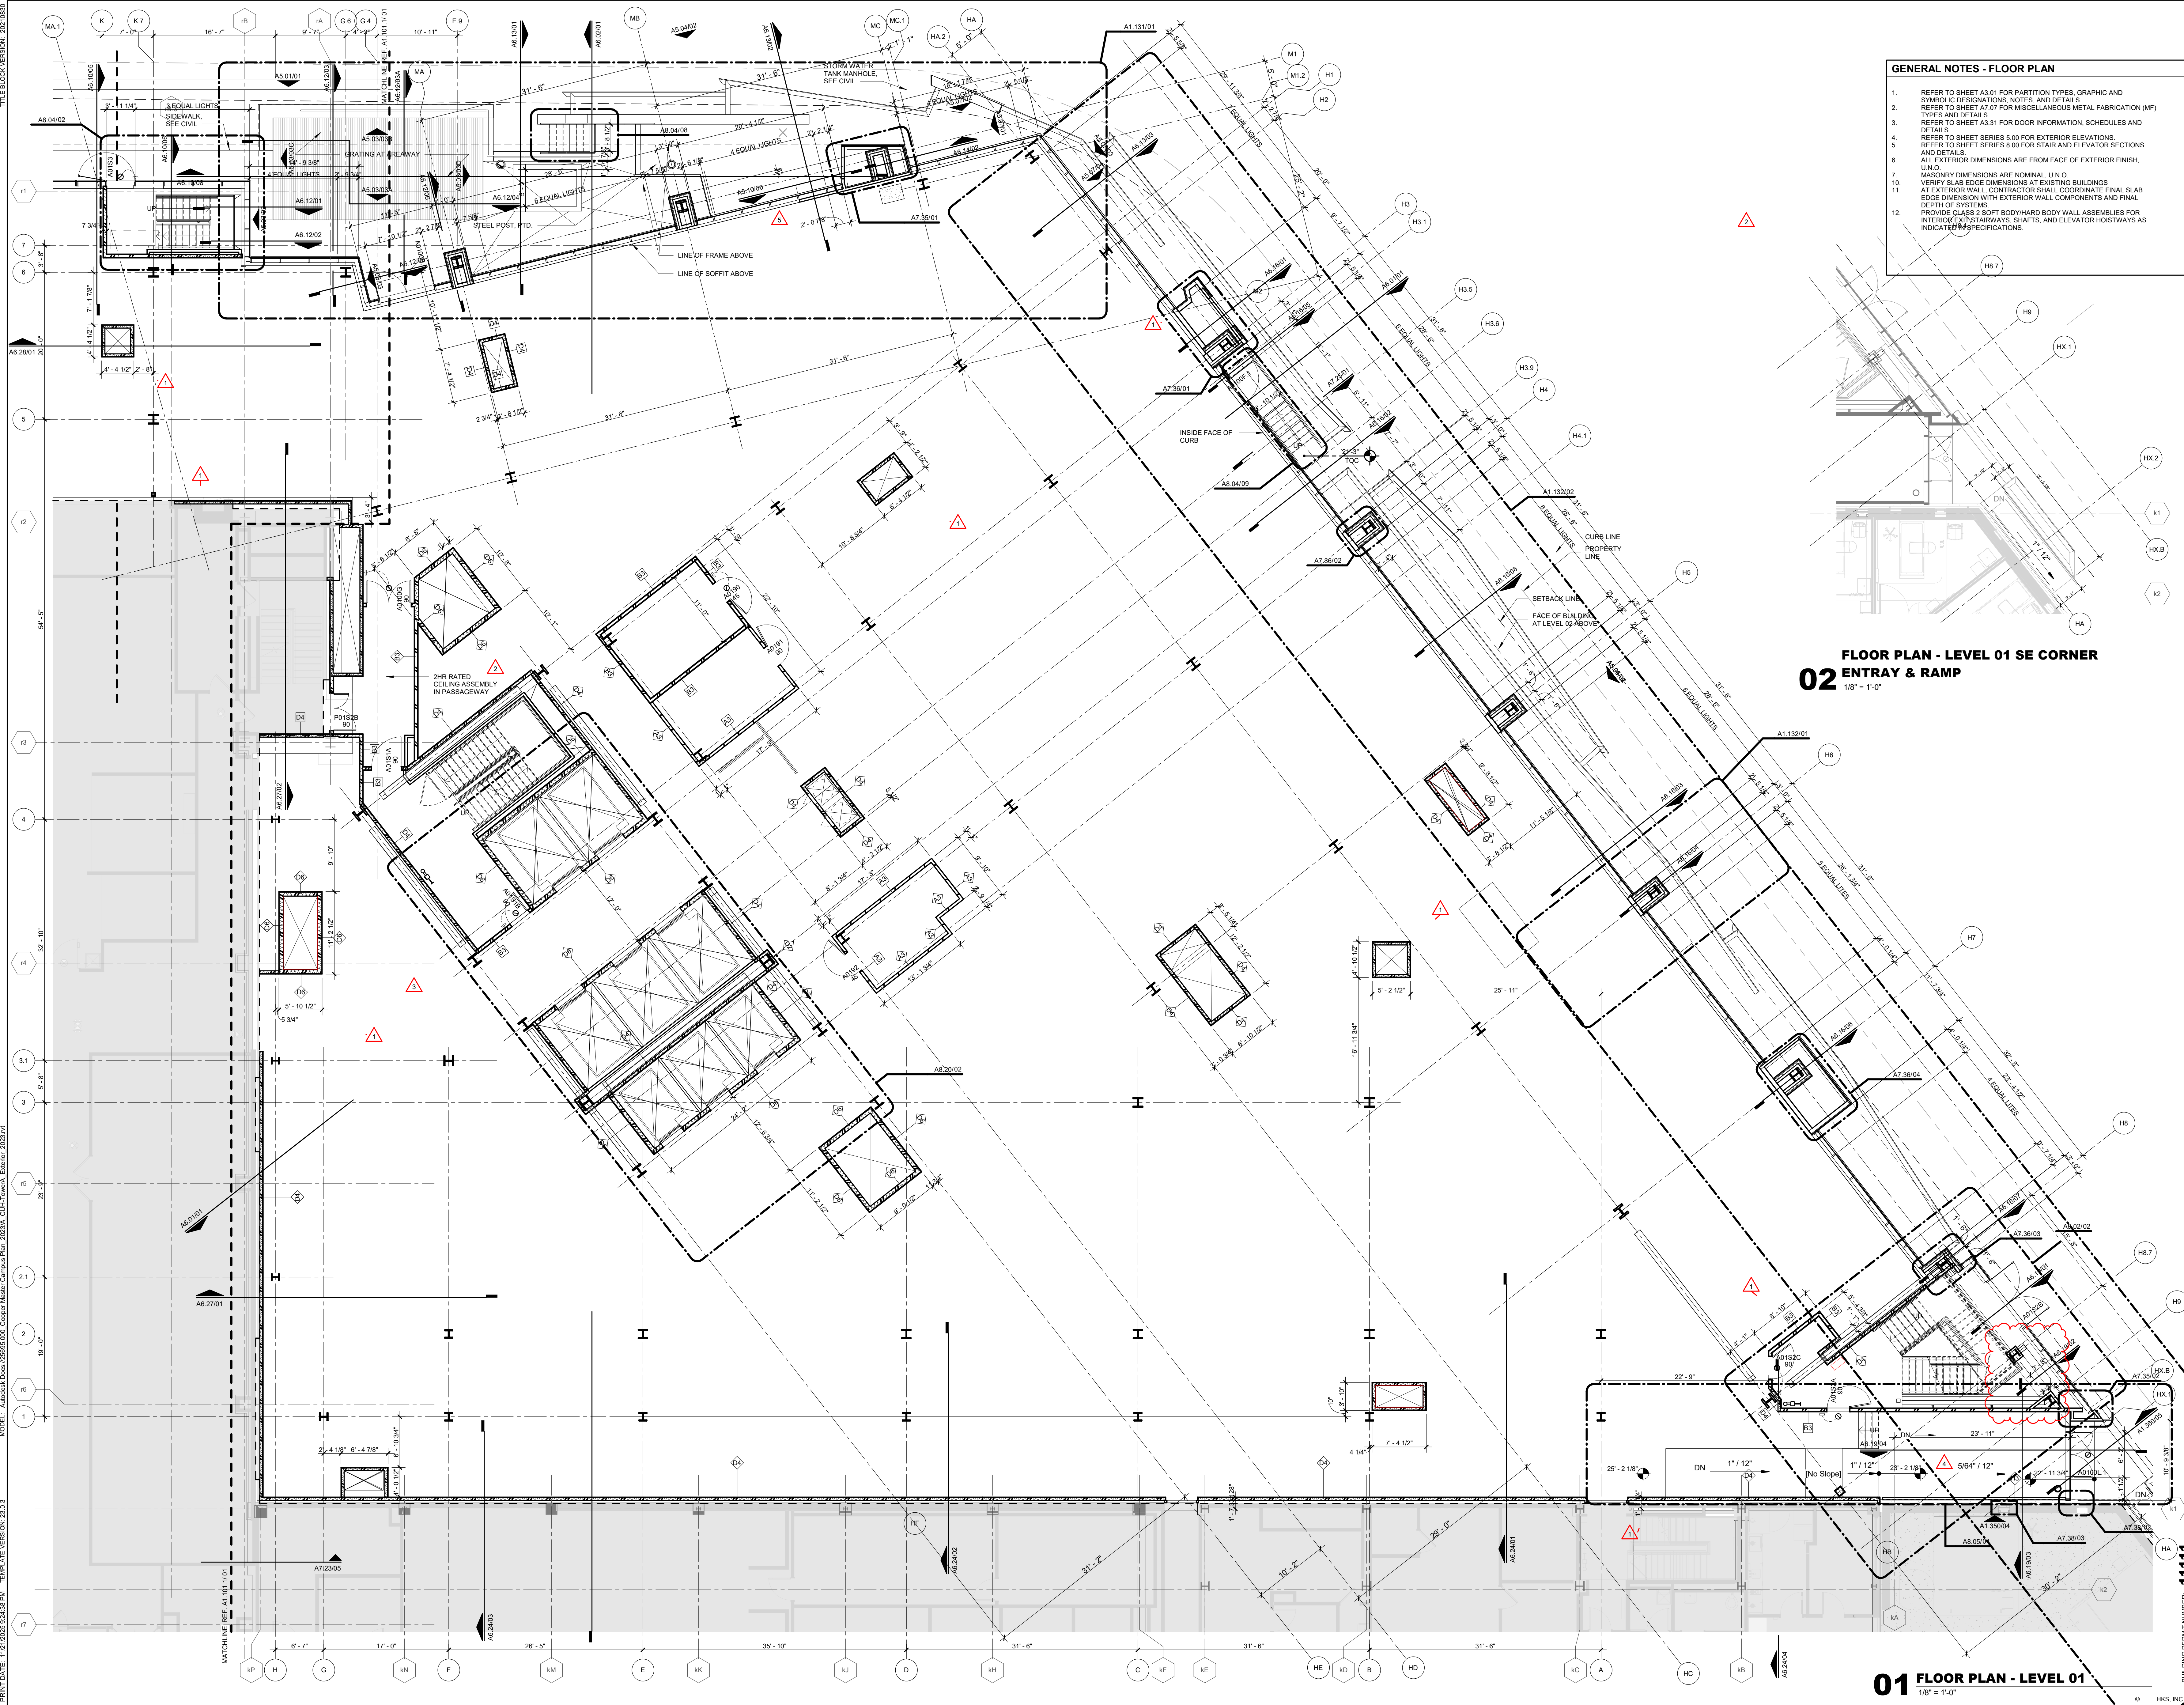

- GENERAL NOTES - FLOOR PLAN**
1. REFER TO SHEET A3.01 FOR PARTITION TYPES, GRAPHIC AND SYMBOLIC DESIGNATIONS, NOTES, AND DETAILS.
 2. REFER TO SHEET A7.07 FOR MISCELLANEOUS METAL FABRICATION (MF) TYPES AND DETAILS.
 3. REFER TO SHEET A3.31 FOR DOOR INFORMATION, SCHEDULES AND DETAILS.
 4. REFER TO SHEET SERIES 5.00 FOR EXTERIOR ELEVATIONS.
 5. REFER TO SHEET SERIES 8.00 FOR STAIR AND ELEVATOR SECTIONS AND DETAILS.
 6. ALL EXTERIOR DIMENSIONS ARE FROM FACE OF EXTERIOR FINISH, UNLESS NOTED OTHERWISE.
 7. MASONRY DIMENSIONS ARE NOMINAL, U.N.O.
 8. VERIFY SLAB EDGE DIMENSIONS AT EXISTING BUILDINGS.
 9. AT EXTERIOR WALL, CONTRACTOR SHALL COORDINATE FINAL SLAB EDGE DIMENSION WITH EXTERIOR WALL COMPONENTS AND FINAL DEPTH OF SYSTEMS.
 10. PROVIDE CLASS 3 SOT BODY AND BODY WALL ASSEMBLIES FOR INTERIOR EXISTING STAIRWAYS, SHAFTS, AND ELEVATOR HOISTWAYS AS INDICATED IN SPECIFICATIONS.
 - 11.
 - 12.

02 FLOOR PLAN - LEVEL 01 SE CORNER ENTRAY & RAMP
1/8" = 1'-0"

01 FLOOR PLAN - LEVEL 01
1/8" = 1'-0"

RESERVE FOR DCA STAMP



ARCHITECT
HKS, P.C.
1250 (EVE) STREET NW, SUITE 600
WASHINGTON, DC 20005

ASSOCIATE ARCHITECT / INTERIOR DESIGNER
ARRAY
1 WEST ELM STREET, SUITE 500
CONSHOHOCKEN, PA 19028

STRUCTURAL ENGINEER
O'DONNELL & NACCARATO
701 MARKET ST., #6000
PHILADELPHIA, PA 19106

MEP-FP / LOW VOLTAGE ENGINEER
BR-A CONSULTING ENGINEERS
2401 WALNUT ST SUITE 701
PHILADELPHIA, PA 19103

ENGINEER
HIGHLAND ASSOCIATES
102 HIGHLAND AVE
CLARKS SUMMIT, PA 18411


Cooper University Health Care
COOPER UNIVERSITY HOSPITAL - TOWER A
PROJECT ADDRESS: 1 COOPER PLAZA, CAMDEN, NJ 08103

OWNER
COOPER UNIVERSITY HEALTHCARE
1 COOPER PLAZA
CAMDEN, NJ 08103

PROJECT MANAGER
PURE PM
2026 RICHMOND STREET
PHILADELPHIA, PA 19134

CIVIL ENGINEER / LANDSCAPE
LANGAN
1818 MARKET STREET, SUITE 3300
PHILADELPHIA, PA 19103

SEAL & SINGATURE

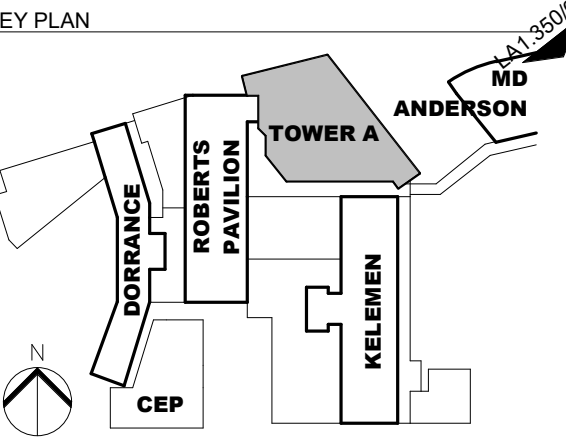

NO.	REVISION	DATE
1	BULLETIN #2	01/23/2025
2	BULLETIN #4	04/28/2025
3	BULLETIN #5	07/11/2025
4	RFI 0174-01	07/22/2025
5	RFI 355	08/29/2025
6	RFI 0416	11/14/2025

HKS PROJECT NUMBER
25695.100


DATE
10/15/2024

ISSUE
CORE & SHELL PERMIT SET

SHEET TITLE
CORE & SHELL FLOOR PLAN - LEVEL 01

SHEET NO.
A1.101

TITLE BLOCK VERSION: 20210830
MODEL: A:\models\25695.000_Cooper_Miller_Campus_Plan_2023.dwg
PRINT DATE: 11/21/2025 9:24:41 PM
TEMPLATE VERSION: 23.0.3

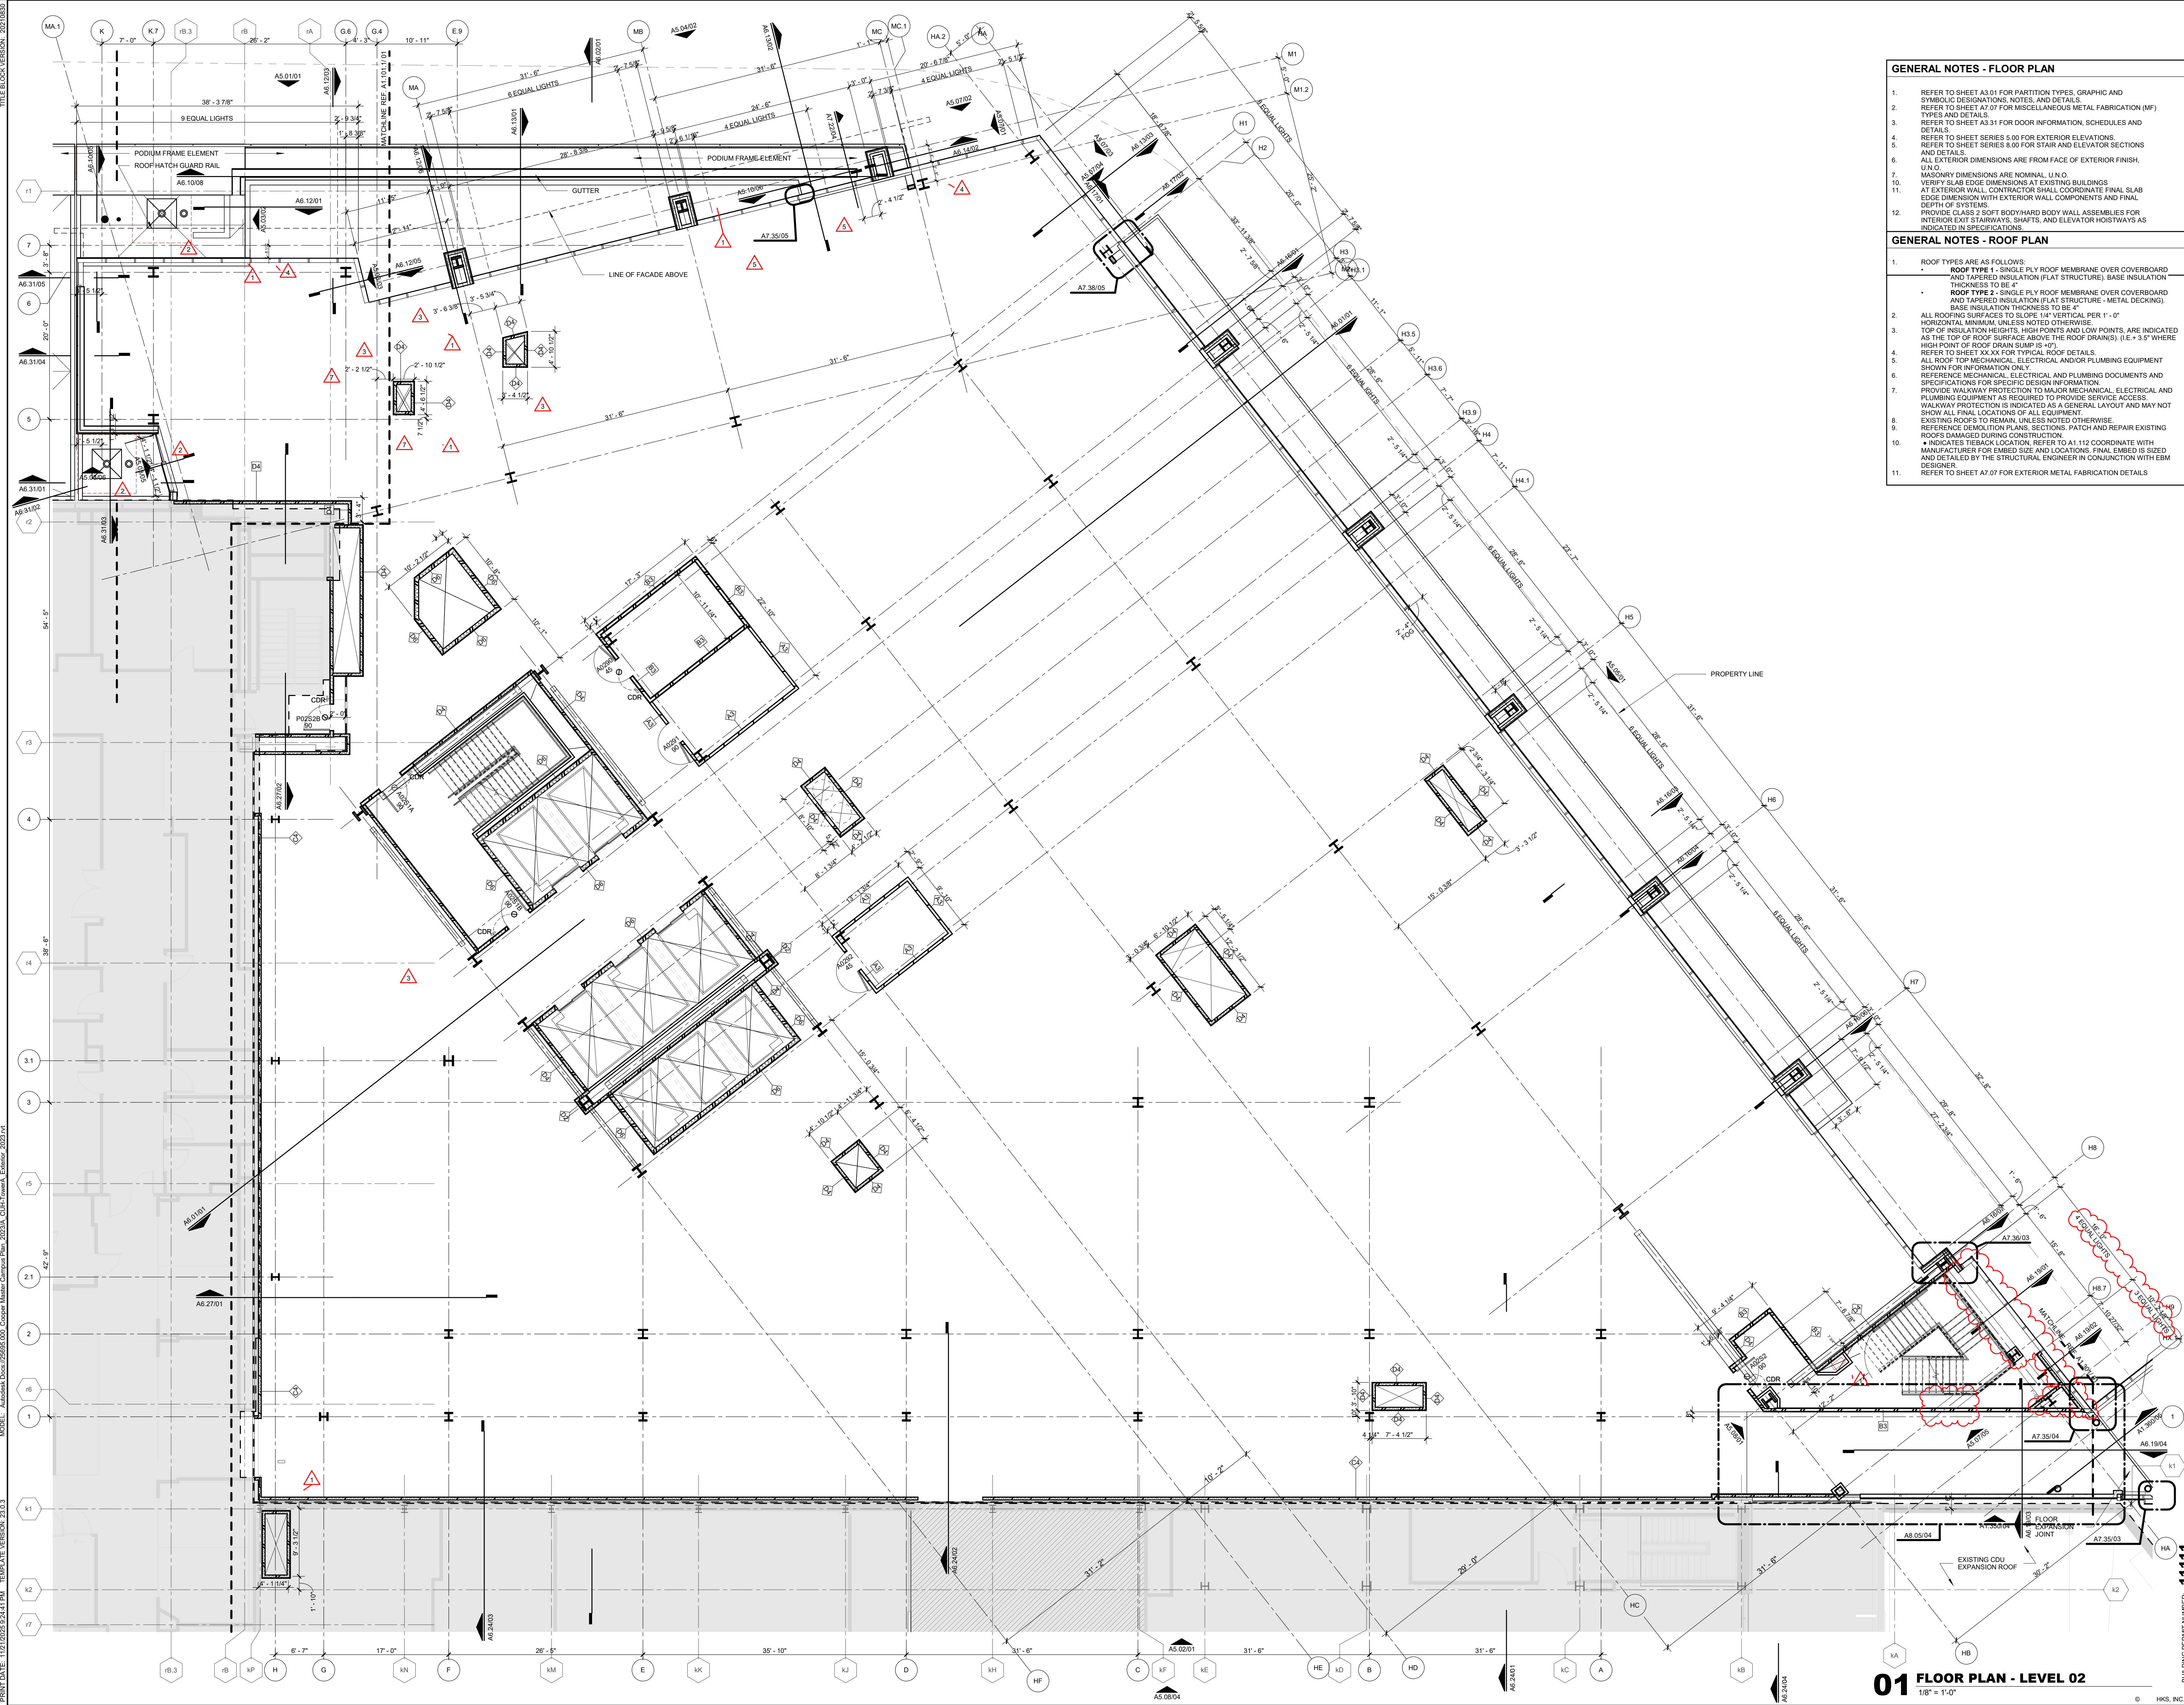

RESERVE FOR DCA STAMP

HKS
ARRAY
architects

ARCHITECT
HKS, P.C.
1250 (EYE) STREET NW, SUITE 600
WASHINGTON, DC 20005

ASSOCIATE ARCHITECT / INTERIOR DESIGNER
ARRAY
1 WEST ELM STREET, SUITE 500
CONSHOHOCKEN, PA 19028

STRUCTURAL ENGINEER
O'DONNELL & NACCARATO
701 MARKET ST., #600
PHILADELPHIA, PA 19106

MEP-FP / LOW VOLTAGE ENGINEER
BR+A CONSULTING ENGINEERS
2401 WALNUT ST SUITE 701
PHILADELPHIA, PA 19103

OWNER
COOPER UNIVERSITY HEALTHCARE
1 COOPER PLAZA
CAMDEN, NJ 08103

PROJECT MANAGER
PURE PM
2026 RICHMOND STREET
PHILADELPHIA, PA 19134

CIVIL ENGINEER / LANDSCAPE
LANGAN
1818 MARKET STREET, SUITE 3300
PHILADELPHIA, PA 19103

SEAL & SIGNATURE

Cooper
University Health Care

COOPER UNIVERSITY HOSPITAL - TOWER A

PROJECT ADDRESS: 1 COOPER PLAZA, CAMDEN, NJ 08103

KEY PLAN

REVISION

NO.	DESCRIPTION	DATE
1	BULLETIN #2	01/23/2025
2	BULLETIN #4	04/28/2025
3	BULLETIN #5	07/11/2025
4	RFI 0252-01	07/14/2025
5	RFI 355	08/29/2025
6	RFI XXX	10/1/2025
7	RFI 0344	10/03/2025
8	RFI 0416	11/14/2025

HKS PROJECT NUMBER
25695.100

DATE
10/15/2024


ISSUE
CORE & SHELL PERMIT SET

SHEET TITLE
CORE & SHELL FLOOR PLAN - LEVEL 02

SHEET NO.
A1.102

BUILDING PERMIT NUMBER: 1111

© HKS, INC.

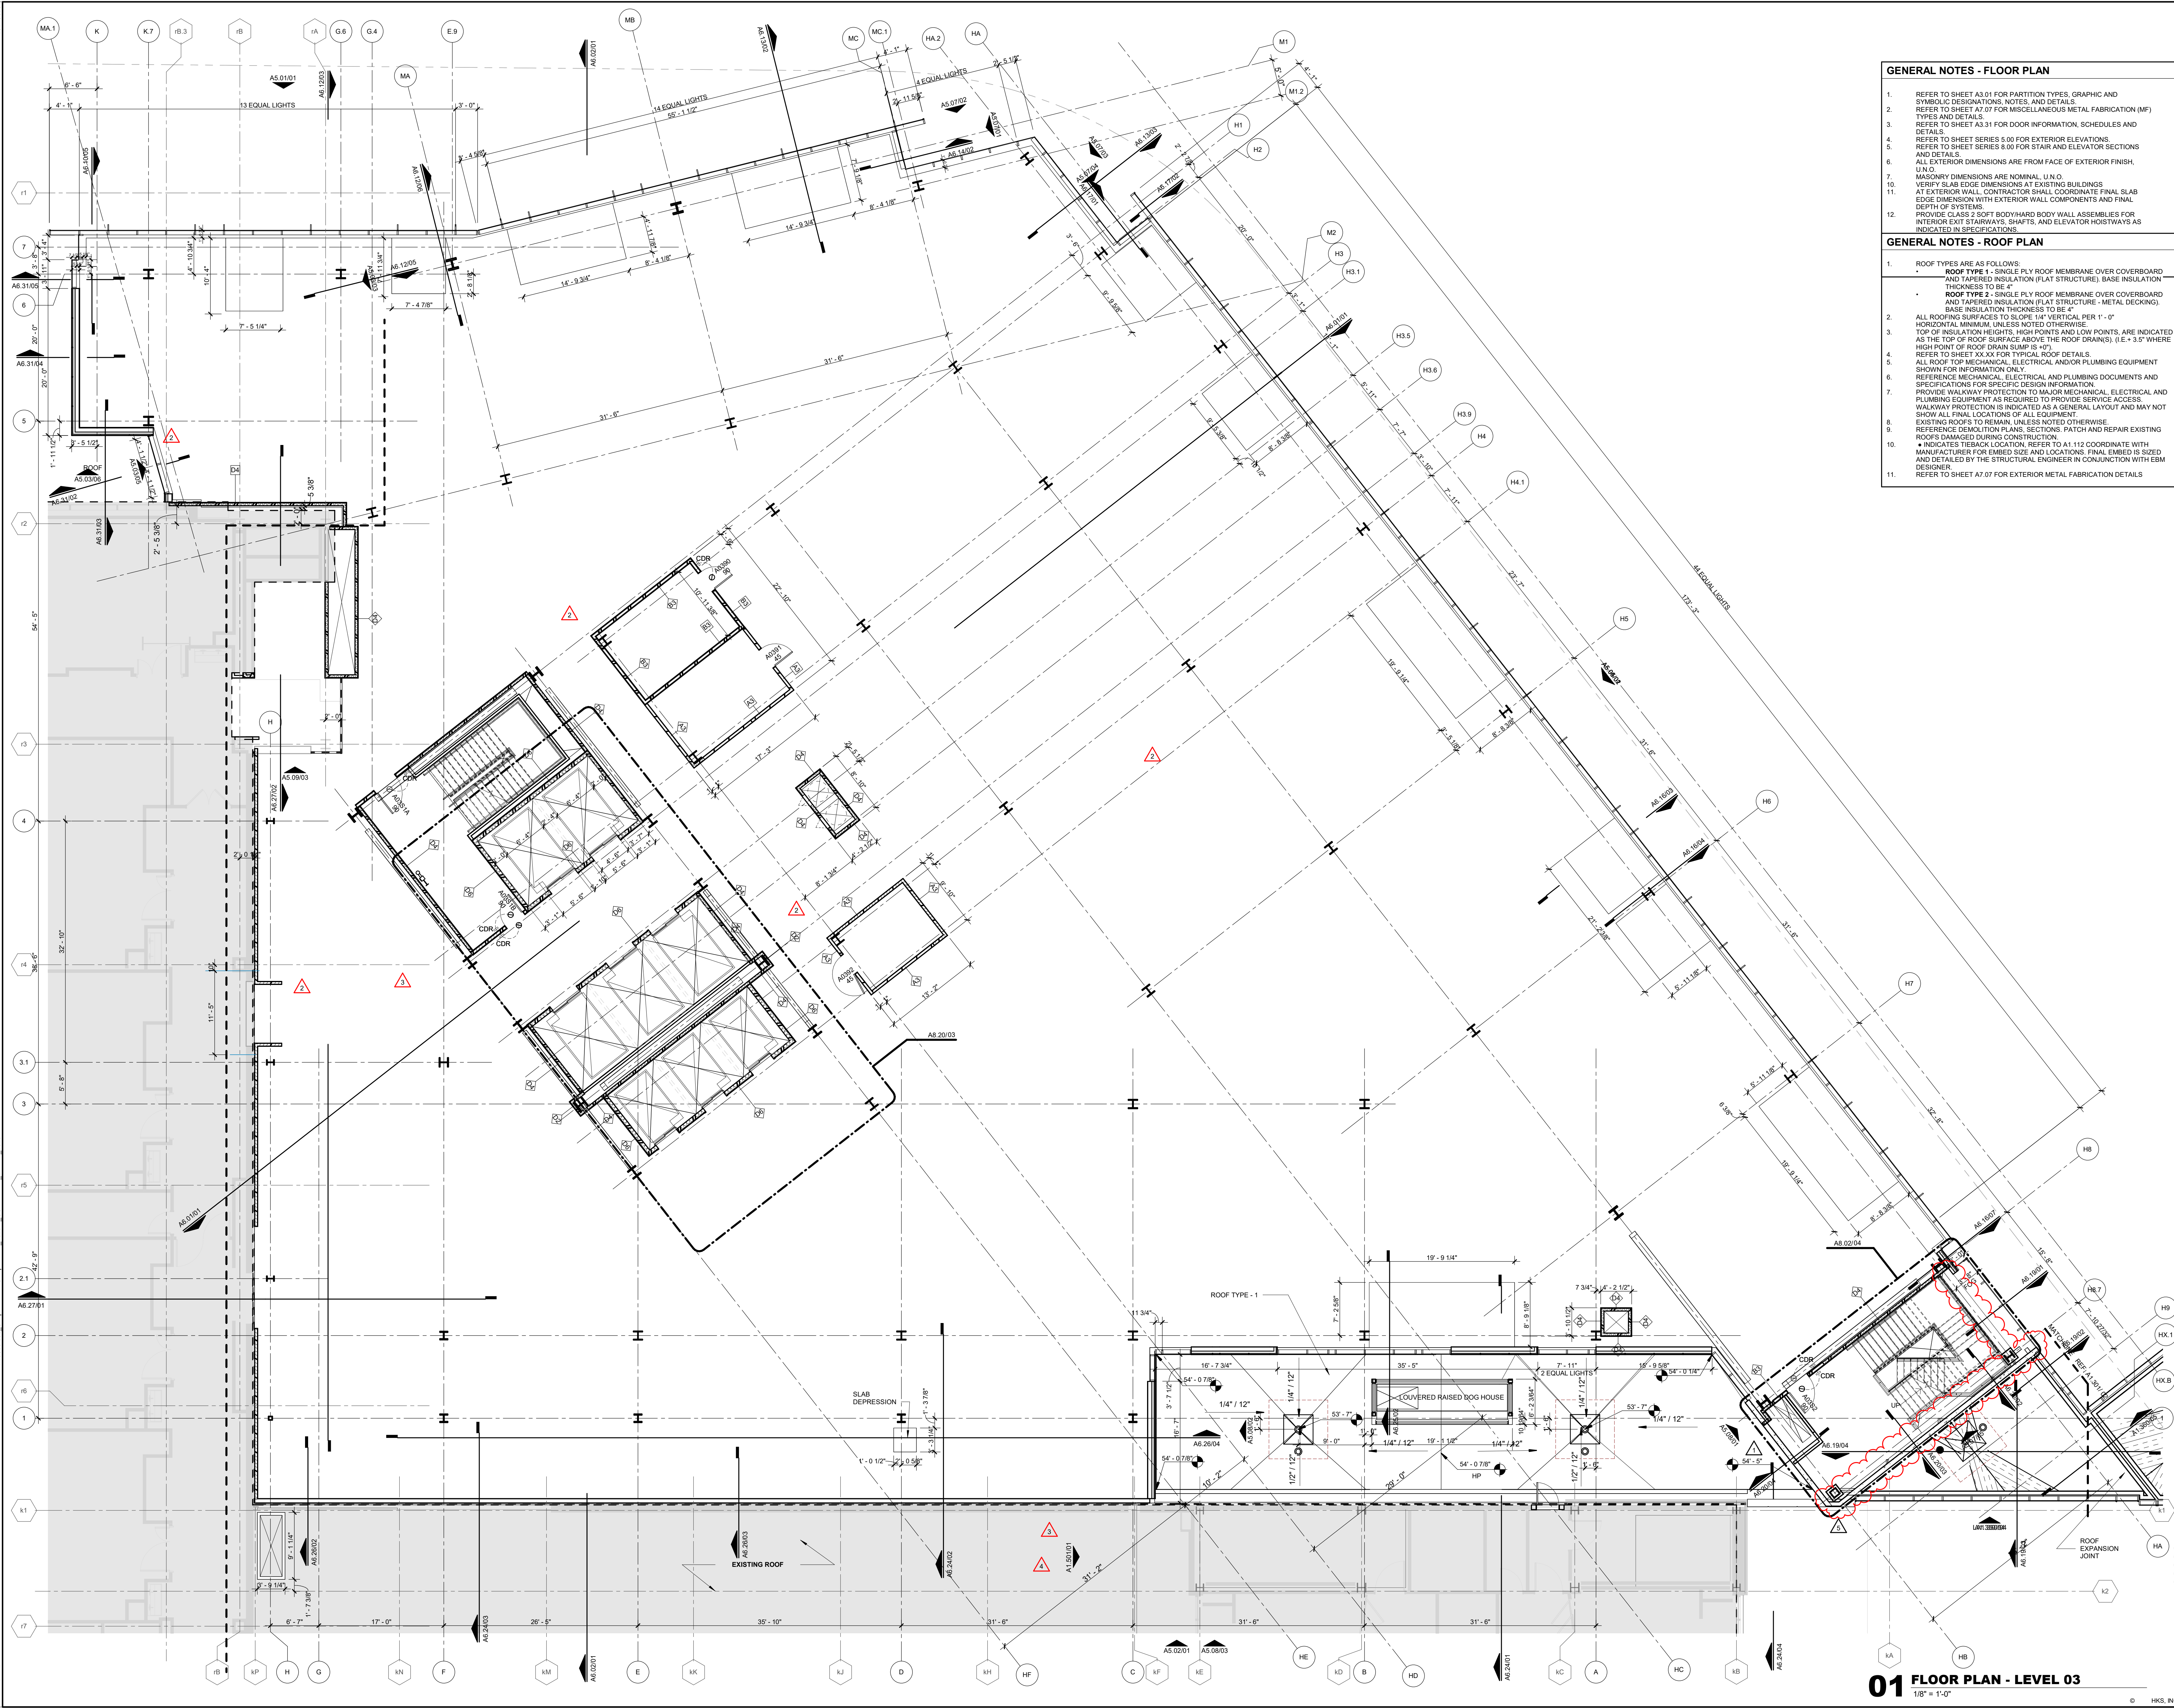

- ## GENERAL NOTES - FLOOR PLAN
- | | |
|-----|---|
| 1. | REFER TO SHEET A0.1 FOR PARTITION TYPES, GRAPHIC AND SYMBOLIC DESIGNATIONS, TYPES, AND DETAILS. |
| 2. | REFER TO SHEET 07.07 FOR INTERMEDIATE METAL FABRICATION (MF) TYPES AND DETAILS. |
| 3. | REFER TO SHEET A0.3.1 FOR DOOR INFORMATION, SCHEDULES AND DETAILS. |
| 4. | REFER TO SHEET SERIES S.00 FOR EXTERIOR ELEVATIONS. |
| 5. | REFER TO SHEET SERIES S.00 FOR STAIR AND ELEVATOR SECTIONS AND DETAILS. |
| 6. | ADDITIONAL DIMENSIONS ARE FROM FACE OF EXTERIOR FINISH, U.N.O. |
| 7. | UNO FINISH DIMENSIONS ARE NOMINAL, U.N.O. |
| 8. | VERIFY SLAB EDGE DIMENSIONS AT EXISTING BUILDINGS. |
| 9. | INTERIOR WALL, CORNER AND COLUMN FINISHES TO MATCH SLAB EDGE DIMENSION WITH EXTERIOR WALL COMPONENTS AND FINAL FINISH SYSTEMS. |
| 10. | PROVIDE GLASS 2" SOFT BODYWARD BODY WALL ASSEMBLIES FOR INTERIOR EXIT STAIRWAYS, SHAFTS, AND ELEVATOR HOISTWAYS AS INDICATED IN SPECIFICATIONS. |
- ## GENERAL NOTES - ROOF PLAN
- | | |
|-----|---|
| 1. | ROOF TYPES ARE AS FOLLOWS: |
| 2. | • ROOF TYPE 1 - SINGLE PLY MEMBRANE OVER COVERBOARD AND TAPERED INSULATION (FLAT STRUCTURE) - BASE INSULATION IS TO BE DETERMINED BY: |
| 3. | • ROOF TYPE 2 - SINGLE PLY MEMBRANE OVER COVERBOARD AND TAPERED INSULATION (FLAT STRUCTURE - METAL DECKING) - BASE INSULATION IS TO BE DETERMINED BY: |
| 4. | • ALL ROOF SURFACES TO SLOPE 1/4" VERTICAL PER 1' - 0" |
| 5. | • MINIMUM ANGLE OF ROOF SLOPE TO BE 1/4" |
| 6. | • TOP OF INSULATION HEIGHTS, HIGH POINTS AND LOW POINTS ARE INDICATED AS THE TOP OF ROOF SURFACE ABOVE THE ROOF DRAINS; (I.E. ± 3") ARE THE HIGHEST OF ROOF DRAIN SUMPS ± 0" |
| 7. | • REFER TO SHEET XXXX FOR TYPICAL ROOF DETAILS |
| 8. | • REFER TO TOP MECHANICAL AND PLUMBING EQUIPMENT LUMMING EQUIPMENT SHOWN FOR INFORMATION ONLY |
| 9. | • REFER TO MECHANICAL AND PLUMBING EQUIPMENT LUMMING EQUIPMENT AND SPECIFICATIONS FOR SPECIFIC DESIGN INFORMATION. |
| 10. | • REFER TO WALKWAY PLAN FOR INFORMATION REGARDING ELECTRICAL AND PLUMBING EQUIPMENT AS REQUIRED TO PROVIDE SERVICE ACCESS. |
| 11. | • WALKWAY PROTECTION IS INDICATED AS A GENERAL ALLEYWAY AND MAY NOT SHOW ALL FINAL LANE TAGS OF ALL EQUIPMENT. |
| 12. | • EXISTING ROOFS TO REMAIN, UNLESS NOTED OTHERWISE. |
| 13. | • EXISTING CRACKS TO BE REPAIRED AND PATCH REPAIR EXISTING ROOFS DAMAGED DURING CONSTRUCTION. |
| 14. | • SEE TRACK LOG FOR LOCATION AND COORDINATES AT 112 COORDINATE WITH MANUFACTURER FOR EMBED SIZE AND LOCATION. FINAL EMBED IS SIZED AND DETAILED BY THE STRUCTURAL ENGINEER IN CONJUNCTION WITH EBM DESIGN. |
| 15. | • REFER TO SHEET A0.7 FOR EXTERIOR METAL FABRICATION DETAILS |

RESERVE FOR DCA STAMP

HKS

ARRAY
architects

ARCHITECT
HKS, P.C.
12501 (EVE) STREET NW, SUITE 600
WASHINGTON, DC 20005

**ASSOCIATE ARCHITECT /
INTERIOR DESIGNER**
ARRAY
1 WEST ELM STREET, SUITE 500
CONSHOHOCKEN, PA 19428

STRUCTURAL ENGINEER
CONDONELL & MACCARATO
701 MARKET ST., #600
PHILADELPHIA, PA 19106

**MEP-FP / LOW VOLTAGE
ENGINEER**
BR+R CONSULTING ENGINEERS
2401 WALNUT ST SUITE 701
PHILADELPHIA, PA 19103

HIGHLAND ASSOCIATES
102 HIGHLAND AVE
CLARKS SUMMIT, PA 18411

Cooper
University Health Care


**COOPER UNIVERSITY
HOSPITAL - TOWER A**

OWNER
COOPER UNIVERSITY HEALTHCARE
1 COOPER PLAZA
CAMDEN, NJ 08103

PROJECT MANAGER
PURE PM
2926 RICHMOND STREET
PHILADELPHIA, PA 19134

CIVIL ENGINEER / LANDSCAPE
LANGAN
1818 MARKET STREET, SUITE 3300
PHILADELPHIA, PA 19103

SEAL & SINGATURE

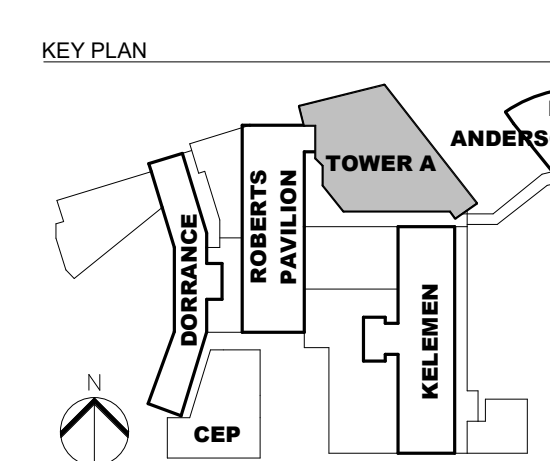

REVISION		
NO.	DESCRIPTION	DATE
1	BULLETIN #2	01/23/00
2	BULLETIN #4	04/28/00
3	BULLETIN #5	07/11/00
4	RFI 0315-00	08/06/00
5	RFI 0416	11/14/00

HKS PROJECT NUMBER
25695.100

DATE
10/15/2024


ISSUE
**CORE & SHELL PERMI
SET**

SHEET TITLE
**CORE & SHELL FLOOR
PLAN - LEVEL 03**

SHEET NO.

A1.103

TITLE BLOCK VERSION: 20210830
MODEL: A:\models\25695.000_Cooper_Miller_Campus_Plan_2023\A_Cooper_TowerA_Exterior_2023.rvt
PRINT DATE: 11/21/2025 9:25:39 PM
TEMPLATE VERSION: 23.0.3
BUILDING PERMIT NUMBER: 1111

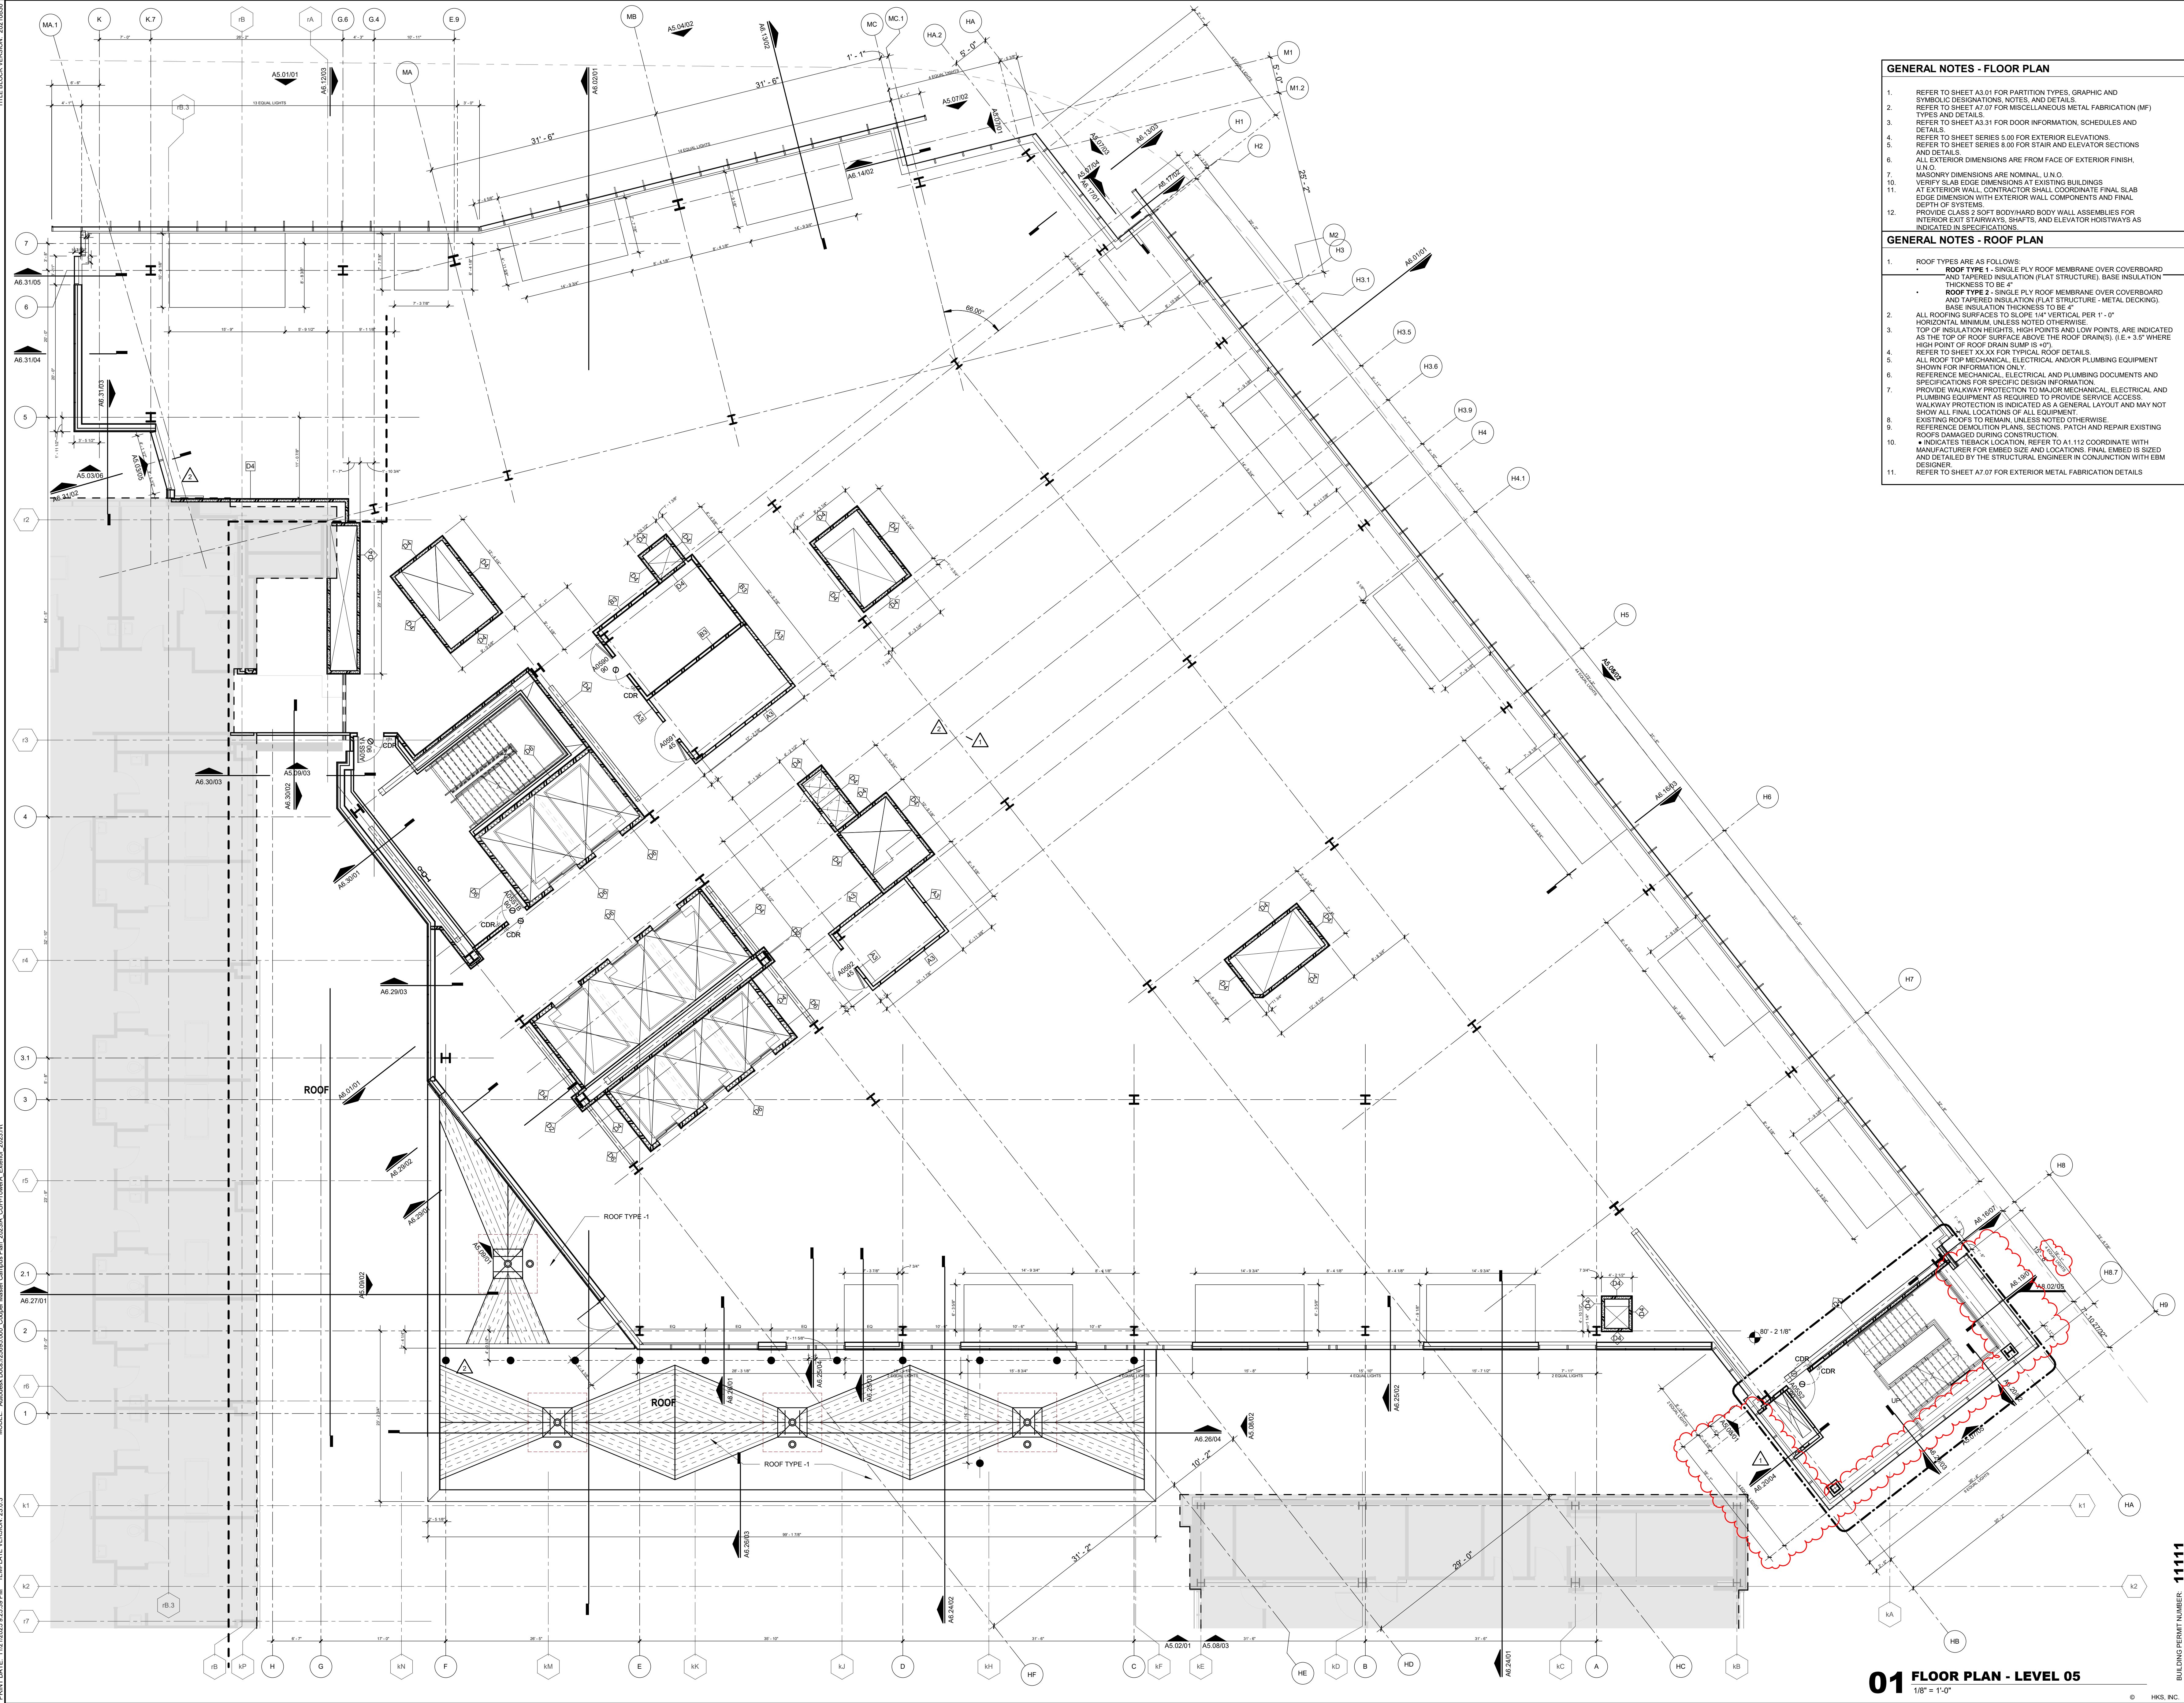

- GENERAL NOTES - FLOOR PLAN**
- REFER TO SHEET A3.01 FOR PARTITION TYPES, GRAPHIC AND SYMBOLIC DESIGNATIONS, NOTES, AND DETAILS.
 - REFER TO SHEET A7.07 FOR MISCELLANEOUS METAL FABRICATION (MF) TYPES AND DETAILS.
 - REFER TO SHEET A3.31 FOR DOOR INFORMATION, SCHEDULES AND DETAILS.
 - REFER TO SHEET SERIES 5.00 FOR EXTERIOR ELEVATIONS.
 - REFER TO SHEET SERIES 8.00 FOR STAIR AND ELEVATOR SECTIONS AND DETAILS.
 - ALL EXTERIOR DIMENSIONS ARE FROM FACE OF EXTERIOR FINISH, UNLESS NOTED OTHERWISE.
 - MASONRY DIMENSIONS ARE NOMINAL, U.N.O.
 - VERIFY SLAB EDGE DIMENSIONS AT EXISTING BUILDINGS.
 - AT EXTERIOR WALL, CONTRACTOR SHALL COORDINATE FINAL SLAB EDGE DIMENSION WITH EXTERIOR WALL COMPONENTS AND FINAL DEPTH OF SYSTEMS.
 - PROVIDE CLASS 2 SCOT BODY/WALL BODY WALL ASSEMBLIES FOR INTERIOR EXIT STAIRWAYS, SHAFTS, AND ELEVATOR HOISTWAYS AS INDICATED IN SPECIFICATIONS.
- GENERAL NOTES - ROOF PLAN**
1. ROOF TYPES ARE AS FOLLOWS:
- ROOF TYPE 1 - SINGLE PLY ROOF MEMBRANE OVER COVERBOARD AND TAPERED INSULATION (FLAT STRUCTURE). BASE INSULATION THICKNESS TO BE 4".
 - ROOF TYPE 2 - SINGLE PLY ROOF MEMBRANE OVER COVERBOARD AND TAPERED INSULATION (FLAT STRUCTURE - METAL DECKING). BASE INSULATION THICKNESS TO BE 4".
2. ALL ROOFING SURFACES TO SLOPE 1/4" VERTICAL PER 1' - 0" HORIZONTAL MINIMUM, UNLESS NOTED OTHERWISE.
3. TOP OF INSULATION HEIGHTS, HIGH POINTS AND LOW POINTS, ARE INDICATED AS THE TOP OF ROOF SURFACE ABOVE THE ROOF DRAIN(S). (0.4 ± 3.5" WHERE HIGH POINT OF ROOF DRAIN SUMP IS 40").
4. REFER TO SHEET XX.XX FOR TYPICAL ROOF DETAILS.
5. ALL ROOF TOP MECHANICAL, ELECTRICAL AND/OR PLUMBING EQUIPMENT SHOWN FOR INFORMATION ONLY.
6. REFERENCE MECHANICAL, ELECTRICAL AND PLUMBING DOCUMENTS AND SPECIFICATIONS FOR SPECIFIC DESIGN INFORMATION.
7. PROVIDE WALKWAY PROTECTION TO MAJOR MECHANICAL, ELECTRICAL AND PLUMBING EQUIPMENT AS REQUIRED TO PROVIDE SERVICE ACCESS.
8. WALKWAY PROTECTION IS INDICATED AS A GENERAL LAYOUT AND MAY NOT SHOW ALL FINAL LOCATIONS OF ALL EQUIPMENT.
9. REFERENCE DEMOLITION PLANS, SECTIONS, PATCH AND REPAIR EXISTING ROOFS DAMAGED DURING CONSTRUCTION.
10. ★ INDICATES TIEBACK LOCATION. REFER TO A1.112 COORDINATE WITH MANUFACTURER FOR EMBED SIZE AND LOCATIONS. FINAL EMBED IS SIZED AND DETAILED BY THE STRUCTURAL ENGINEER IN CONJUNCTION WITH EBM DESIGNER.
11. REFER TO SHEET A7.07 FOR EXTERIOR METAL FABRICATION DETAILS.

RESERVE FOR DCA STAMP

HKS
architects

ARCHITECT
HKS, P.C.
1250 (EYE) STREET NW, SUITE 600
WASHINGTON, DC 20005

ASSOCIATE ARCHITECT / INTERIOR DESIGNER
ARRAY
1 WEST ELM STREET, SUITE 500
CONSHOHOCKEN, PA 19048

STRUCTURAL ENGINEER
O'DONNELL & NACCARATO
701 MARKET ST., #600
PHILADELPHIA, PA 19106

MEP-FP / LOW VOLTAGE ENGINEER
BR-A CONSULTING ENGINEERS
2401 WALNUT ST SUITE 701
PHILADELPHIA, PA 19103
HIGHLAND ASSOCIATES
102 HIGHLAND AVE
CLARKS SUMMIT, PA 18411

Cooper University Health Care
COOPER UNIVERSITY HOSPITAL - TOWER A
PROJECT ADDRESS: 1 COOPER PLAZA, CAMDEN, NJ 08103

OWNER
COOPER UNIVERSITY HEALTHCARE
1 COOPER PLAZA
CAMDEN, NJ 08103

PROJECT MANAGER
PURE PM
2026 RICHMOND STREET
PHILADELPHIA, PA 19134

CIVIL ENGINEER / LANDSCAPE
LANGAN
1818 MARKET STREET, SUITE 3300
PHILADELPHIA, PA 19103

SEAL & SIGNATURE

KEY PLAN

REVISION

NO.	DESCRIPTION	DATE
1	BULLETIN #2	01/23/2025
2	BULLETIN #4	04/28/2025
3	RFI 0416	11/14/2025

HKS PROJECT NUMBER
25695.100

DATE
10/15/2024

ISSUE
CORE & SHELL PERMIT SET


SHEET TITLE
CORE & SHELL FLOOR PLAN - LEVEL 05

SHEET NO.
A1.105

BUILDING PERMIT NUMBER: 1111

© HKS, INC.

TITLE BLOCK VERSION: 20210830
MODEL: A:\models\255695.000_Cooper_Miller_Campus_Plan_2023.dwg
PRINT DATE: 1/21/2025 9:26:01 PM
TEMPLATE VERSION: 23.0.3
MICHEL: A:\models\255695.000_Cooper_Miller_Campus_Plan_2023.dwg
PROJECT: CHH Tower A, Exhibit: 2023.rvt

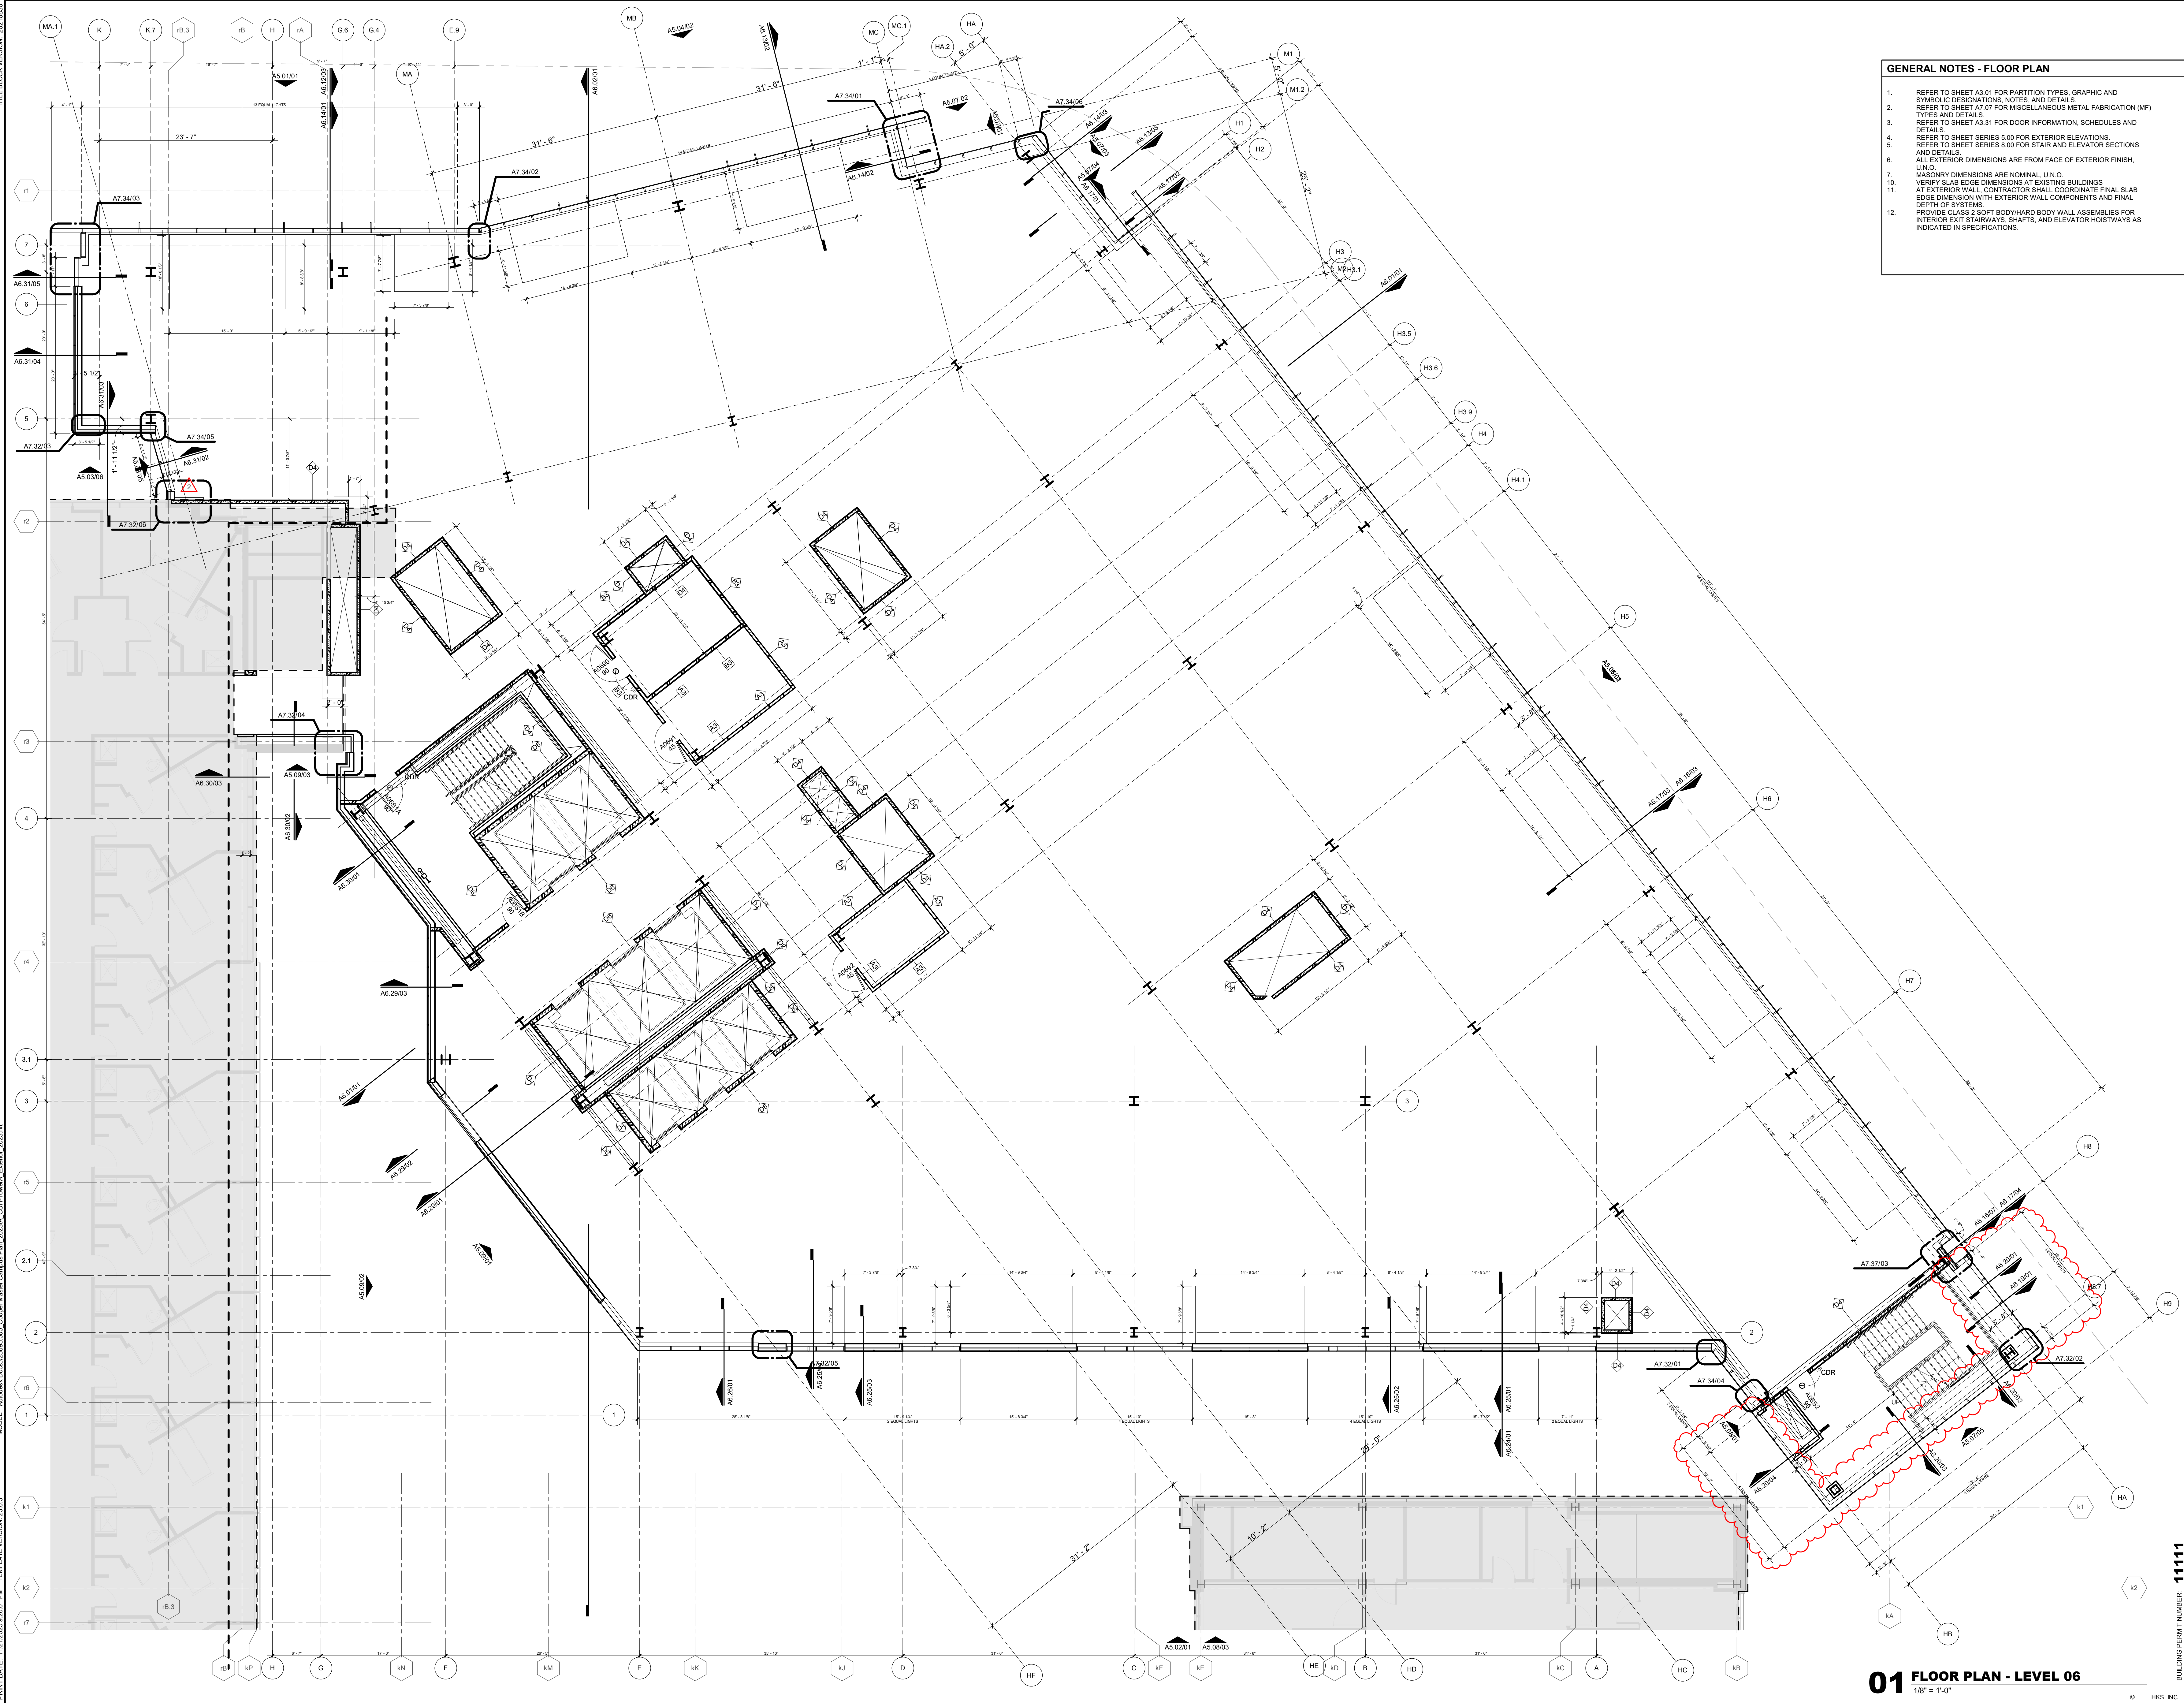

- GENERAL NOTES - FLOOR PLAN**
1. REFER TO SHEET A3.01 FOR PARTITION TYPES, GRAPHIC AND SYMBOLIC DESIGNATIONS, NOTES, AND DETAILS.
 2. REFER TO SHEET A7.07 FOR MISCELLANEOUS METAL FABRICATION (MF) TYPES AND DETAILS.
 3. REFER TO SHEET A3.31 FOR DOOR INFORMATION, SCHEDULES AND DETAILS.
 4. REFER TO SHEET SERIES 5.00 FOR EXTERIOR ELEVATIONS.
 5. REFER TO SHEET SERIES 6.00 FOR STAIR AND ELEVATOR SECTIONS AND DETAILS.
 6. ALL EXTERIOR DIMENSIONS ARE FROM FACE OF EXTERIOR FINISH, U.N.O.
 7. MASONRY DIMENSIONS ARE NOMINAL, U.N.O.
 8. VERIFY SLAB EDGE DIMENSIONS AT EXISTING BUILDINGS.
 9. AT EXTERIOR WALL, CONTRACTOR SHALL COORDINATE FINAL SLAB EDGE DIMENSION WITH EXTERIOR WALL COMPONENTS AND FINAL DEPTH OF SYSTEMS.
 10. PROVIDE CLASS 2 SOFT BODY/MD BODY WALL ASSEMBLIES FOR INTERIOR EXIT STAIRWAYS, SHAFTS, AND ELEVATOR HOISTWAYS AS INDICATED IN SPECIFICATIONS.

RESERVE FOR DCA STAMP



ARCHITECT
HKS, P.C.
1250 I (EYE) STREET NW, SUITE 600
WASHINGTON, DC 20005

ASSOCIATE ARCHITECT / INTERIOR DESIGNER
ARRAY
1 WEST ELM STREET, SUITE 500
CONSHOHOCKEN, PA 19028

STRUCTURAL ENGINEER
O'DONNELL & NACCARATO
701 MARKET ST., #6000
PHILADELPHIA, PA 19106

MEP-FP / LOW VOLTAGE ENGINEER
BR-A CONSULTING ENGINEERS
2401 WALNUT ST SUITE 701
PHILADELPHIA, PA 19103

HIGHLAND ASSOCIATES
102 HIGHLAND AVE
CLARKS SUMMIT, PA 18411




OWNER
COOPER UNIVERSITY HEALTHCARE
1 COOPER PLAZA
CAMDEN, NJ 08103

PROJECT MANAGER
PURE PM
2026 RICHMOND STREET
PHILADELPHIA, PA 19134

CIVIL ENGINEER / LANDSCAPE
LANGAN
1818 MARKET STREET, SUITE 3300
PHILADELPHIA, PA 19103

SEAL & SINGATURE

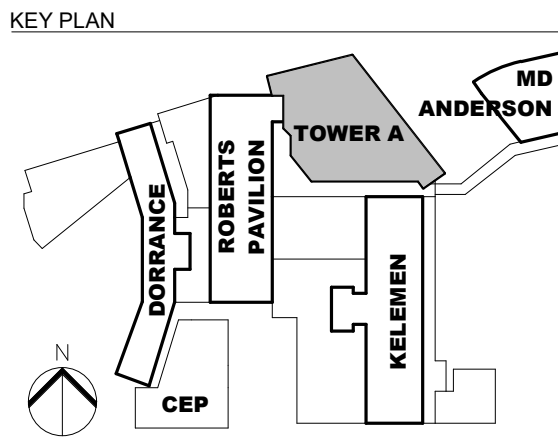

REVISION	DESCRIPTION	DATE
1	BULLETIN #2	01/23/2025
2	BULLETIN #4	04/28/2025
3	RFI 0416	11/14/2025

HKS PROJECT NUMBER
25695.100


DATE
10/15/2024

ISSUE
CORE & SHELL PERMIT SET


SHEET TITLE
CORE & SHELL FLOOR PLAN - LEVEL 06

SHEET NO.
A1.106

TITLE BLOCK: REVISION: 20210830
MODEL: A:\models\255695.000_Cooper_Miller_Campus_Plan_2023.dwg CHIT: Tower A, Exterior, 2023.rvt
PRINT DATE: 1/12/2025 9:25:26 PM TEMPLATE: VERSION: 23.0.3
BUILDING PERMIT NUMBER: 1111

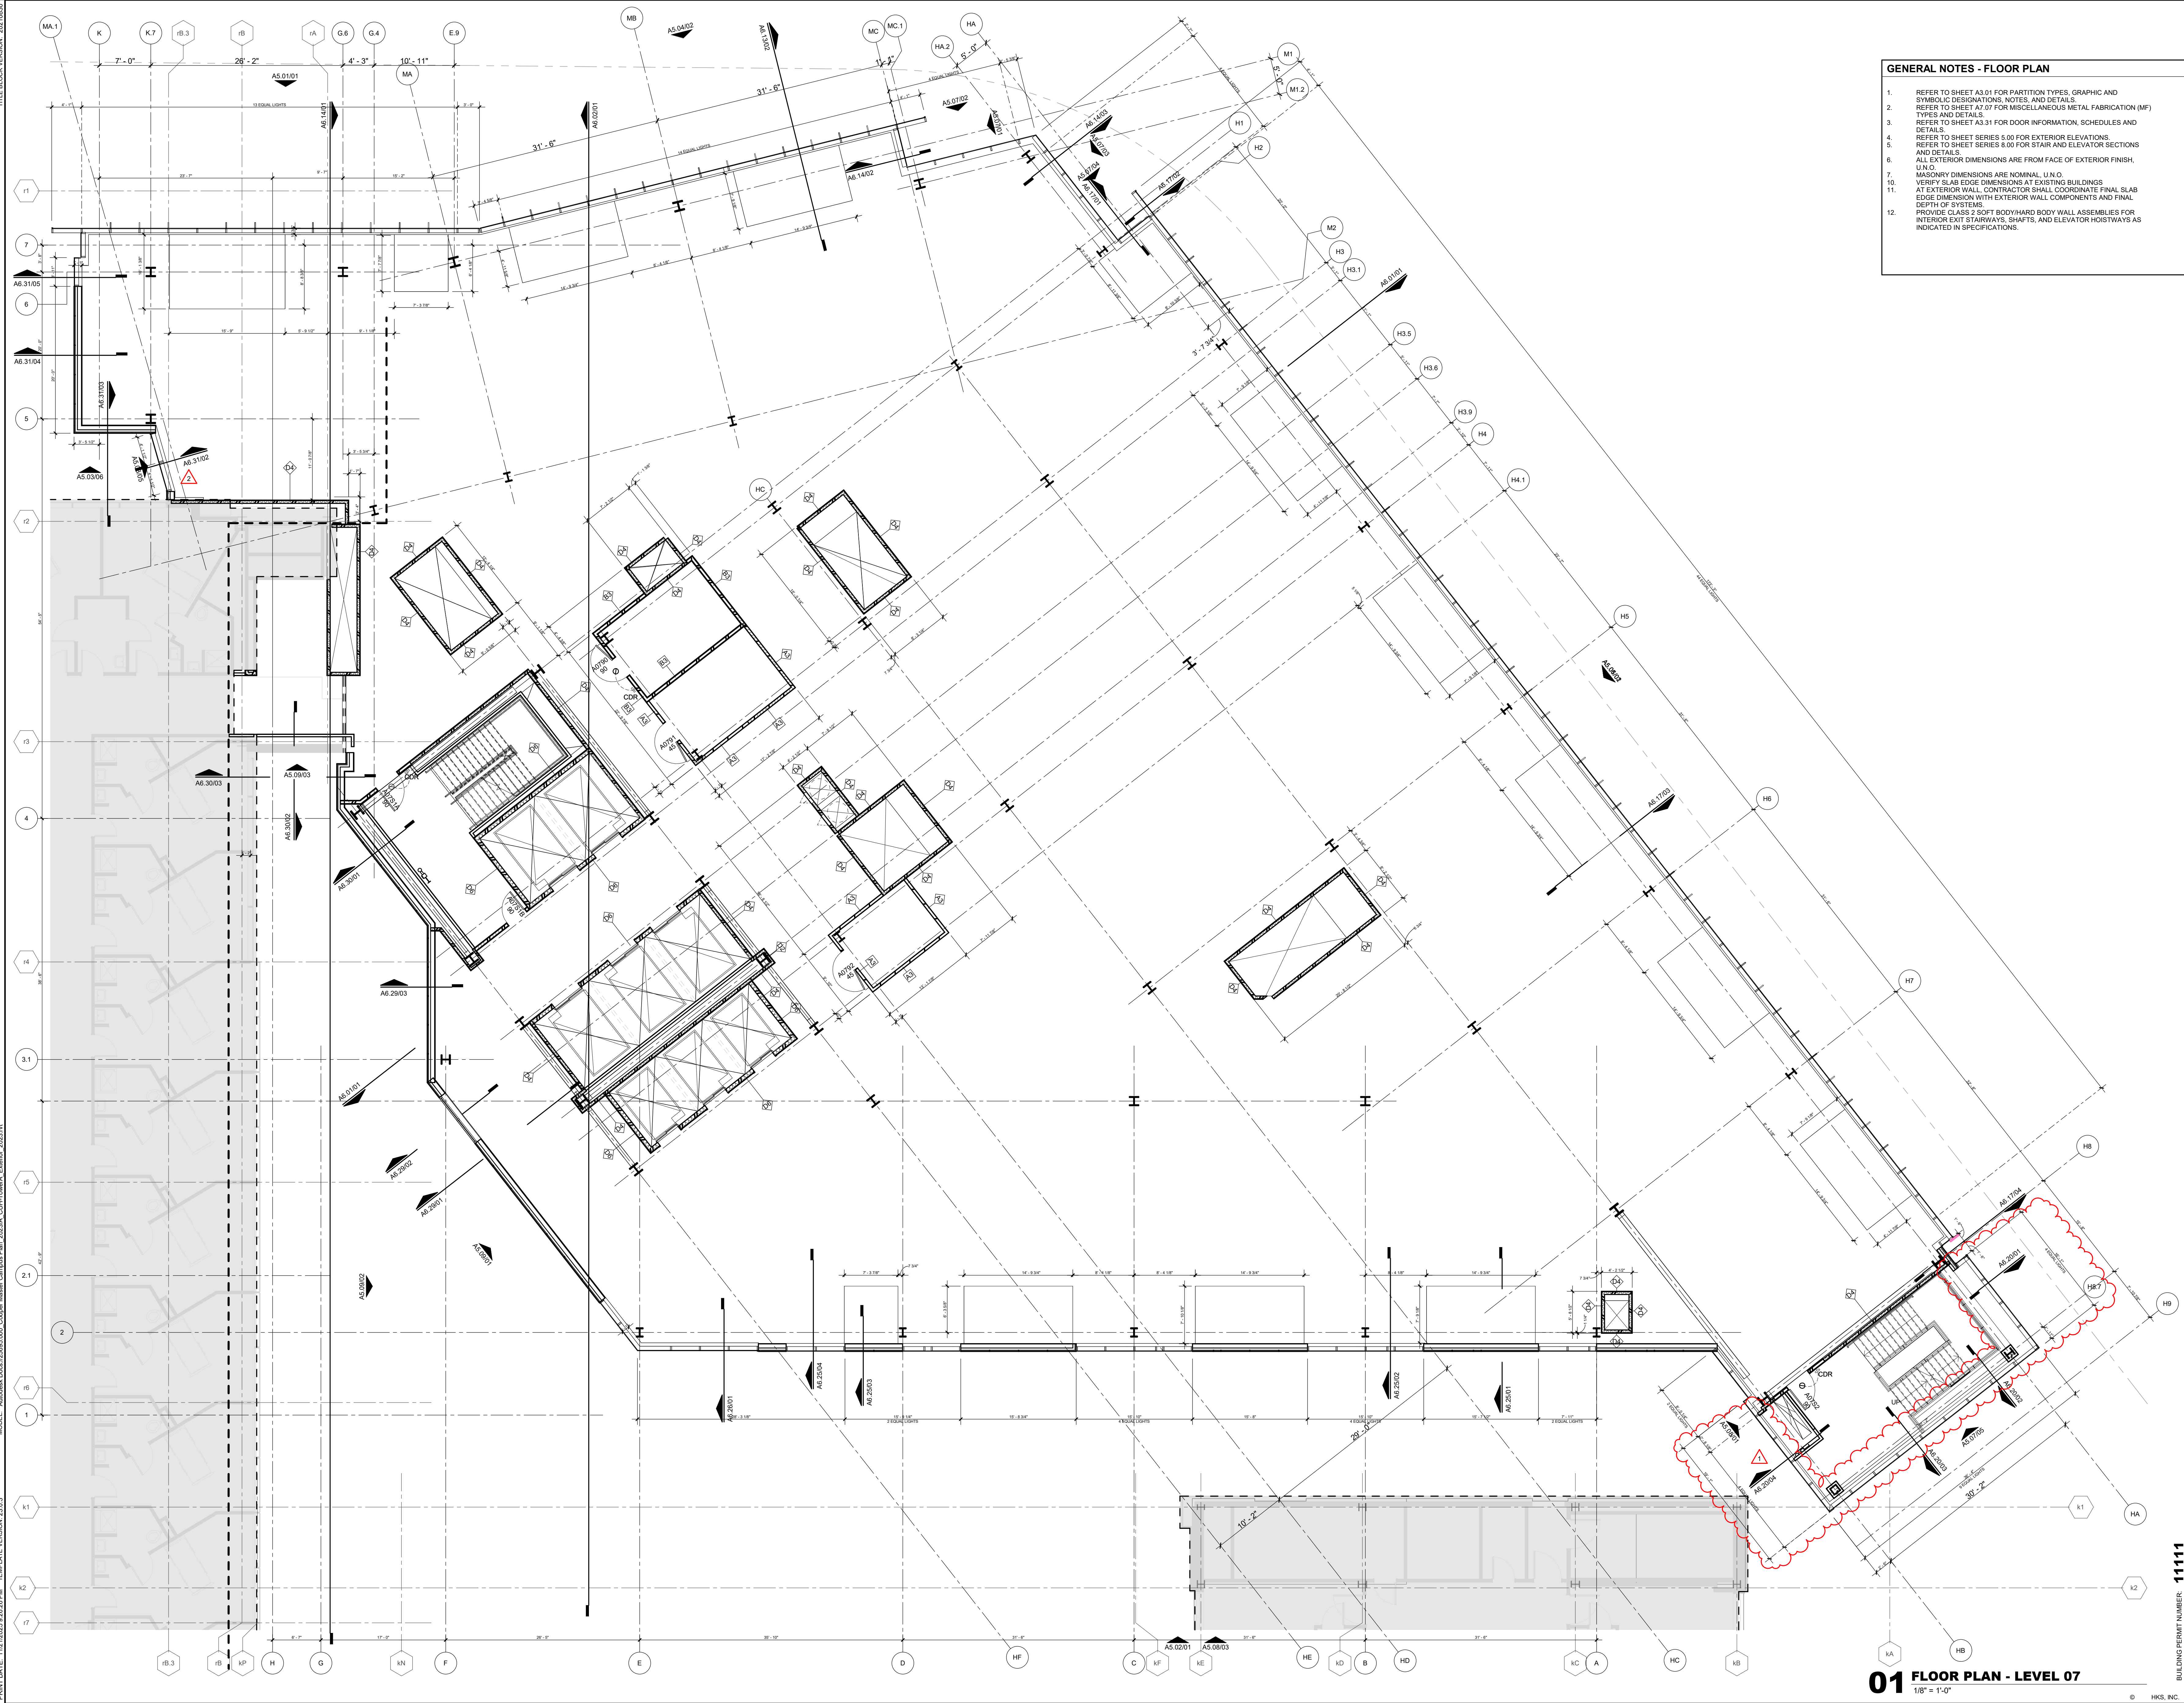

TITLE BLOCK VERSION: 20210830
MODEL: A:\models\25695.000_Cooper_Miller_Campus_Plan_2023.a_Cooper_TowerA_Exterior_2023.rvt
PRINT DATE: 11/21/2025 9:26:46 PM
TEMPLATE VERSION: 23.0.3
HKS, INC.

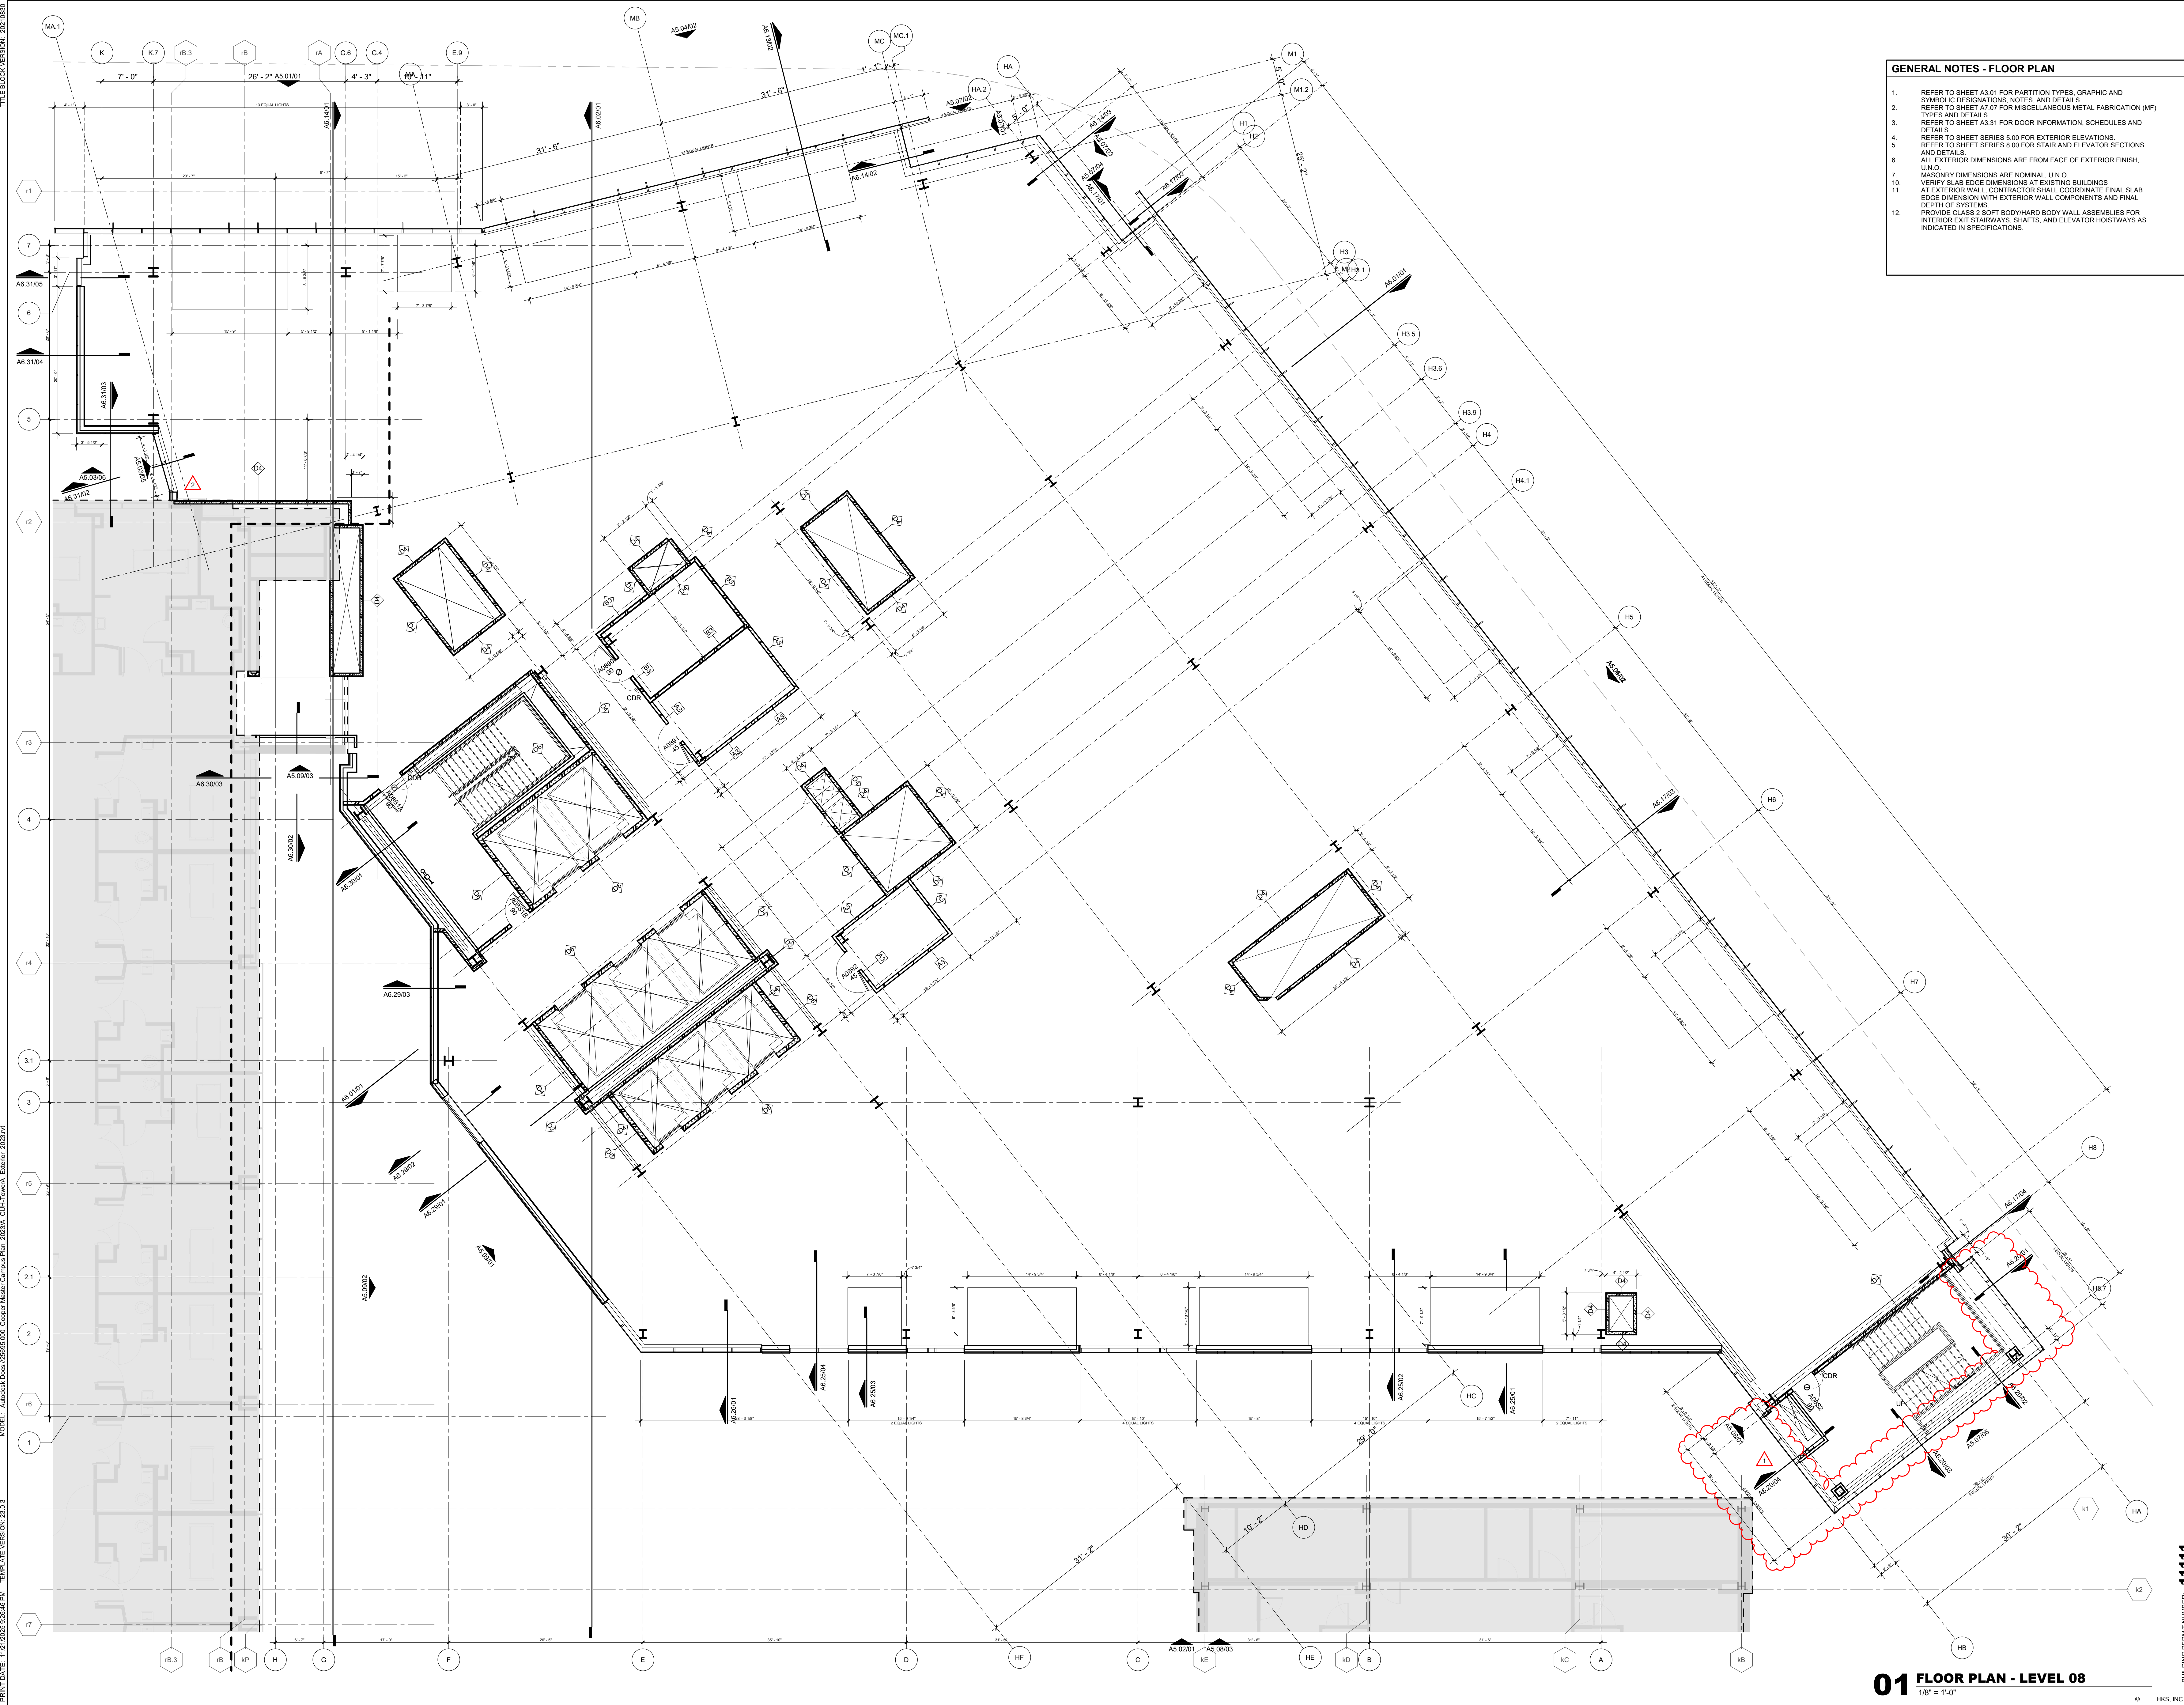

- GENERAL NOTES - FLOOR PLAN**
1. REFER TO SHEET A3.01 FOR PARTITION TYPES, GRAPHIC AND SYMBOLIC DESIGNATIONS, NOTES, AND DETAILS.
 2. REFER TO SHEET A7.07 FOR MISCELLANEOUS METAL FABRICATION (MF) TYPES AND DETAILS.
 3. REFER TO SHEET A3.31 FOR DOOR INFORMATION, SCHEDULES AND DETAILS.
 4. REFER TO SHEET SERIES 5.00 FOR EXTERIOR ELEVATIONS.
 5. REFER TO SHEET SERIES 6.00 FOR STAIR AND ELEVATOR SECTIONS AND DETAILS.
 6. ALL EXTERIOR DIMENSIONS ARE FROM FACE OF EXTERIOR FINISH, U.N.O.
 7. MASONRY DIMENSIONS ARE NOMINAL, U.N.O.
 8. VERIFY SLAB EDGE DIMENSIONS AT EXISTING BUILDINGS.
 9. AT EXTERIOR WALL, CONTRACTOR SHALL COORDINATE FINAL SLAB EDGE DIMENSION WITH EXTERIOR WALL COMPONENTS AND FINAL DEPTH OF SYSTEMS.
 10. PROVIDE CLASS 2 SOFT BODY/AND BODY WALL ASSEMBLIES FOR INTERIOR EXIT STAIRWAYS, SHAFTS, AND ELEVATOR HOISTWAYS AS INDICATED IN SPECIFICATIONS.

RESERVE FOR DCA STAMP

HKS
ARRAY
architects

ARCHITECT
HKS, P.C.
1250 I (EYE) STREET NW, SUITE 600
WASHINGTON, DC 20005

ASSOCIATE ARCHITECT / INTERIOR DESIGNER
ARRAY
1 WEST ELM STREET, SUITE 500
CONSHOHOCKEN, PA 19028

STRUCTURAL ENGINEER
O'DONNELL & NACCARATO
701 MARKET ST., #6000
PHILADELPHIA, PA 19106

MEP-FP / LOW VOLTAGE ENGINEER
BR-A CONSULTING ENGINEERS
2401 WALNUT ST SUITE 701
PHILADELPHIA, PA 19103
HIGHLAND ASSOCIATES
102 HIGHLAND AVE
CLARKS SUMMIT, PA 18411

Cooper
University Health Care

COOPER UNIVERSITY HOSPITAL - TOWER A


PROJECT ADDRESS: 1 COOPER PLAZA, CAMDEN, NJ 08103

OWNER
COOPER UNIVERSITY HEALTHCARE
1 COOPER PLAZA
CAMDEN, NJ 08103

PROJECT MANAGER
PURE PM
2026 RICHMOND STREET
PHILADELPHIA, PA 19134

CIVIL ENGINEER / LANDSCAPE
LANGAN
1818 MARKET STREET, SUITE 3300
PHILADELPHIA, PA 19103

SEAL & SIGNATURE

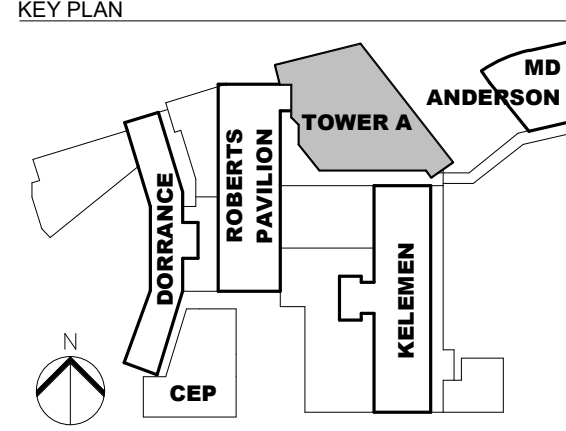

REVISION	DESCRIPTION	DATE
1	BULLETIN #2	01/23/2025
2	BULLETIN #4	04/28/2025
3	RFI 0416	11/14/2025

HKS PROJECT NUMBER
25695.100

DATE
10/15/2024

ISSUE
CORE & SHELL PERMIT SET

SHEET TITLE
CORE & SHELL FLOOR PLAN - LEVEL 08

SHEET NO.
A1.108



1. REFER TO SHEET A3.01 FOR PARTITION TYPES, GRAPHIC AND SYMBOLIC DESIGNATIONS, NOTATIONS, AND DETAILS.
2. REFER TO SHEET A7.07 FOR MISCELLANEOUS METAL FABRICATION TYPES AND DETAILS.
3. REFER TO SHEET A3.31 FOR DOOR INFORMATION, SCHEDULES AND DETAILS.
4. REFER TO SHEET SERIES 5.00 FOR EXTERIOR ELEVATIONS.
5. REFER TO SHEET SERIES 8.00 FOR STAIR AND ELEVATOR SECTIONS AND DETAILS.
6. ALL EXTERIOR DIMENSIONS ARE FROM FACE OF EXTERIOR FINISH, UNLESS NOTED OTHERWISE.
7. MASONRY DIMENSIONS ARE NOMINAL, U.N.O.
8. VERTICAL SLAB EDGE DIMENSIONS AT EXISTING BUILDINGS.
9. AT EXTERIOR WALL, CONTRACTOR SHALL COORDINATE FINAL SLAB EDGE DIMENSION WITH EXTERIOR WALL COMPONENTS AND FINAL FINISH OF SYSTEM.
10. PROVIDE CLASS 2 SFT BODYBOARD BODY WALL ASSEMBLIES FOR INTERIOR EXIST STAIRWAYS, SHAFTS, AND ELEVATOR HOISTWAYS AS NOTED IN SPECIFICATIONS.

RESERVE FOR DCA STAMP



ARCHITECT
HKS, P.C.
12501 (EVE) STREET NW, SUITE 600
WASHINGTON, DC 20005

**ASSOCIATE ARCHITECT
INTERIOR DESIGNER**
ARRAY
1 WEST ELM STREET, SUITE 500
CONSHOHOCKEN, PA 19428

STRUCTURAL ENGINEER
O'DONNELL & NACCARATO
701 MARKET ST, #6000
PHILADELPHIA, PA 19106

**MEP-FP / LOW VOLTAGE
ENGINEER**
BRA+A CONSULTING ENGINEERS
2041 WALNUT ST SUITE 701
PHILADELPHIA, PA 19103
HIGHLAND ASSOCIATES
102 HIGHLAND AVE
CLARK SUMMIT, PA 18411




OWNER
COOPER UNIVERSITY HEALTHCARE
1 COOPER PLAZA
CAMDEN, NJ 08103

PROJECT MANAGER
PURE PM
2926 RICHMOND STREET
PHILADELPHIA, PA 19134

CIVIL ENGINEER / LANDSCAPE
LANGAN
1818 MARKET STREET, SUITE 3300
PHILADELPHIA, PA 19103

SEAL & SINGATURE

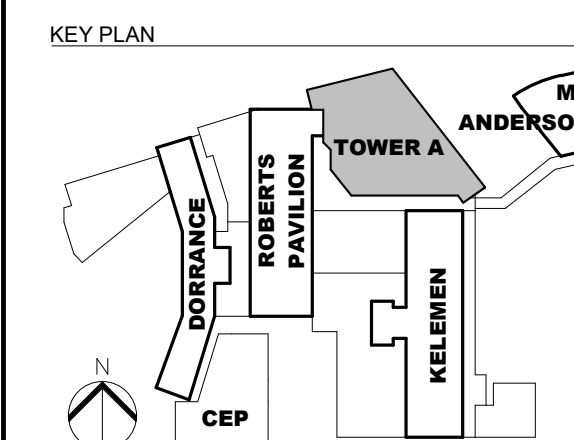

REVISION		
NO.	DESCRIPTION	DATE
1	BULLETIN #2	01/23/20
2	BULLETIN #4	04/28/20
3	RFI 0416	11/14/20

HKS PROJECT NUMBER
25695.100

DATE
10/15/2024


ISSUE
CORE & SHELL PERMIT SET

SHEET TITLE
CORE & SHELL FLOOR PLAN - LEVEL 09

SHEET NO.

A1.109

TITLE BLOCK: REVISION: 20210830
MODEL: Autodesk Docs 25695.000 Cooper Medical Campus Plan 2023.a CHH Tower A, Exterior 2023.rvt
PRINT DATE: 1/12/2025 9:27:29 PM TEMPLATE VERSION: 23.3.3
BUILDING PERMIT NUMBER: 1111 HKS, INC.

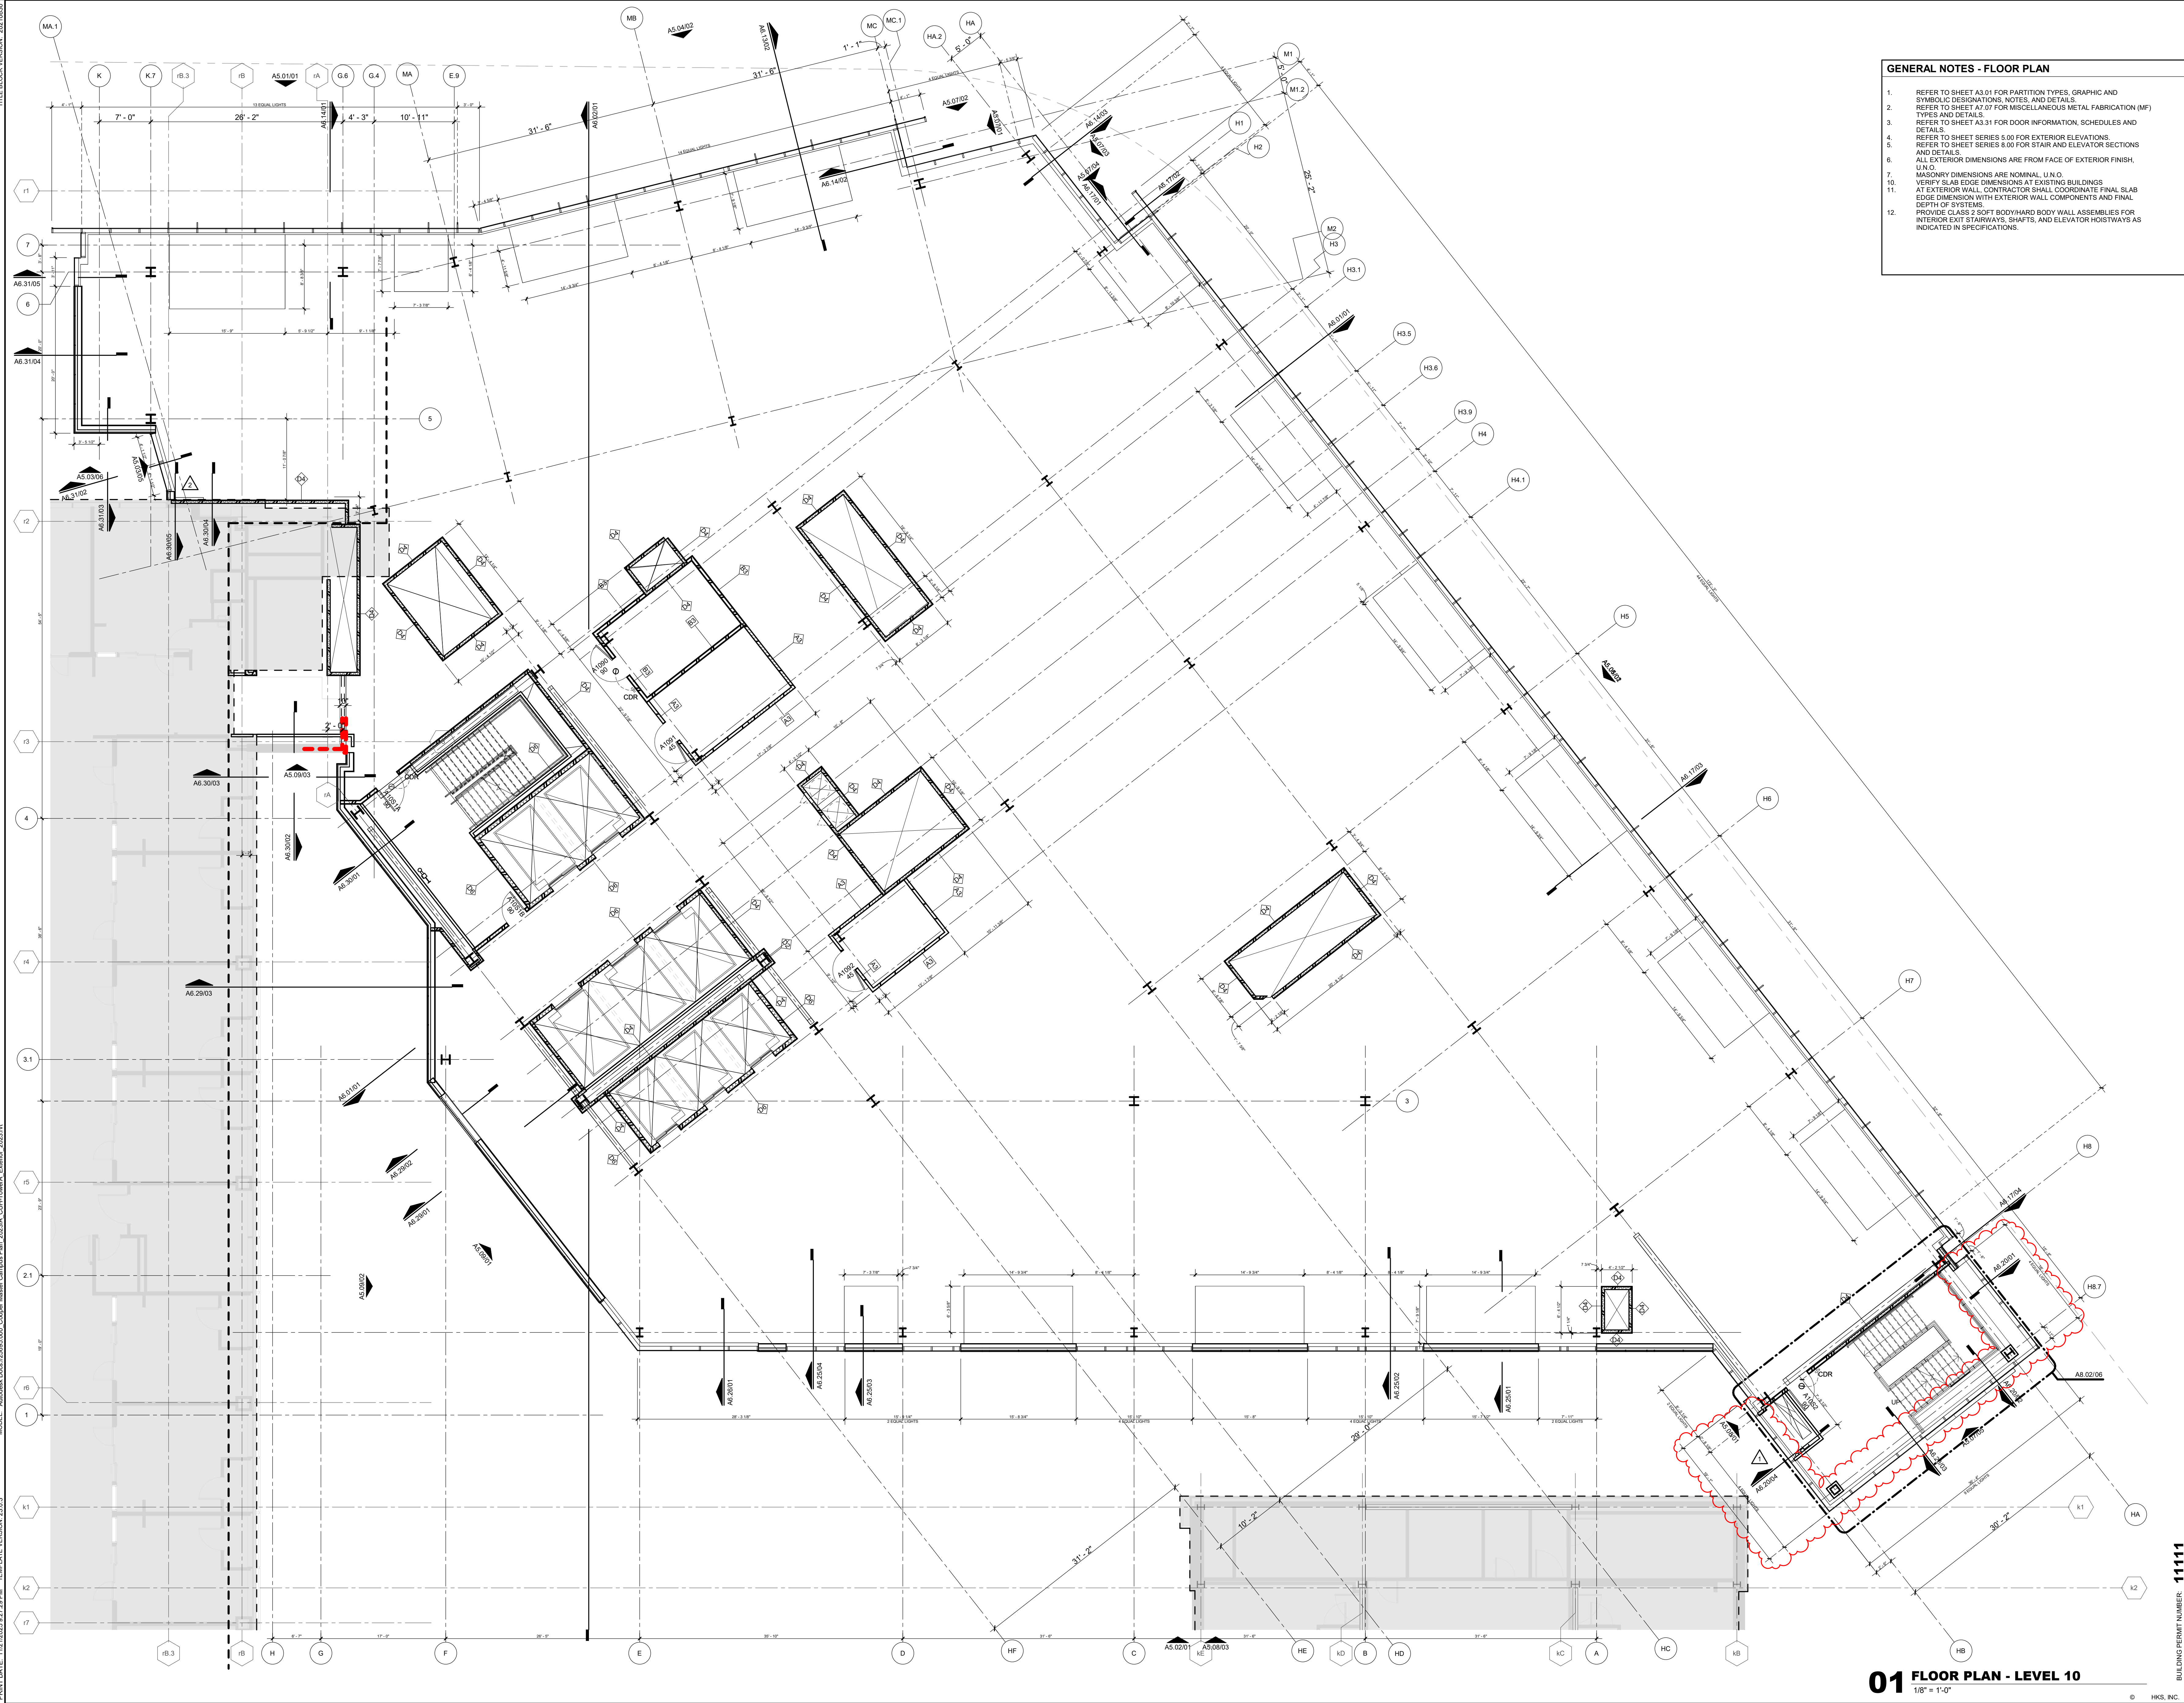

- GENERAL NOTES - FLOOR PLAN**
1. REFER TO SHEET A3.01 FOR PARTITION TYPES, GRAPHIC AND SYMBOLIC DESIGNATIONS, NOTES, AND DETAILS.
 2. REFER TO SHEET A7.07 FOR MISCELLANEOUS METAL FABRICATION (MF) TYPES AND DETAILS.
 3. REFER TO SHEET A3.31 FOR DOOR INFORMATION, SCHEDULES AND DETAILS.
 4. REFER TO SHEET SERIES 5.00 FOR EXTERIOR ELEVATIONS.
 5. REFER TO SHEET SERIES 6.00 FOR STAIR AND ELEVATOR SECTIONS AND DETAILS.
 6. ALL EXTERIOR DIMENSIONS ARE FROM FACE OF EXTERIOR FINISH, U.N.O.
 7. MASONRY DIMENSIONS ARE NOMINAL, U.N.O.
 8. VERIFY SLAB EDGE DIMENSIONS AT EXISTING BUILDINGS.
 9. AT EXTERIOR WALL, CONTRACTOR SHALL COORDINATE FINAL SLAB EDGE DIMENSION WITH EXTERIOR WALL COMPONENTS AND FINAL DEPTH OF SYSTEMS.
 10. PROVIDE CLASS 2 SOFT BODY/MD BODY WALL ASSEMBLIES FOR INTERIOR EXIT STAIRWAYS, SHAFTS, AND ELEVATOR HOISTWAYS AS INDICATED IN SPECIFICATIONS.

RESERVE FOR DCA STAMP

HKS
ARRAY
architects

ARCHITECT
HKS, P.C.
1250 I (EYE) STREET NW, SUITE 600
WASHINGTON, DC 20005

ASSOCIATE ARCHITECT / INTERIOR DESIGNER
ARRAY
1 WEST ELM STREET, SUITE 500
CONSHOHOCKEN, PA 19028

STRUCTURAL ENGINEER
O'DONNELL & NACCARATO
701 MARKET ST., #6000
PHILADELPHIA, PA 19106

MEP-FP / LOW VOLTAGE ENGINEER
BR-A CONSULTING ENGINEERS
2401 WALNUT ST SUITE 701
PHILADELPHIA, PA 19103
HIGHLAND ASSOCIATES
102 HIGHLAND AVE
CLARKS SUMMIT, PA 18411

Cooper
University Health Care
COOPER UNIVERSITY HOSPITAL - TOWER A
PROJECT ADDRESS: 1 COOPER PLAZA, CAMDEN, NJ 08103

OWNER
COOPER UNIVERSITY HEALTHCARE
1 COOPER PLAZA
CAMDEN, NJ 08103

PROJECT MANAGER
PURE PM
2026 RICHMOND STREET
PHILADELPHIA, PA 19134

CIVIL ENGINEER / LANDSCAPE
LANGAN
1818 MARKET STREET, SUITE 3300
PHILADELPHIA, PA 19103
SEAL & SINGATURE


KEY PLAN

REVISION

NO.	DESCRIPTION	DATE
1	BULLETIN #2	01/23/2025
2	BULLETIN #4	04/28/2025
3	RFI 0416	11/14/2025

HKS PROJECT NUMBER
25695.100
DATE
10/15/2024
ISSUE
CORE & SHELL PERMIT SET
SHEET TITLE
CORE & SHELL FLOOR PLAN - LEVEL 10
SHEET NO.
A1.110

TITLE BLOCK VERSION: 20210830
MODEL: A:\models\25695\002_Cooper_Mater_Campus_Plan_2023\A_Cooper_TowerA_Elevs.dwg
PRINT DATE: 11/15/2025 9:28:00 PM
TEMPLATE VERSION: 23.0.3

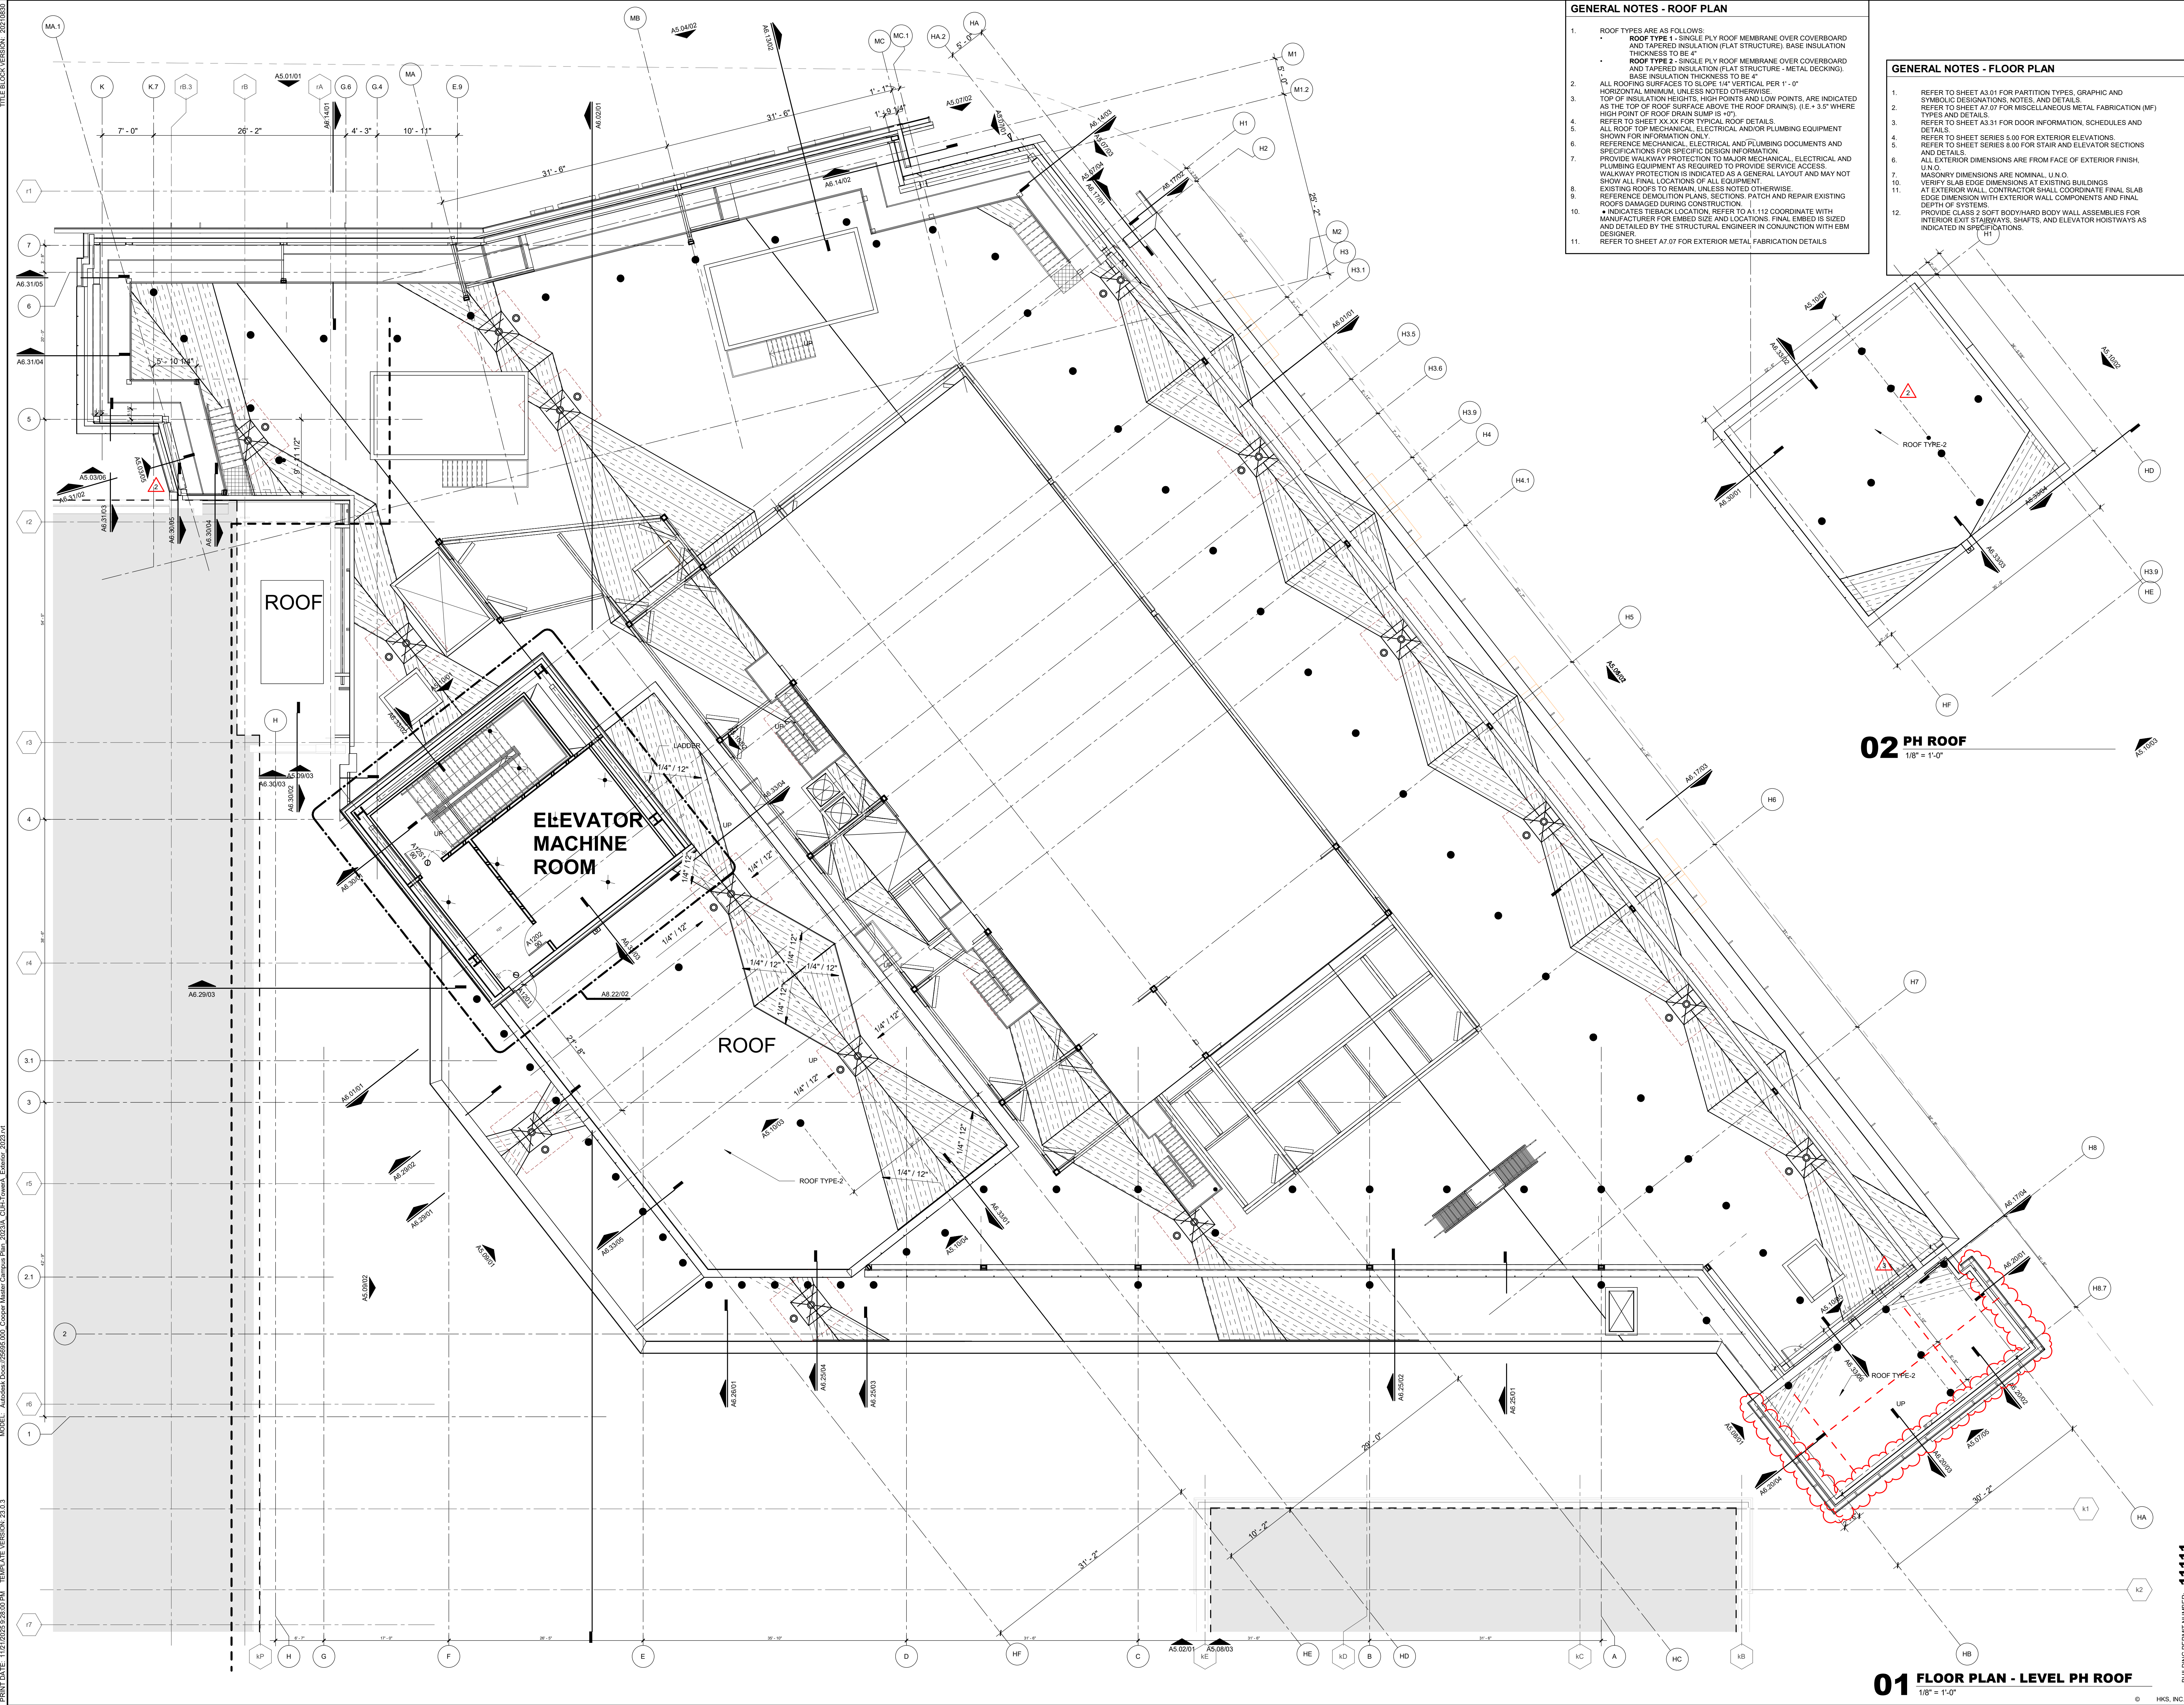

RESERVE FOR DCA STAMP

HKS

ARRAY
architects

ARCHITECT
HKS, P.C.
1250 I (EYE) STREET NW, SUITE 600
WASHINGTON, DC 20005
ASSOCIATE ARCHITECT / INTERIOR DESIGNER
ARRAY
1 WEST ELM STREET, SUITE 500
CONSHOHOCKEN, PA 19028
STRUCTURAL ENGINEER
O'DONNELL & NACCARATO
701 MARKET ST., #6000
PHILADELPHIA, PA 19106
MEP-FP / LOW VOLTAGE ENGINEER
BR+A CONSULTING ENGINEERS
2401 WALNUT ST. SUITE 701
PHILADELPHIA, PA 19103
HIGHLAND ASSOCIATES
102 HIGHLAND AVE
CLARKS SUMMIT, PA 18411

Cooper
University Health Care

COOPER UNIVERSITY HOSPITAL - TOWER A

PROJECT ADDRESS: 1 COOPER PLAZA, CAMDEN, NJ 08103

OWNER
COOPER UNIVERSITY HEALTHCARE
1 COOPER PLAZA
CAMDEN, NJ 08103
PROJECT MANAGER
PURE PM
2026 RICHMOND STREET
PHILADELPHIA, PA 19134
CIVIL ENGINEER / LANDSCAPE
LANGAN
1818 MARKET STREET, SUITE 3300
PHILADELPHIA, PA 19103
SEAL & SINGATURE

KEY PLAN

REVISION


NO.	DESCRIPTION	DATE
1	BULLETIN #2	01/23/2025
2	BULLETIN #4	04/28/2025
3	RFI #255-01	06/18/2025
4	RFI 0320	08/14/2025
5	RFI 0416	11/14/2025

HKS PROJECT NUMBER
25695.100
DATE
10/15/2024
ISSUE
CORE & SHELL PERMIT SET
SHEET TITLE
CORE & SHELL FLOOR PLAN - LEVEL PH ROOF
SHEET NO.
A1.112

BUILDING PERMIT NUMBER: 1111



TITLE BLOCK VERSION: 20210830
MODEL: A:\models\Draw\25695.000_Cooper_Miller_Campus_Plan_2023\A_Cooper_Tower_A_Exterior_2023.rvt
PRINT DATE: 1/21/2025 9:28:12 PM
TEMPLATE VERSION: 23.0.3
© HKS, INC.

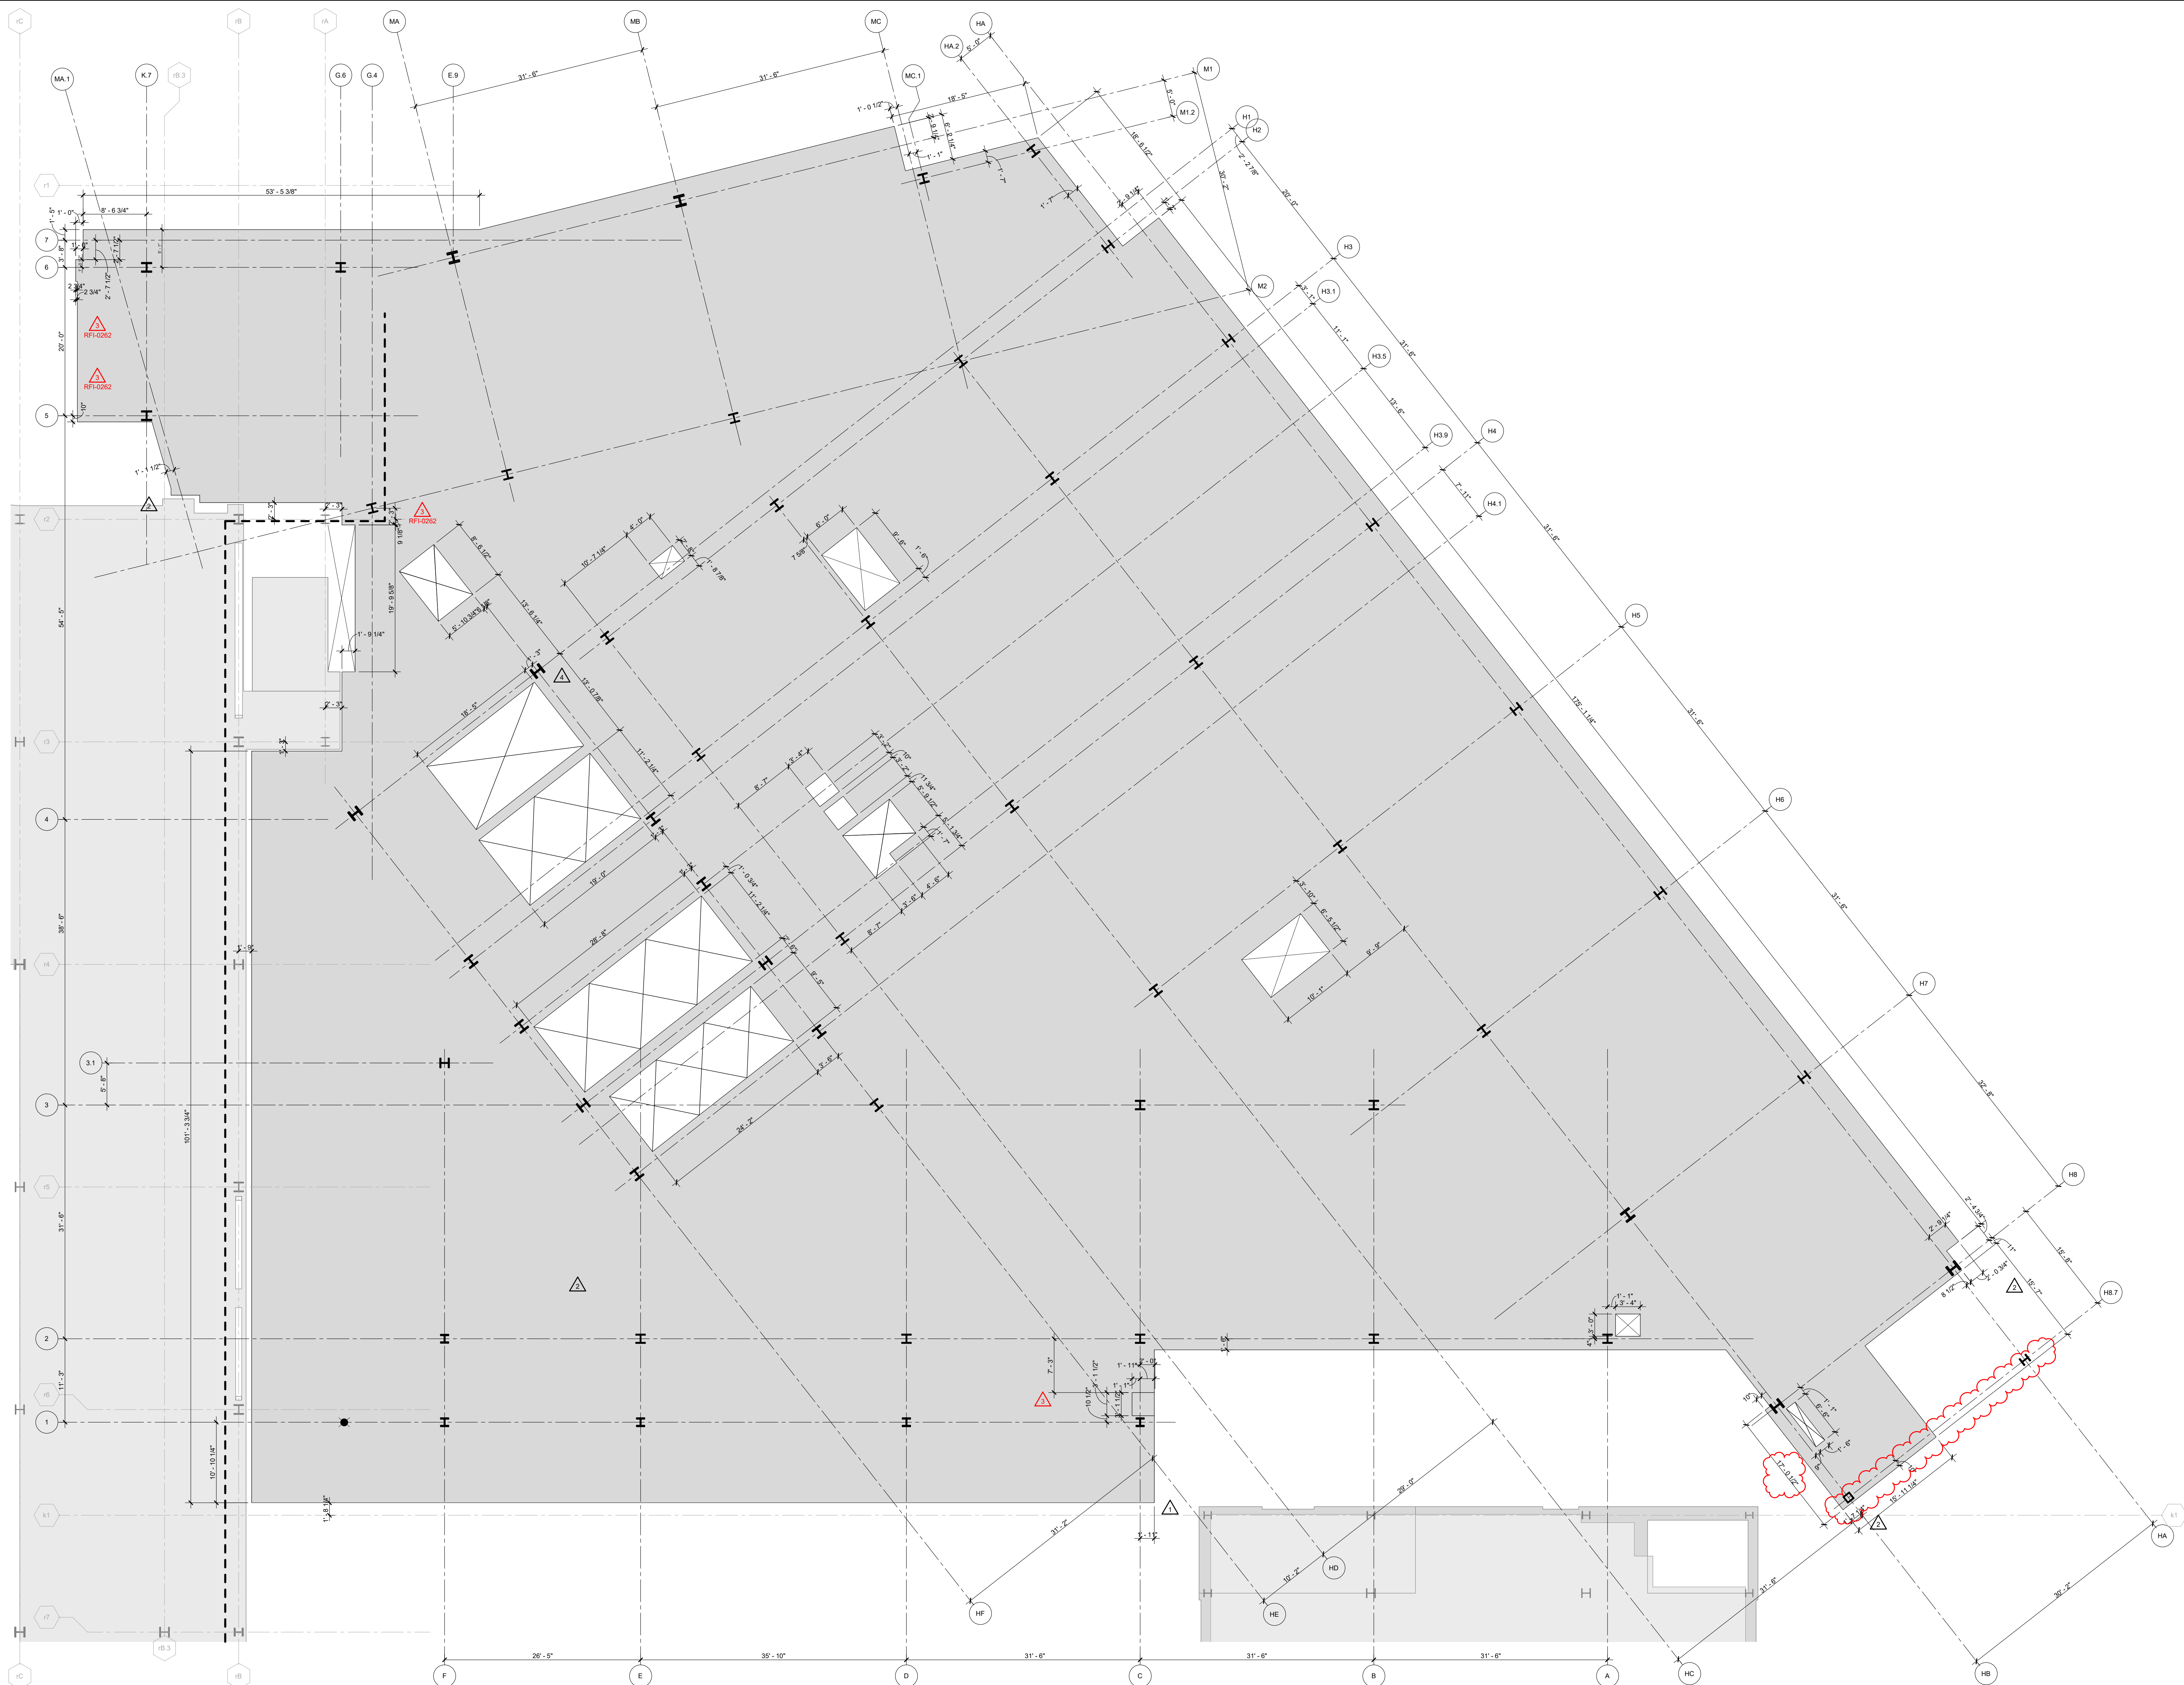


RESERVE FOR DCA STAMP



ARCHITECT
HKS, P.C.
1250 I (EYE) STREET NW, SUITE 600
WASHINGTON, DC 20005
ASSOCIATE ARCHITECT / INTERIOR DESIGNER
ARRAY
1 WEST ELM STREET, SUITE 500
CONSHOHOCKEN, PA 19428
STRUCTURAL ENGINEER
O'DONNELL & NACCARATO
701 MARKET ST., #6000
PHILADELPHIA, PA 19106
MEP-FP / LOW VOLTAGE ENGINEER
BR-A CONSULTING ENGINEERS
2401 WALNUT ST SUITE 701
PHILADELPHIA, PA 19103
HIGHLAND ASSOCIATES
102 HIGHLAND AVE
CLARKS SUMMIT, PA 18411



OWNER
COOPER UNIVERSITY HEALTHCARE
1 COOPER PLAZA
CAMDEN, NJ 08103
PROJECT MANAGER
PURE PM
2026 RICHMOND STREET
PHILADELPHIA, PA 19134
CIVIL ENGINEER / LANDSCAPE
LANGAN
1818 MARKET STREET, SUITE 3300
PHILADELPHIA, PA 19103
SEAL & SIGNATURE

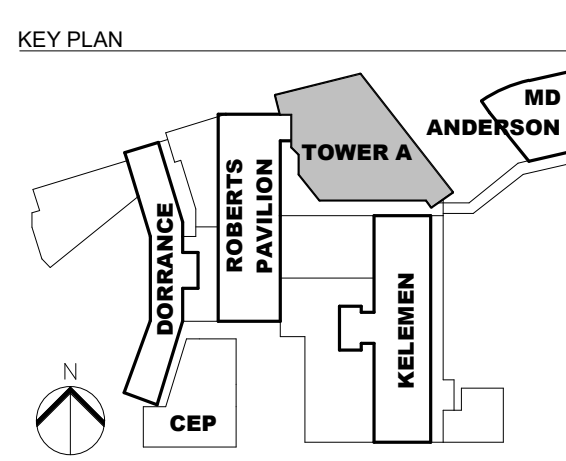

NO.	DESCRIPTION	DATE
1	BULLETIN #2	01/23/2025
2	BULLETIN #4	04/28/2025
3	BULLETIN #5	07/11/2025
4	RFI 0343	09/08/2025
5	RFI 0416	11/14/2025


HKS PROJECT NUMBER
25695.100
DATE
10/15/2024
ISSUE
CORE & SHELL PERMIT SET
SHEET TITLE
EDGE OF SLAB PLAN - LEVEL 04

SHEET NO.
A1.204

TITLE BLOCK VERSION: 20210830

MODEL: A:\models\25695.000_Cooper_Miller_Campus_Plan_2023.dwg CHAT: Tower A, Exterior, 2023.rvt

PRINT DATE: 11/21/2025 9:28:18 PM TEMPLATE VERSION: 23.0.3

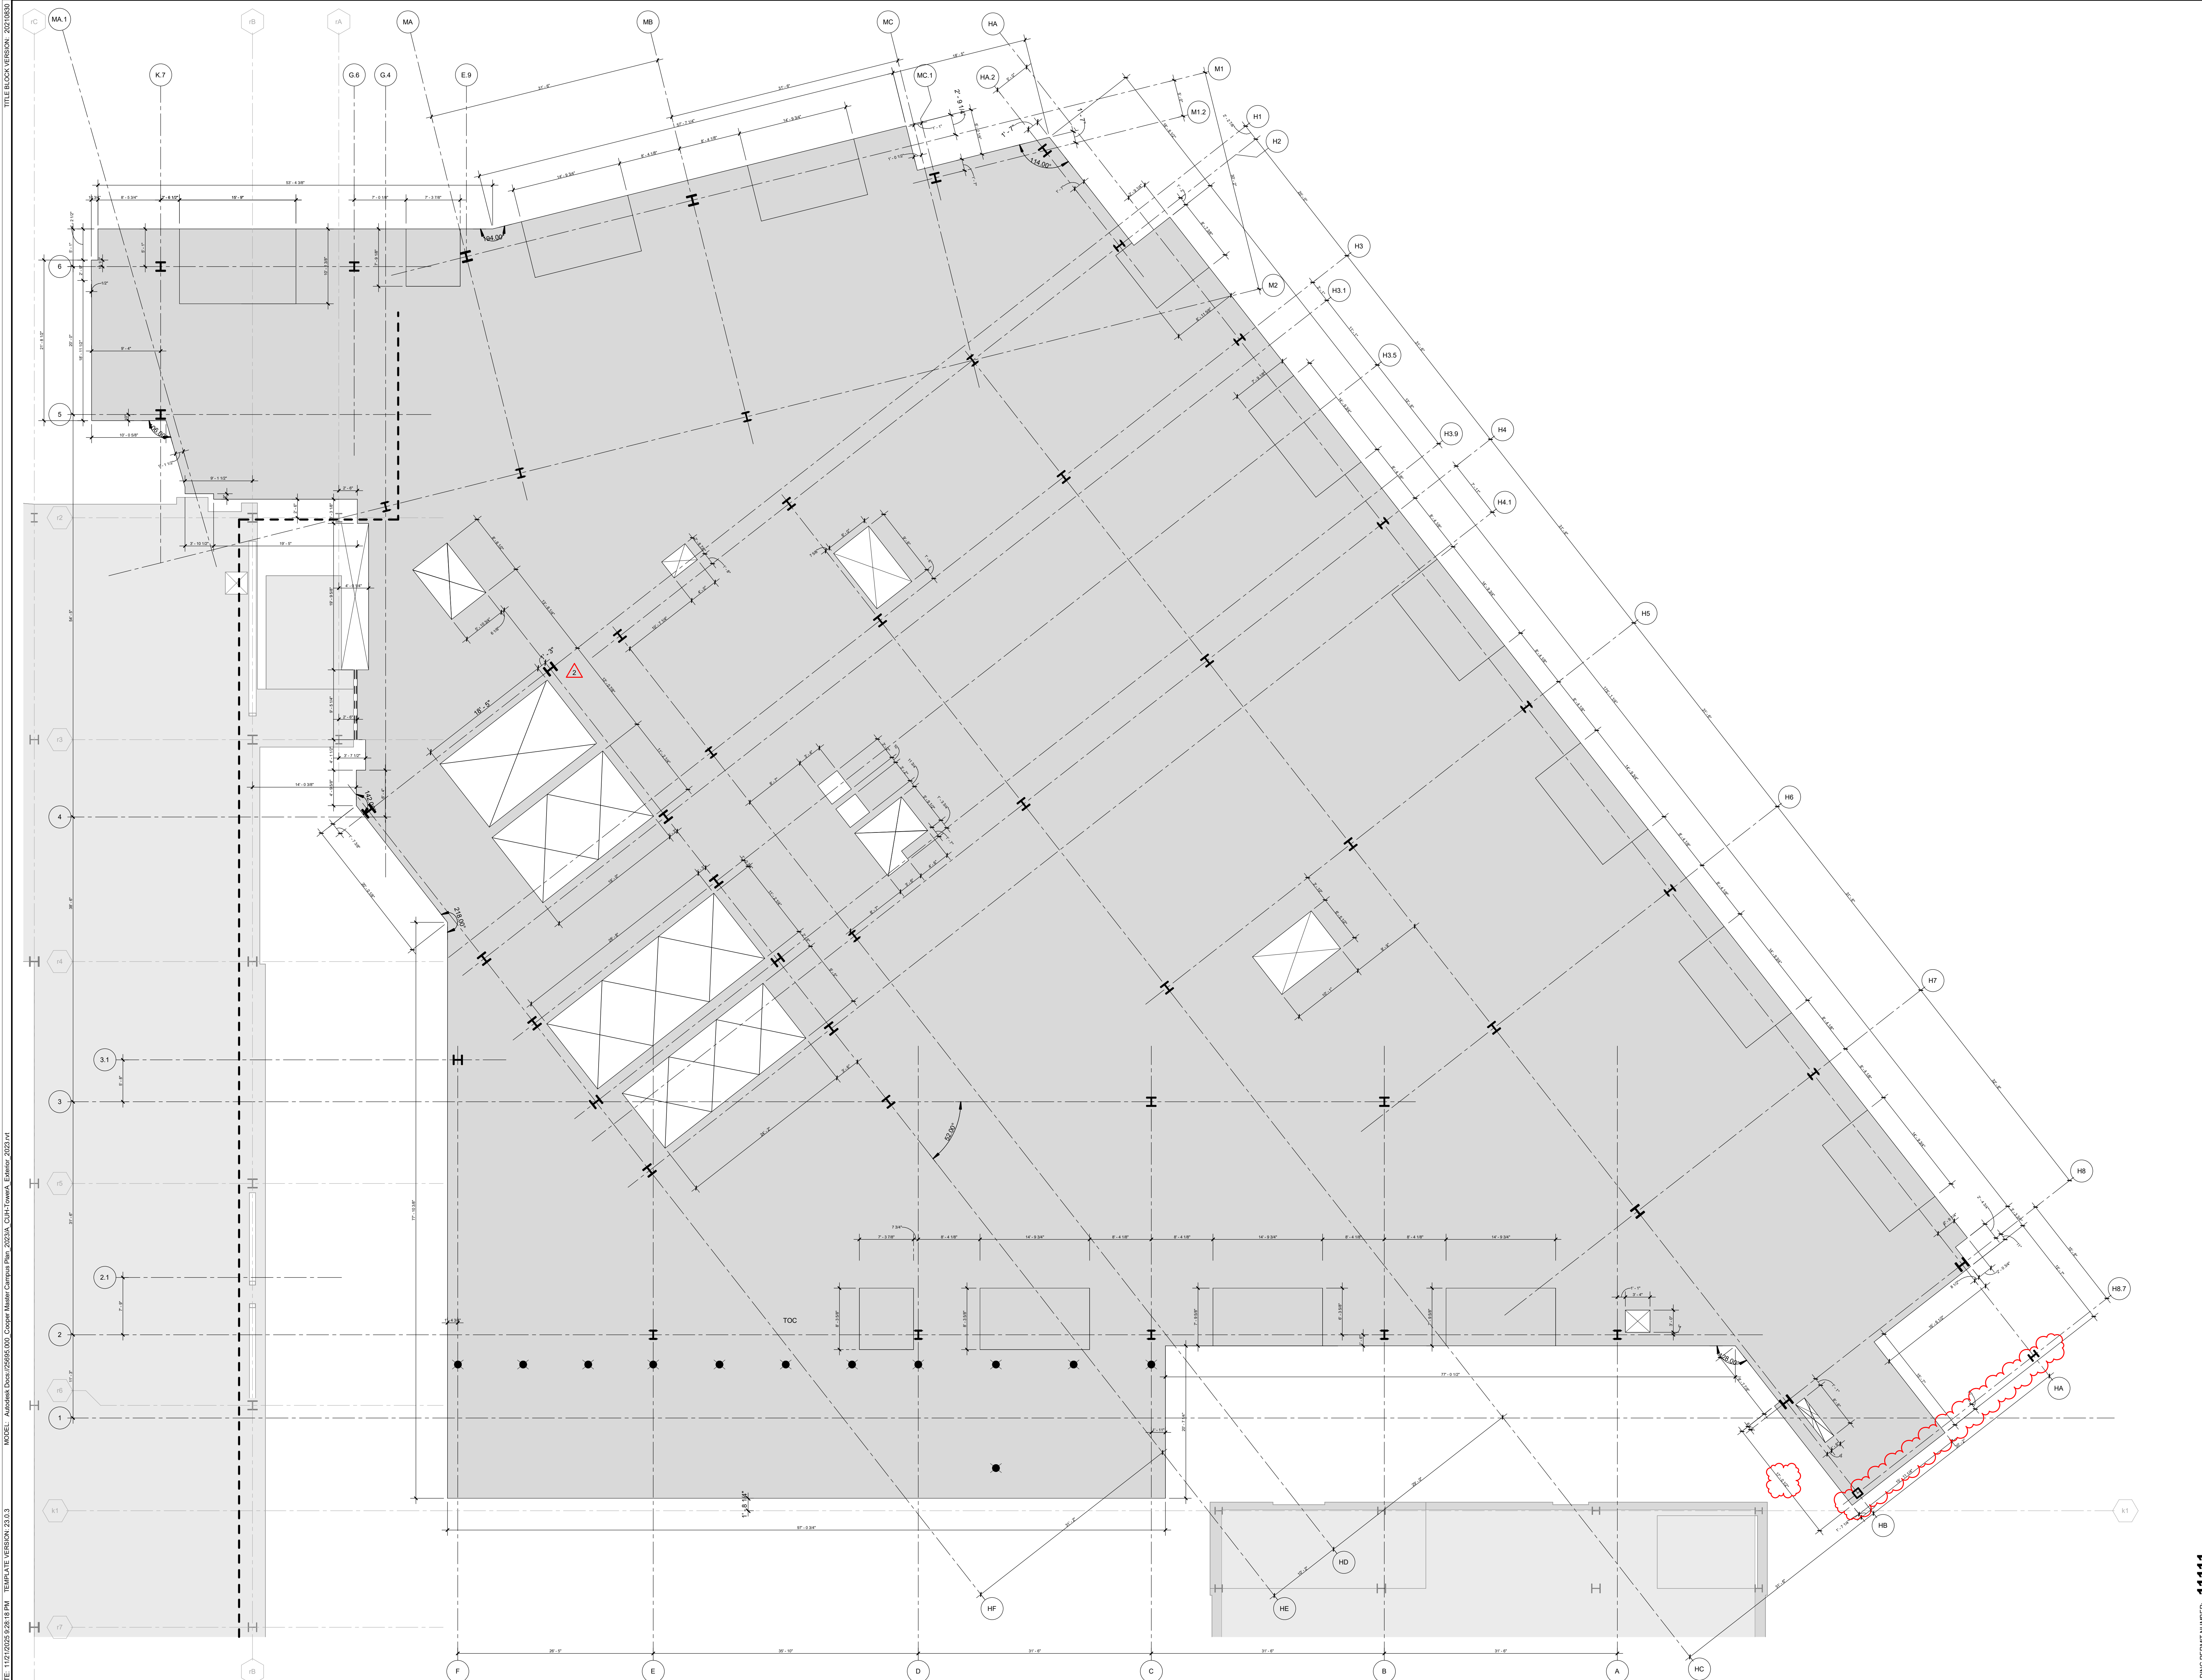

RESERVE FOR DCA STAMP




ARCHITECT
HKS, P.C.
1250 I (EYE) STREET NW, SUITE 600
WASHINGTON, DC 20005
ASSOCIATE ARCHITECT / INTERIOR DESIGNER
ARRAY
1 WEST ELM STREET, SUITE 500
CONSHOHOCKEN, PA 19428
STRUCTURAL ENGINEER
O'DONNELL & NACCARATO
701 MARKET ST., #6000
PHILADELPHIA, PA 19106
MEP-FP / LOW VOLTAGE ENGINEER
BR-A CONSULTING ENGINEERS
2401 WALNUT ST SUITE 701
PHILADELPHIA, PA 19103
HIGHLAND ASSOCIATES
102 HIGHLAND AVE
CLARKS SUMMIT, PA 18411



OWNER
COOPER UNIVERSITY HEALTHCARE
1 COOPER PLAZA
CAMDEN, NJ 08103
PROJECT MANAGER
PURE PM
2026 RICHMOND STREET
PHILADELPHIA, PA 19134
CIVIL ENGINEER / LANDSCAPE
LANGAN
1818 MARKET STREET, SUITE 3300
PHILADELPHIA, PA 19103
SEAL & SIGNATURE

KEY PLAN

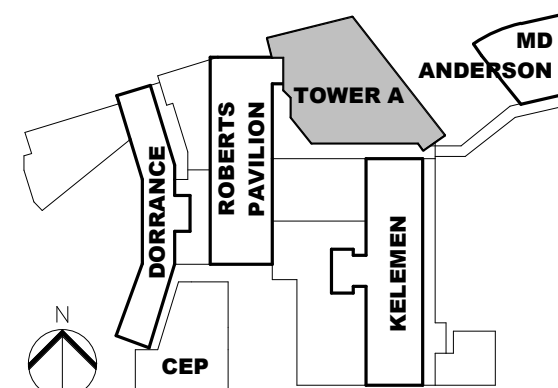

REVISION	NO.	DESCRIPTION	DATE
1	BULLETIN #4		04/28/2025
2	RFI 0343		08/08/2025
3	RFI XXX		10/16/2025
4	RFI 0416		11/14/2025

HKS PROJECT NUMBER
25695.100
DATE
10/15/2024

ISSUE
CORE & SHELL PERMIT SET
SHEET TITLE
EDGE OF SLAB PLAN - LEVEL 05

SHEET NO.


A1.205

BUILDING PERMIT NUMBER: 1111

01 EOS PLAN - LEVEL 05
1/8" = 1'-0"

HKS, INC.

TITLE BLOCK VERSION: 20210830
MODEL: A:\models\25695.100_Cooper_Miller_Campus_Plan_2023.dwg
PRINT DATE: 1/12/2025 9:29:25 PM
TEMPLATE VERSION: 23.0.3
HKS, INC.

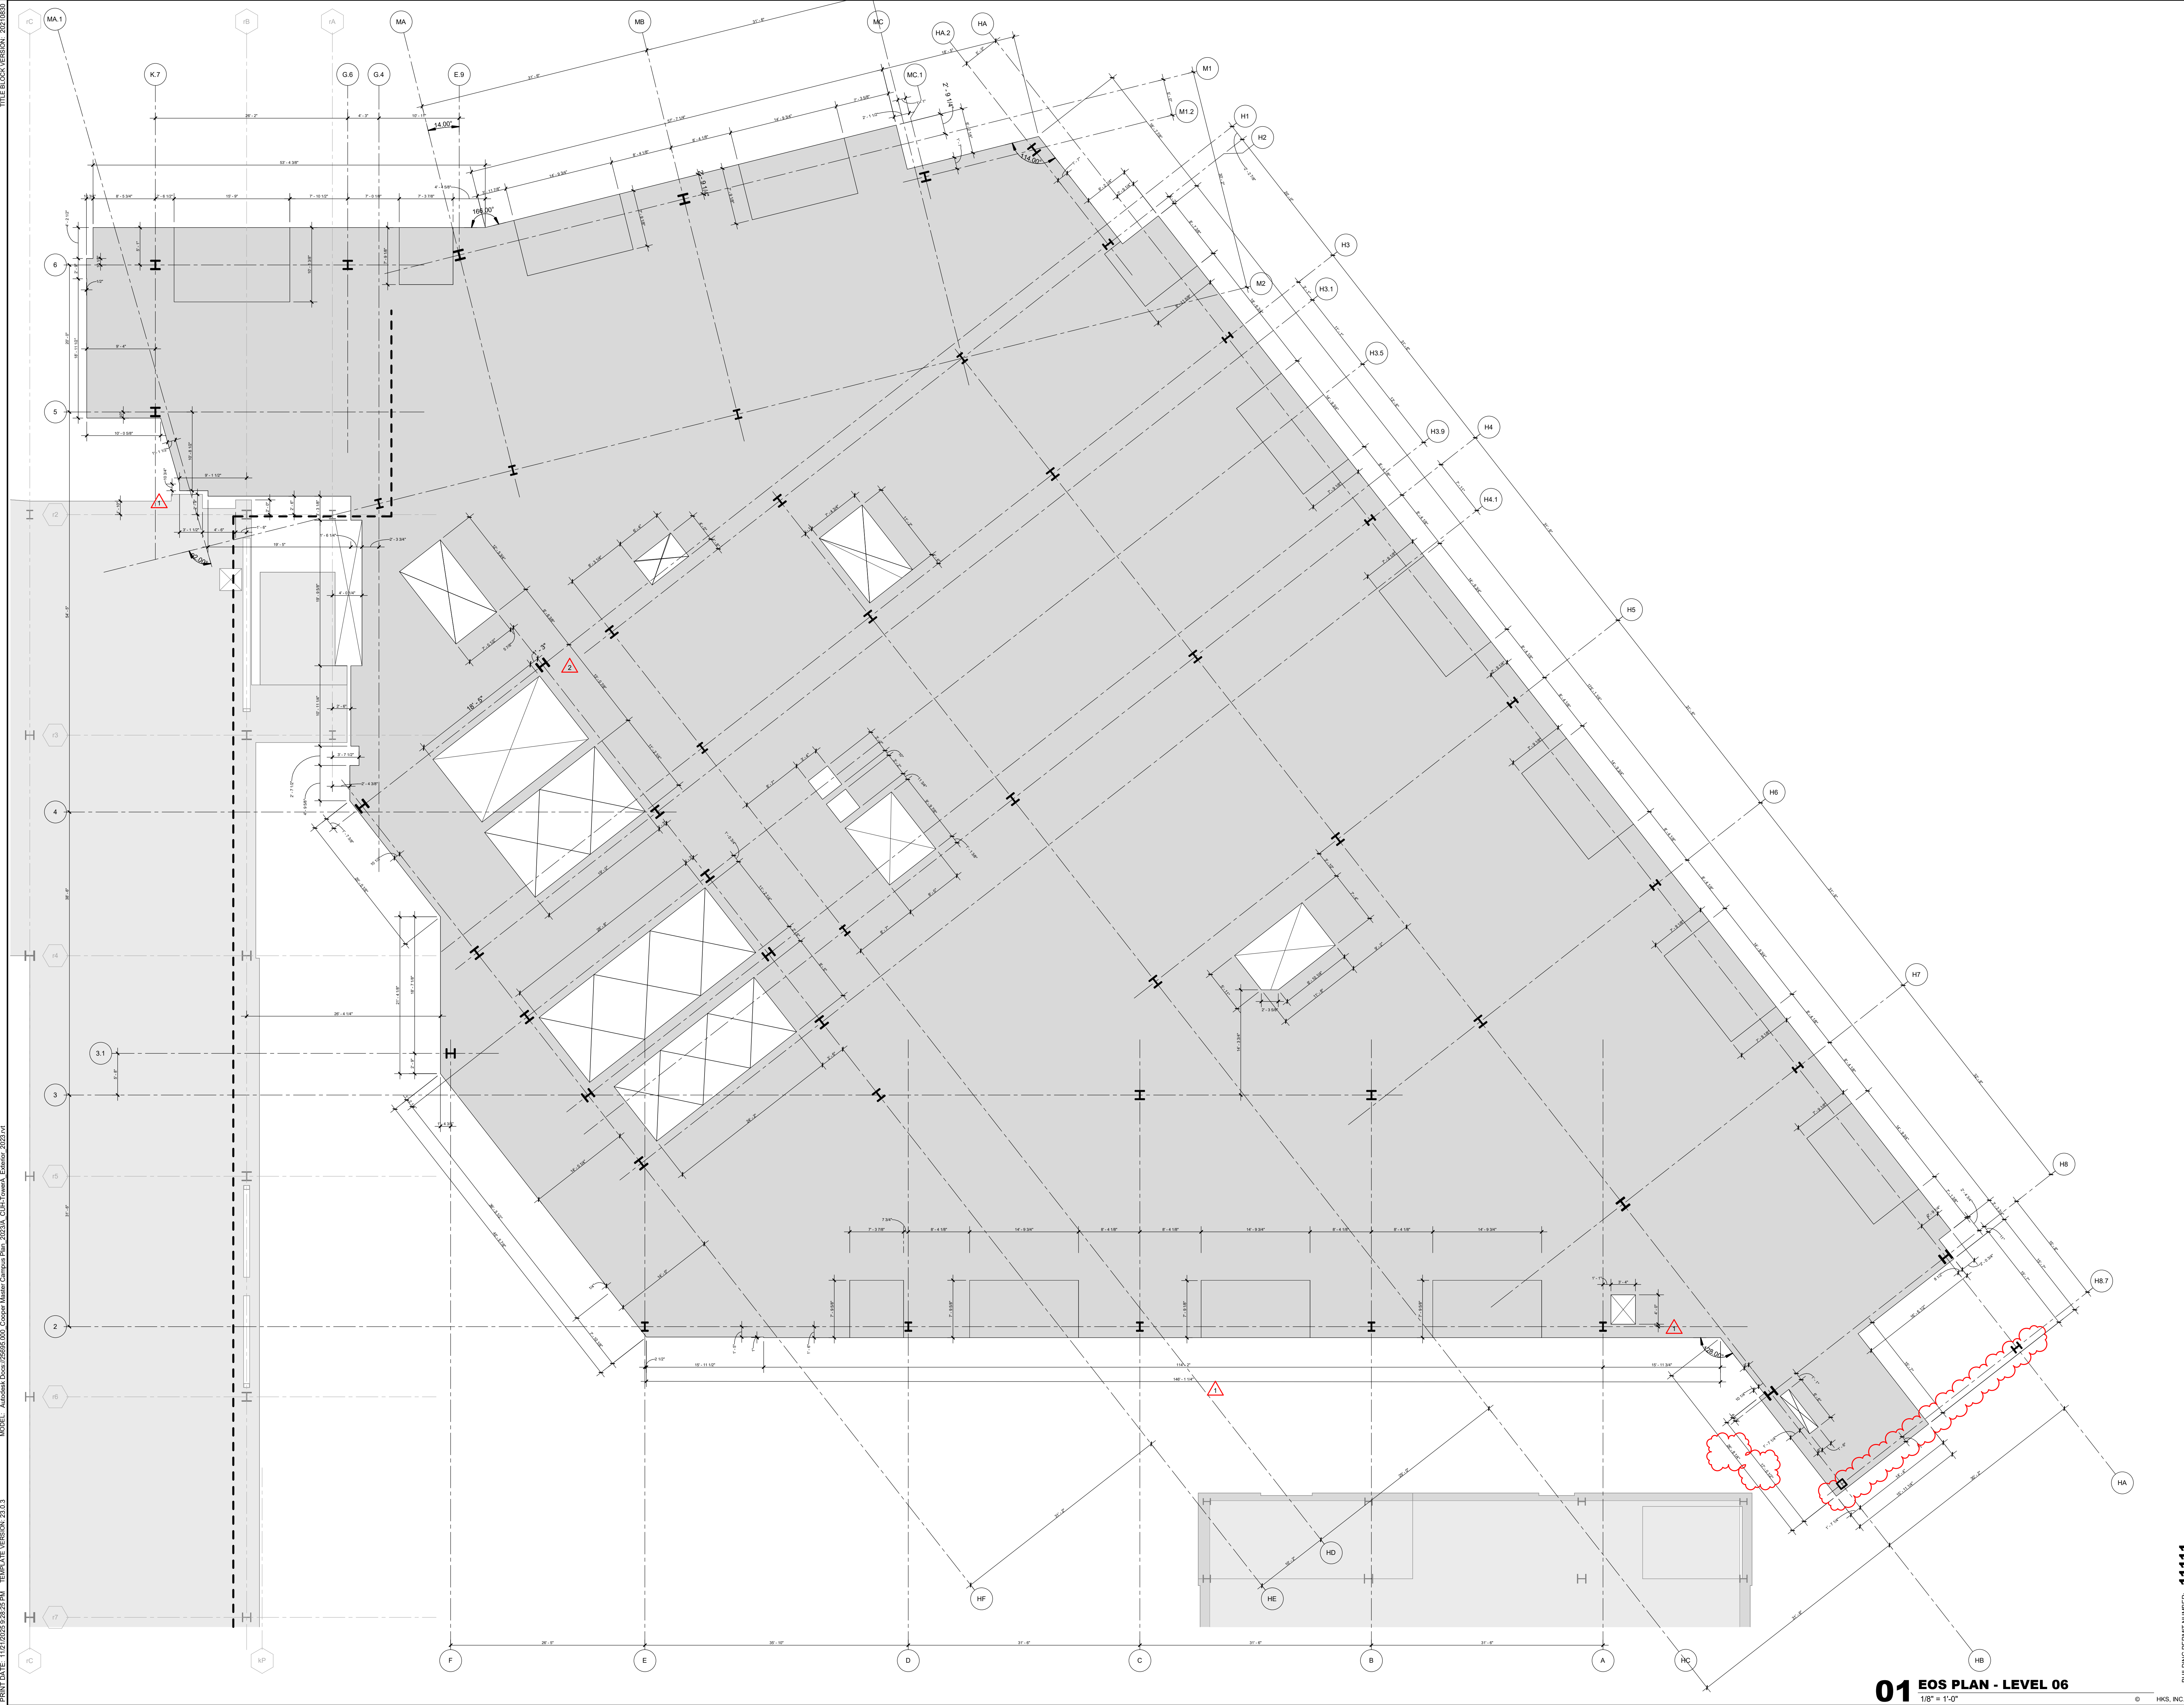


RESERVE FOR DCA STAMP



ARCHITECT
HKS, P.C.
1250 I (EYE) STREET NW, SUITE 600
WASHINGTON, DC 20005
ASSOCIATE ARCHITECT / INTERIOR DESIGNER
ARRAY
1 WEST ELM STREET, SUITE 500
CONSHOHOCKEN, PA 19028
STRUCTURAL ENGINEER
O'DONNELL & NACCARATO
701 MARKET ST., #6000
PHILADELPHIA, PA 19106
MEP-FP / LOW VOLTAGE ENGINEER
BR-A CONSULTING ENGINEERS
2401 WALNUT ST SUITE 701
PHILADELPHIA, PA 19103
HIGHLAND ASSOCIATES
102 HIGHLAND AVE
CLARKS SUMMIT, PA 18411



OWNER
COOPER UNIVERSITY HEALTHCARE
1 COOPER PLAZA
CAMDEN, NJ 08103
PROJECT MANAGER
PURE PM
2026 RICHMOND STREET
PHILADELPHIA, PA 19134
CIVIL ENGINEER / LANDSCAPE
LANGAN
1818 MARKET STREET, SUITE 3300
PHILADELPHIA, PA 19103
SEAL & SIGNATURE

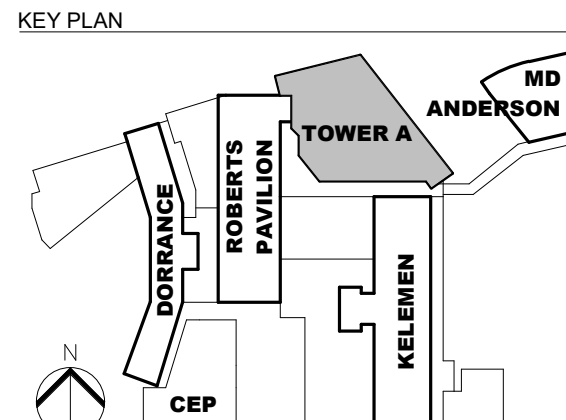



REVISION	NO.	DESCRIPTION	DATE
1	BULLETIN #4		04/28/2025
2	RFI 0343		09/08/2025
3	RFI 0416		11/14/2025

HKS PROJECT NUMBER
25695.100
DATE
10/15/2024
ISSUE
CORE & SHELL PERMIT SET
SHEET TITLE
EDGE OF SLAB PLAN - LEVEL 06

SHEET NO.
A1.206

TITLE BLOCK VERSION: 20210830
MODEL: A:\models\25695.000_Cooper_Miller_Campus_Plan_2023\A_Cooper_Tower_A_Edging_2023.rvt
PRINT DATE: 11/21/2025 9:28:32 PM
TEMPLATE VERSION: 23.0.3
HKS, INC.

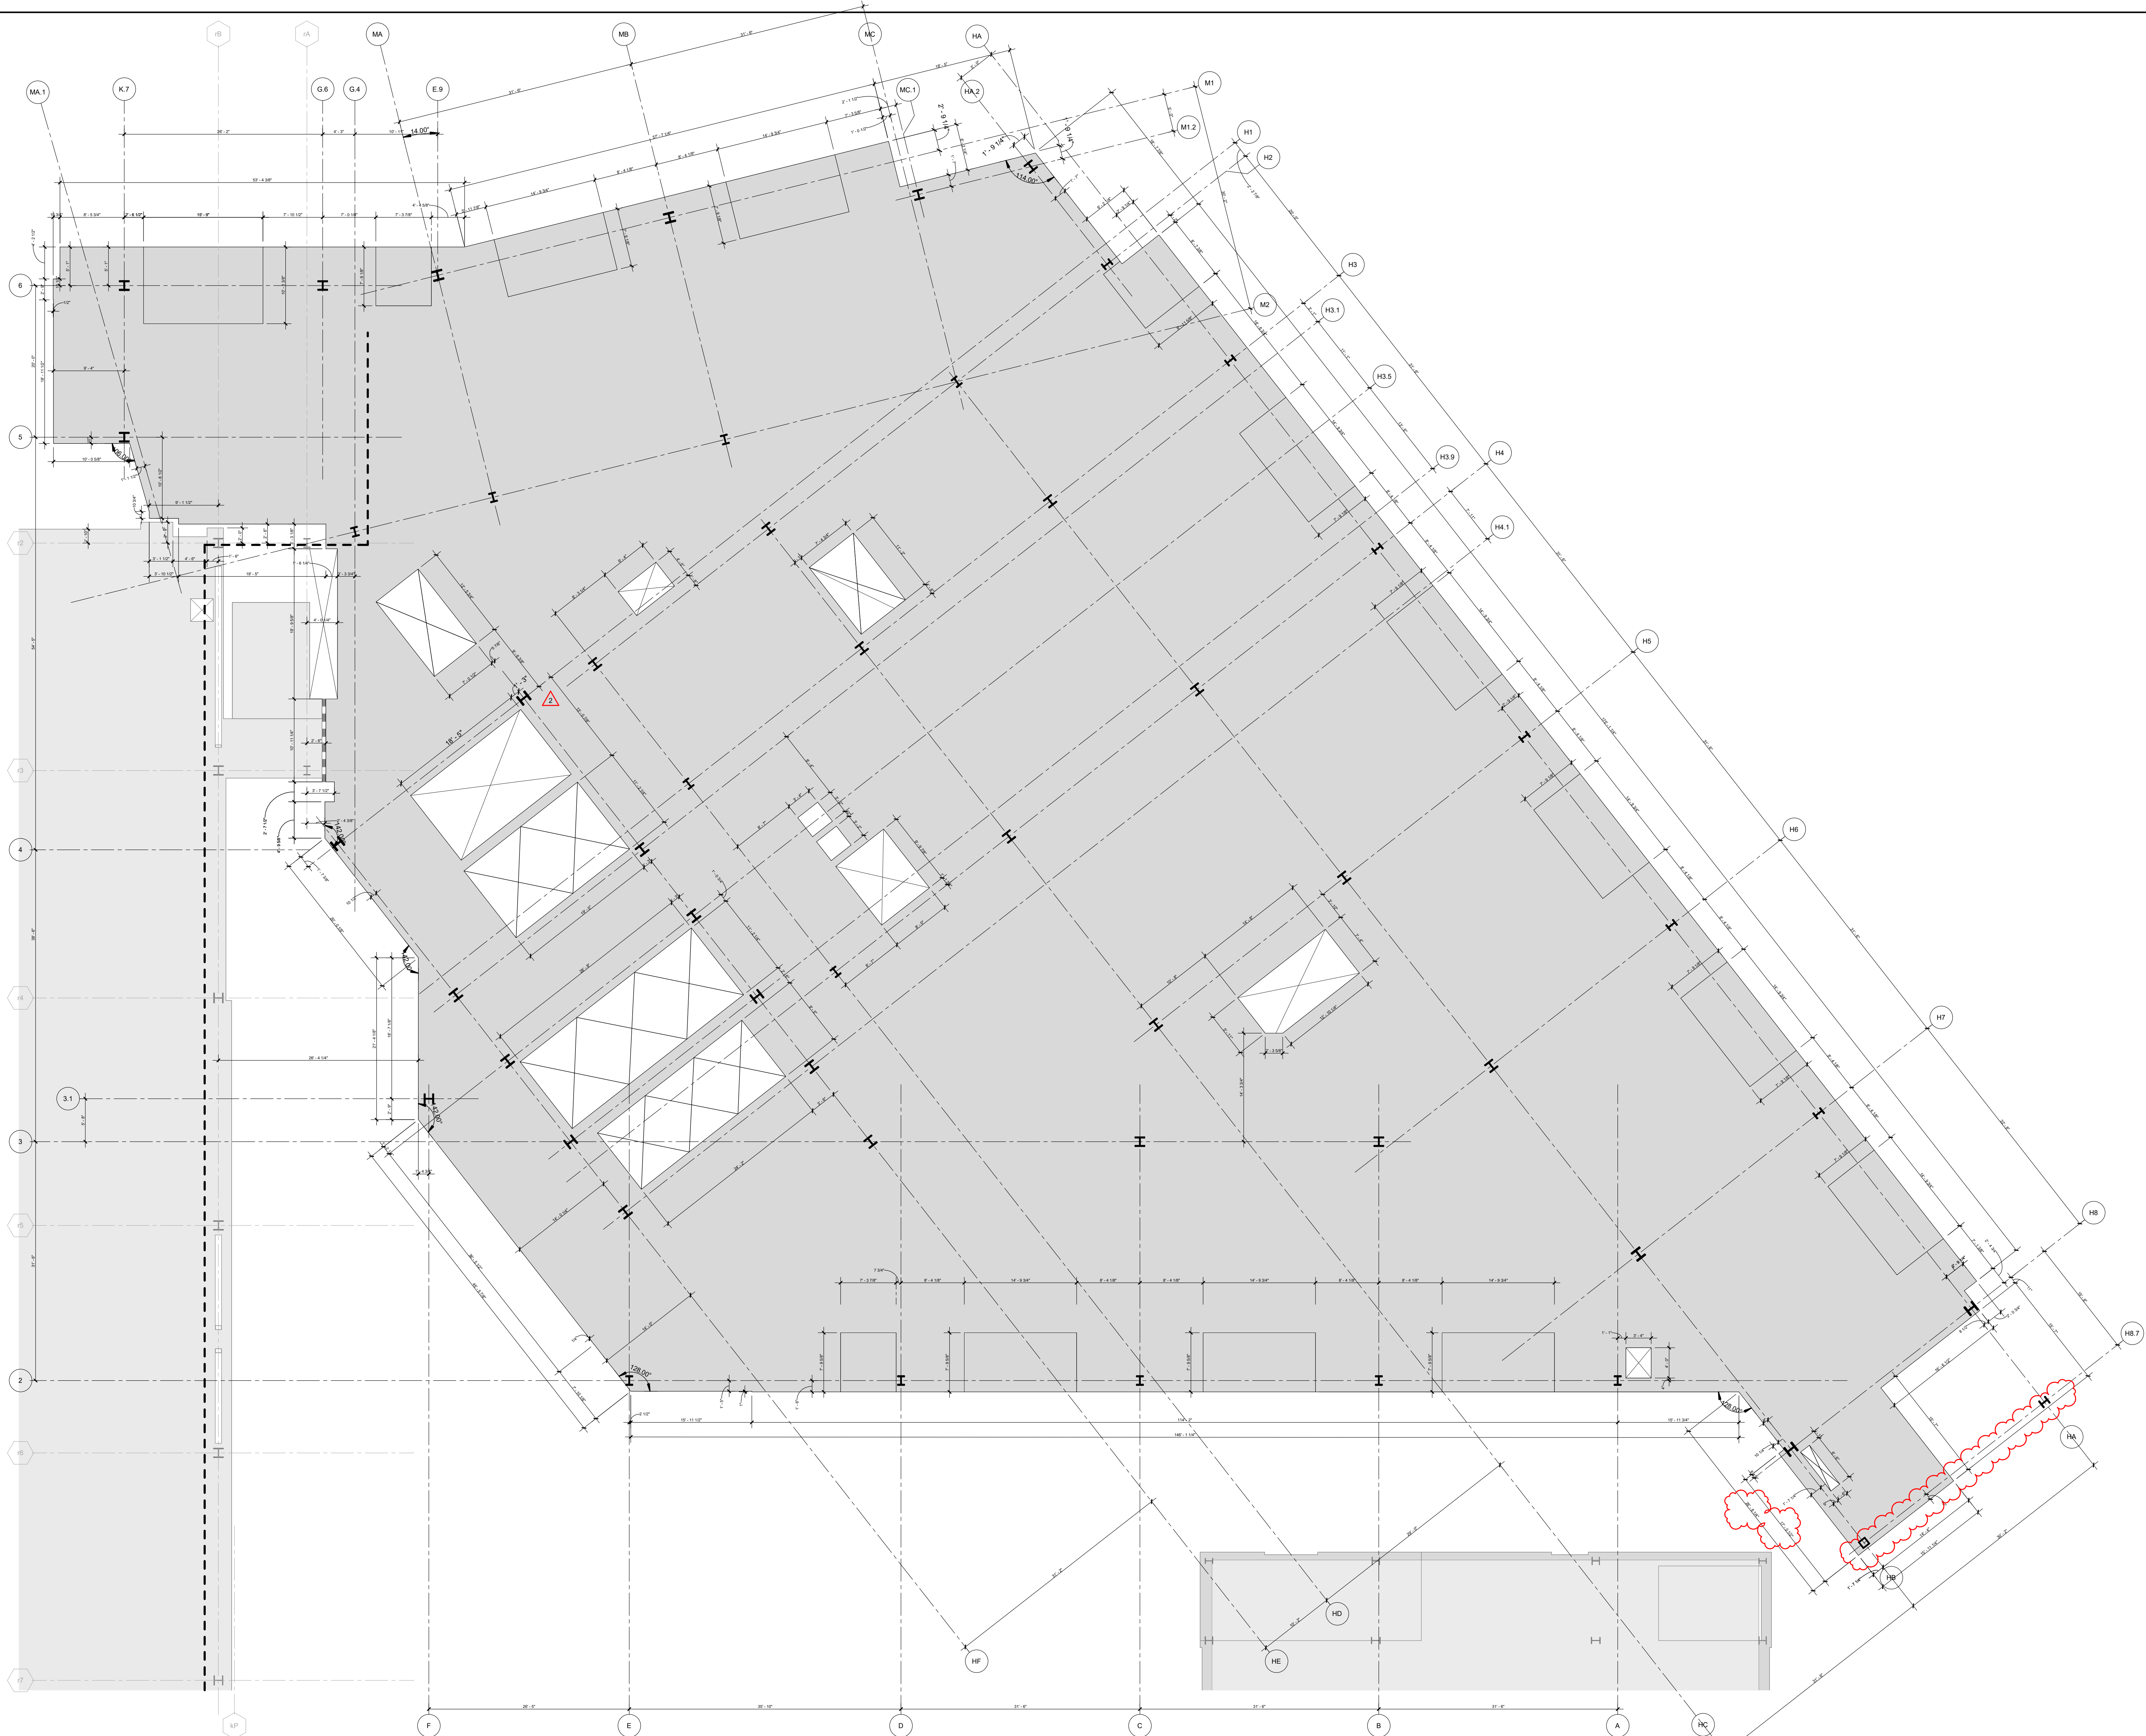

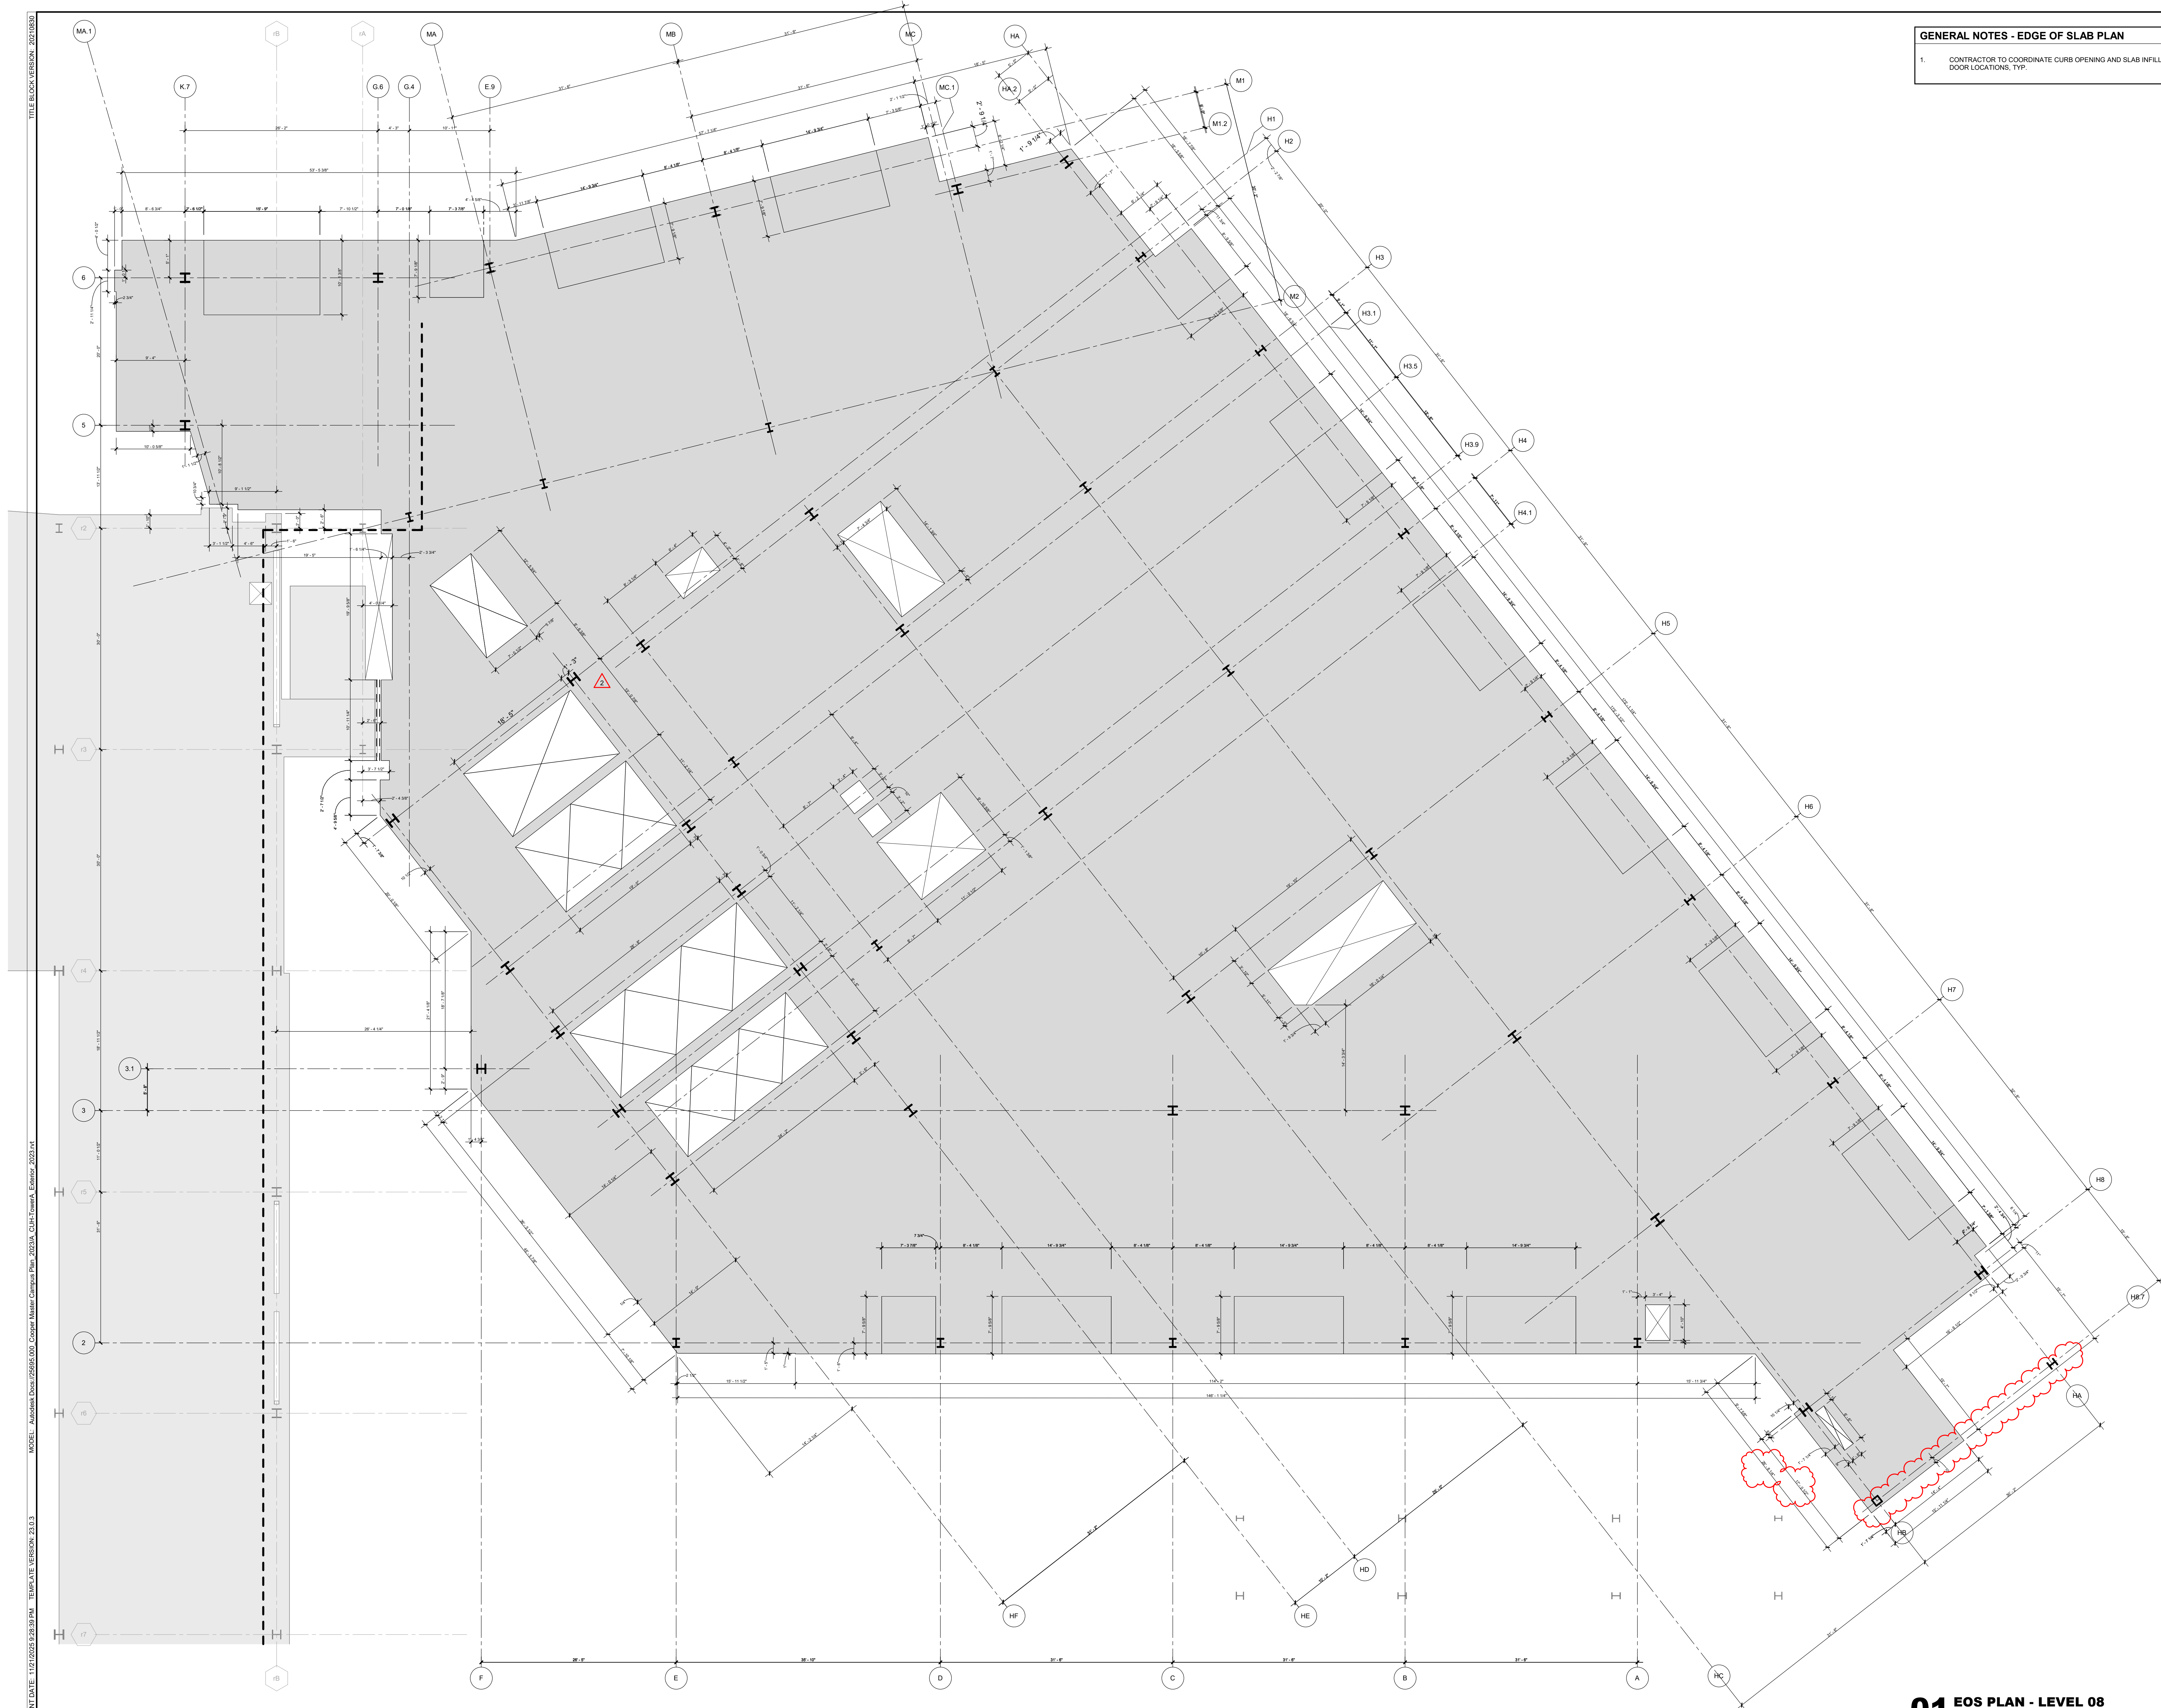

GENERAL NOTES - EDGE OF SLAB PLAN

1. CONTRACTOR TO COORDINATE CURB OPENING AND SLAB INFILL AT DOOR LOCATIONS, TYP.

RESERVE FOR DCA STAMP



ARCHITECT
HKS, P.C.
1250 I (EYE) STREET NW, SUITE 600
WASHINGTON, DC 20005

ASSOCIATE ARCHITECT / INTERIOR DESIGNER
ARRAY
1 WEST ELM STREET, SUITE 500
CONSHOHOCKEN, PA 19028

STRUCTURAL ENGINEER
O'DONNELL & NACCARATO
701 MARKET ST., #6000
PHILADELPHIA, PA 19106

MEP-FP / LOW VOLTAGE ENGINEER
BR-A CONSULTING ENGINEERS
2401 WALNUT ST SUITE 701
PHILADELPHIA, PA 19103
HIGHLAND ASSOCIATES
102 HIGHLAND AVE
CLARKS SUMMIT, PA 18411




OWNER
COOPER UNIVERSITY HEALTHCARE
1 COOPER PLAZA
CAMDEN, NJ 08103

PROJECT MANAGER
PURE PM
2026 RICHMOND STREET
PHILADELPHIA, PA 19134

CIVIL ENGINEER / LANDSCAPE
LANGAN
1818 MARKET STREET, SUITE 3300
PHILADELPHIA, PA 19103

SEAL & SIGNATURE

KEY PLAN

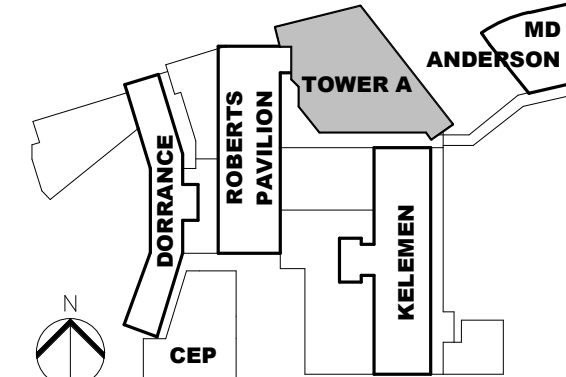

NO.	DESCRIPTION	DATE
1	BULLETIN #4	04/28/2025
2	RFI 0343	09/08/2025
3	RFI 0416	11/14/2025

HKS PROJECT NUMBER
25695.100
DATE
10/15/2024

ISSUE
CORE & SHELL PERMIT SET
SHEET TITLE
EDGE OF SLAB PLAN - LEVEL 08


SHEET NO.

01 EOS PLAN - LEVEL 08
1/8" = 1'-0"

BUILDING PERMIT NUMBER: 1111

HKS, INC.

A1.208

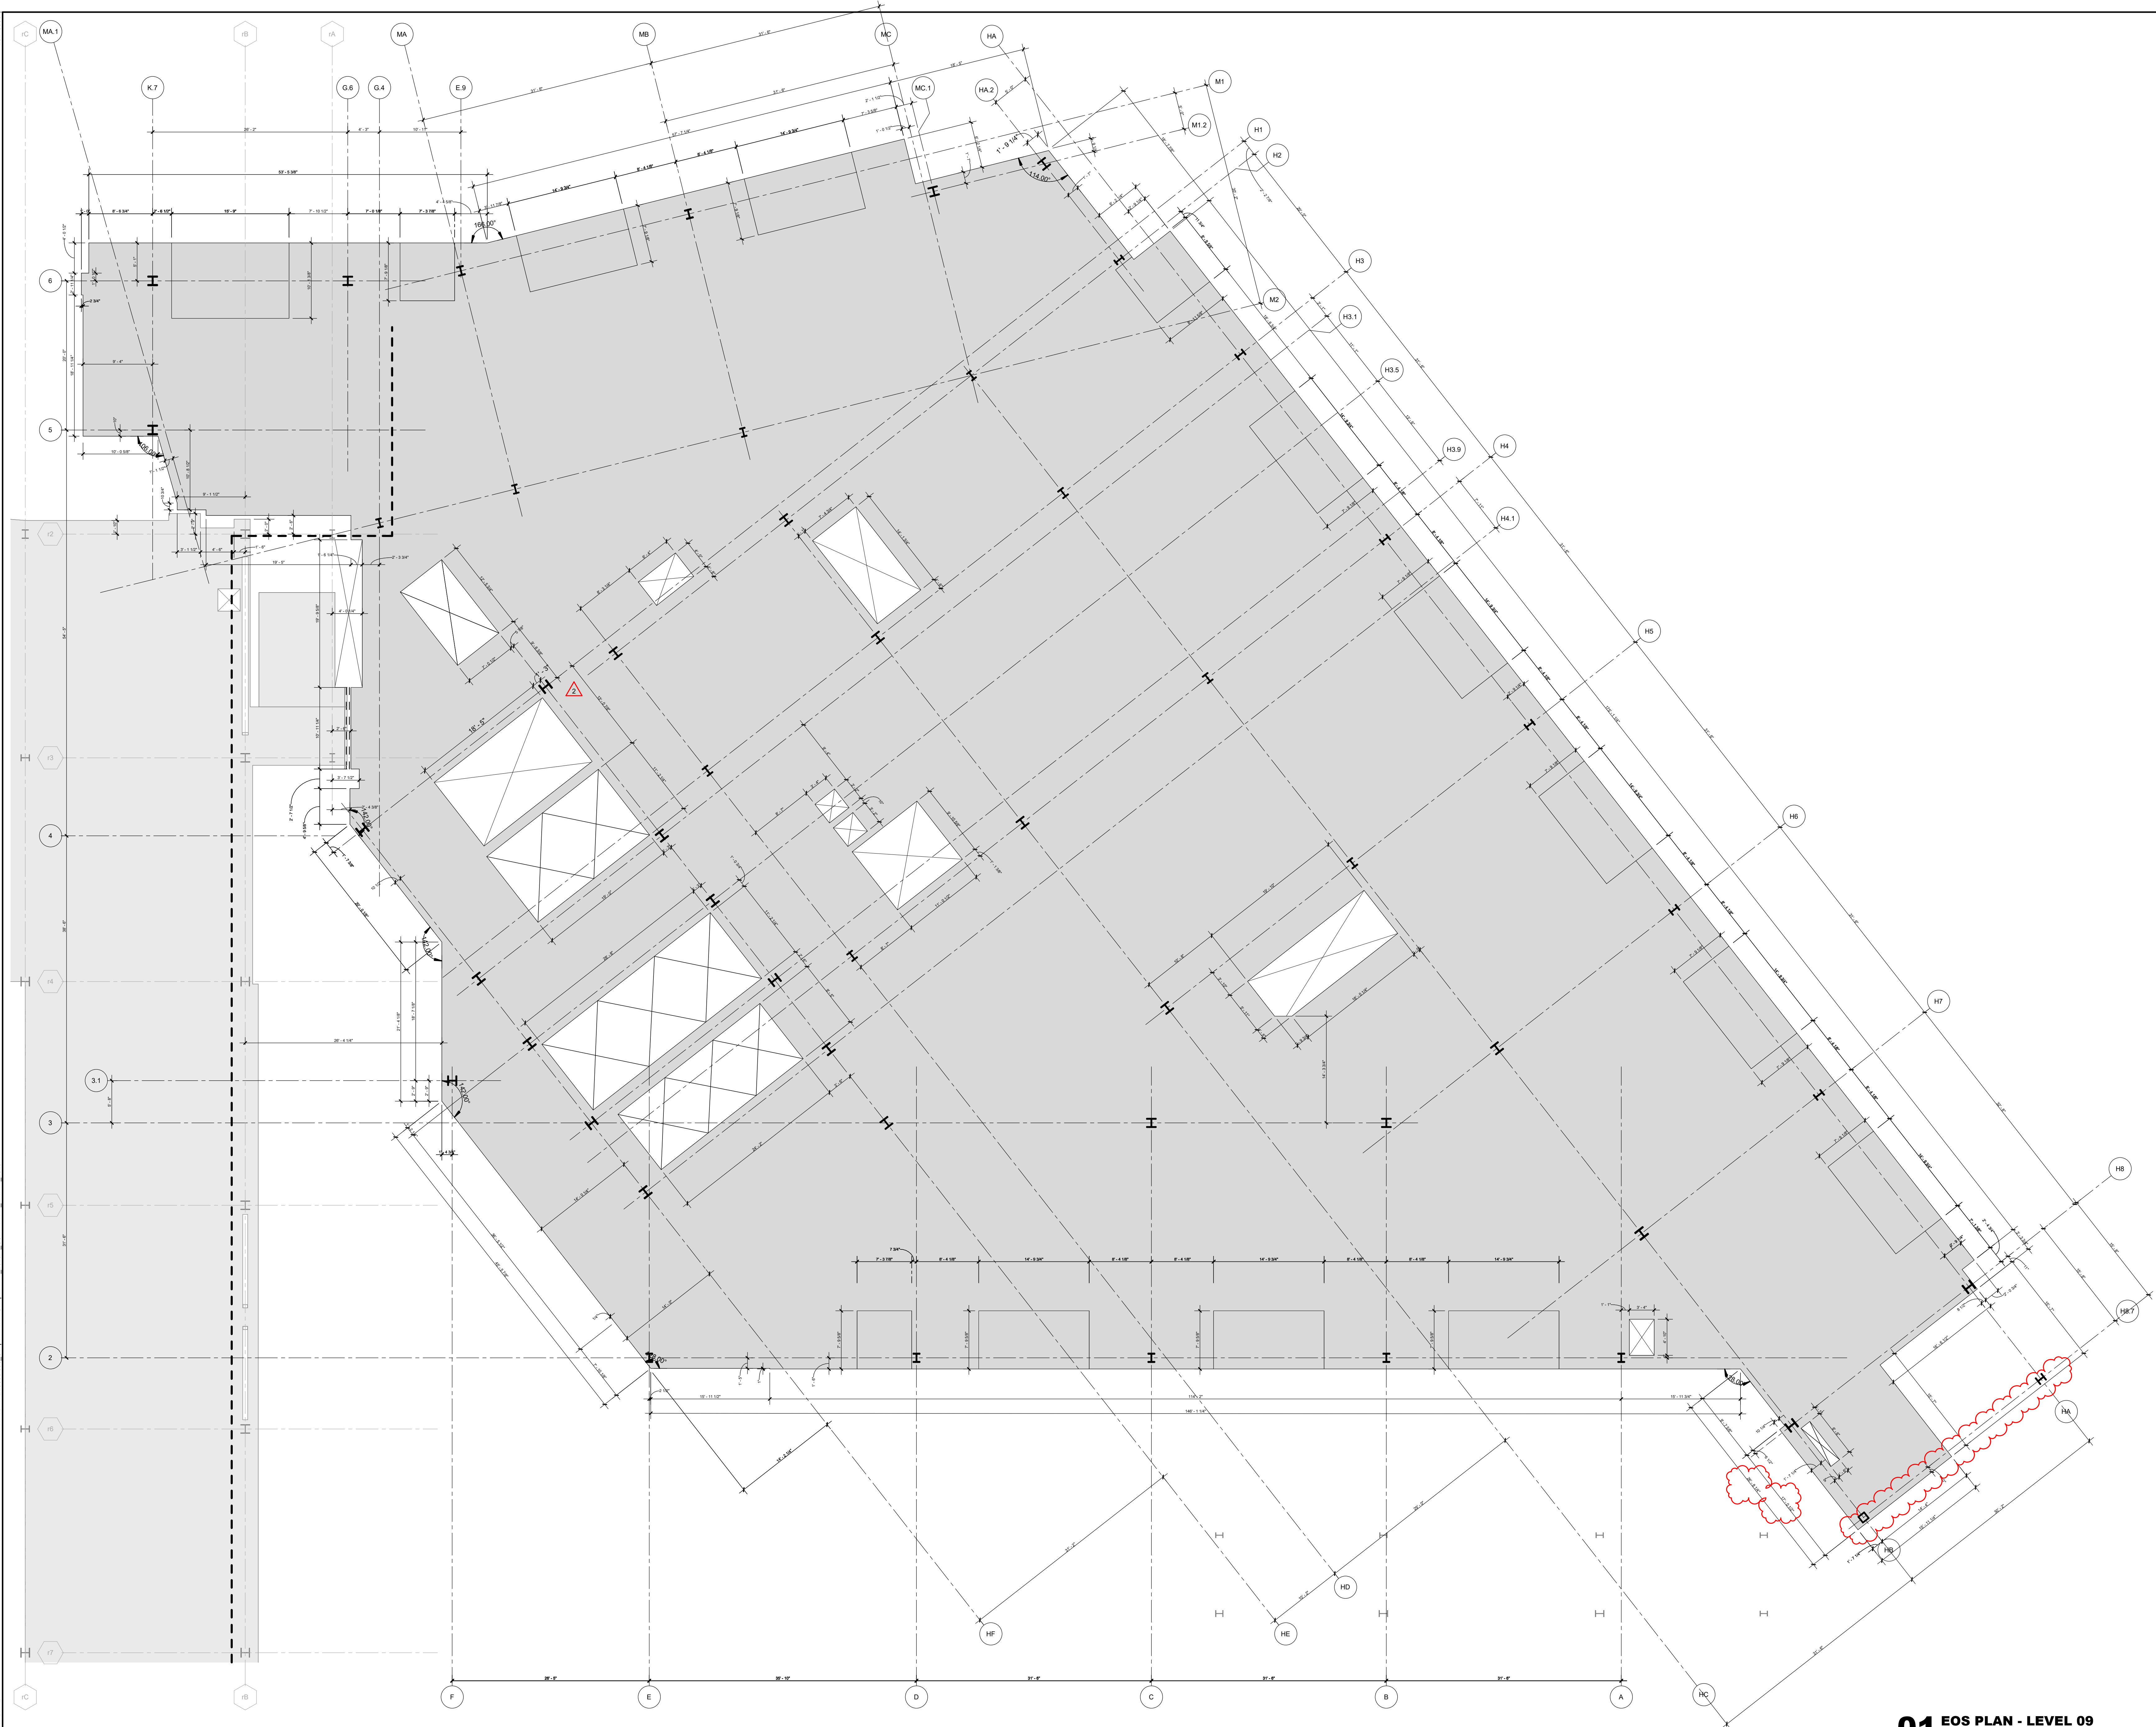

01 EOS PLAN - LEVEL 09
1/8" = 1'-0"

HKS, INC.

RESERVE FOR DCA STAMP



ARCHITECT
HKS, P.C.
1250 I (EYE) STREET NW, SUITE 600
WASHINGTON, DC 20005

**ASSOCIATE ARCHITECT /
INTERIOR DESIGNER**
ARRAY
1 WEST ELM STREET, SUITE 500
CONSHOHOCKEN, PA 19428

STRUCTURAL ENGINEER
O'DONNELL & NACCARATO
701 MARKET ST., #0000
PHILADELPHIA, PA 19106

**MEP-PP / LOW VOLTAGE
ENGINEER**
BR4 CONSULTING ENGINEERS
2041 WALNUT ST SUITE 701
PHILADELPHIA, PA 19103
HIGHLAND ASSOCIATES
102 HIGHLAND AVE
CLARKS SUMMIT, PA 18411




OWNER
COOPER UNIVERSITY HEALTHCARE
1 COOPER PLAZA
CAMDEN, NJ 08103

PROJECT MANAGER
PURE PM
2926 RICHMOND STREET
PHILADELPHIA, PA 19134

CIVIL ENGINEER / LANDSCAPE
LANGAN
1818 MARKET STREET, SUITE 3300
PHILADELPHIA, PA 19103

SEAL & SINGATURE

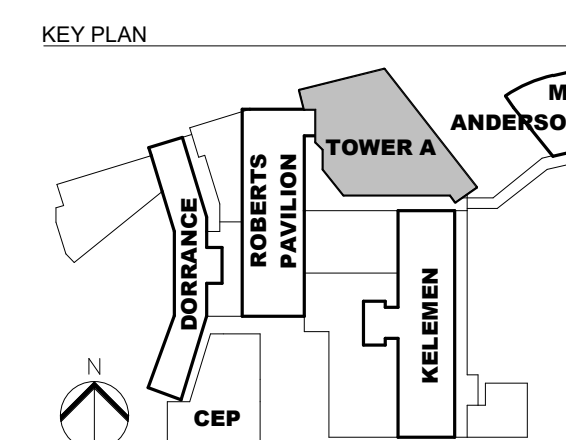

REVISION		
NO.	DESCRIPTION	DATE
1	BULLETIN #4	04/28/20
2	RFI 0343	09/08/20
3	RFI 0416	11/14/20

HKS PROJECT NUMBER
25695.100

DATE
10/15/2024

ISSUE
CORE & SHELL PERMIT SET

SHEET TITLE
EDGE OF SLAB PLAN - LEVEL 09


SHEET NO.

A1.209

TITLE BLOCK VERSION: 20210830

MODEL: Autodesk Docs 25695.000 Cooper Medical Campus Plan 2023.0A CHA Tower A, Exterior 2023.rvt

PRINT DATE: 1/21/2025 9:29:53 PM TEMPLATE VERSION: 23.0.3

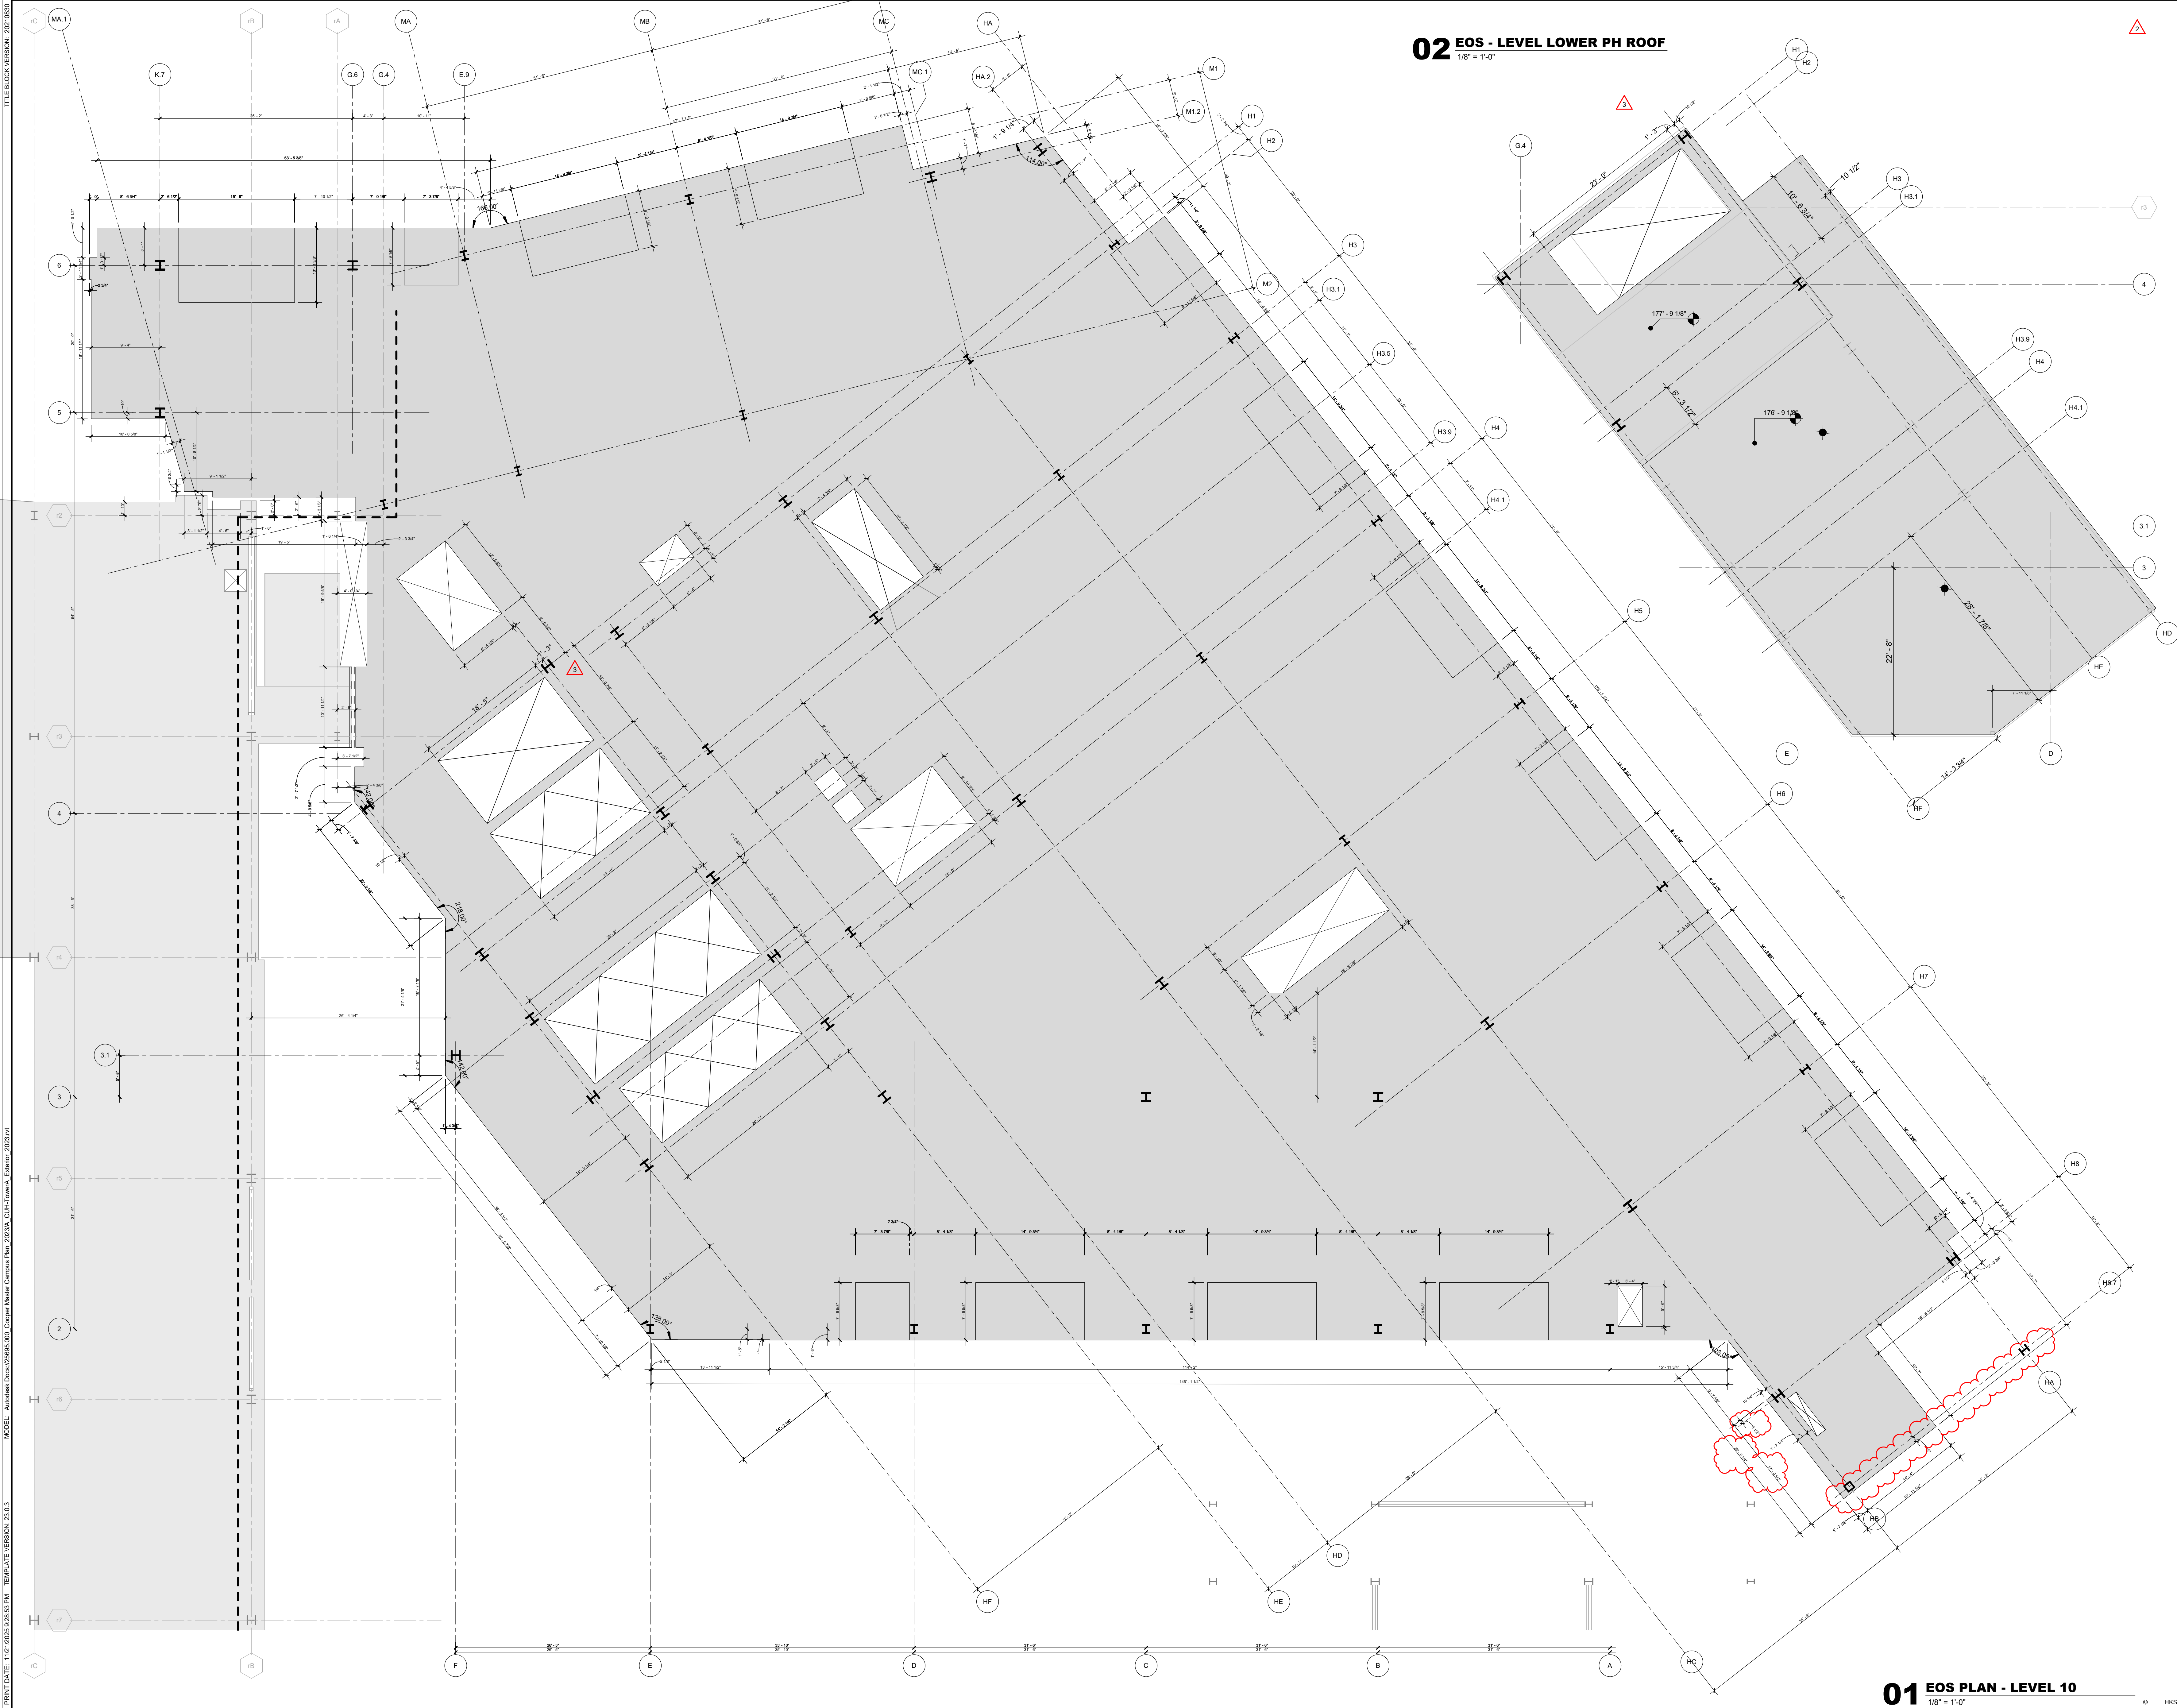

RESERVE FOR DCA STAMP




ARCHITECT
HKS, P.C.
1250 I (EYE) STREET NW, SUITE 600
WASHINGTON, DC 20005
ASSOCIATE ARCHITECT / INTERIOR DESIGNER
ARRAY
1 WEST ELM STREET, SUITE 500
CONSHOHOCKEN, PA 19428
STRUCTURAL ENGINEER
O'DONNELL & NACCARATO
701 MARKET ST., #6000
PHILADELPHIA, PA 19106
MEP-FP / LOW VOLTAGE ENGINEER
BR-A CONSULTING ENGINEERS
2401 WALNUT ST SUITE 701
PHILADELPHIA, PA 19103
HIGHLAND ASSOCIATES
102 HIGHLAND AVE
CLARKS SUMMIT, PA 18411



OWNER
COOPER UNIVERSITY HEALTHCARE
1 COOPER PLAZA
CAMDEN, NJ 08103
PROJECT MANAGER
PURE PM
2026 RICHMOND STREET
PHILADELPHIA, PA 19134
CIVIL ENGINEER / LANDSCAPE
LANGAN
1818 MARKET STREET, SUITE 3300
PHILADELPHIA, PA 19103
SEAL & SIGNATURE

KEY PLAN

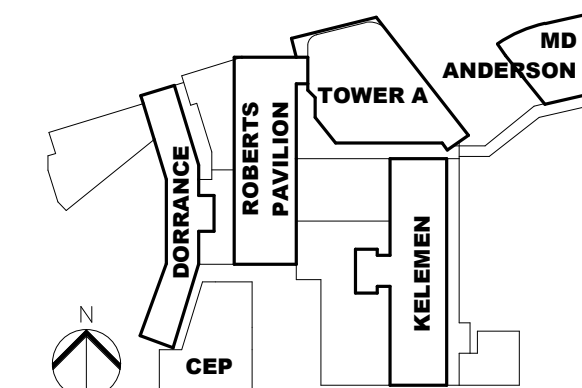

NO.	REVISION	DATE
1	BULLETIN #4	04/28/2025
2	RFI 0320	08/14/2025
3	RFI 0343	09/08/2025
4	RFI 0416	11/14/2025

HKS PROJECT NUMBER
25695.100
DATE
10/15/2024

ISSUE
CORE & SHELL PERMIT SET
SHEET TITLE
EDGE OF SLAB PLAN - LEVEL 10


SHEET NO.

A1.210

BUILDING PERMIT NUMBER: 1111

© HKS, INC.

TITLE BLOCK VERSION: 20210830
MODEL: A:\models\25695.000_Cooper_Miller_Campus_Plan_2023\A_Cooper_Tower_A_Existing_2023.rvt
PRINT DATE: 11/21/2025 9:29:01 PM
TEMPLATE VERSION: 23.0.3
© HKS, INC.

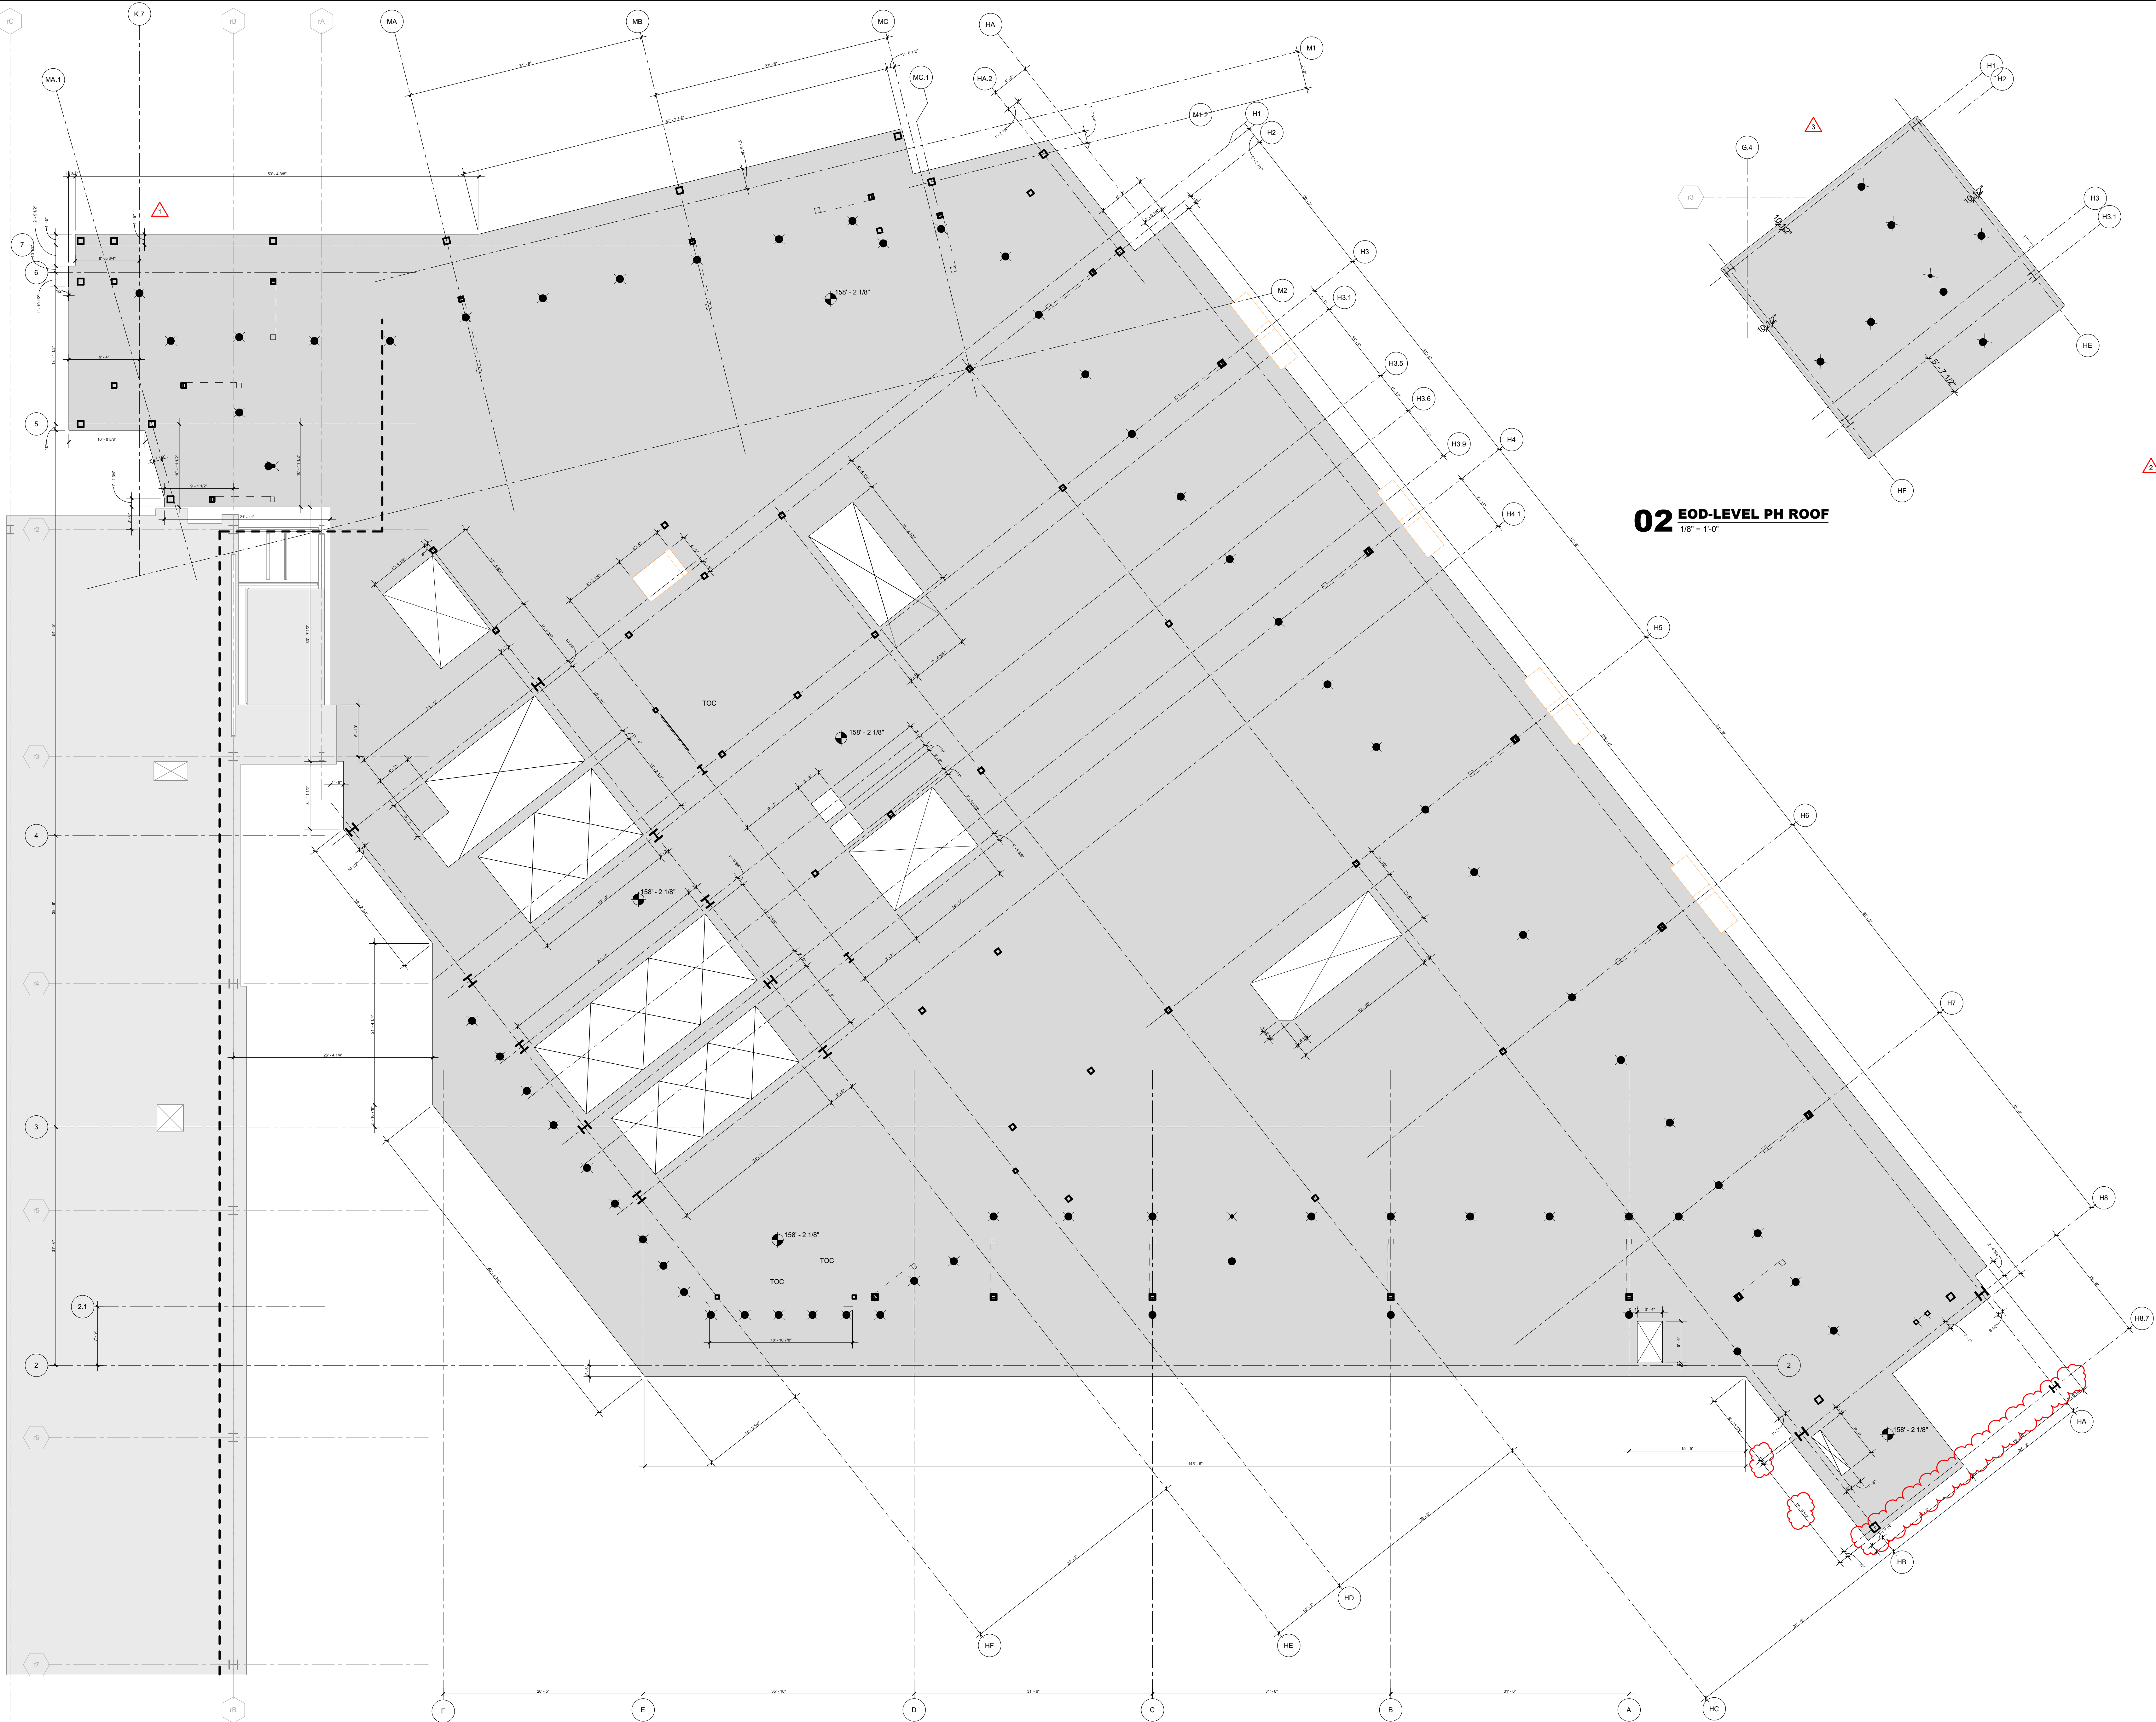


RESERVE FOR DCA STAMP



ARCHITECT
HKS, P.C.
1250 I (EYE) STREET NW, SUITE 600
WASHINGTON, DC 20005
ASSOCIATE ARCHITECT / INTERIOR DESIGNER
ARRAY
1 WEST ELM STREET, SUITE 500
CONSHOHOCKEN, PA 19428
STRUCTURAL ENGINEER
O'DONNELL & NACCARATO
701 MARKET ST., #6000
PHILADELPHIA, PA 19106
MEP-FP / LOW VOLTAGE ENGINEER
BR-A CONSULTING ENGINEERS
2401 WALNUT ST SUITE 701
PHILADELPHIA, PA 19103
HIGHLAND ASSOCIATES
102 HIGHLAND AVE
CLARKS SUMMIT, PA 18411



OWNER
COOPER UNIVERSITY HEALTHCARE
1 COOPER PLAZA
CAMDEN, NJ 08103
PROJECT MANAGER
PURE PM
2026 RICHMOND STREET
PHILADELPHIA, PA 19134
CIVIL ENGINEER / LANDSCAPE
LANGAN
1818 MARKET STREET, SUITE 3300
PHILADELPHIA, PA 19103
SEAL & SIGNATURE

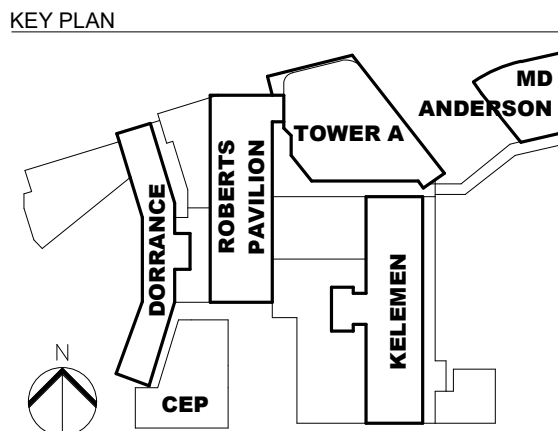

REVISION	NO.	DESCRIPTION	DATE
1	BULLETIN #4		04/28/2025
2	RFI 0320		08/14/2025
3	RFI 0343		09/08/2025
4	RFI 0416		11/14/2025

HKS PROJECT NUMBER
25695.100
DATE
10/15/2024
ISSUE
CORE & SHELL PERMIT SET
SHEET TITLE
EDGE OF SLAB PLAN - LEVEL ROOF

BUILDING PERMIT NUMBER: 1111
SHEET NO.
A1.211

TITLE BLOCK VERSION: 20210830
MODEL: AutoCAD Docs 25695.00 Cooper Master Campus Plan 2023.a CHAT TowerA_Elevs.dwg 2023.rvt
PRINT DATE: 1/21/2025 9:29:13 PM TEMPLATE VERSION: 23.0.3
© HKS, INC.

FACADE MATERIAL LEGEND

CURTAIN WALL GLAZING - VISION - LAMINATED GL-1V

CURTAIN WALL GLAZING - SPANDREL GL-1S

CURTAIN WALL GLAZING - LOW IRON VISION W/ CUSTOM FRIT GL-2V

CURTAIN WALL GLAZING - LOW IRON VISION - W/ CUSTOM FRIT - LAMINATED GL-2V2

CURTAIN WALL GLAZING - LOW IRON SPANDREL GL-2S

CURTAIN WALL GLAZING - LOW IRON VISION GL-3V

CURTAIN WALL GLAZING - LOW IRON SPANDREL GL-3S

CURTAIN WALL GLAZING - LOW IRON VISION W/ CUSTOM FRIT GL-6V

CURTAIN WALL GLAZING - LOW IRON SPANDREL W/ CUSTOM FRIT GL-6S

METAL PANEL, GLAZED IN METAL PANEL GL-1MP, AMF-02

METAL PANEL AMF-01

METAL PANEL AMF-03

METAL PANEL AMF-01B

METAL PANEL AMF-01B

BRICK VENEER MV-01

NATURAL STONE VENEER ST-01

GENERAL NOTES

1. REFER TO SPECIFICATION SECTION XX.XX.XX FOR DETAILED EXTERIOR DESIGN SELECTIONS.
2. SEE NOTES ON ELEVATIONS FOR LOUVER LOCATIONS.
3. SEE NOTES ON ELEVATIONS AND DETAILS FOR PARAPET CORING AND CAP TYPES. ALL CORING AND CAP FINISHES TO MATCH CARPENTRY MATERIAL, UNO.
4. PROVIDE SIGNAGE SUPPORT THROUGH CURTAIN WALL FRAMING.
5. SEE LIGHTING DRAWINGS FOR EXTERIOR LIGHTING.

RESERVE FOR DCA STAMP

ARCHITECT
HKS, P.C.
1250 I (EYE) STREET NW, SUITE 600
WASHINGTON, DC 20005
ASSOCIATE ARCHITECT / INTERIOR DESIGNER
ARRAY
1 WEST ELM STREET, SUITE 500
CONSHOHOCKEN, PA 19028
STRUCTURAL ENGINEER
O'DONNELL & NACCARATO
701 MARKET ST., #6000
PHILADELPHIA, PA 19106
MEP-FP / LOW VOLTAGE ENGINEER
BR-A CONSULTING ENGINEERS
2401 WALNUT ST SUITE 701
PHILADELPHIA, PA 19103
HIGHLAND ASSOCIATES
102 HIGHLAND AVE
CLARKS SUMMIT, PA 18411

OWNER
COOPER UNIVERSITY HEALTHCARE
1 COOPER PLAZA
CAMDEN, NJ 08103
PROJECT MANAGER
PURE PM
2026 RICHMOND STREET
PHILADELPHIA, PA 19134
CIVIL ENGINEER / LANDSCAPE
LANGAN
1818 MARKET STREET, SUITE 3300
PHILADELPHIA, PA 19103
SEAL & SIGNATURE

KEY PLAN

NO.	REVISION	DATE
1	BULLETIN #2	01/23/2025
2	BULLETIN #4	04/28/2025
3	RFI 0416	11/14/2025


HKS PROJECT NUMBER
25695.100
DATE
10/15/2024
ISSUE
CORE & SHELL PERMIT SET
SHEET TITLE
OVERALL BUILDING ELEVATIONS

SHEET NO.

A5.01

TITLE BLOCK VERSION: 20210830
MODEL: Autodesk Docs 25695.000 Cooper Mater Campus Plan 2023A CH1 TowerA Exterior 2023.rvt
PRINT DATE: 1/21/2025 3:29:25 PM TEMPLATE VERSION: 23.0.3
BUILDING PERMIT NUMBER: 1111

FACADE MATERIAL LEGEND

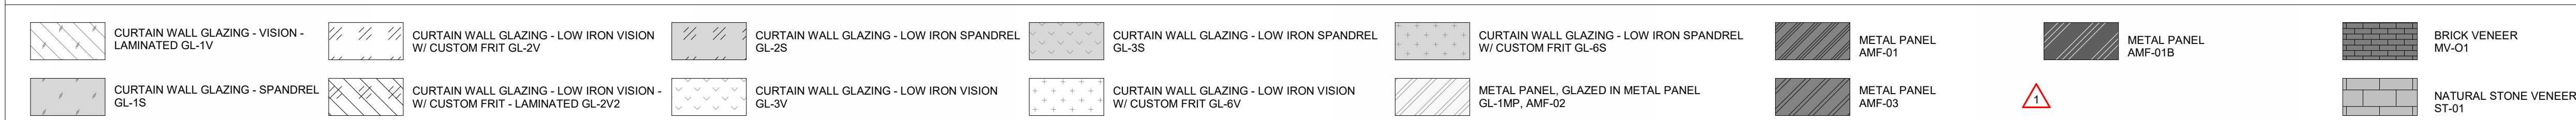

GENERAL NOTES

1. REFER TO SPECIFICATION SECTION XX.XX.XX FOR DETAILED EXTERIOR DESIGN SELECTIONS.
2. SEE NOTES ON ELEVATIONS AND DETAILS FOR PARAPET CORING AND CAP TYPES. ALL CORING AND CAP FINISHES TO MATCH CARVED MATERIAL UNO.
3. PROVIDE SIGNAGE SUPPORT THROUGH CURTAIN WALL FRAMING.
4. SEE LIGHTING DRAWINGS FOR EXTERIOR LIGHTING.
- 5.

RESERVE FOR DCA STAMP



ARCHITECT
HKS, P.C.
1250 I (EYE) STREET NW, SUITE 600
WASHINGTON, DC 20005
ASSOCIATE ARCHITECT / INTERIOR DESIGNER
ARRAY
1 WEST ELM STREET, SUITE 500
CONSHOHOCKEN, PA 19028
STRUCTURAL ENGINEER
O'DONNELL & NACCARATO
701 MARKET ST., #6000
PHILADELPHIA, PA 19106
MEP-FP / LOW VOLTAGE ENGINEER
BR+A CONSULTING ENGINEERS
2401 WALNUT ST SUITE 701
PHILADELPHIA, PA 19103
HIGHLAND ASSOCIATES
102 HIGHLAND AVE
CLARKS SUMMIT, PA 18411



OWNER
COOPER UNIVERSITY HEALTHCARE
1 COOPER PLAZA
CAMDEN, NJ 08103
PROJECT MANAGER
PURE PM
2026 RICHMOND STREET
PHILADELPHIA, PA 19134
CIVIL ENGINEER / LANDSCAPE
LANGAN
1818 MARKET STREET, SUITE 3300
PHILADELPHIA, PA 19103
SEAL & SINGATURE


KEY PLAN

NO.	REVISION	DESCRIPTION	DATE
1	BULLETIN #4		04/28/2025
2	RFI 355		08/29/2025
3	RFI 0416		11/14/2025


HKS PROJECT NUMBER
25695.100
DATE
10/15/2024
ISSUE
CORE & SHELL PERMIT SET
SHEET TITLE
PARTIAL BUILDING ELEVATIONS

SHEET NO.


A5.06

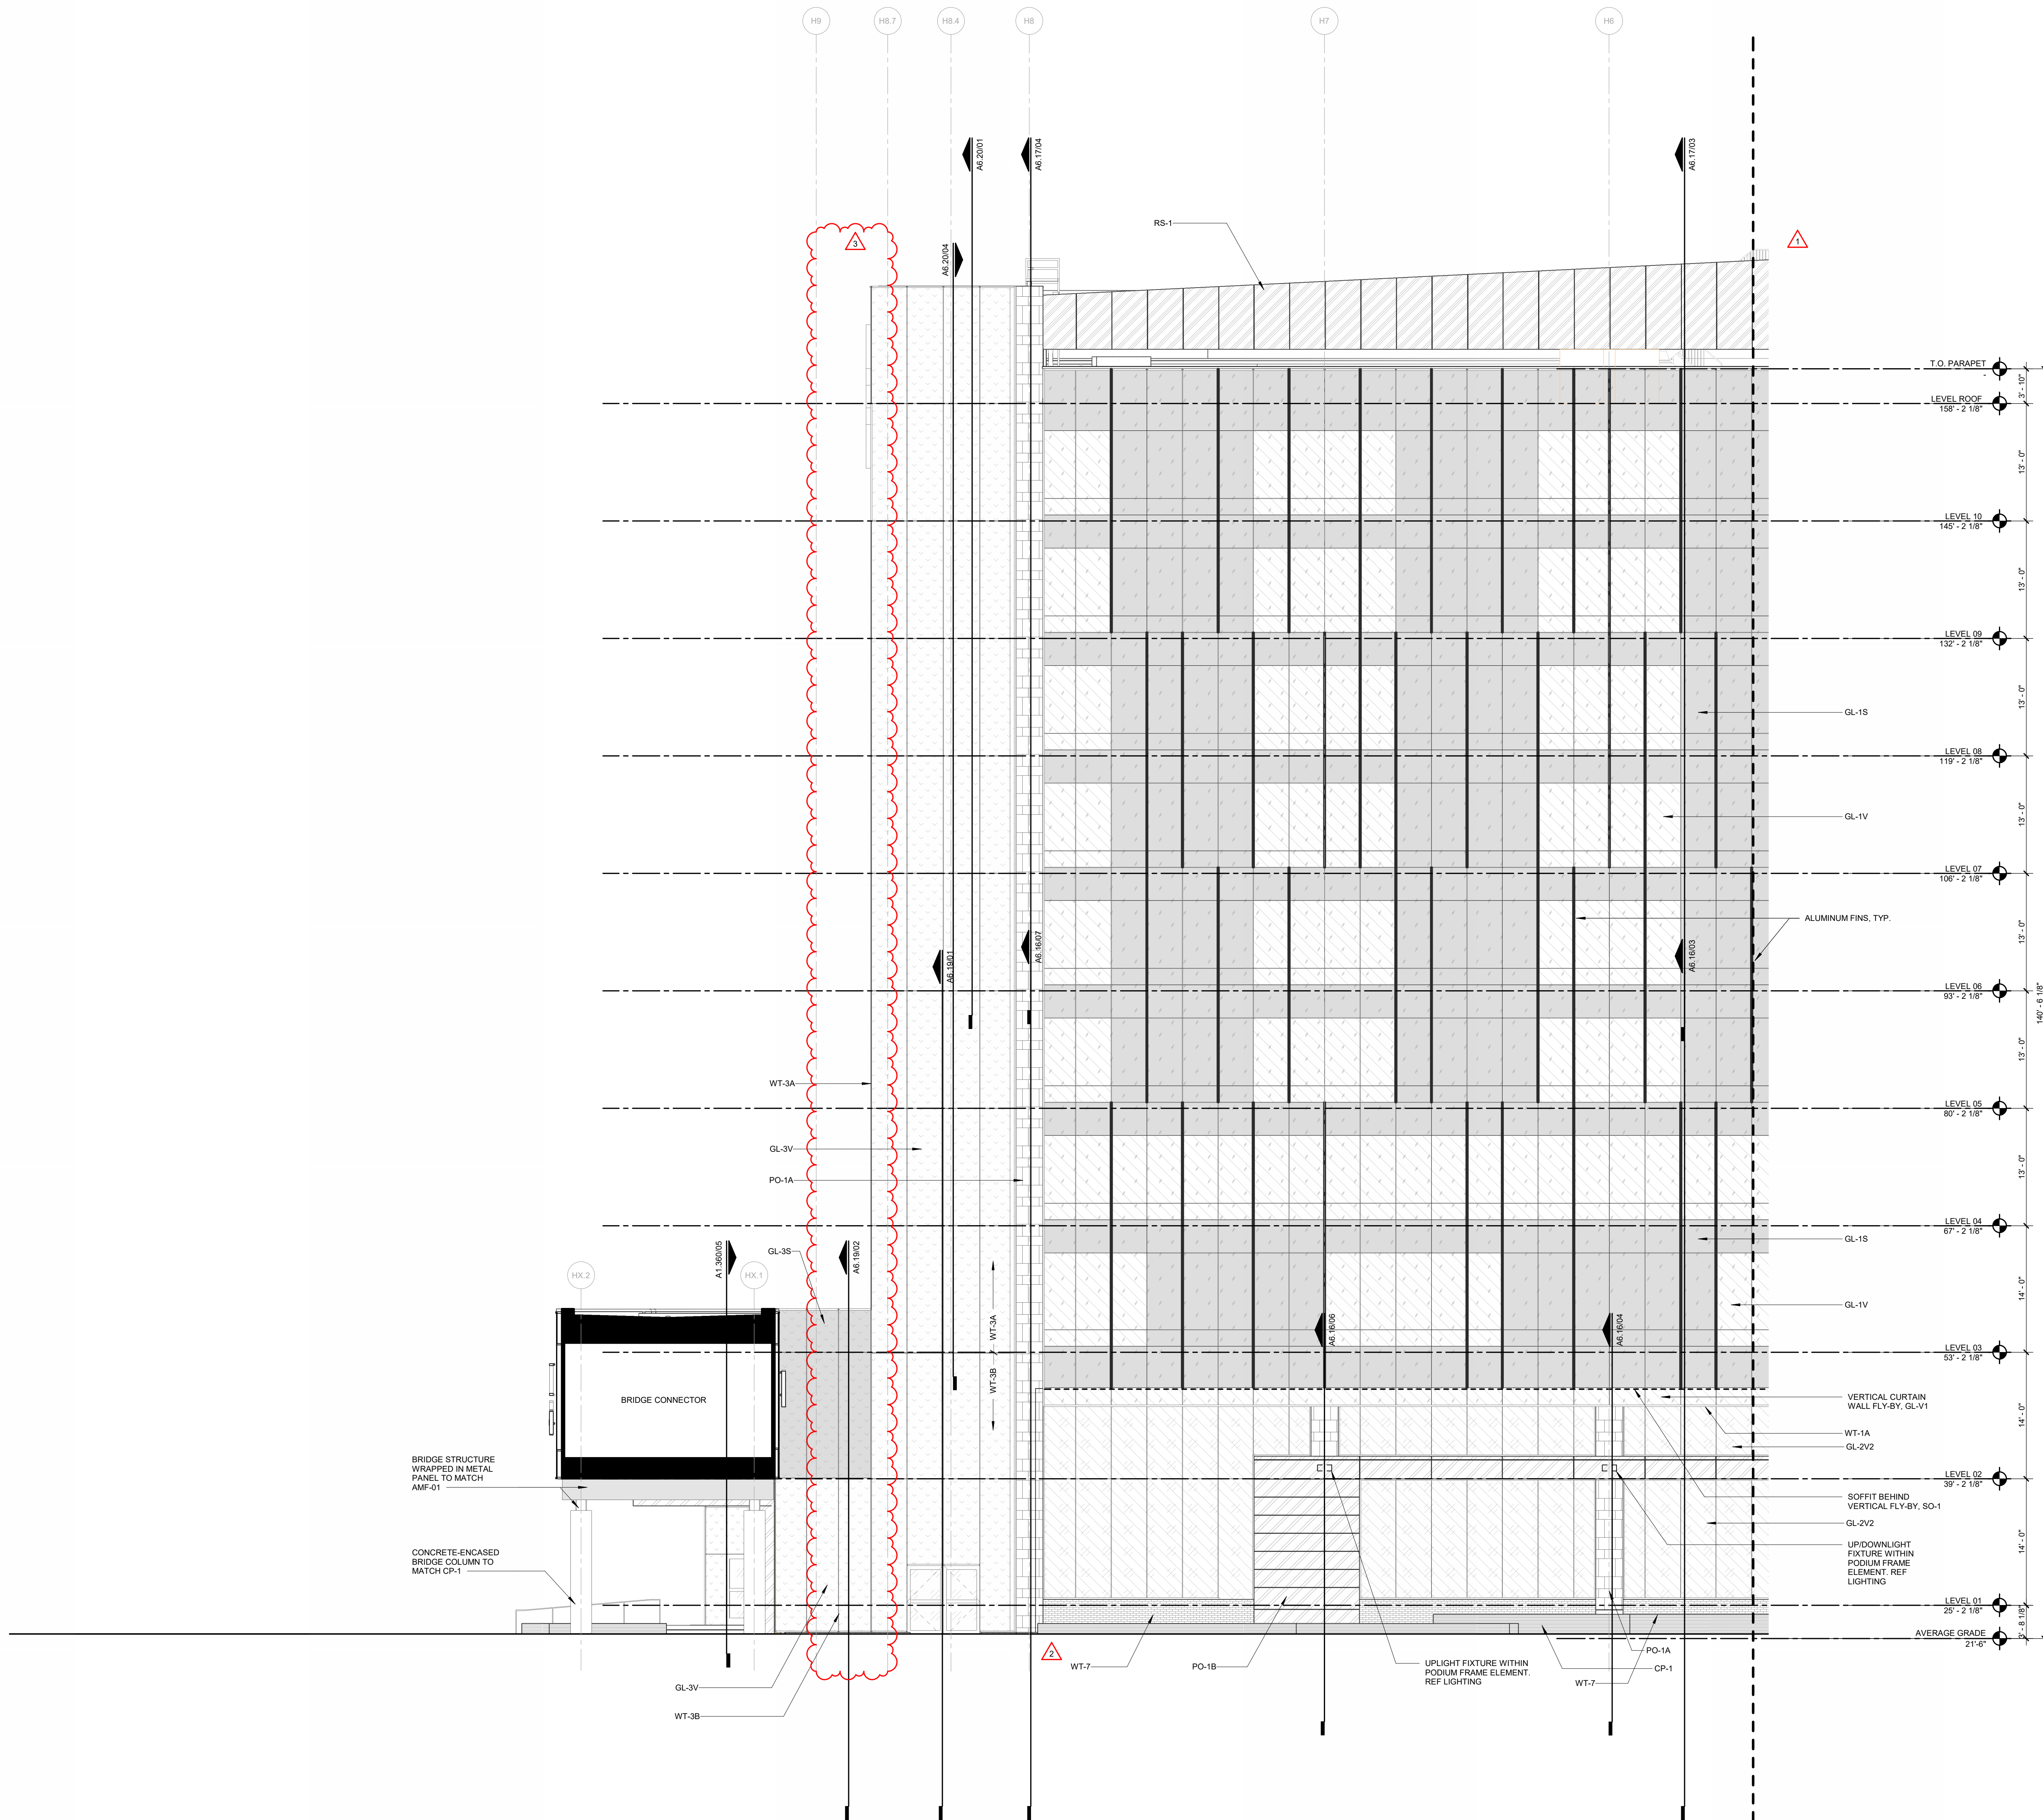


01 PARTIAL BUILDING ELEVATION - EAST
1/8" = 1'-0"

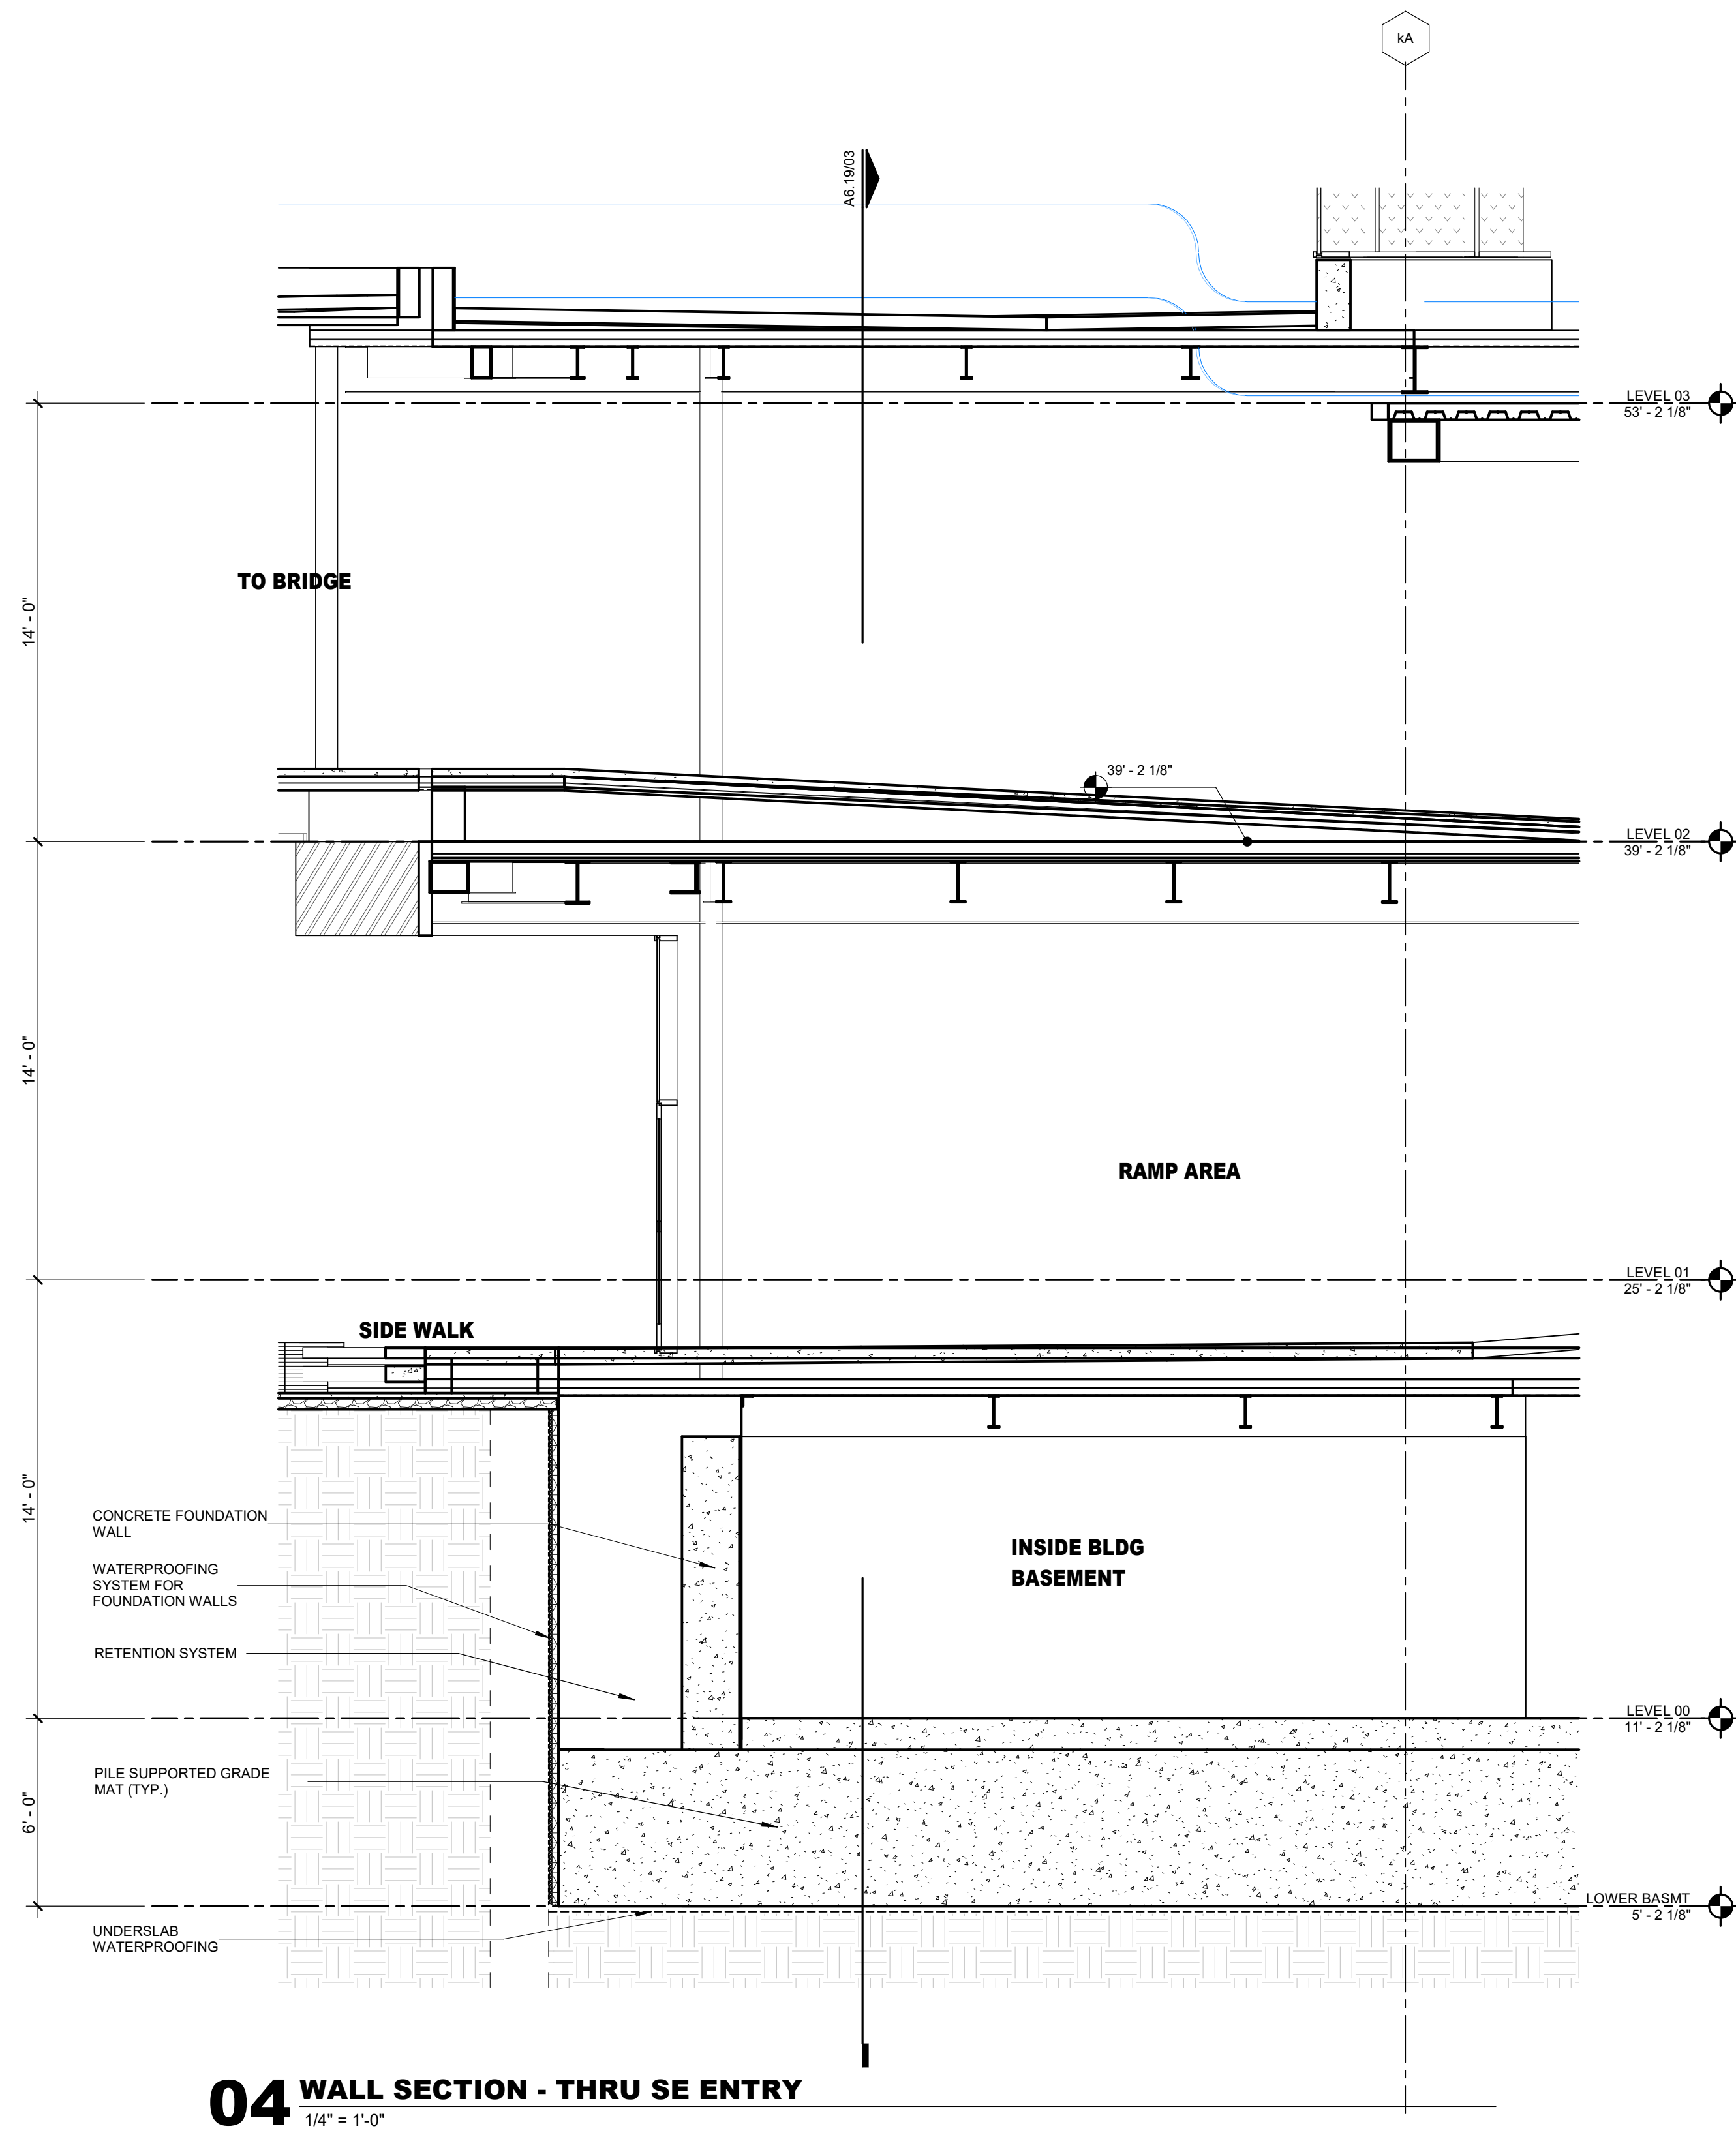


04 WALL SECTION - THRU SE ENTRY

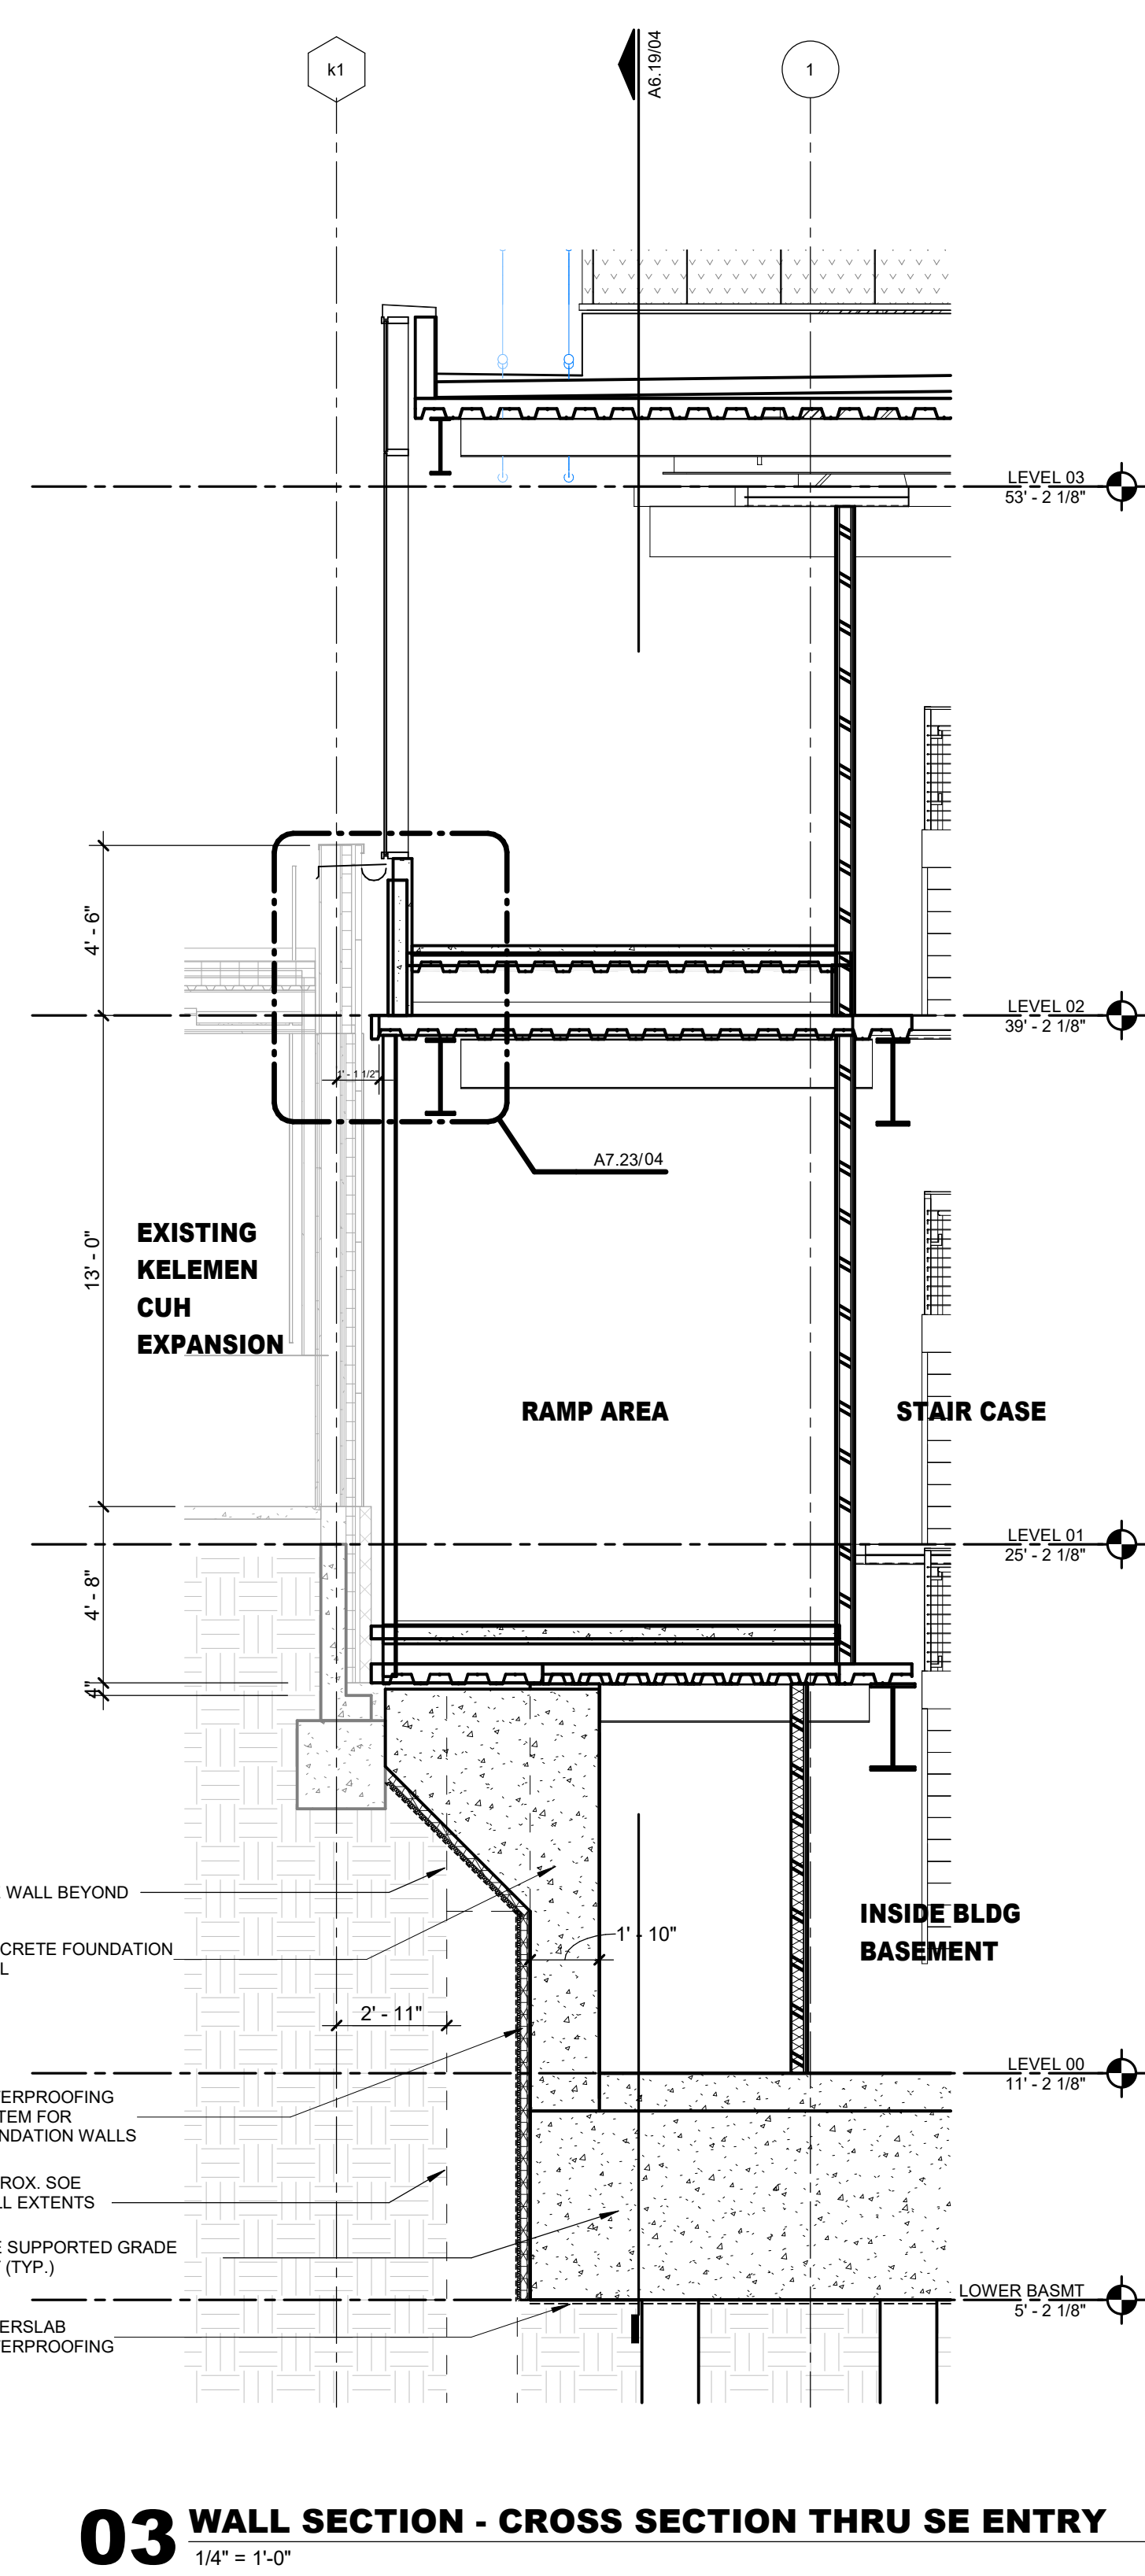


03 WALL SECTION - CROSS SECTION THRU SE ENTRY

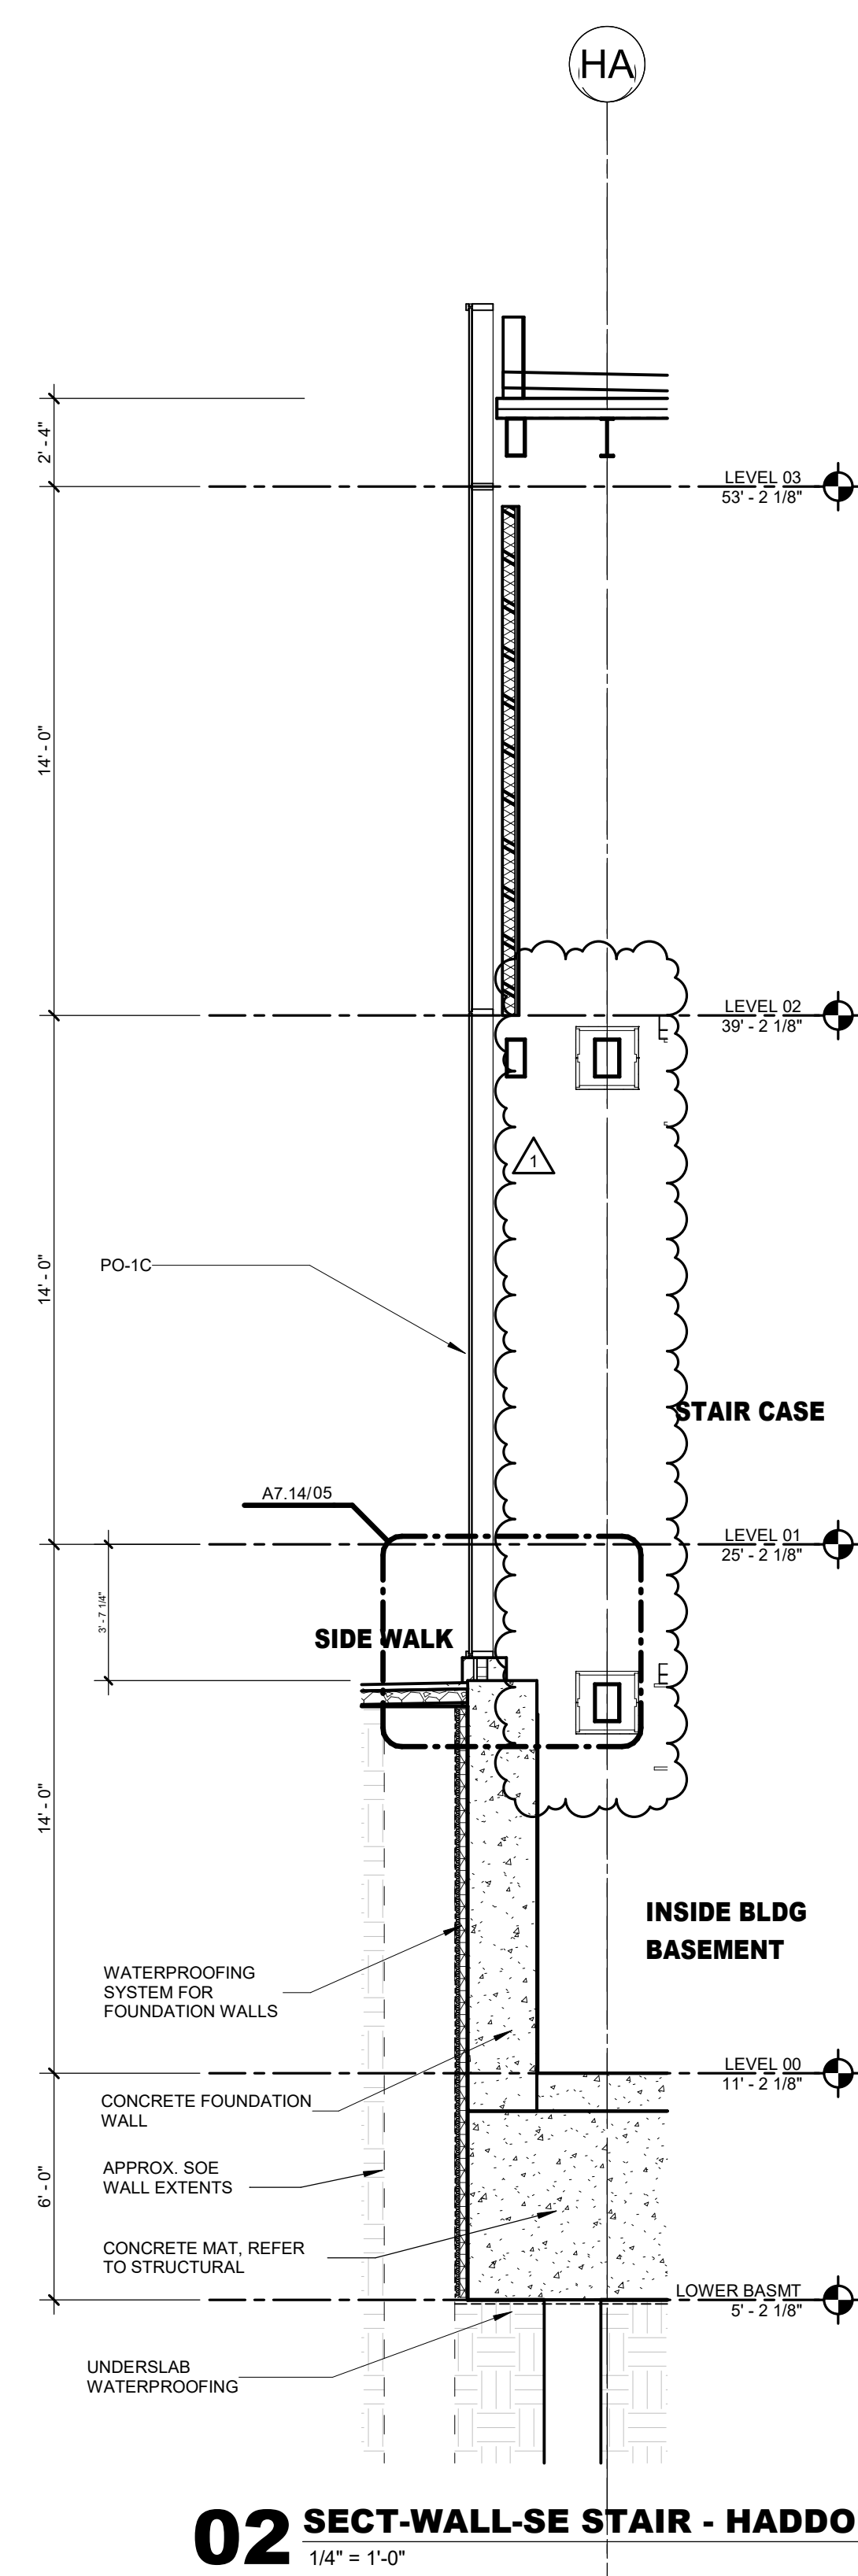


02 SECT-WALL-SE STAIR - HADDON - 2
1/4" = 1'-0"

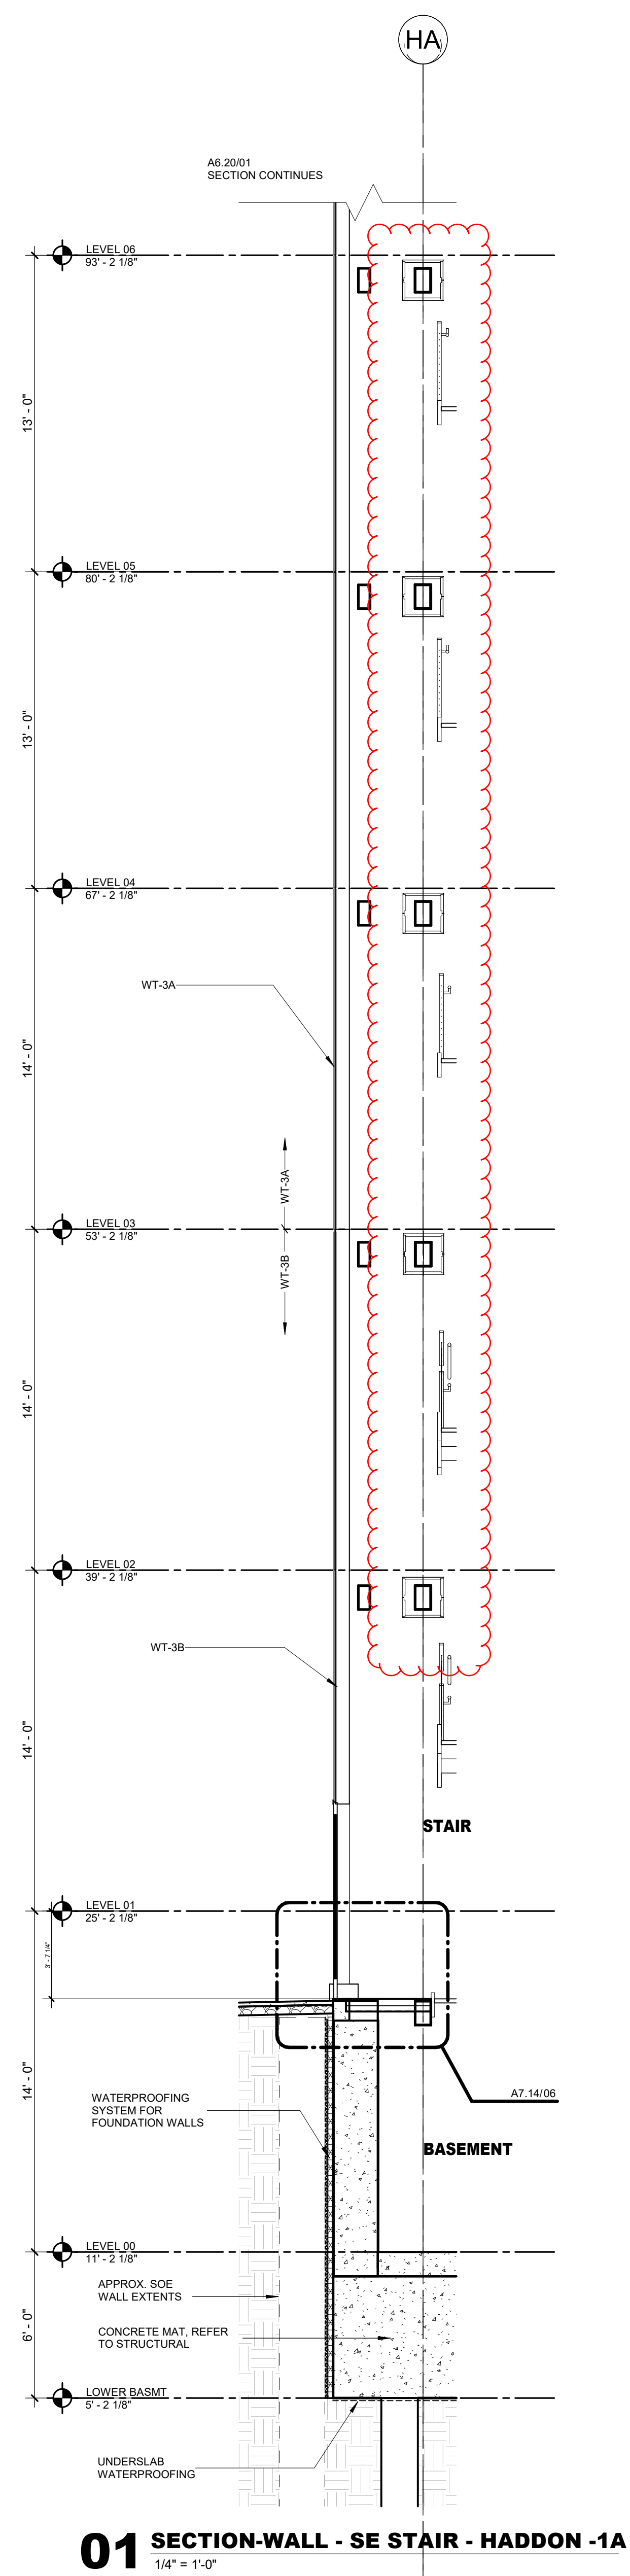


01 SECTION-WALL - SE STAIR - HADDON -1A
1/4" = 1'-0"

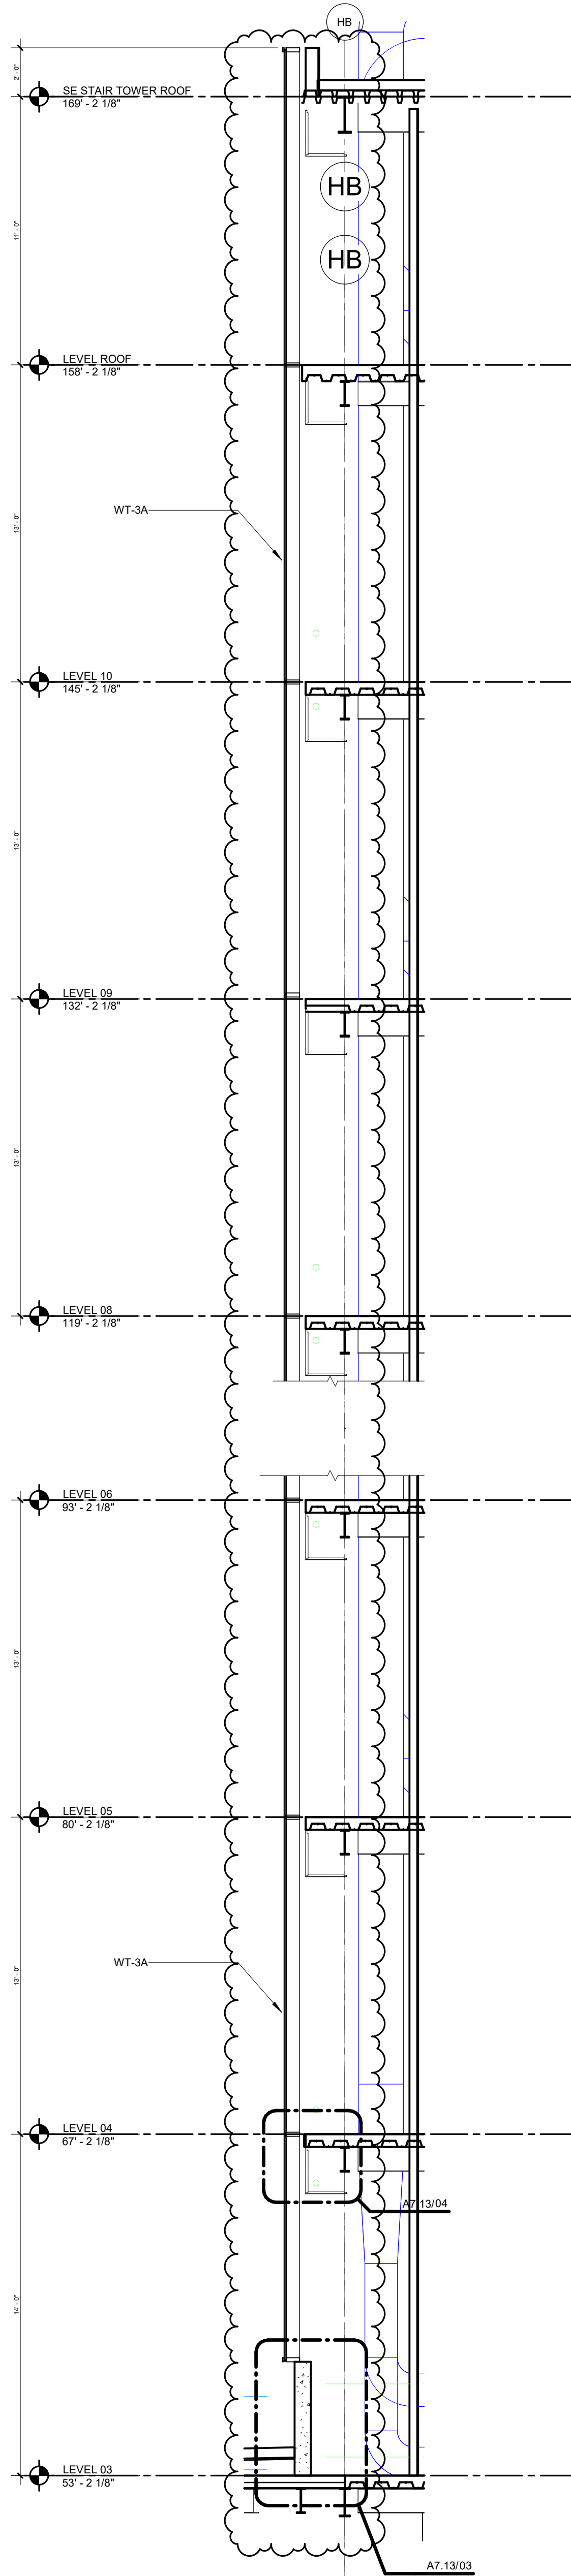


04 SECT-WALL-SE STAIR - W
1/4" = 1'-0"

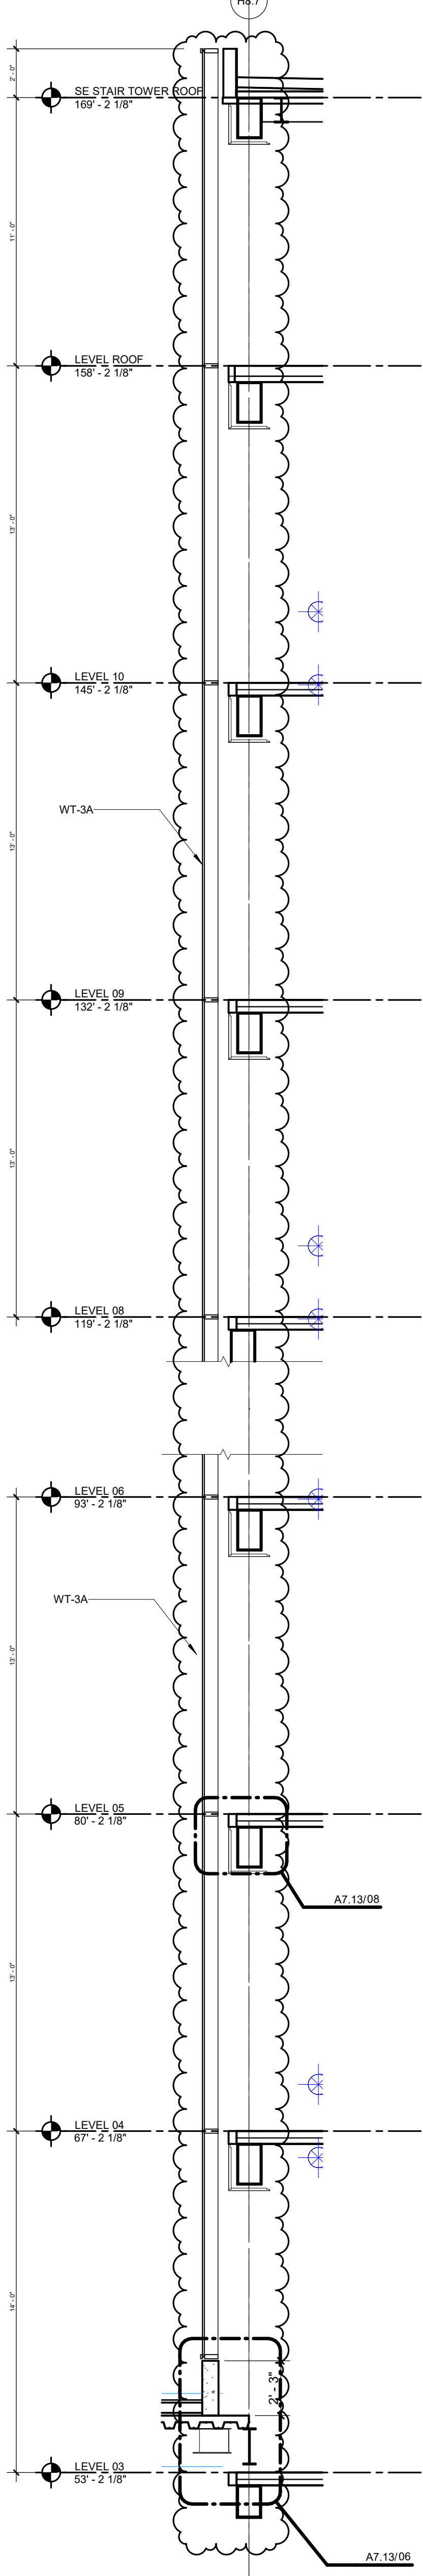

03 SECT-WALL-SE STAIR - S THRU LANDING
1/4" = 1'-0"

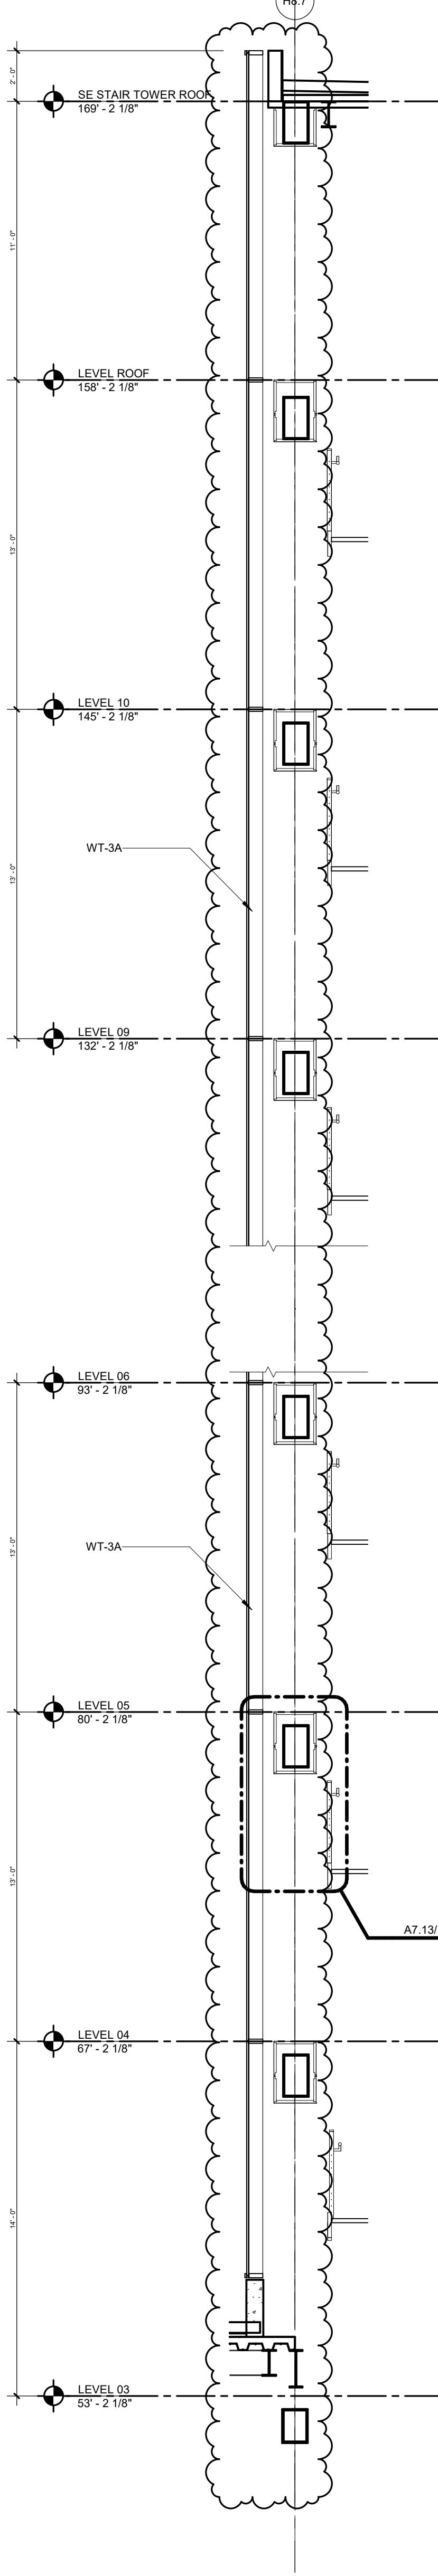

02 SECT-WALL-SE STAIR - S
1/4" = 1'-0"

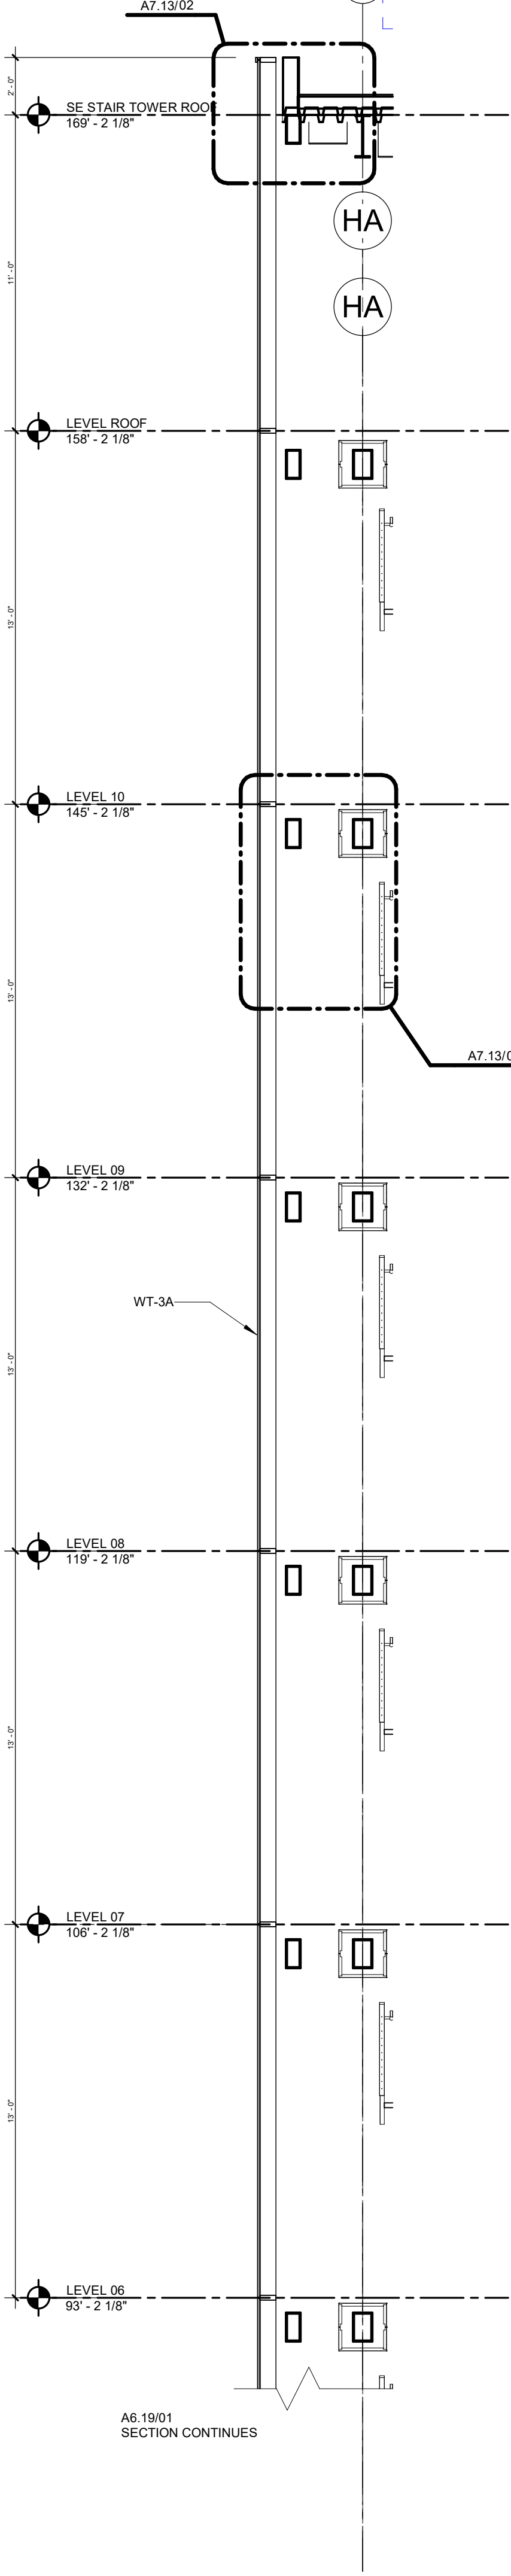

01 SECTION-WALL - SE STAIR - HADDON -1B
1/4" = 1'-0"


RESERVE FOR DCA STAMP



ARCHITECT
HKS, P.C.
1250 I (EYE) STREET NW, SUITE 600
WASHINGTON, DC 20005
ASSOCIATE ARCHITECT / INTERIOR DESIGNER
ARRAY
1 WEST ELM STREET, SUITE 500
CONSHOHOCKEN, PA 19028
STRUCTURAL ENGINEER
O'DONNELL & NACCARATO
701 MARKET ST., #6000
PHILADELPHIA, PA 19106
MEP-FP / LOW VOLTAGE ENGINEER
BR+A CONSULTING ENGINEERS
2401 WALNUT ST SUITE 701
PHILADELPHIA, PA 19103
HIGHLAND ASSOCIATES
102 HIGHLAND AVE
CLARKS SUMMIT, PA 18411



OWNER
COOPER UNIVERSITY HEALTHCARE
1 COOPER PLAZA
CAMDEN, NJ 08103
PROJECT MANAGER
PURE PM
2926 RICHMOND STREET
PHILADELPHIA, PA 19134
CIVIL ENGINEER / LANDSCAPE
LANGAN
1818 MARKET STREET, SUITE 3300
PHILADELPHIA, PA 19103
SEAL & SIGNATURE

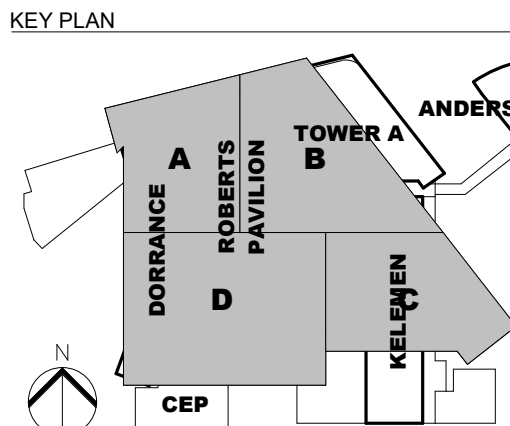


REVISION	NO.	DESCRIPTION	DATE
1	RFI 0416		11/14/2025

HKS PROJECT NUMBER
25695.100
DATE
10/15/2024
ISSUE
CORE & SHELL PERMIT SET
SHEET TITLE
WALL SECTIONS - SE STAIR


SHEET NO.

A6.20


BUILDING PERMIT NUMBER: 1111

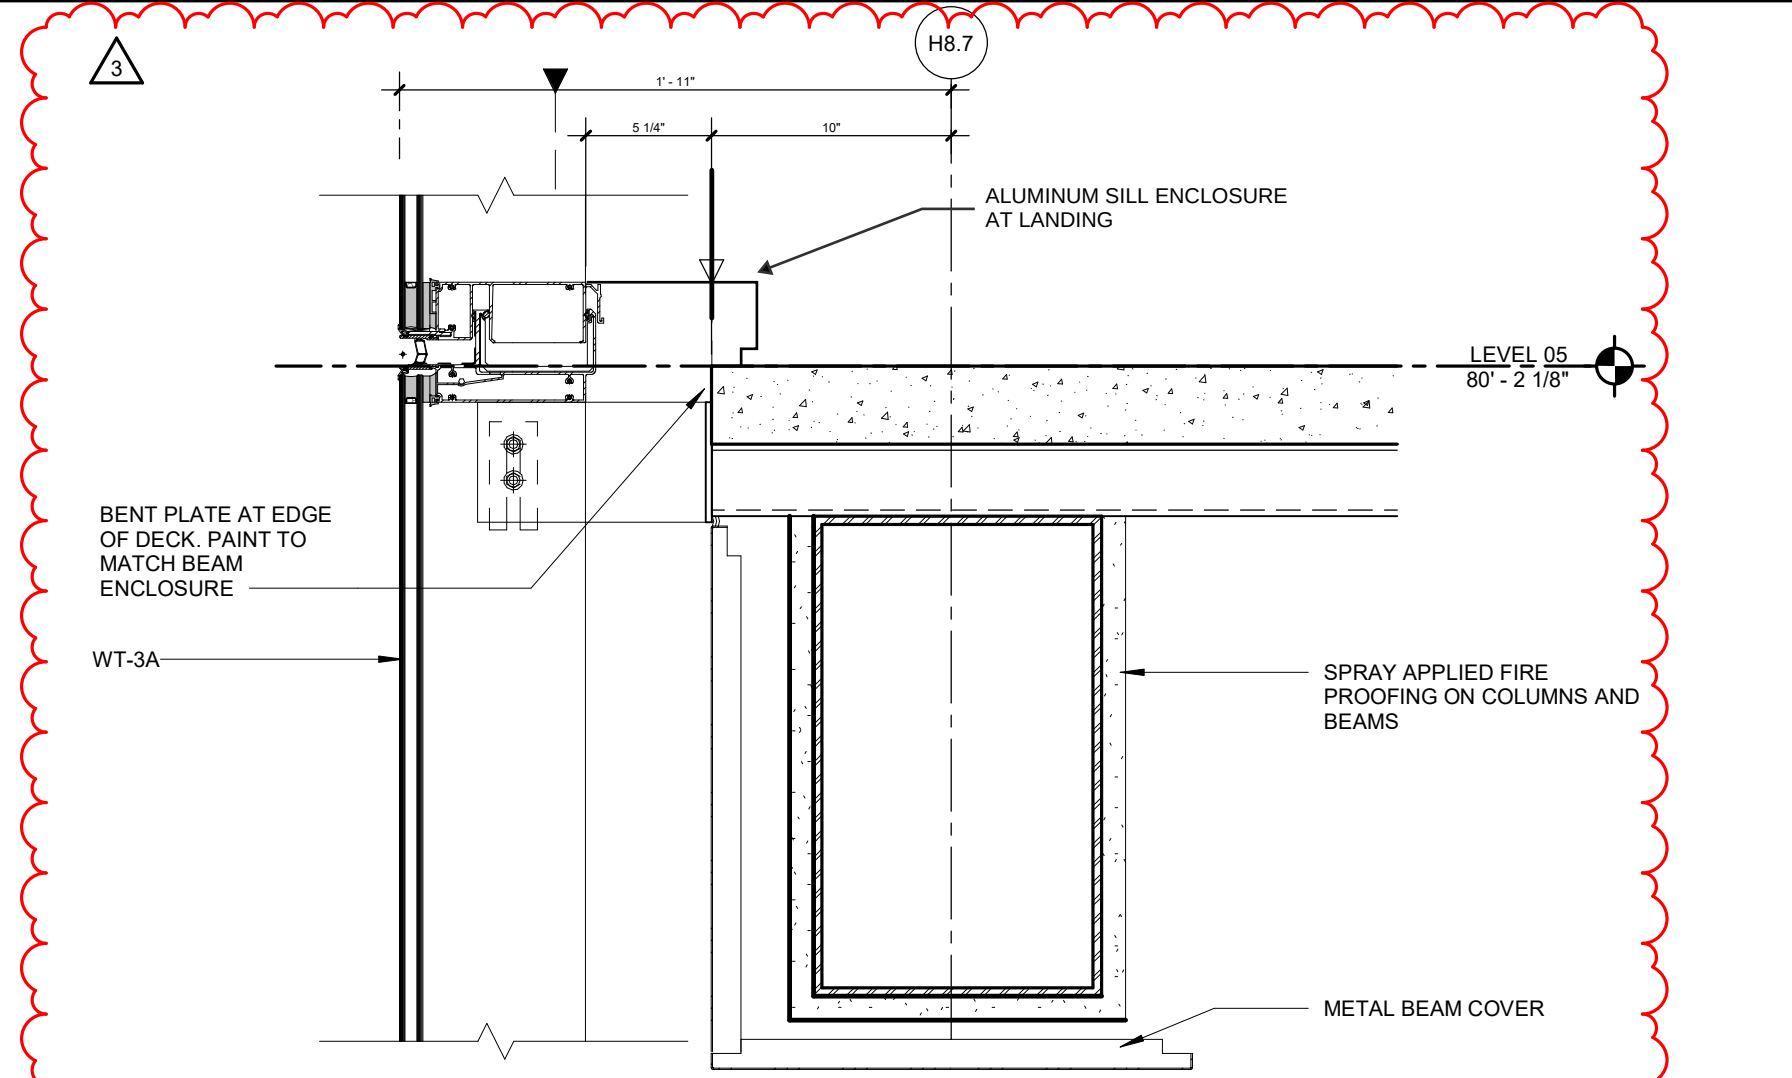


08 SECTION DTL - SE STAIR TOWER SOUTH CW TO SLAB
 1 1/2" = 1'-0"

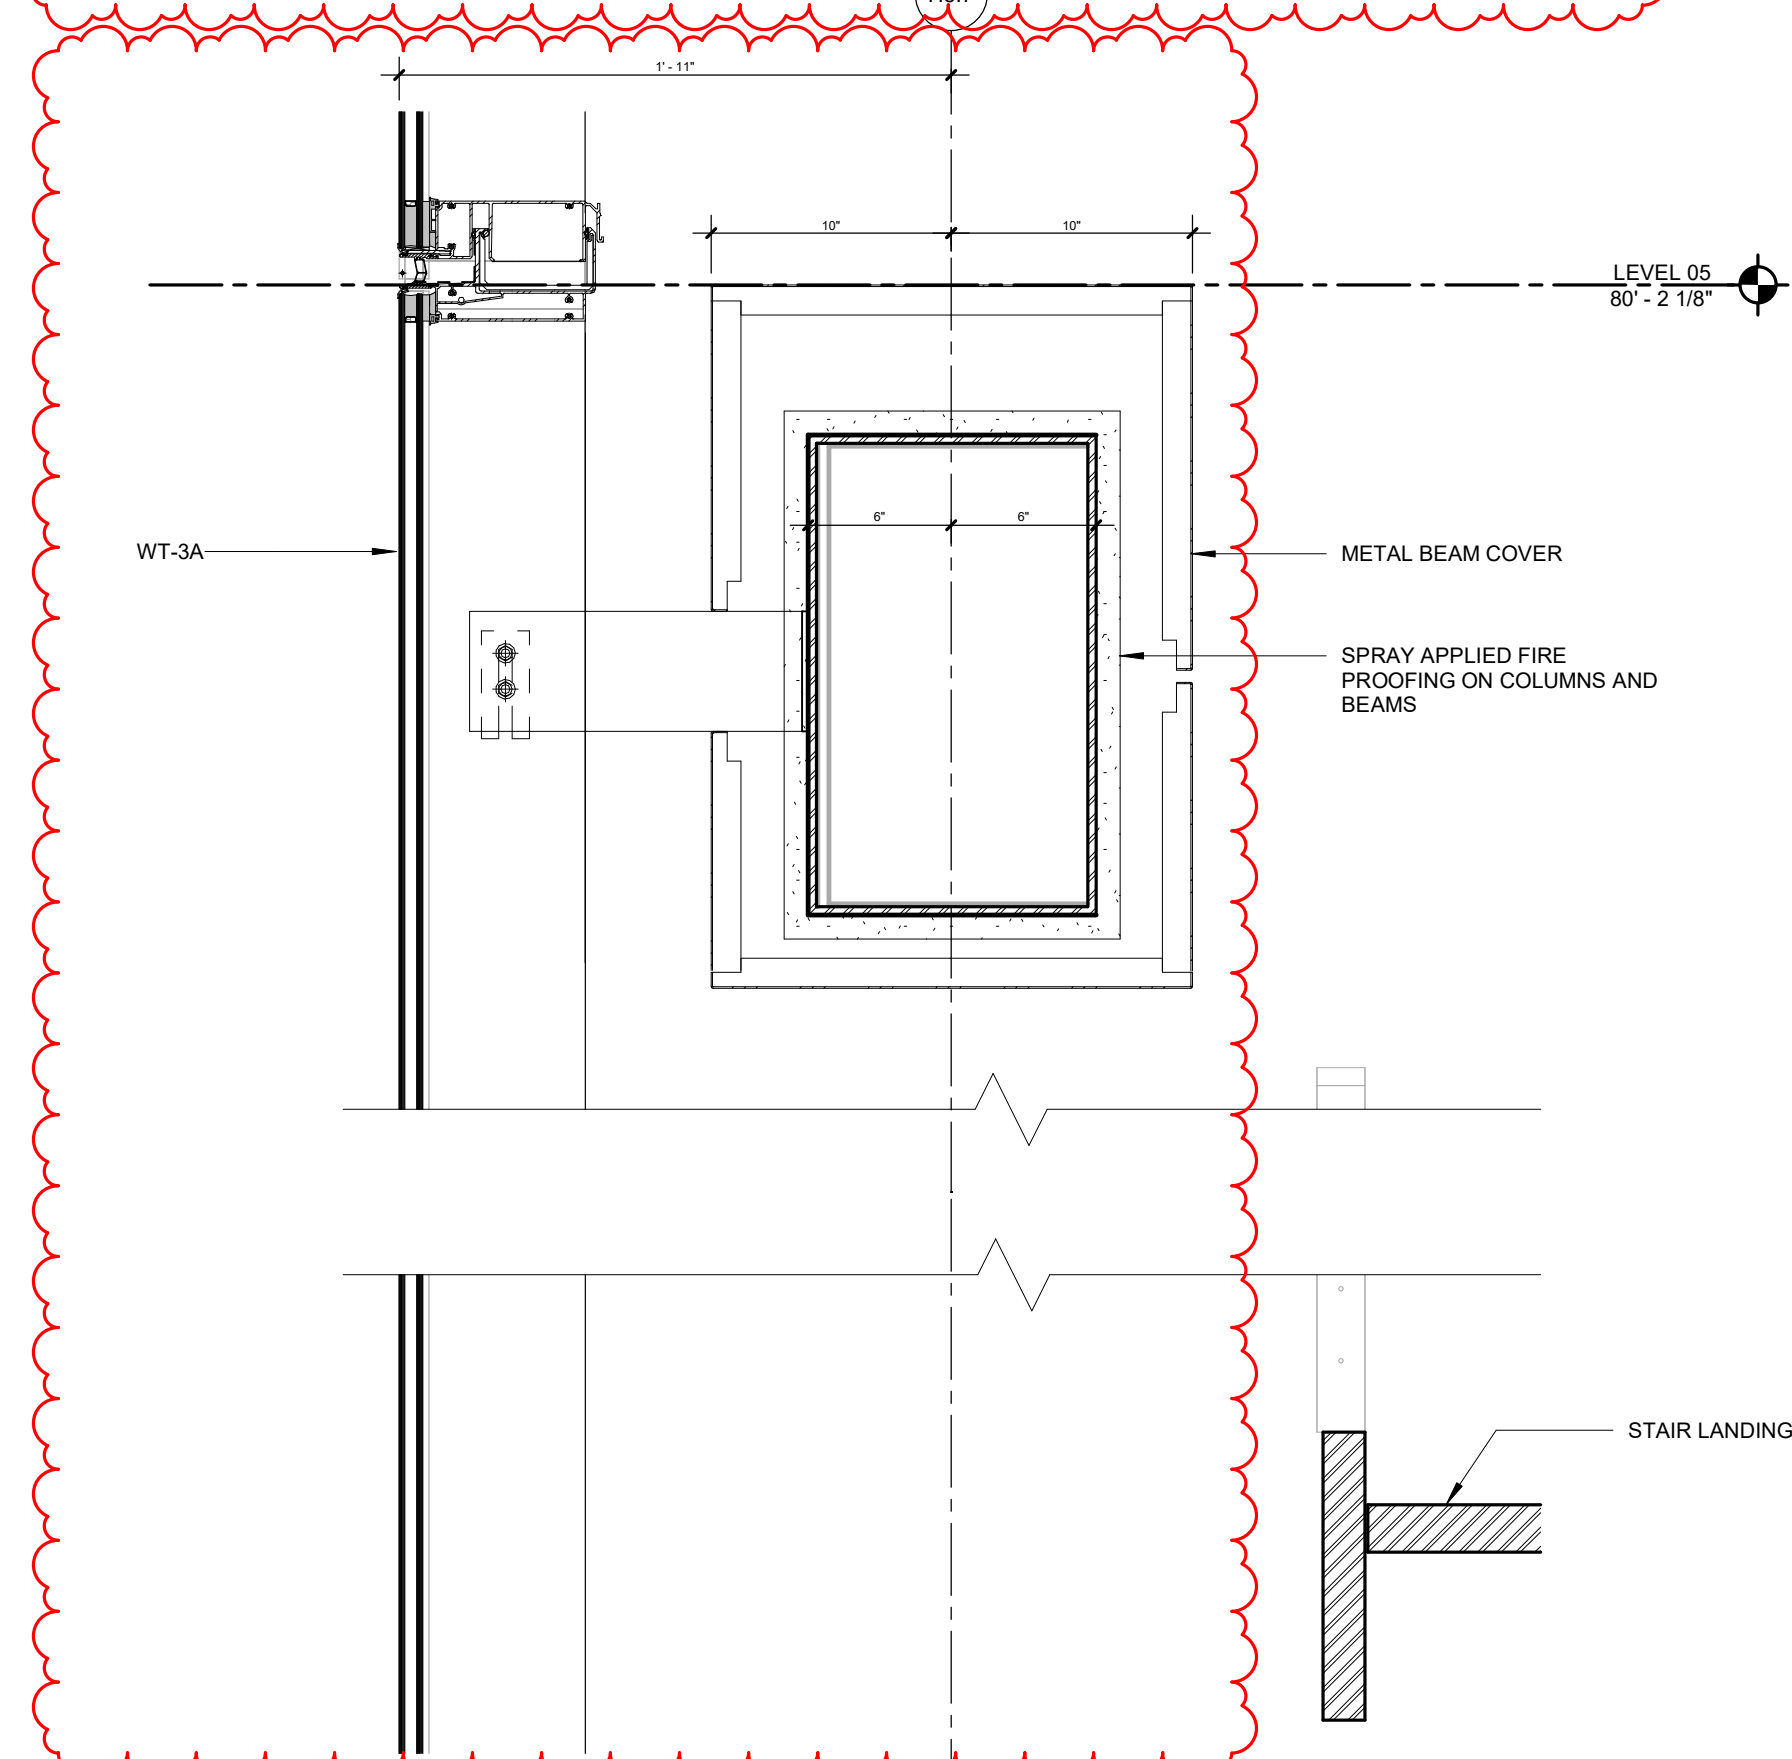


07 SECTION DTL - SE STAIR TOWER SOUTH CW TO STAIR INTERMEDIATE LANDING
 1 1/2" = 1'-0"

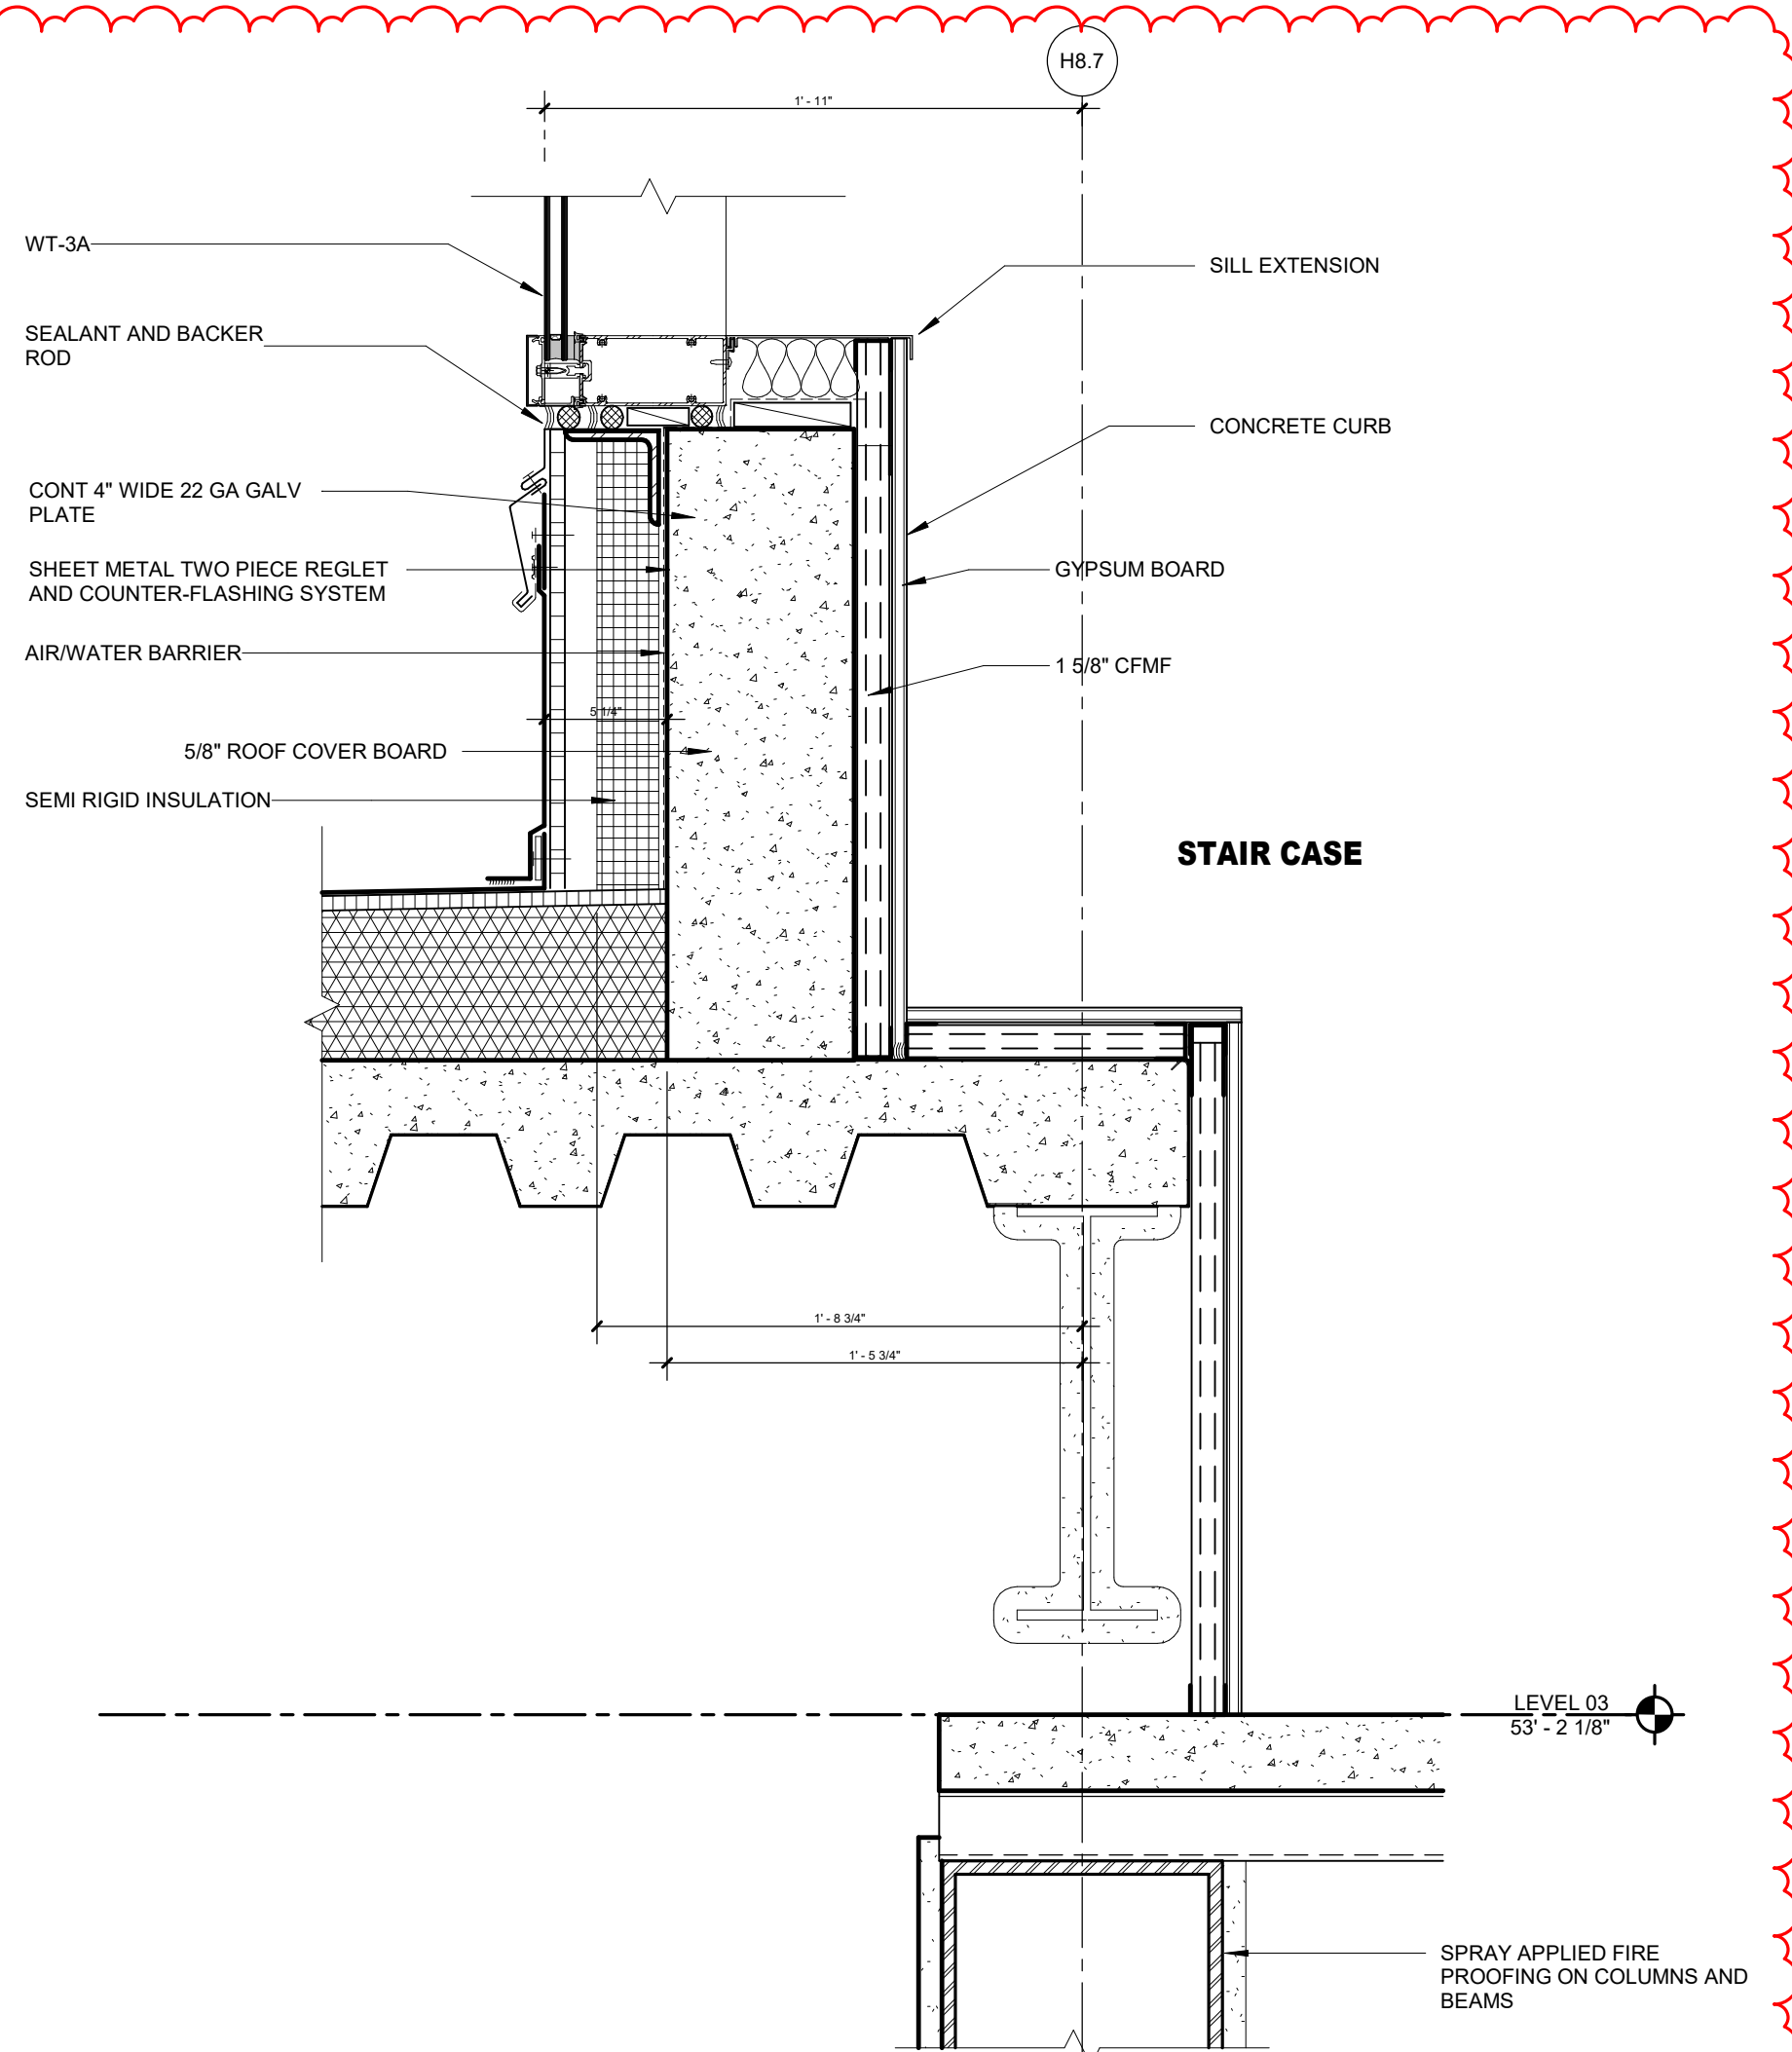


06 SECTION DTL - SE STAIR TOWER SOUTH CW TO BRIDGE ROOF
 1 1/2" = 1'-0"

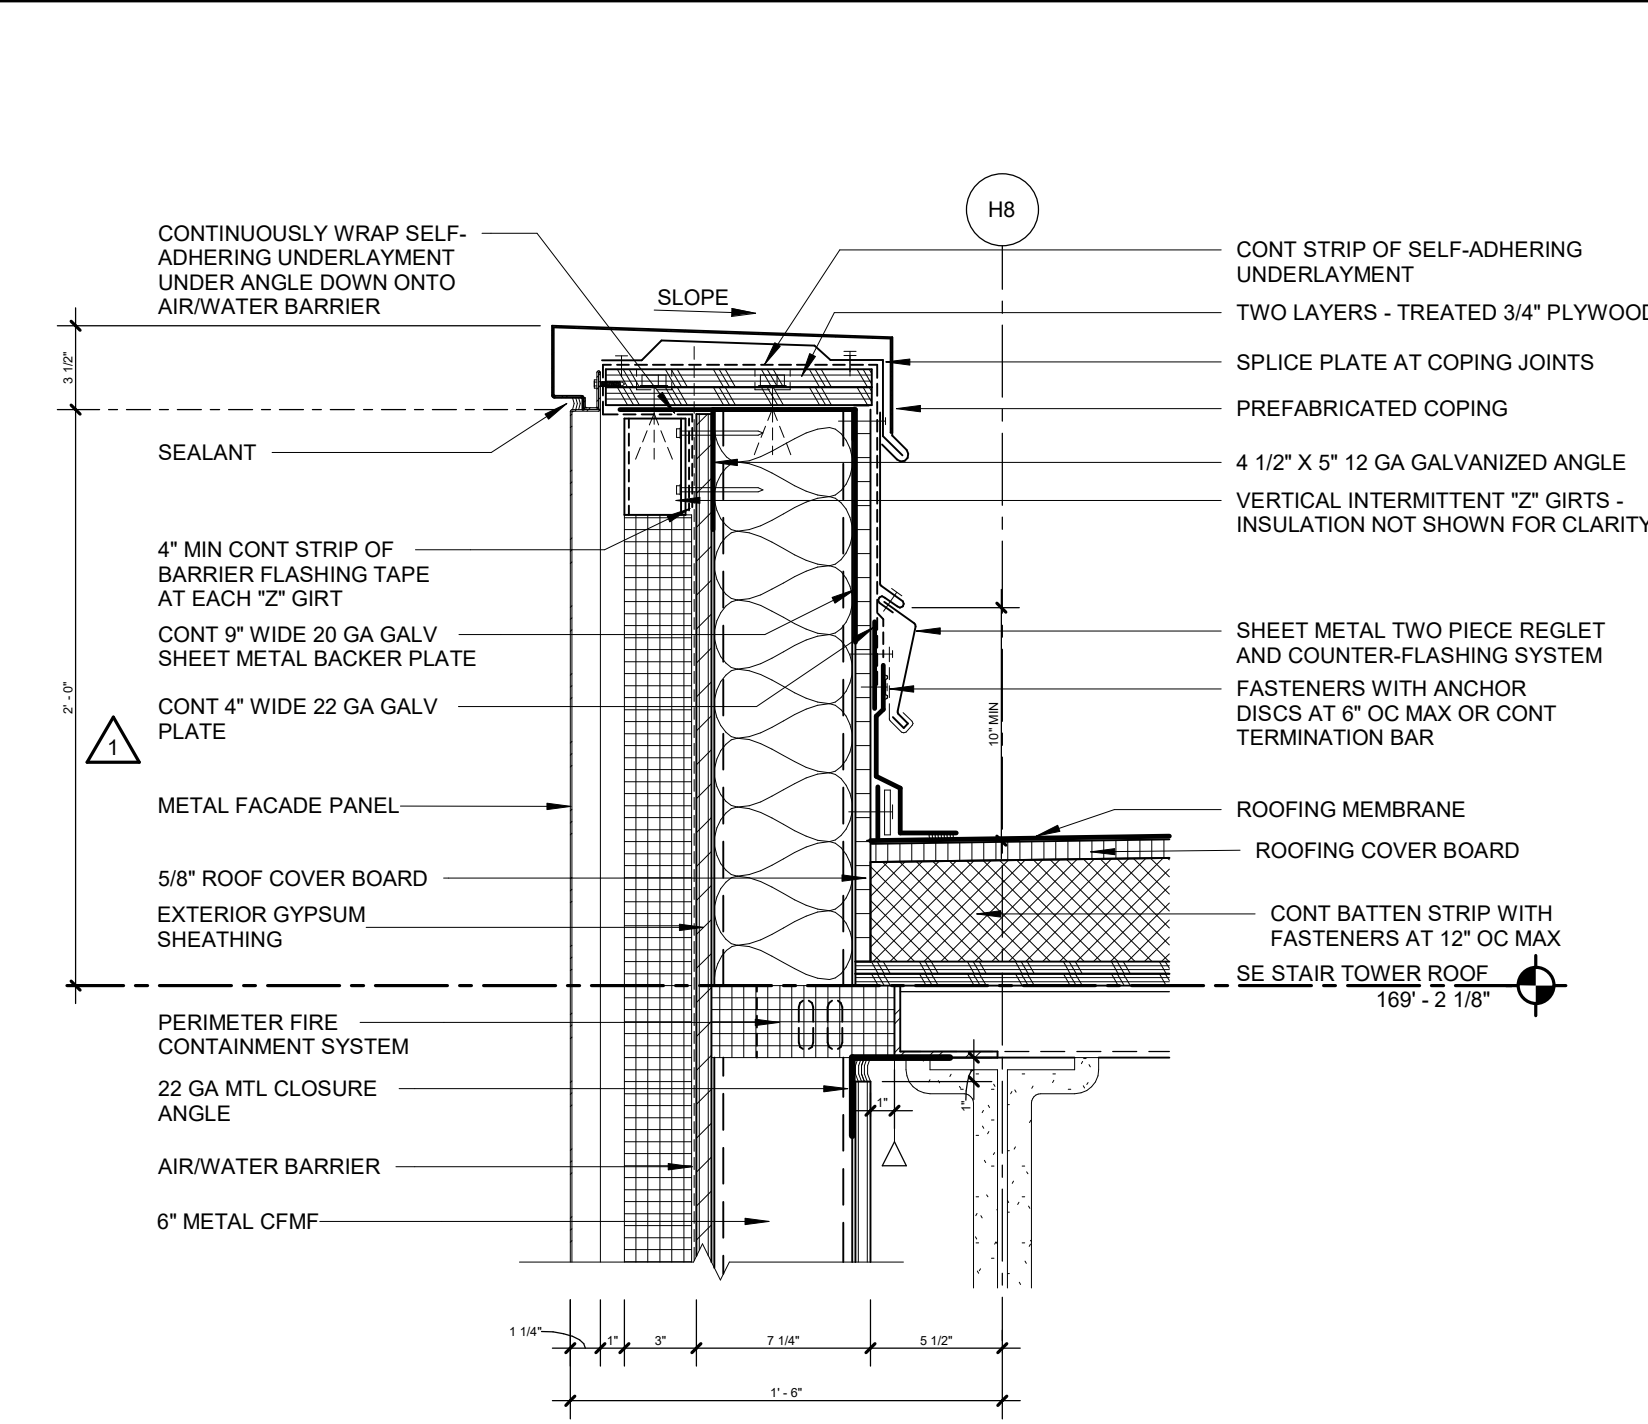


05 SECTION DTL - SE STAIR TOWER EAST NORTH METAL PANEL WALL PARAPET
 1 1/2" = 1'-0"

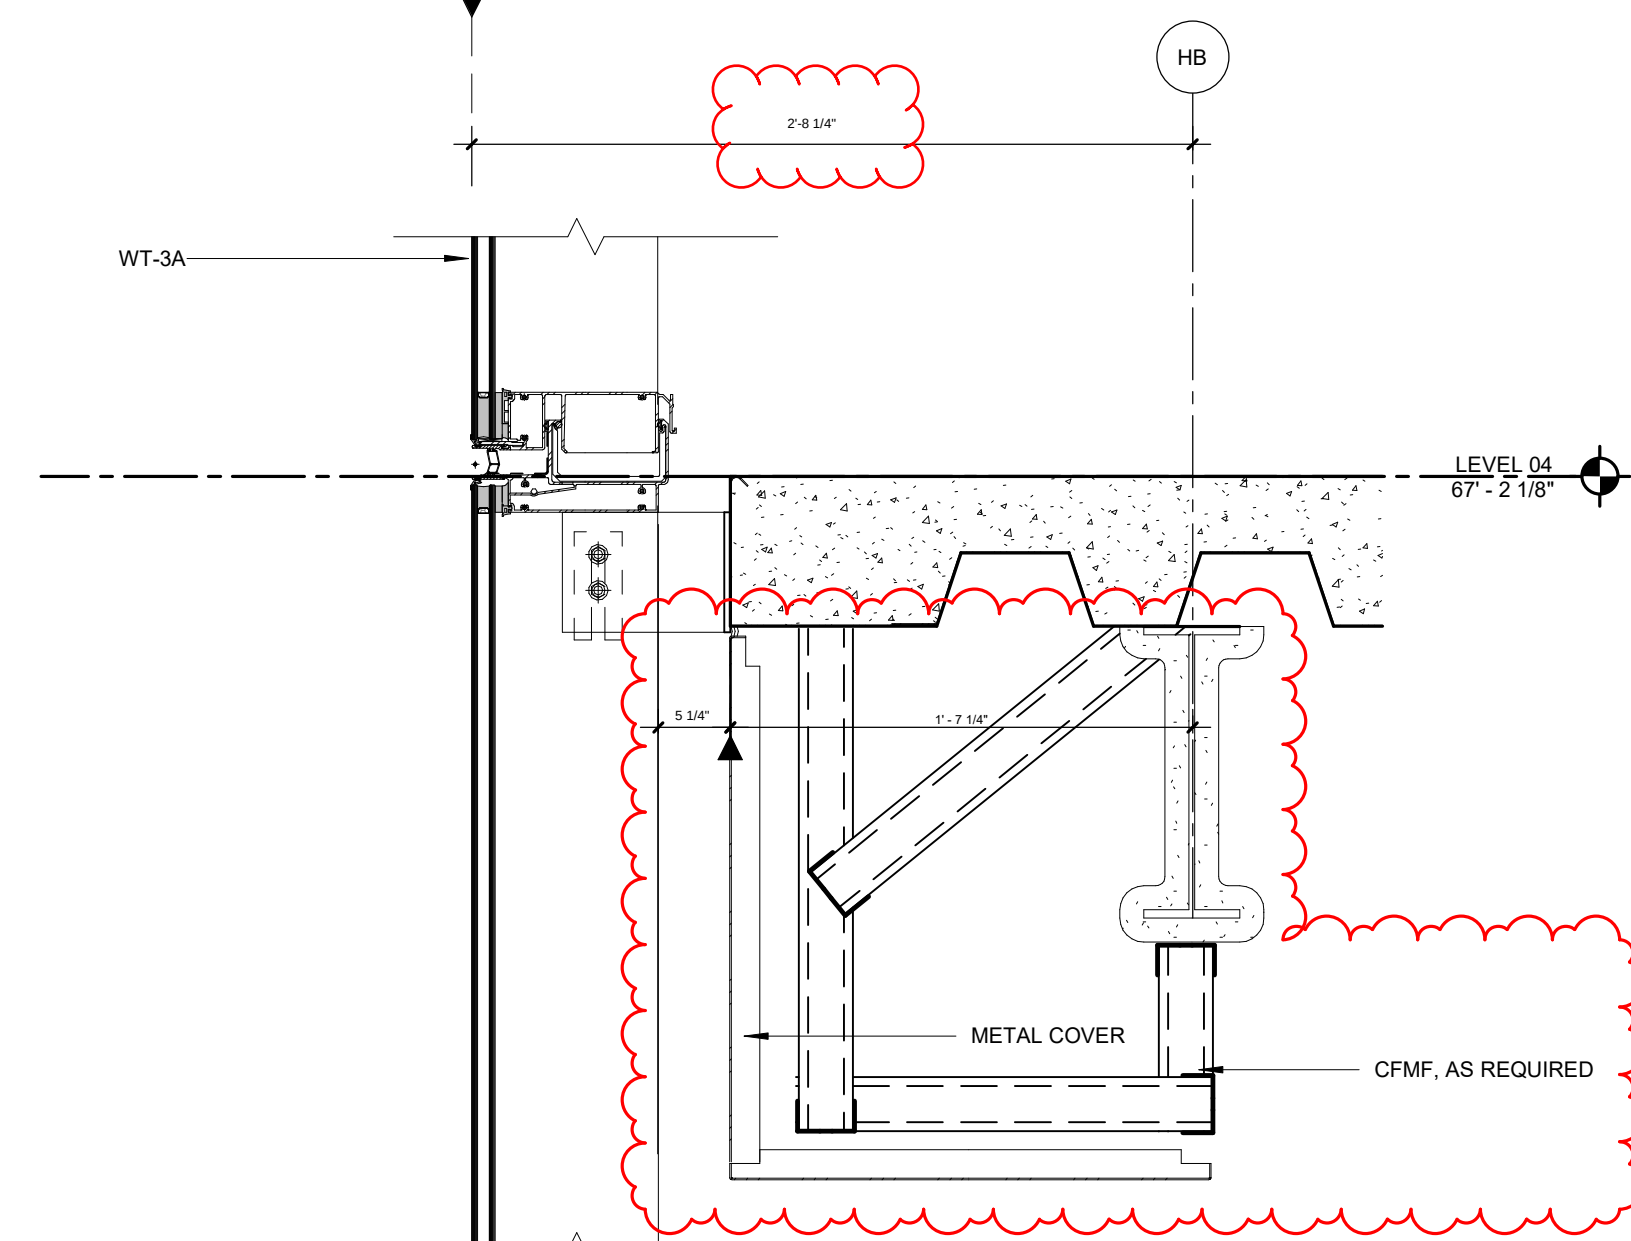


04 SECTION DTL - SE STAIR TOWER WEST CW TO LANDING
 1 1/2" = 1'-0"

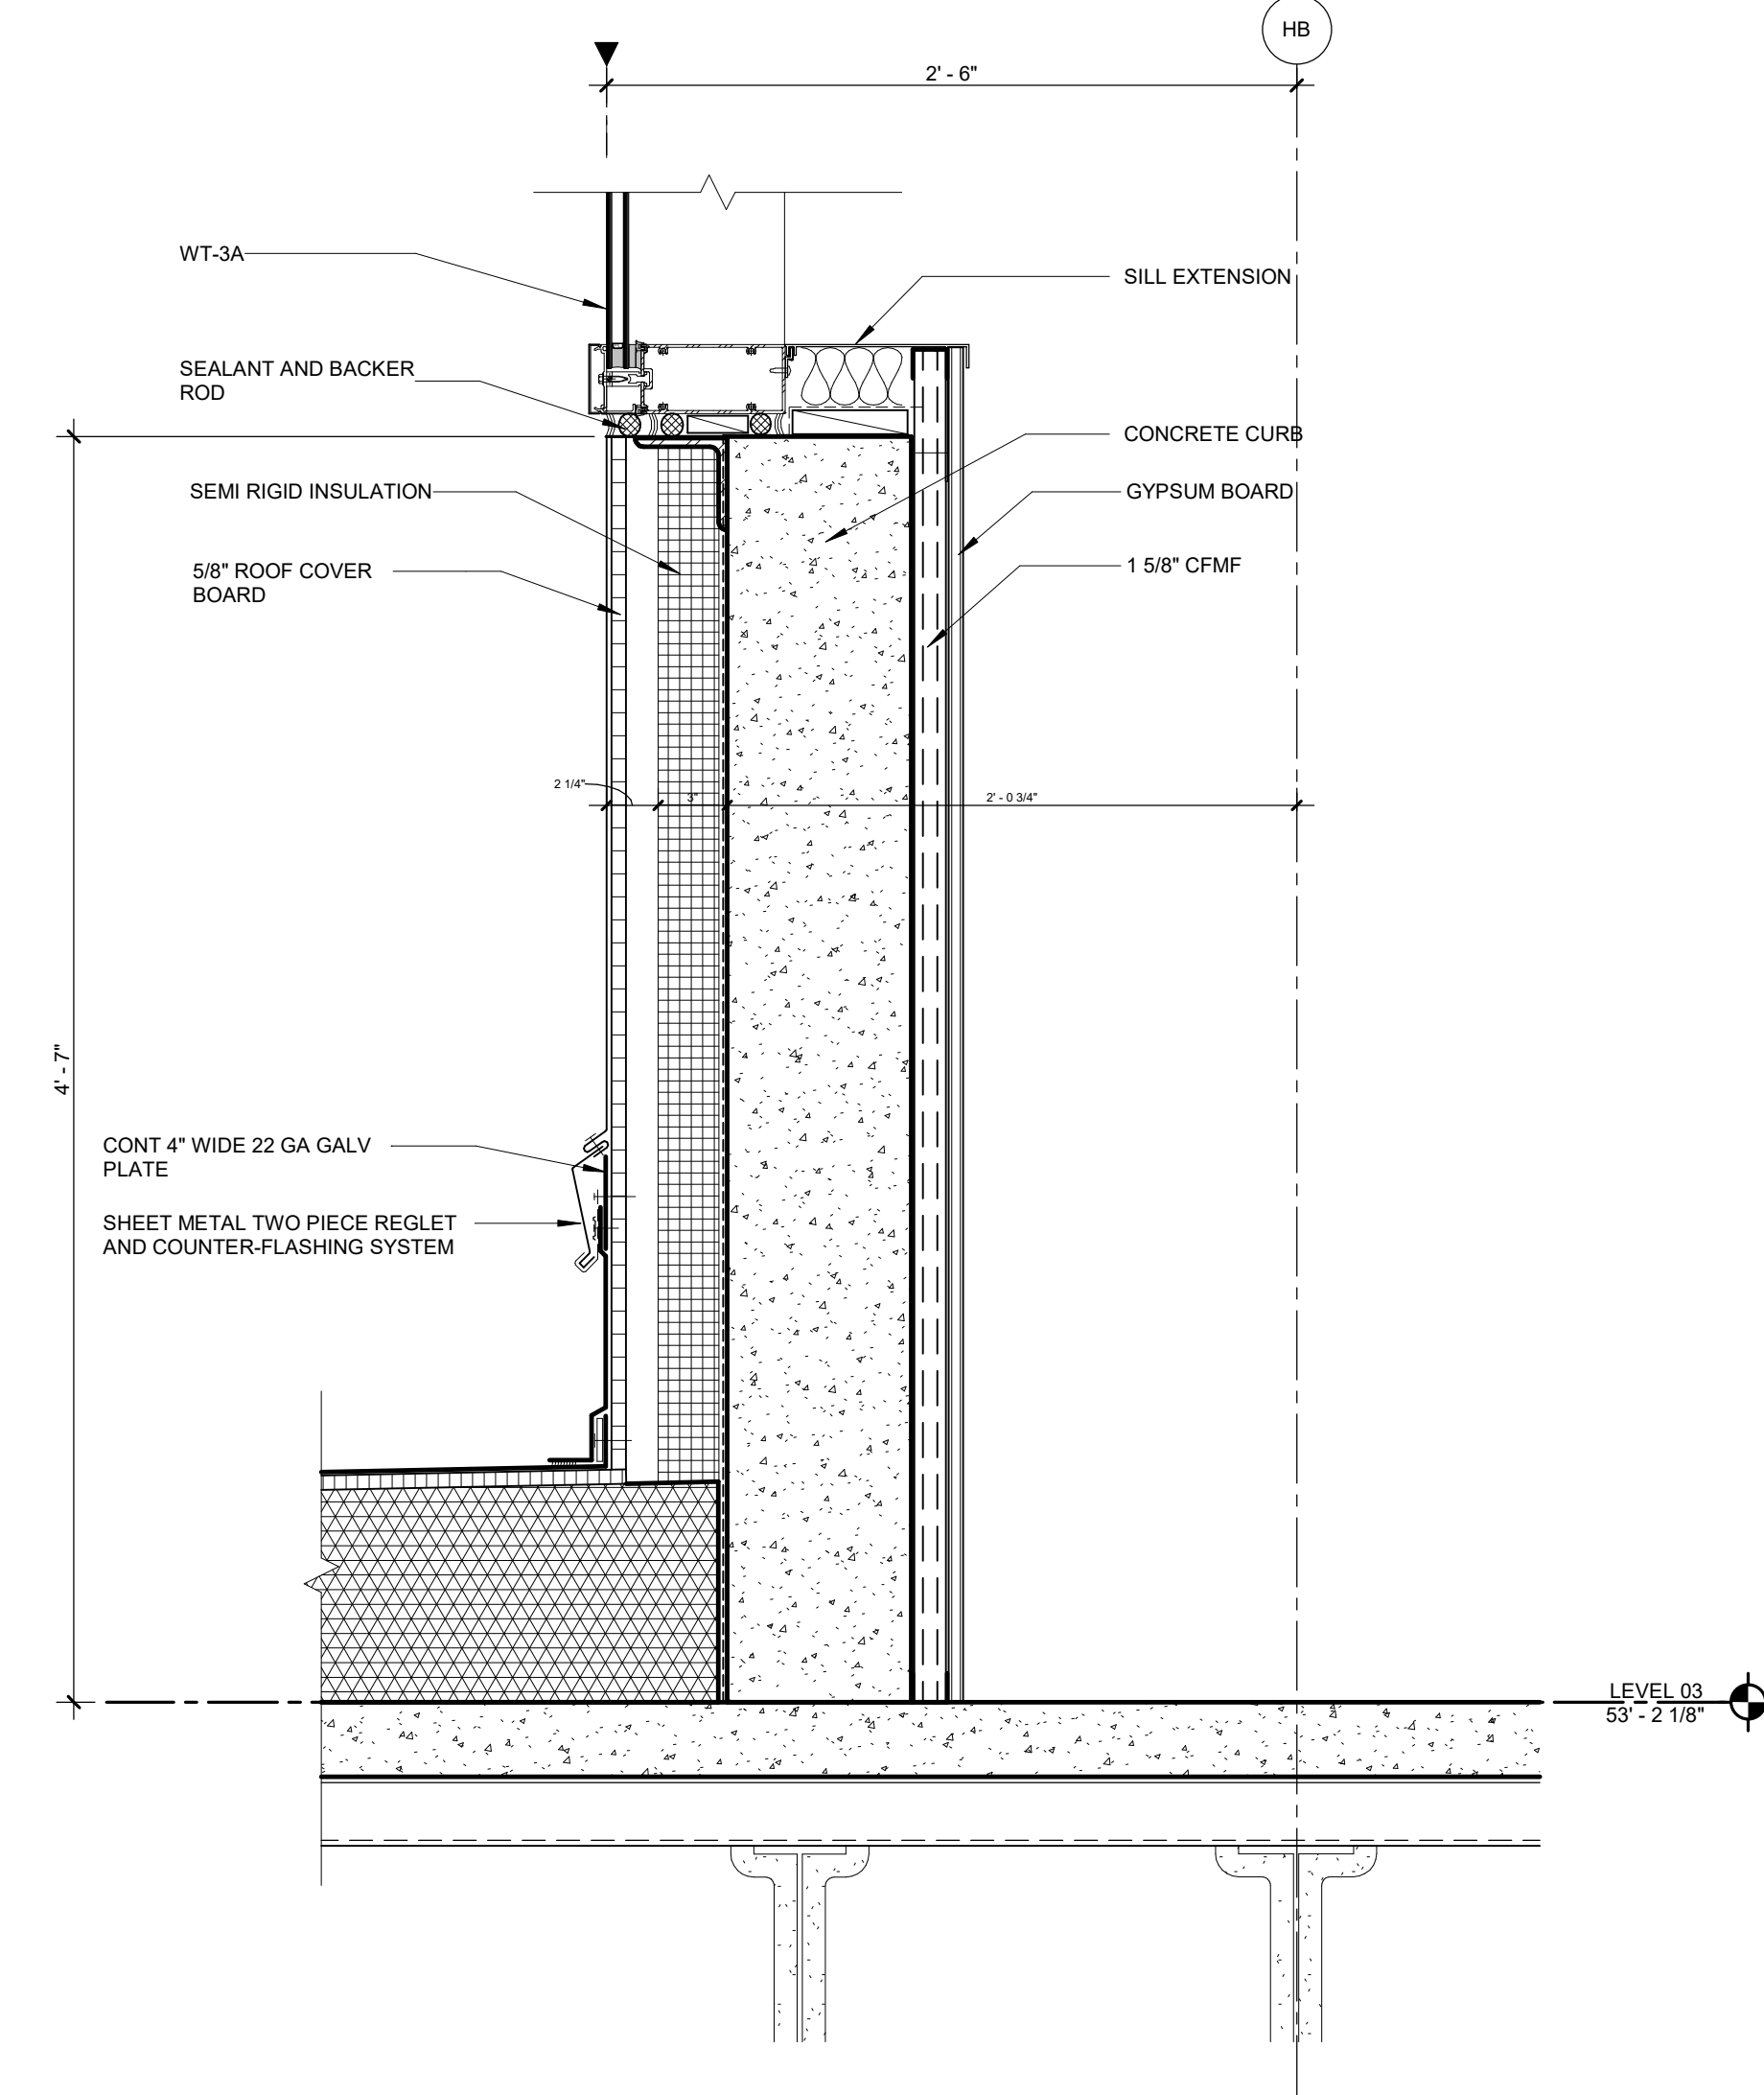

03 SECTION DTL - SE STAIR TOWER WEST CW TO ROOF
 1 1/2" = 1'-0"

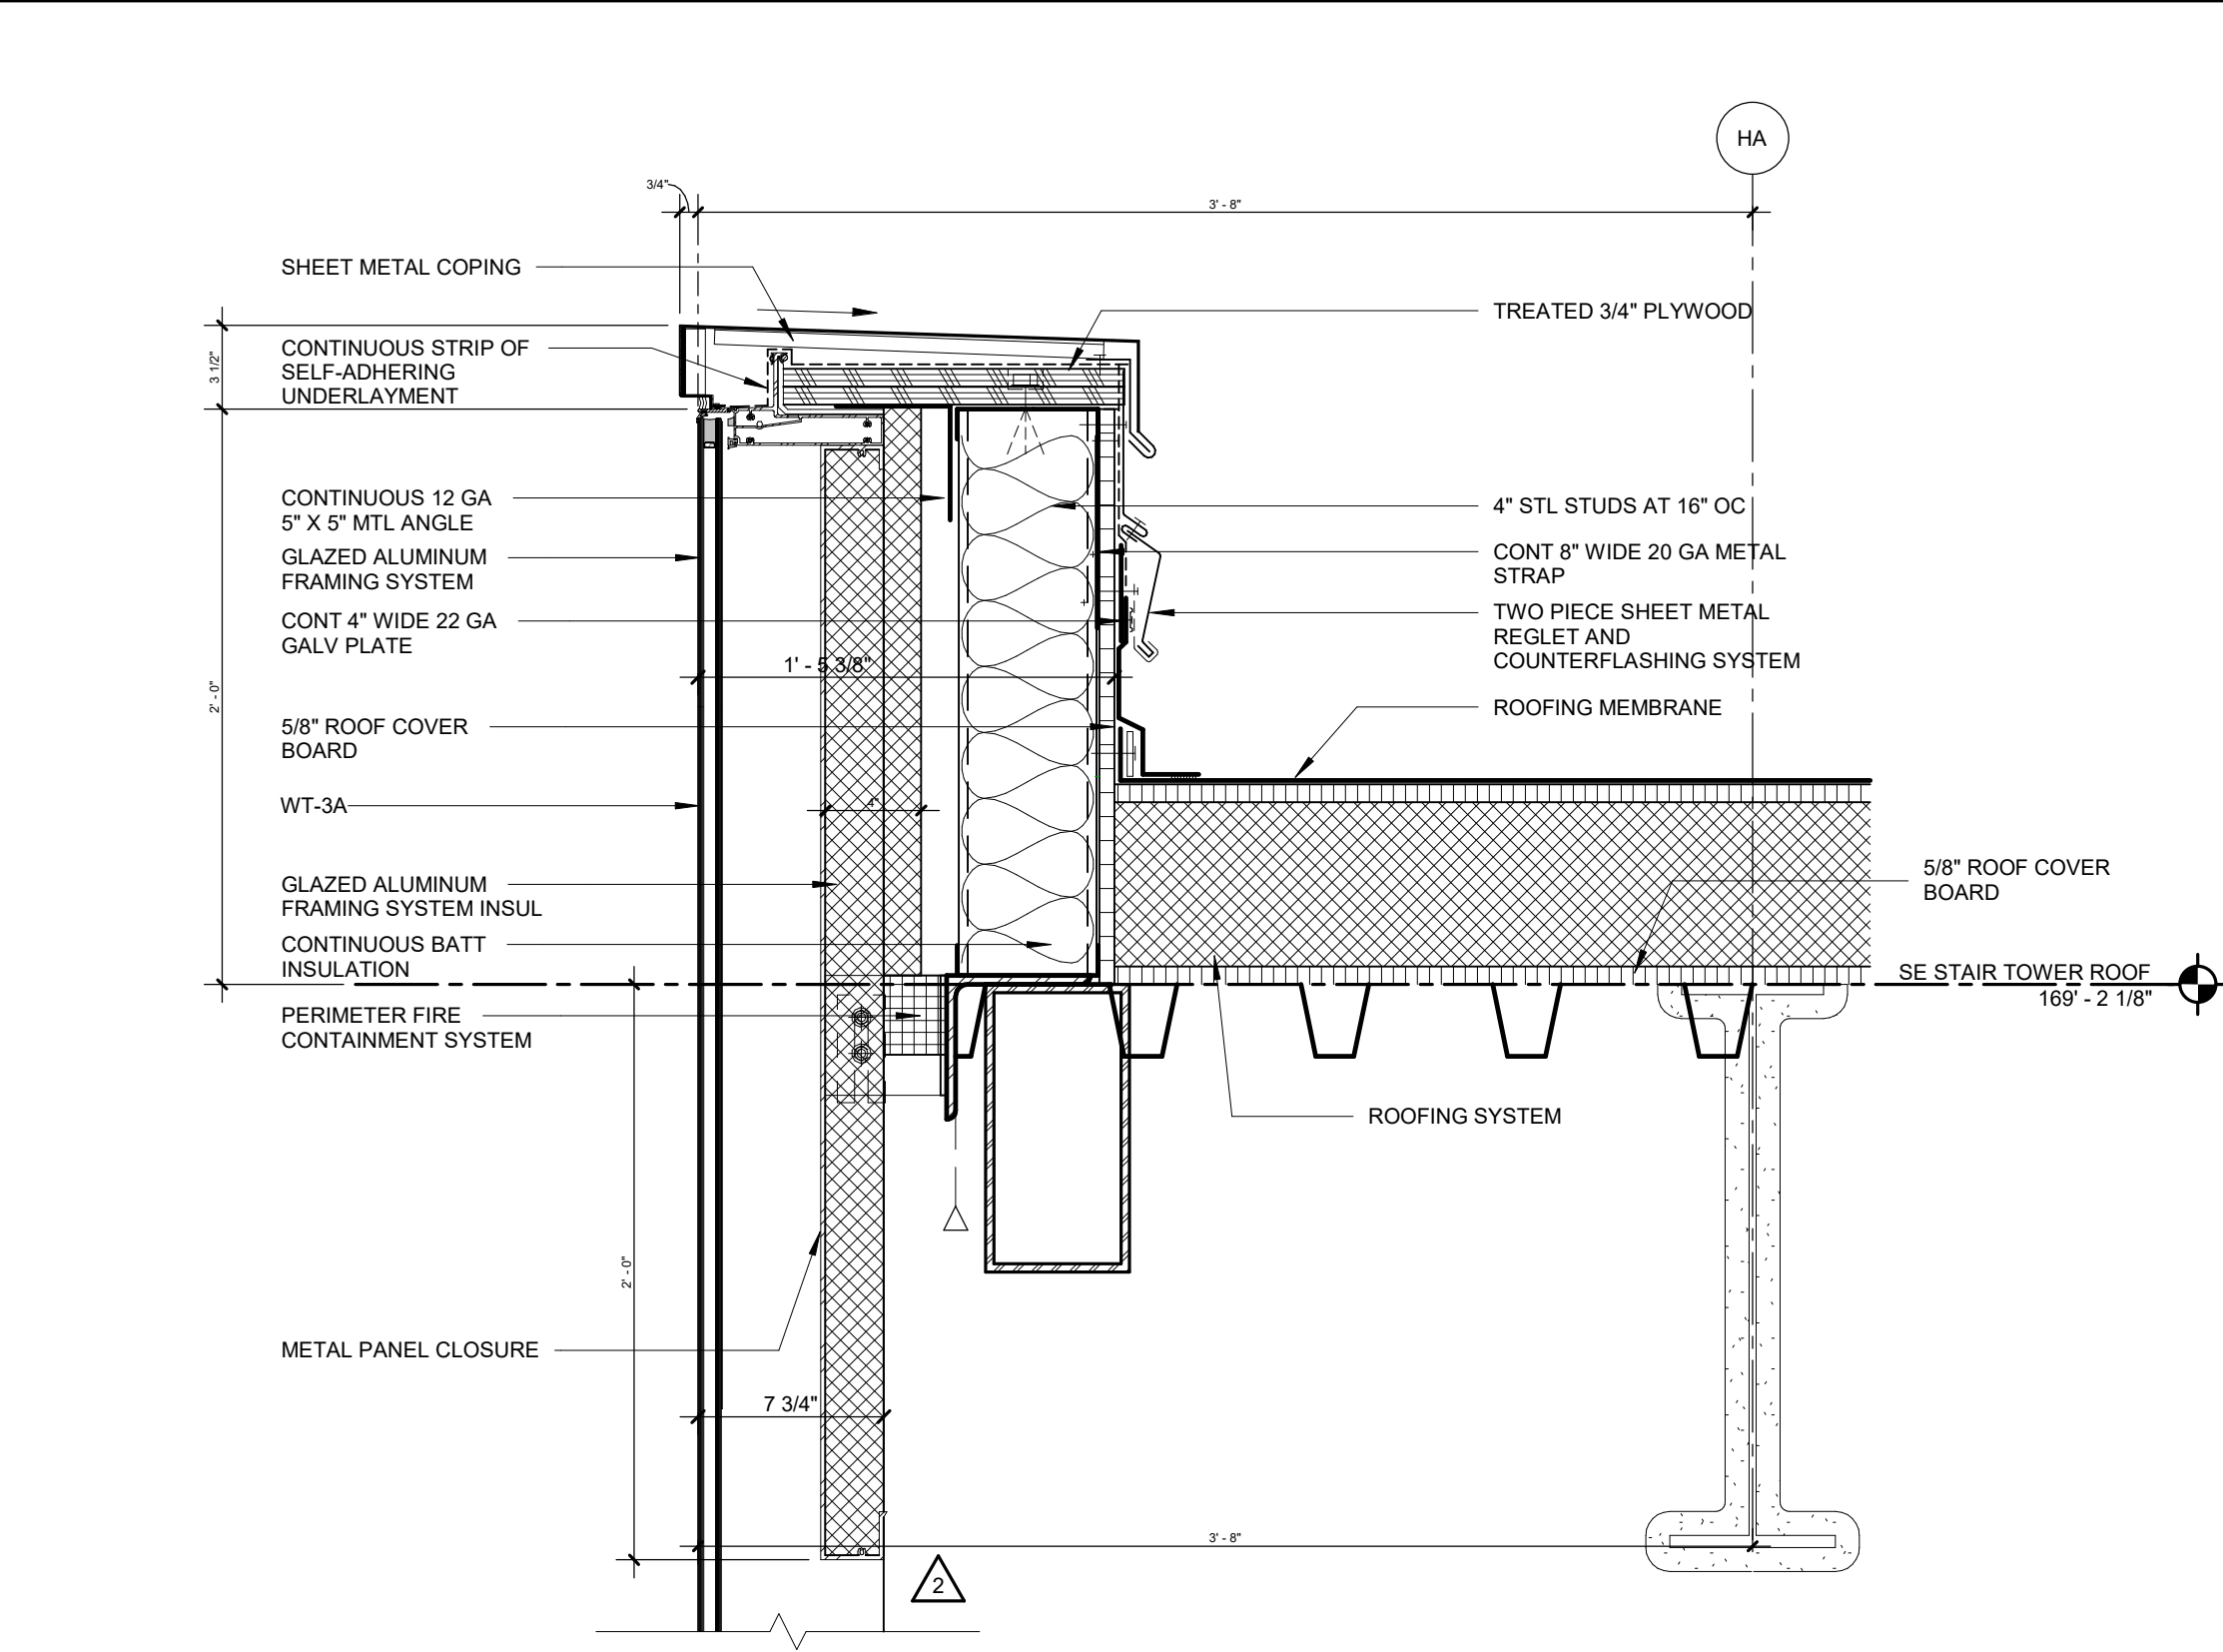

02 SECTION DTL - SE STAIR TOWER EAST CW PARAPHET
 1 1/2" = 1'-0"

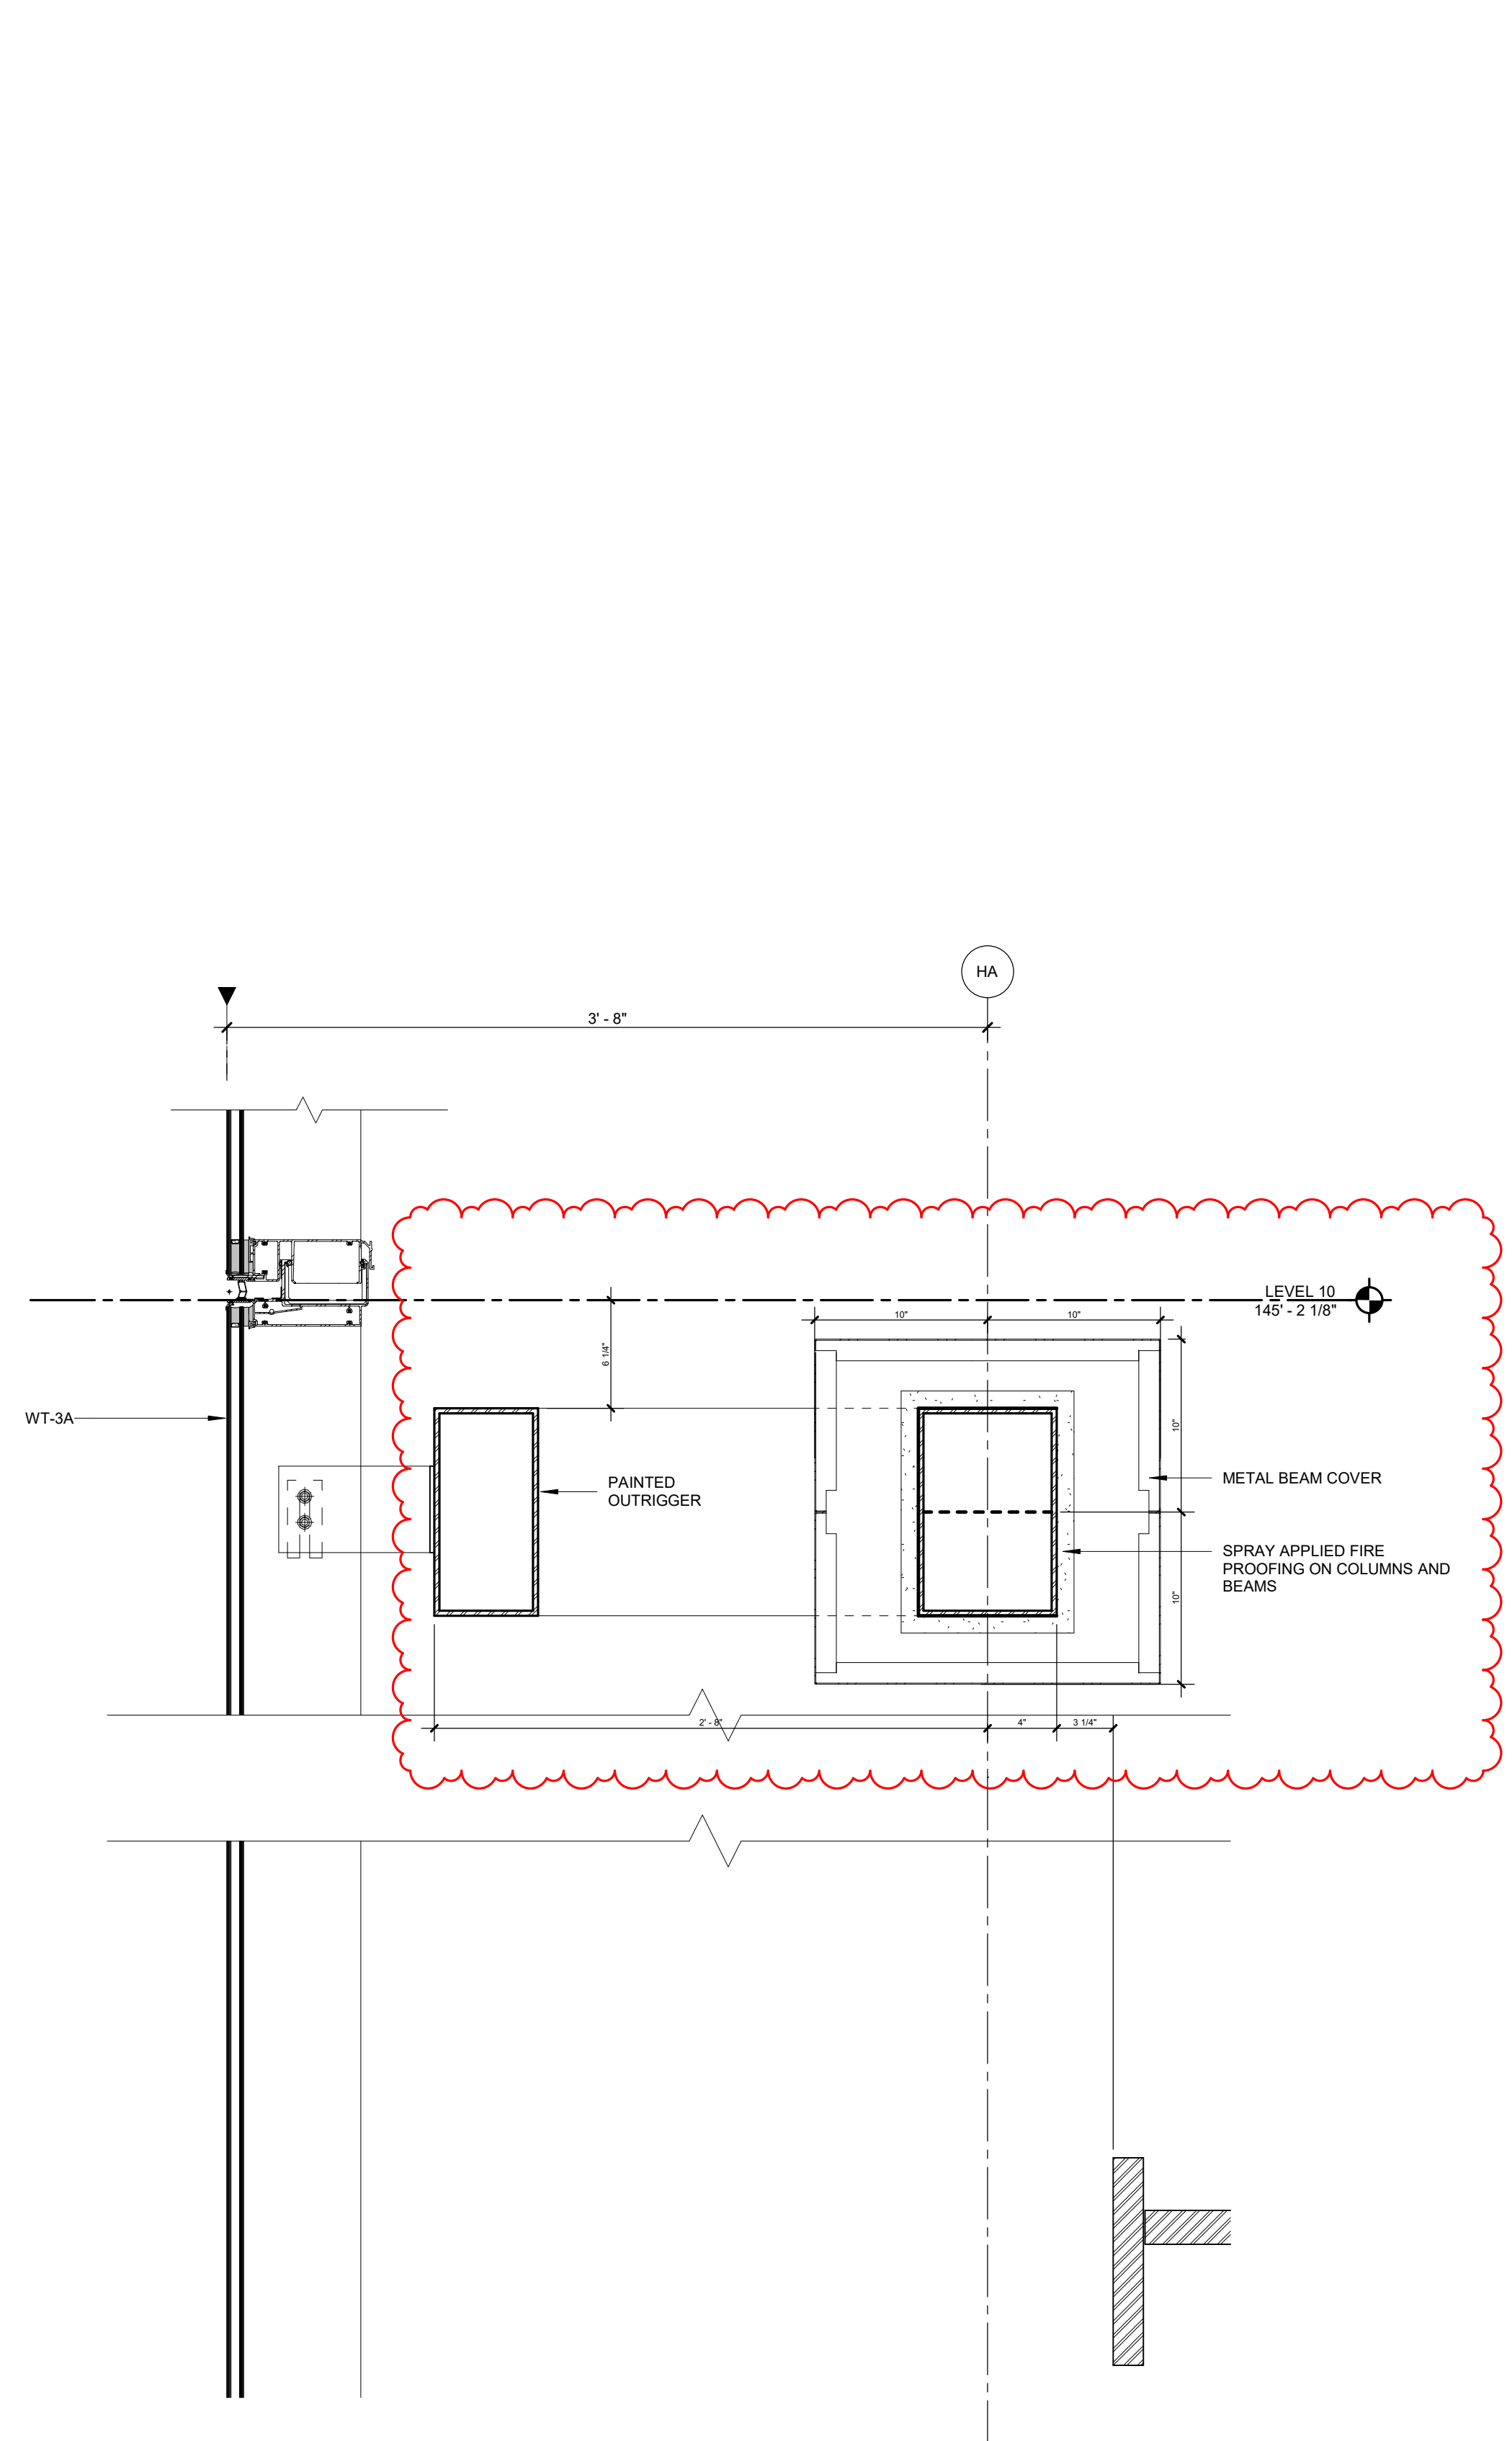

01 SECTION DTL - SE STAIR TOWER EAST CW TO STAIR INTERMEDIATE LANDING, TYP
 1 1/2" = 1'-0"

RESERVE FOR DCA STAMP



ARCHITECT
 HKS, P.C.
 1250 I (EYE) STREET NW, SUITE 600
 WASHINGTON, DC 20005
ASSOCIATE ARCHITECT / INTERIOR DESIGNER
 ARRAY
 1 WEST ELM STREET, SUITE 500
 CONSHOHOCKEN, PA 19028
STRUCTURAL ENGINEER
 O'DONNELL & NACCARATO
 701 MARKET ST., #6000
 PHILADELPHIA, PA 19106
MEP-FP / LOW VOLTAGE ENGINEER
 BR+A CONSULTING ENGINEERS
 2401 WALNUT ST SUITE 701
 PHILADELPHIA, PA 19103
 HIGHLAND ASSOCIATES
 102 HIGHLAND AVE
 CLARKS SUMMIT, PA 18411



OWNER
 COOPER UNIVERSITY HEALTHCARE
 1 COOPER PLAZA
 CAMDEN, NJ 08103
PROJECT MANAGER
 PURE PM
 2026 RICHMOND STREET
 PHILADELPHIA, PA 19134
CIVIL ENGINEER / LANDSCAPE
 LANGAN
 1818 MARKET STREET, SUITE 3300
 PHILADELPHIA, PA 19103
 SEAL & SINGATURE

KEY PLAN

REVISION	NO.	DESCRIPTION	DATE
1	BULLETIN #2		01/23/2025
2	BULLETIN #4		04/28/2025
3	RFI 0416		11/14/2025


HKS PROJECT NUMBER
25695.100
 DATE
10/15/2024
 ISSUE
CORE & SHELL PERMIT SET
 SHEET TITLE
EXTERIOR SECTION DETAILS

SHEET NO.


A7.13

BUILDING PERMIT NUMBER: 1111


TITLE BLOCK VERSION: 20210830
MODEL: A:\models\Draw\25695.000_Cooper_Miller_Campus_Plan_2023.dwg
PRINT DATE: 11/21/2025 9:29:41 PM
TEMPLATE VERSION: 23.0.3
HKS, INC.

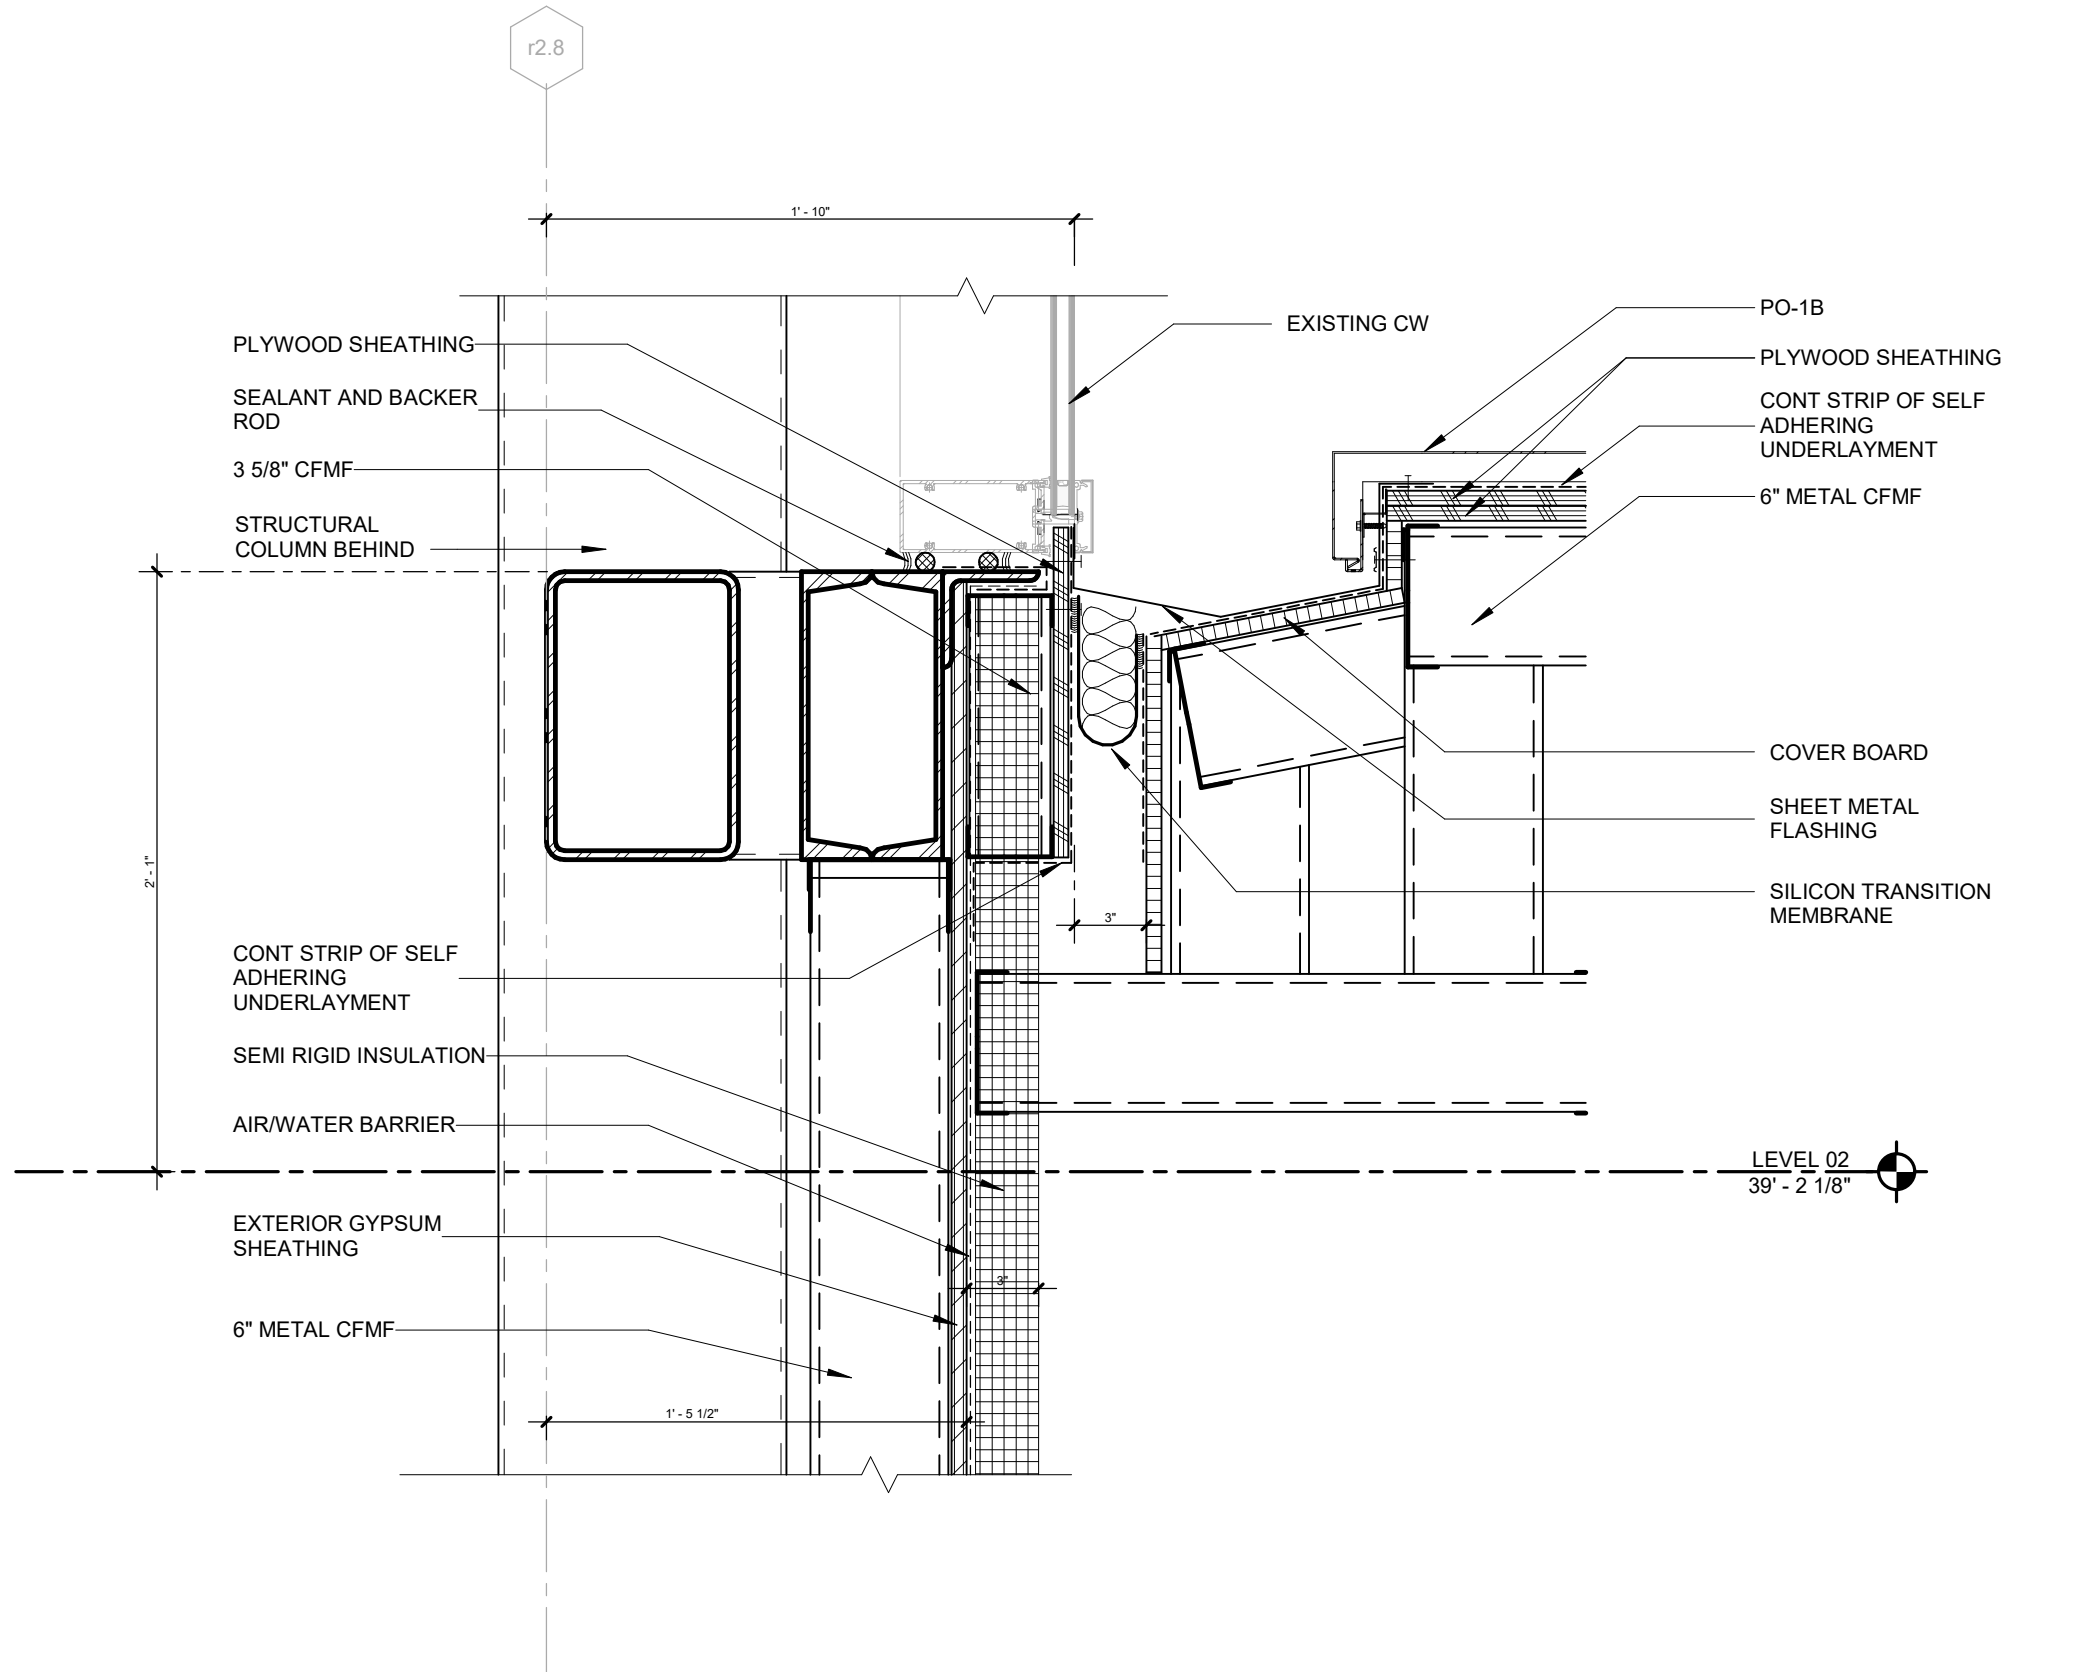


SECTION DETAIL - AT ROBERTS EXISTING CURTAIN WALL TO CONFERENCE CENTER FRAME ABOVE ENTRANCE
08
1 1/2" = 1'-0"

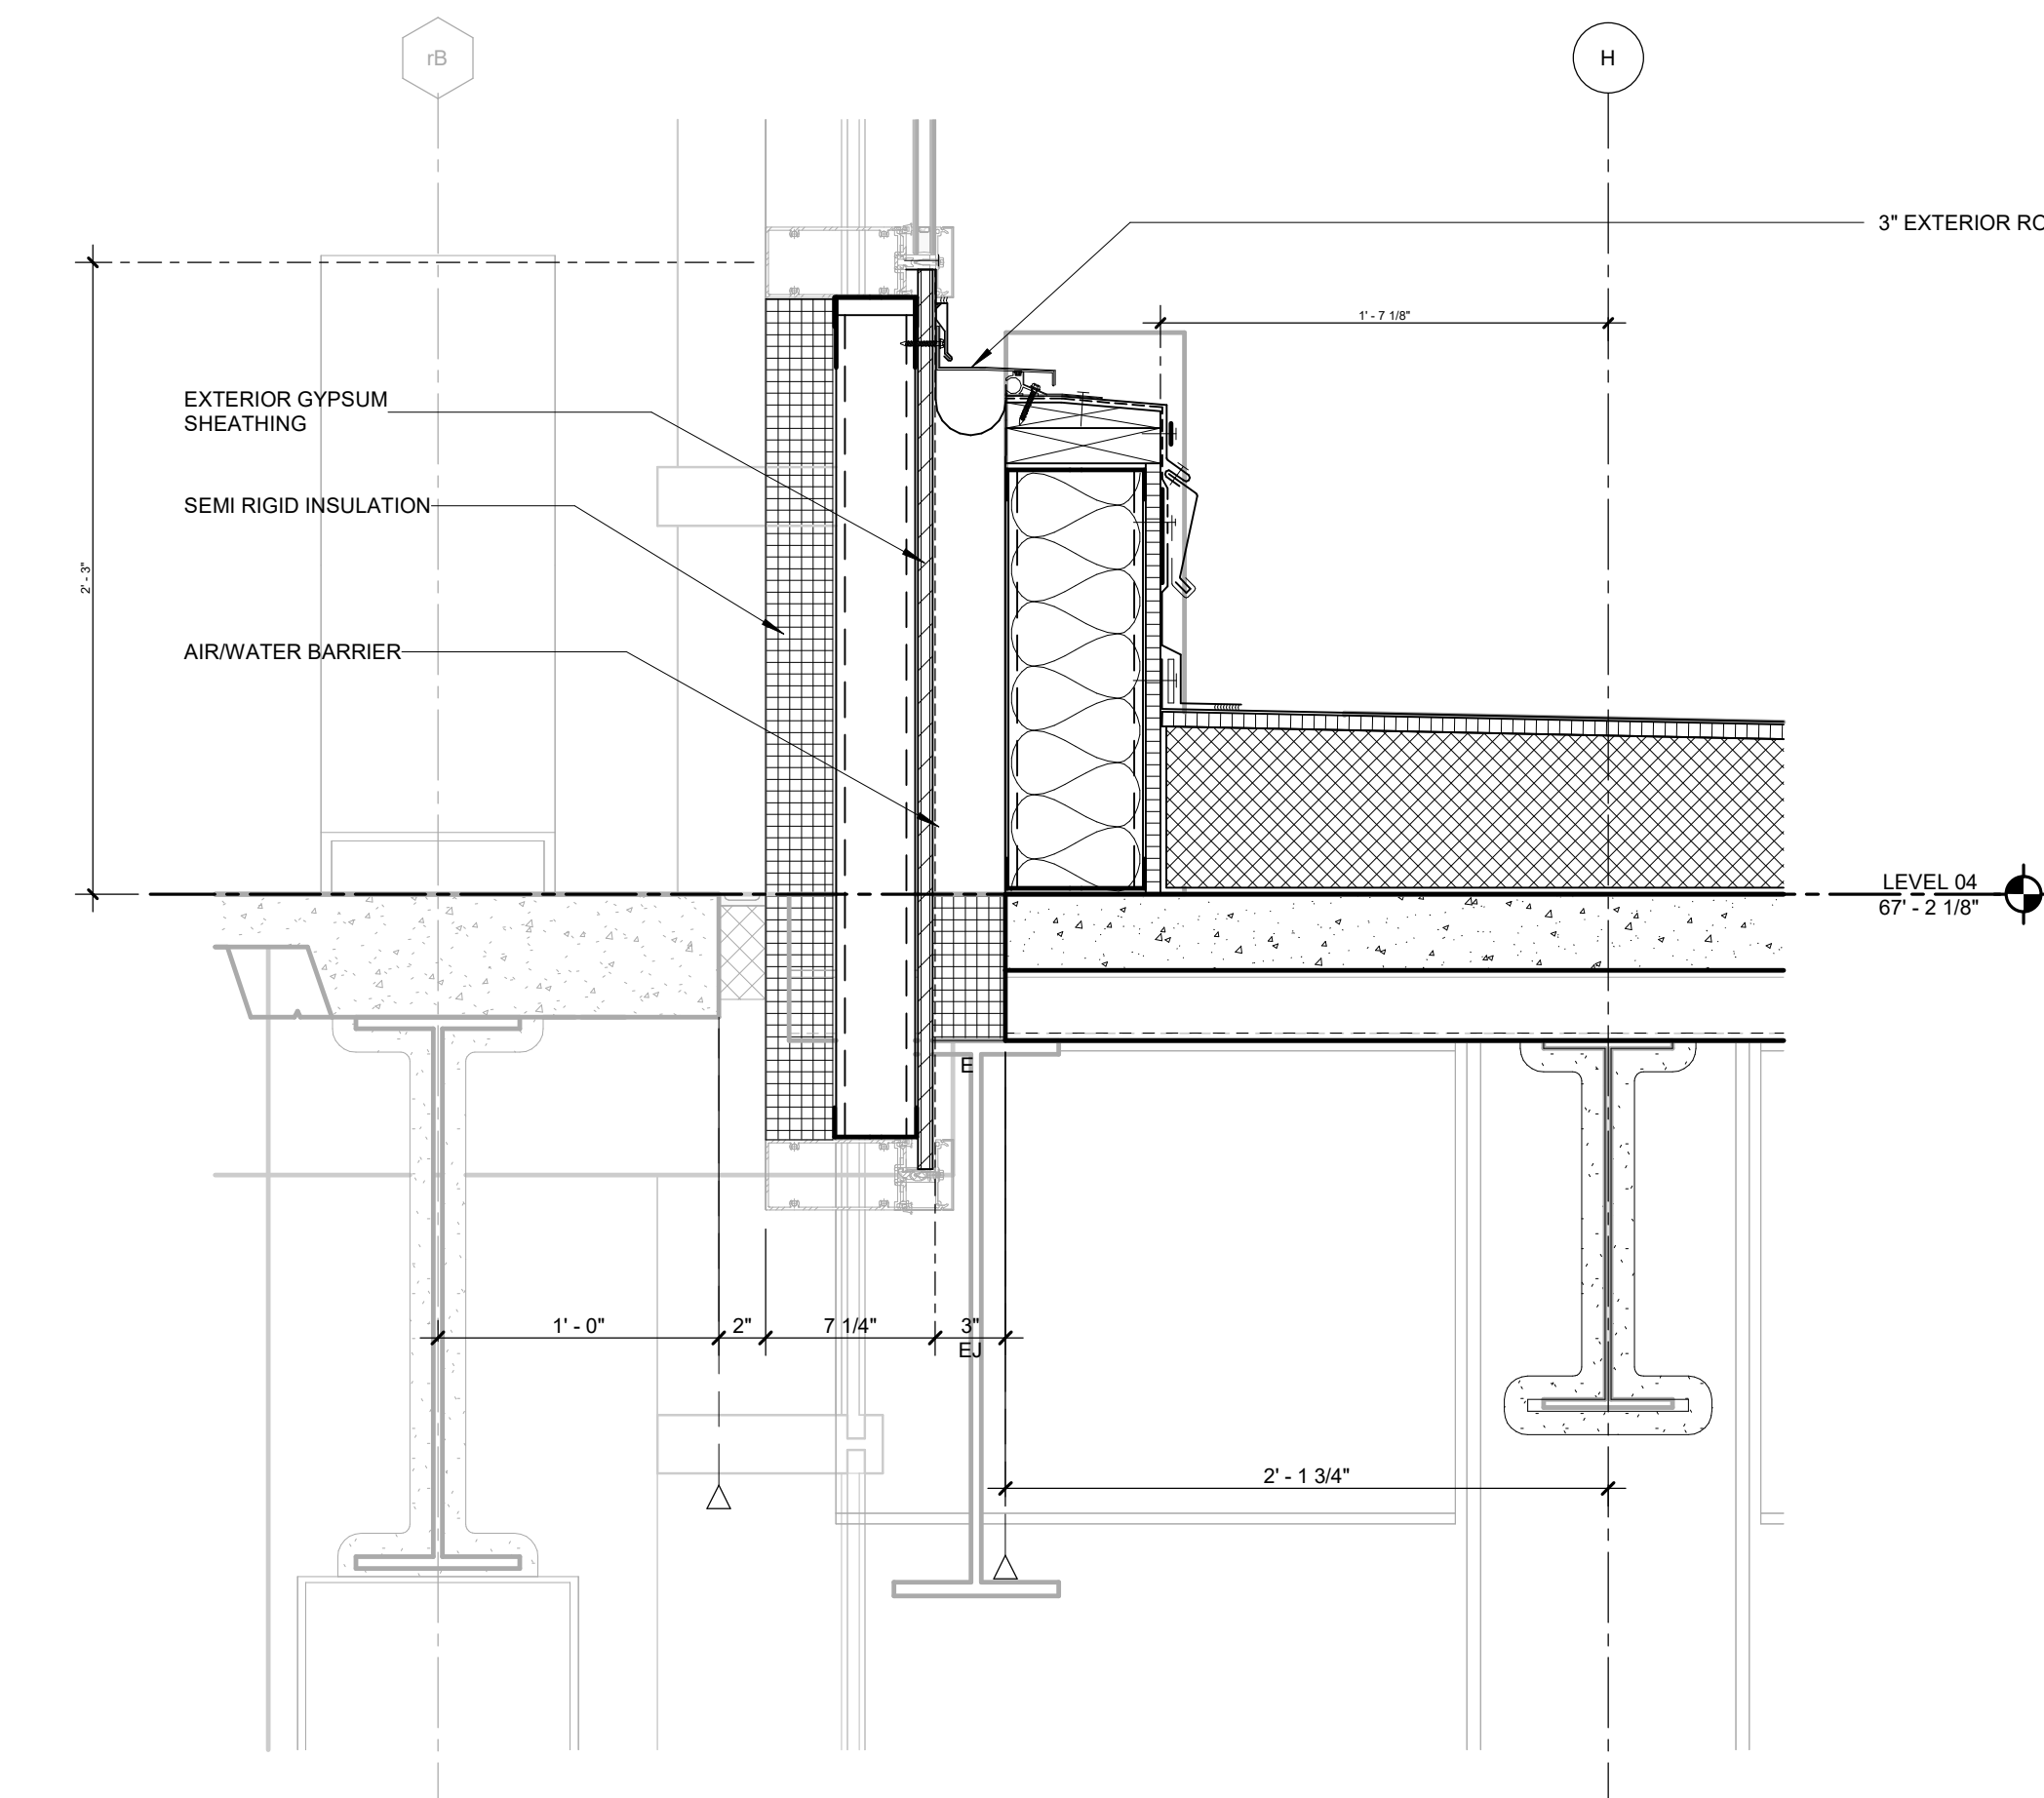


SECTION DETAIL - AT LEVEL 04 ROOF TO ROBERTS EXPANSION JOINT
07
1 1/2" = 1'-0"

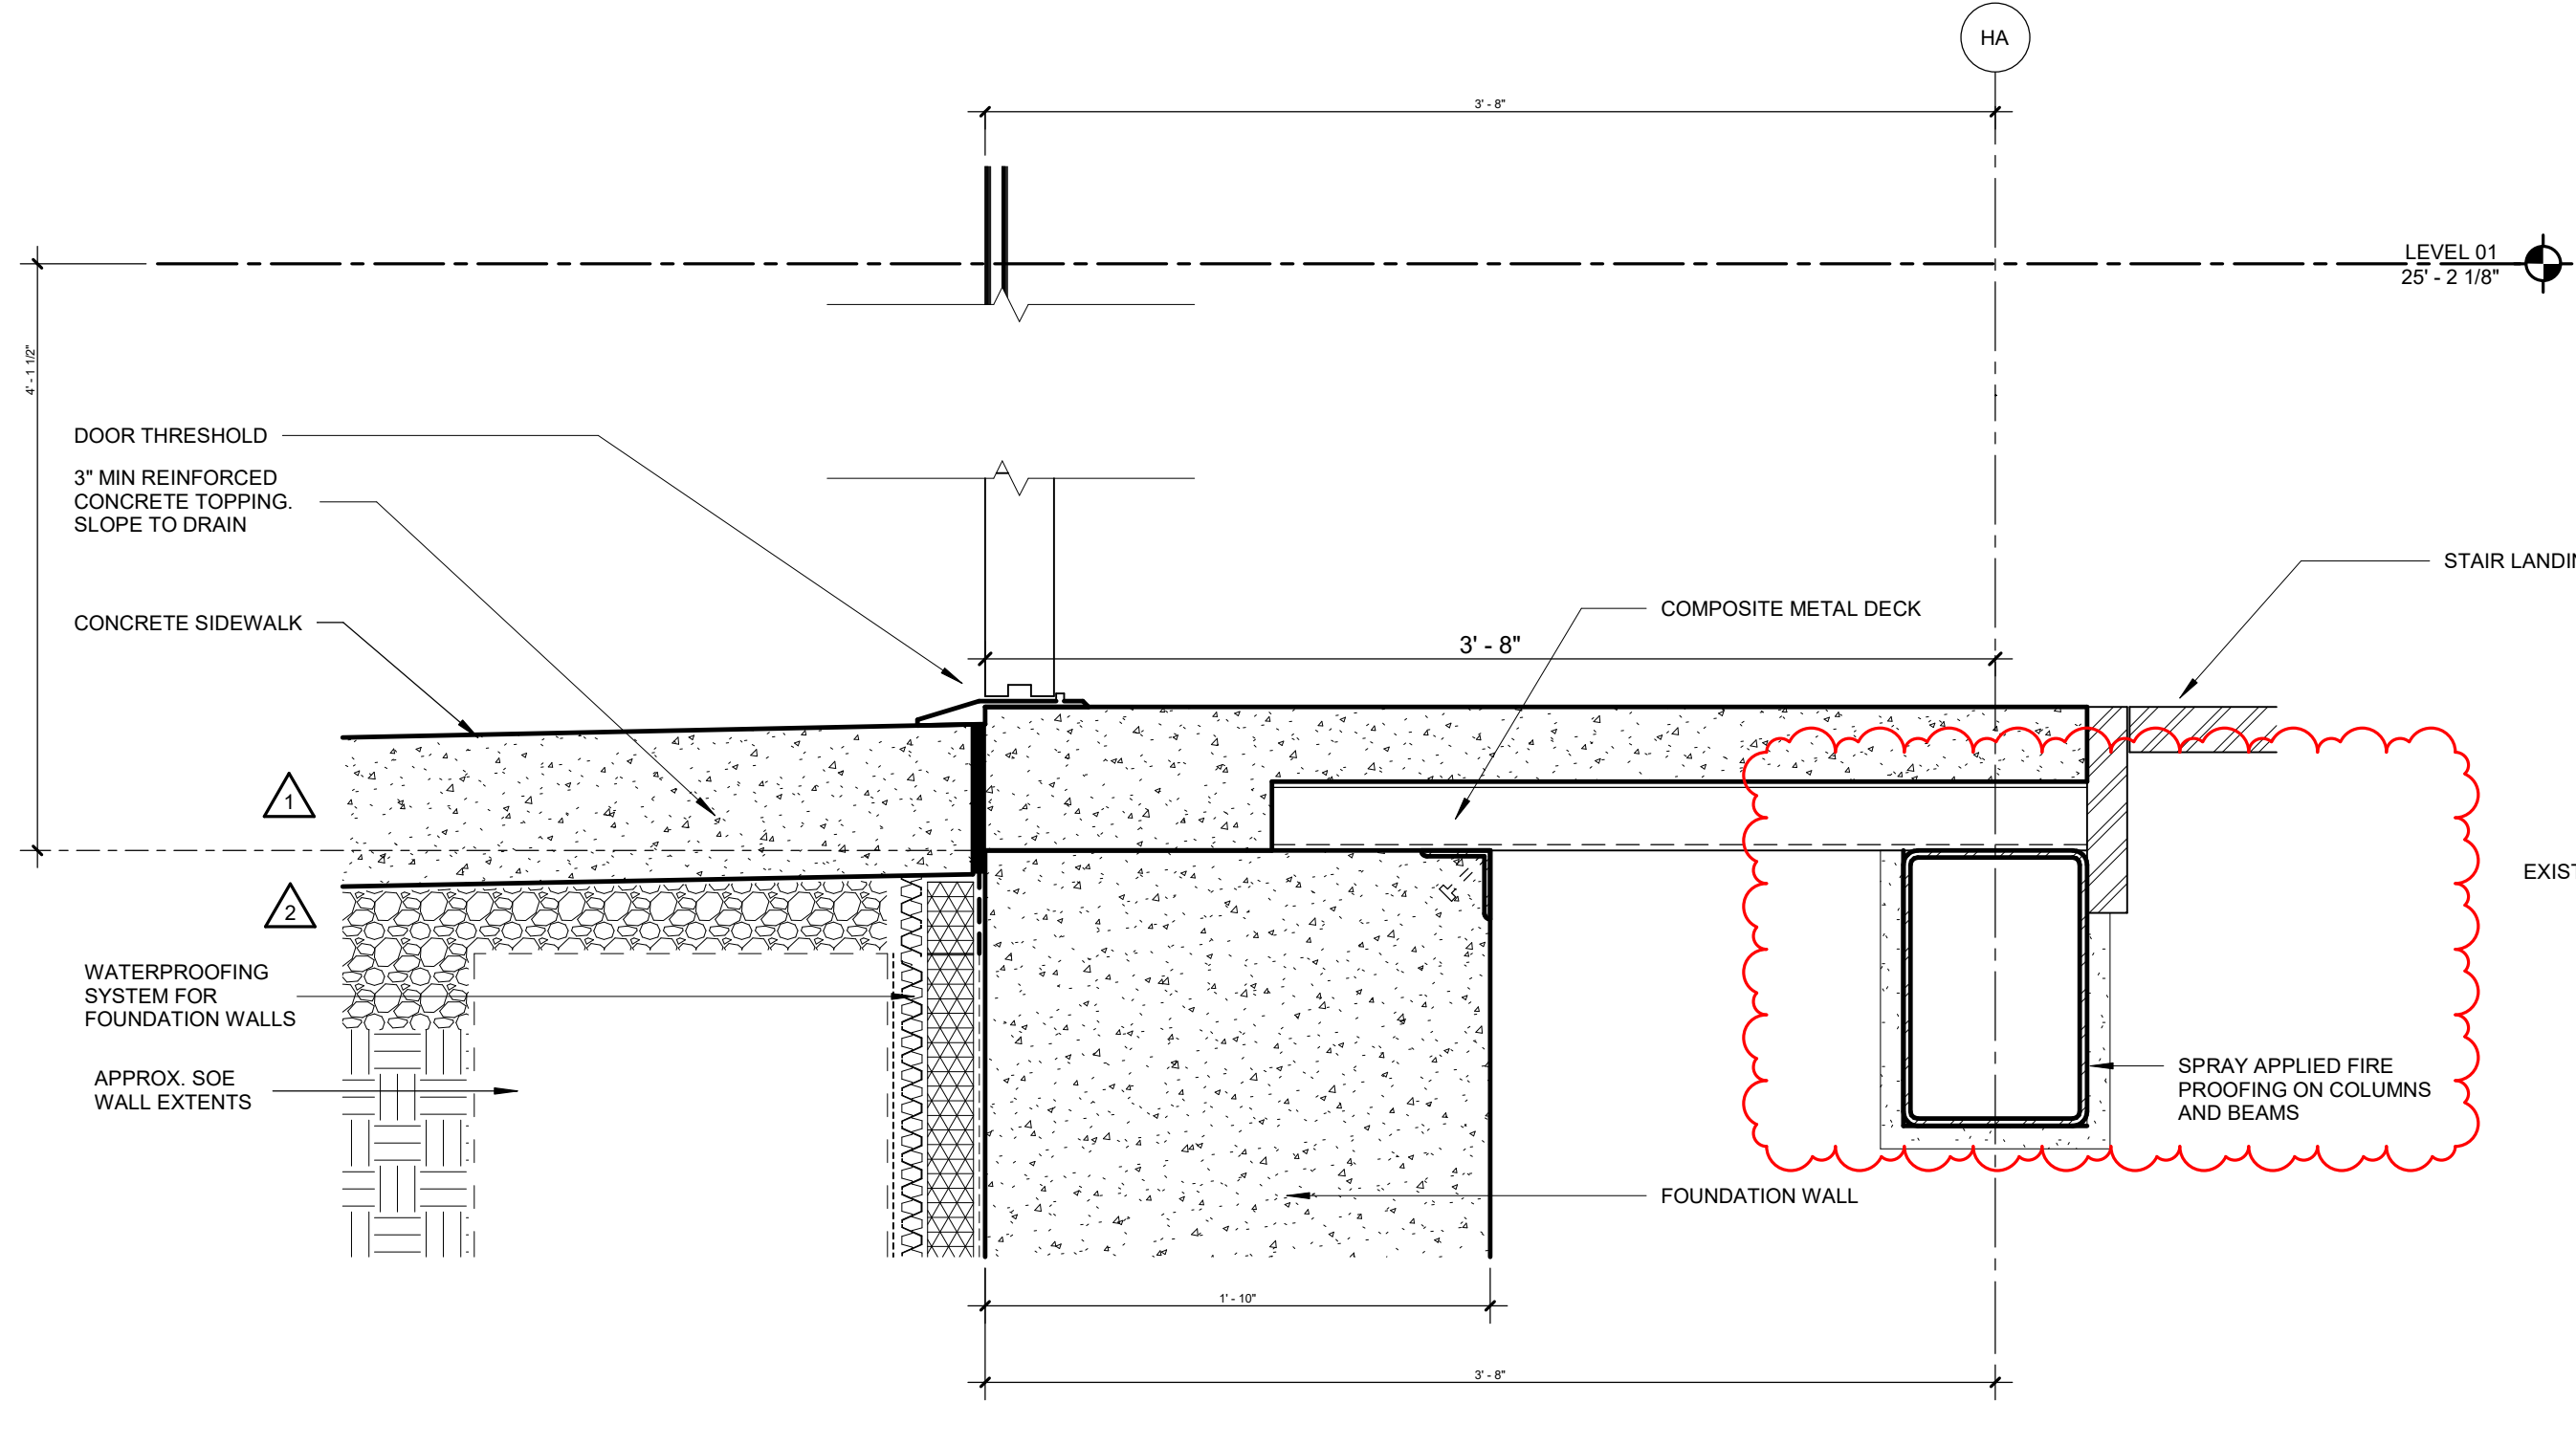


SECTION DTL - SE STAIR TOWER STAIR LANDING TO SIDEWALK
06
1 1/2" = 1'-0"

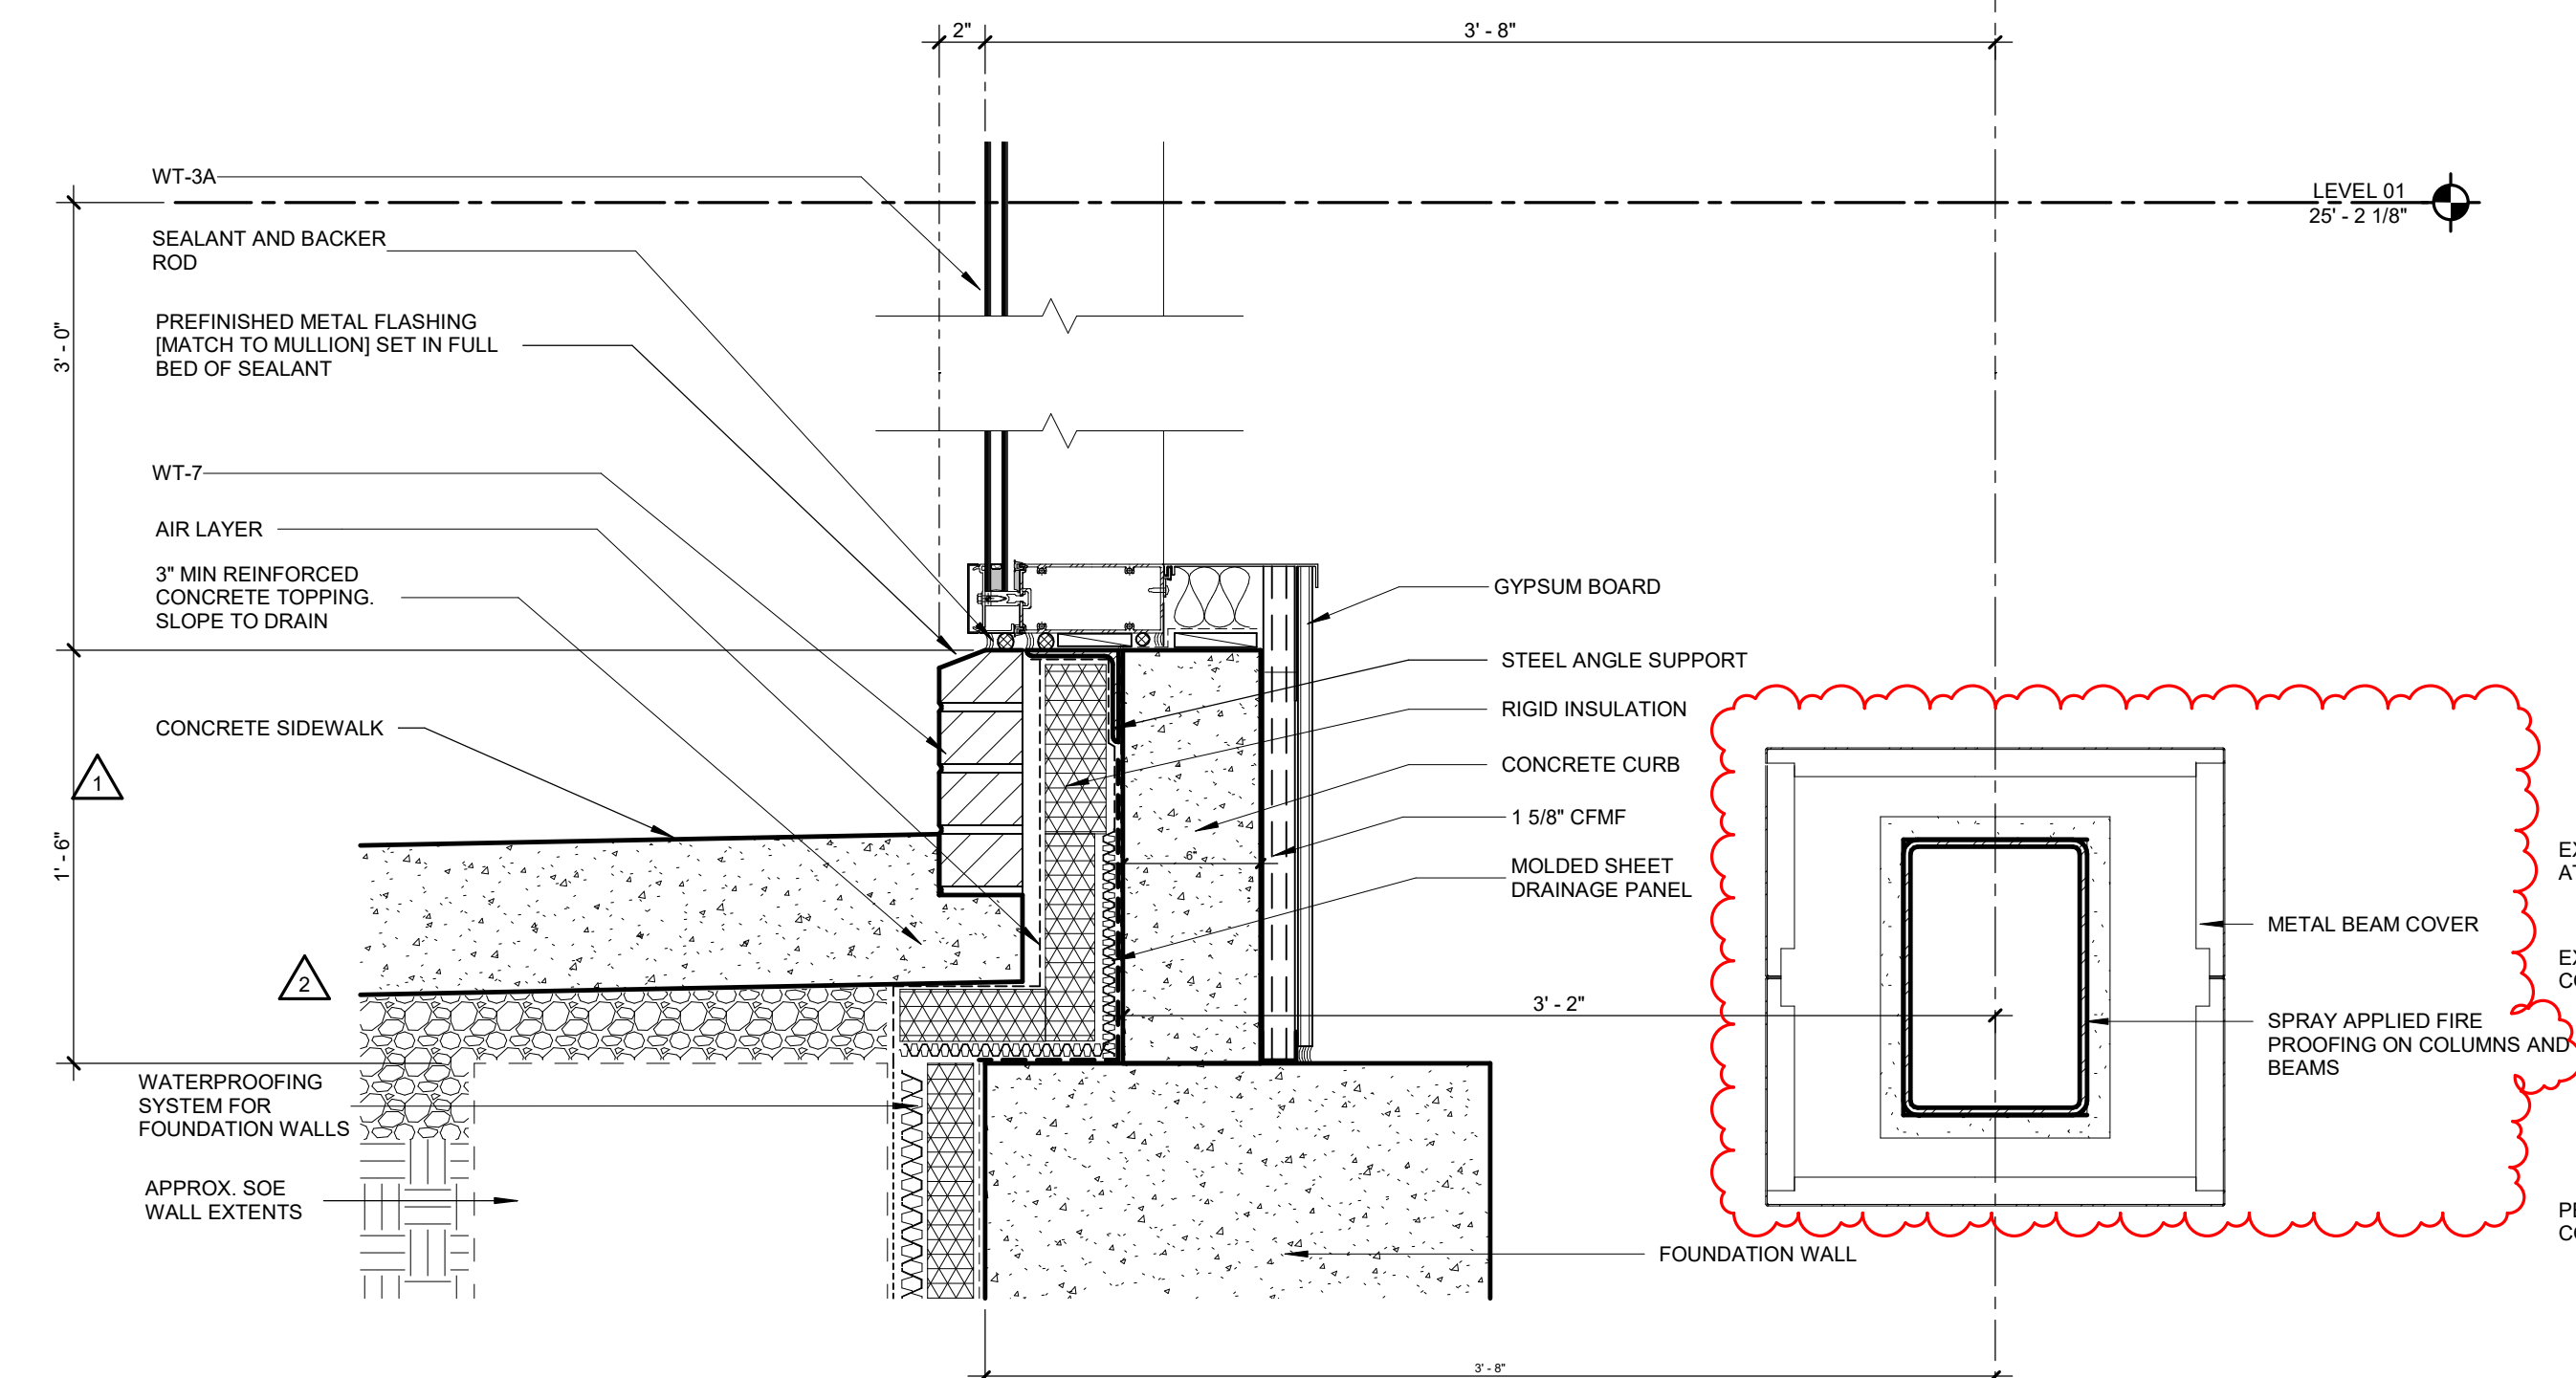


SECTION DETAIL - AT SE STAIR EAST CW TO SIDEWALK
05
1 1/2" = 1'-0"

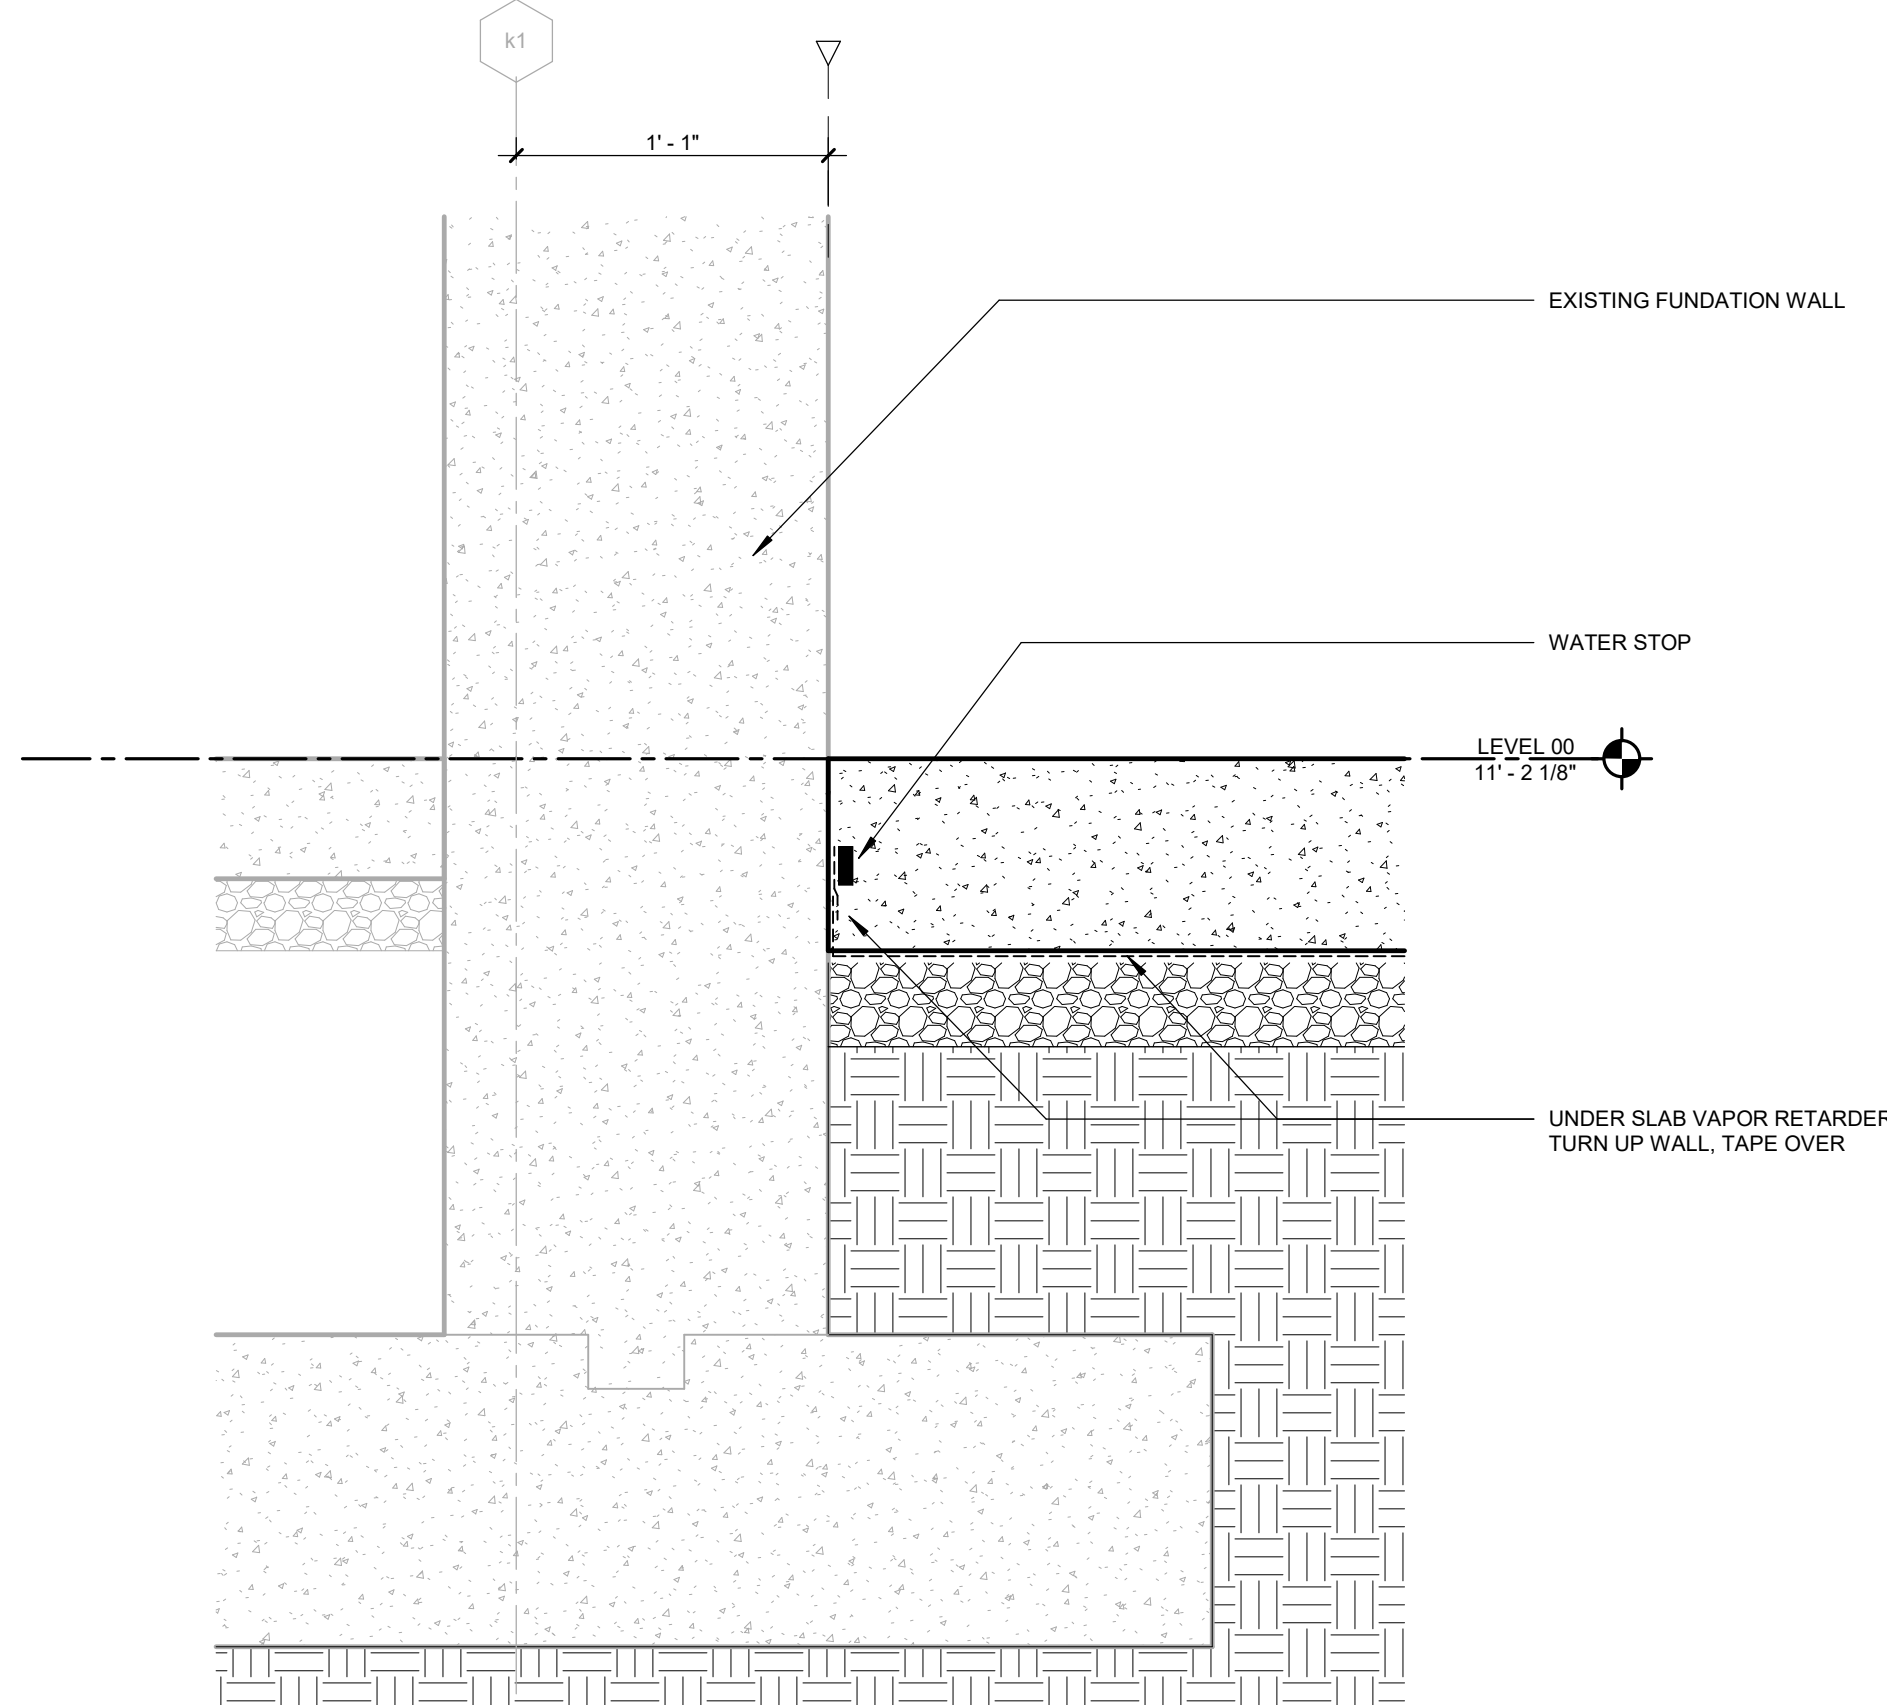


SECTION DETAIL - AT TOWER A TO ROBERTS AT LEVEL 00 CONDITION 01
04
1 1/2" = 1'-0"

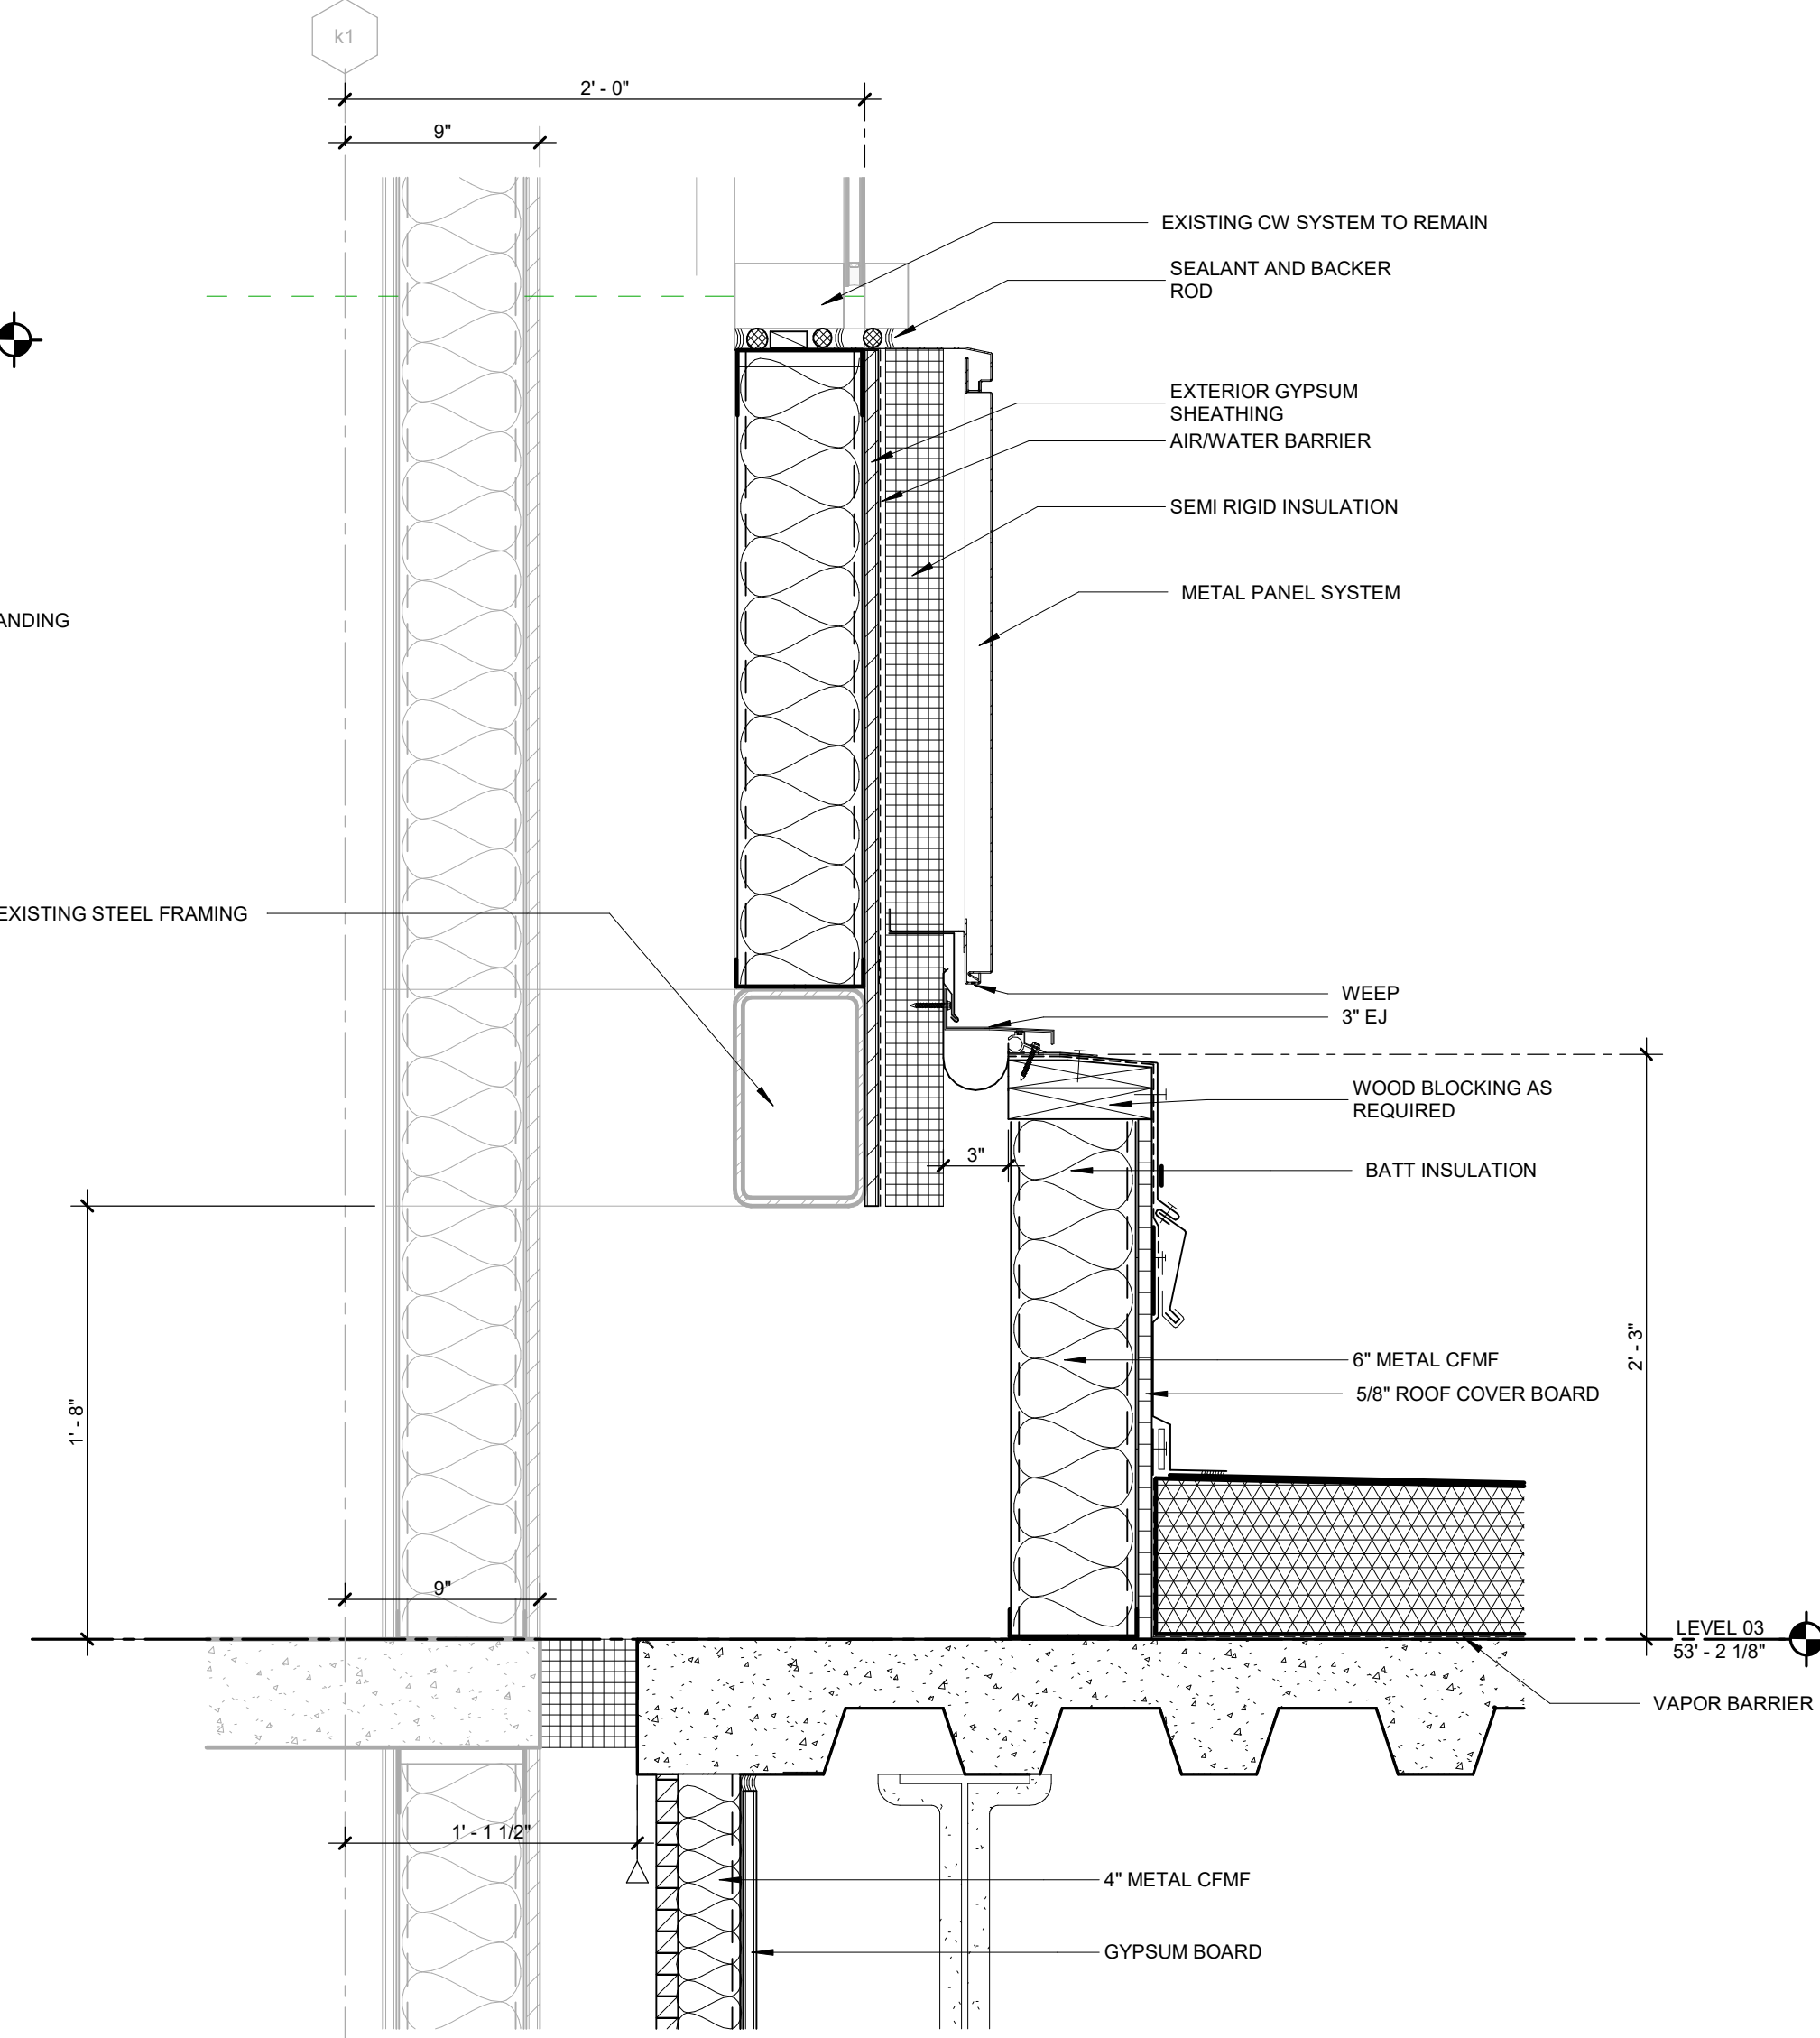

SECTION DTL - LVL 03 ROOF TRANSITION TO KEELMEN TOWER
03
1 1/2" = 1'-0"

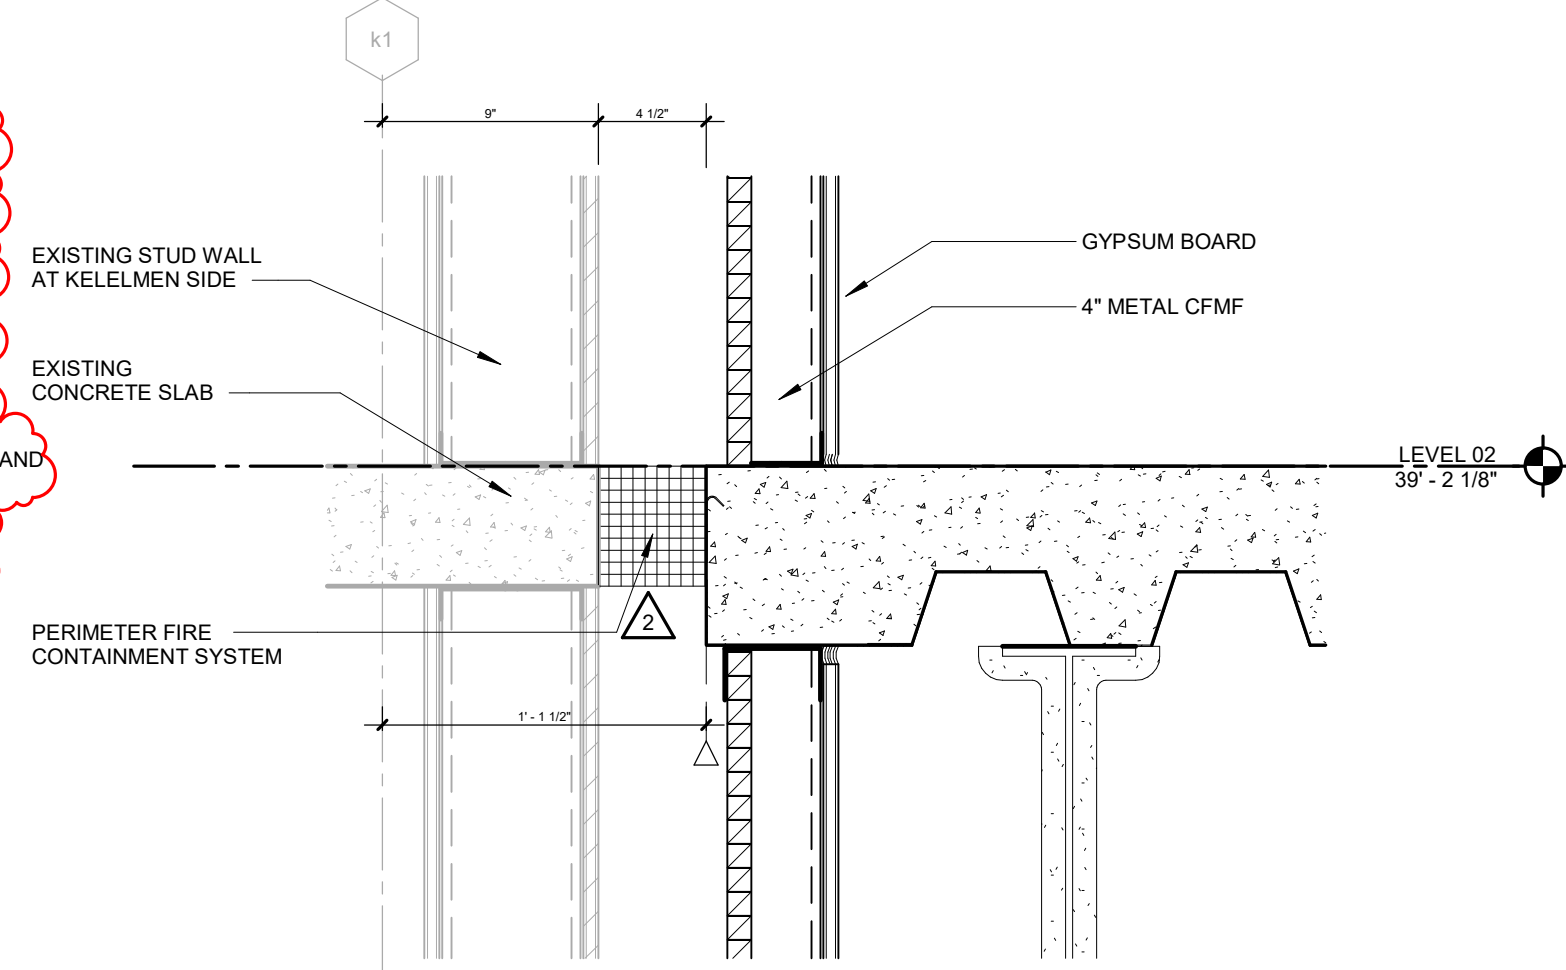

SECTION DETAIL - AT LEVEL 02 SOUTH SLAB EDGE TRANSITION TO KEELMEN
02
1 1/2" = 1'-0"

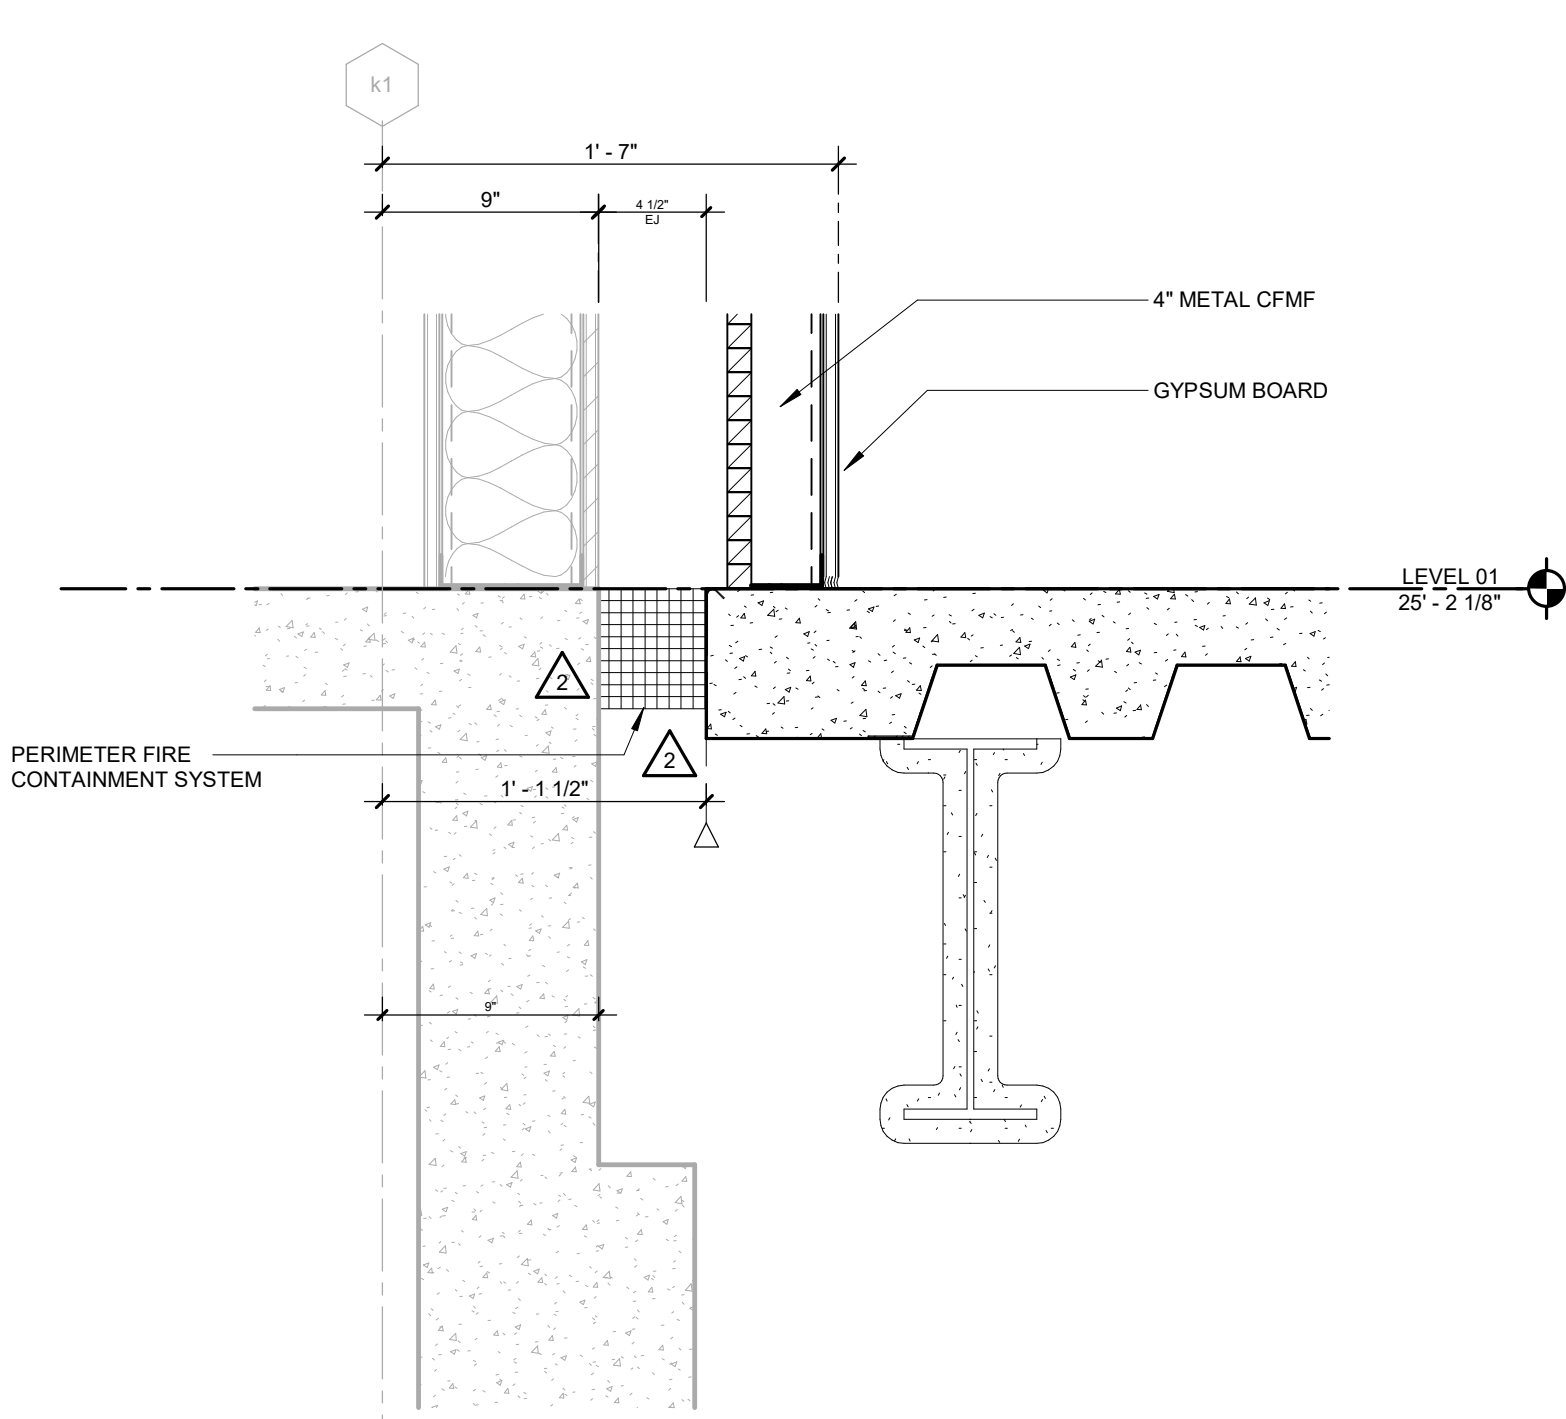

SECTION DTL - AT LEVEL 01 SOUTH SLAB EDGE TRANSITION TO KEELMEN
01
1 1/2" = 1'-0"

RESERVE FOR DCA STAMP



ARCHITECT
HKS, P.C.
1250 I (EYE) STREET NW, SUITE 600
WASHINGTON, DC 20005
ASSOCIATE ARCHITECT / INTERIOR DESIGNER
ARRAY
1 WEST ELM STREET, SUITE 500
CONSHOHOCKEN, PA 19428
STRUCTURAL ENGINEER
O'DONNELL & NACCARATO
701 MARKET ST., #6000
PHILADELPHIA, PA 19106
MEP-FP / LOW VOLTAGE ENGINEER
BR-A CONSULTING ENGINEERS
2401 WALNUT ST SUITE 701
PHILADELPHIA, PA 19103
HIGHLAND ASSOCIATES
102 HIGHLAND AVE
CLARKS SUMMIT, PA 18411

Cooper
University Health Care
COOPER UNIVERSITY HOSPITAL - TOWER A
PROJECT ADDRESS: 1 COOPER PLAZA, CAMDEN, NJ 08103

OWNER
COOPER UNIVERSITY HEALTHCARE
1 COOPER PLAZA
CAMDEN, NJ 08103
PROJECT MANAGER
PURE PM
2026 RICHMOND STREET
PHILADELPHIA, PA 19134
CIVIL ENGINEER / LANDSCAPE
LANGAN
1818 MARKET STREET, SUITE 3300
PHILADELPHIA, PA 19103
SEAL & SINGATURE

KEY PLAN


REVISION	NO.	DESCRIPTION	DATE
1	BULLETIN #2		01/23/2025
2	BULLETIN #4		04/28/2025
3	RFI 0416		11/14/2025

HKS PROJECT NUMBER
25695.100
DATE
10/15/2024
ISSUE
CORE & SHELL PERMIT SET
SHEET TITLE
EXTERIOR SECTION DETAILS


SHEET NO.

A7.14


TITLE BLOCK VERSION: 20210830
MODEL: Alameda Docs 25695.100 Cooper Master Curtain Plan 2023A CH1 TowerA, Exterior 2023.rvt
PRINT DATE: 11/21/2025 9:29:49 PM
TEMPLATE VERSION: 23.0.3

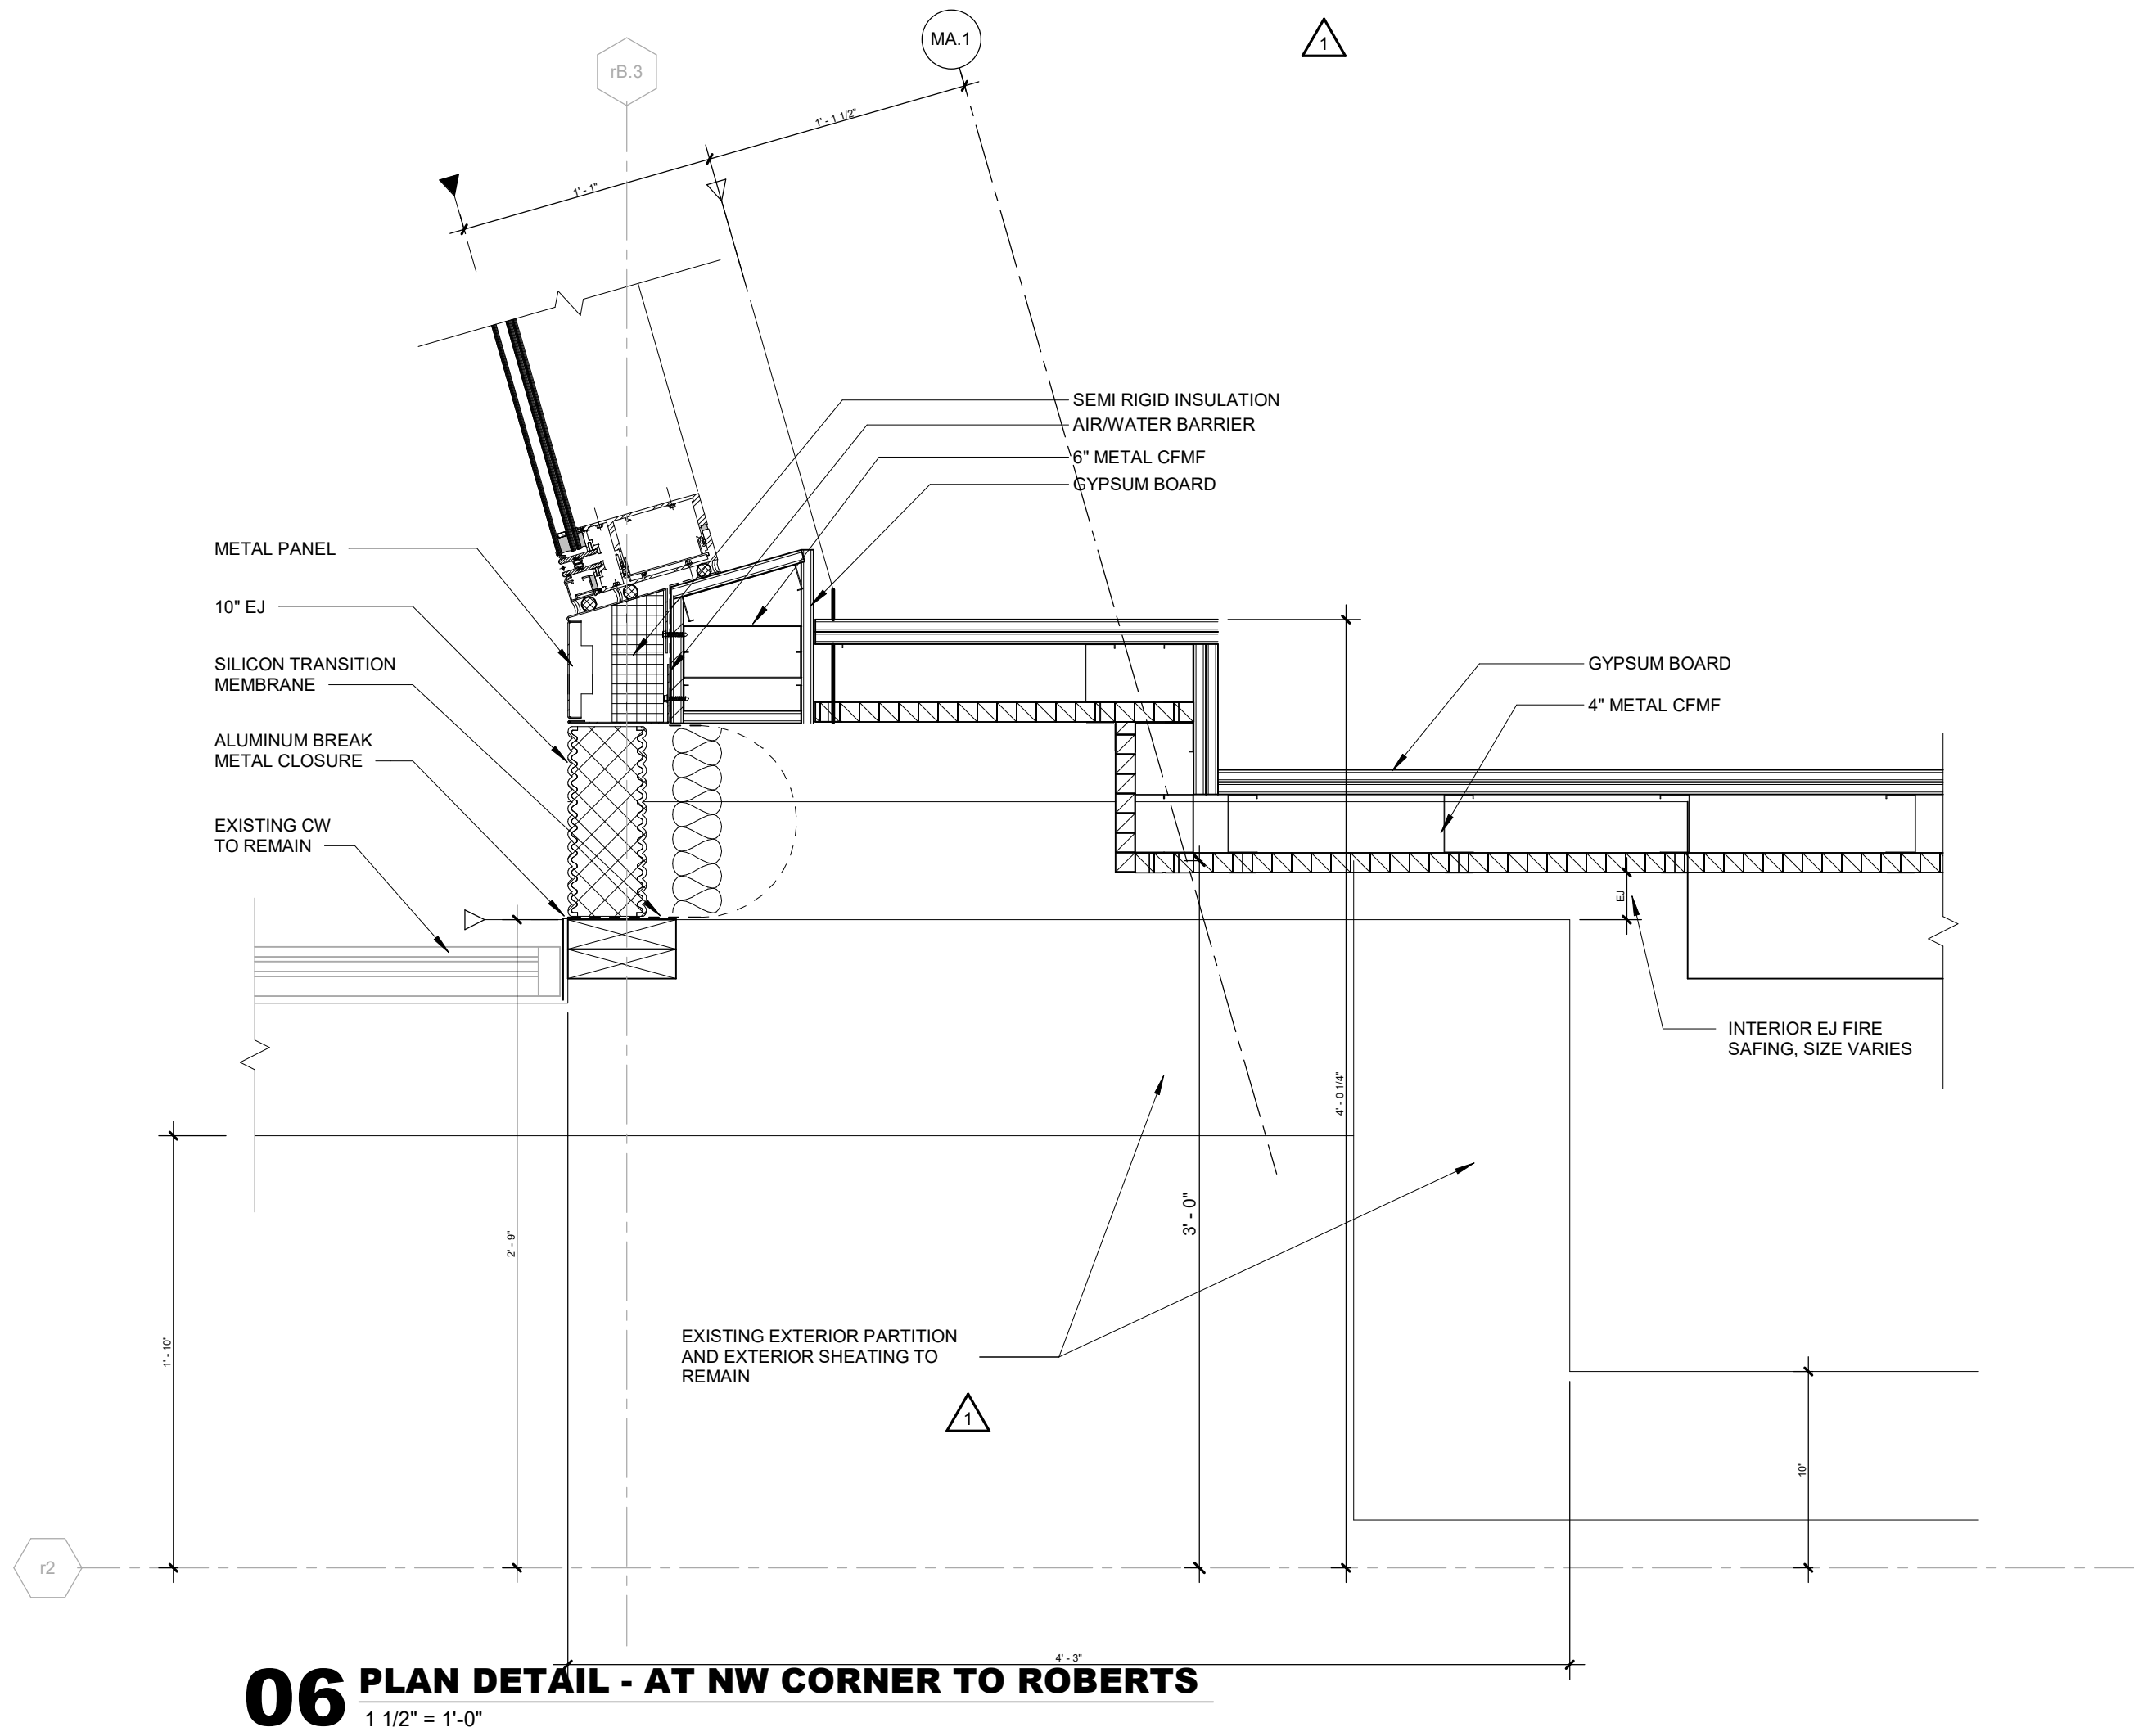


06 PLAN DETAIL - AT NW CORNER TO ROBERTS
1 1/2" = 1'-0"

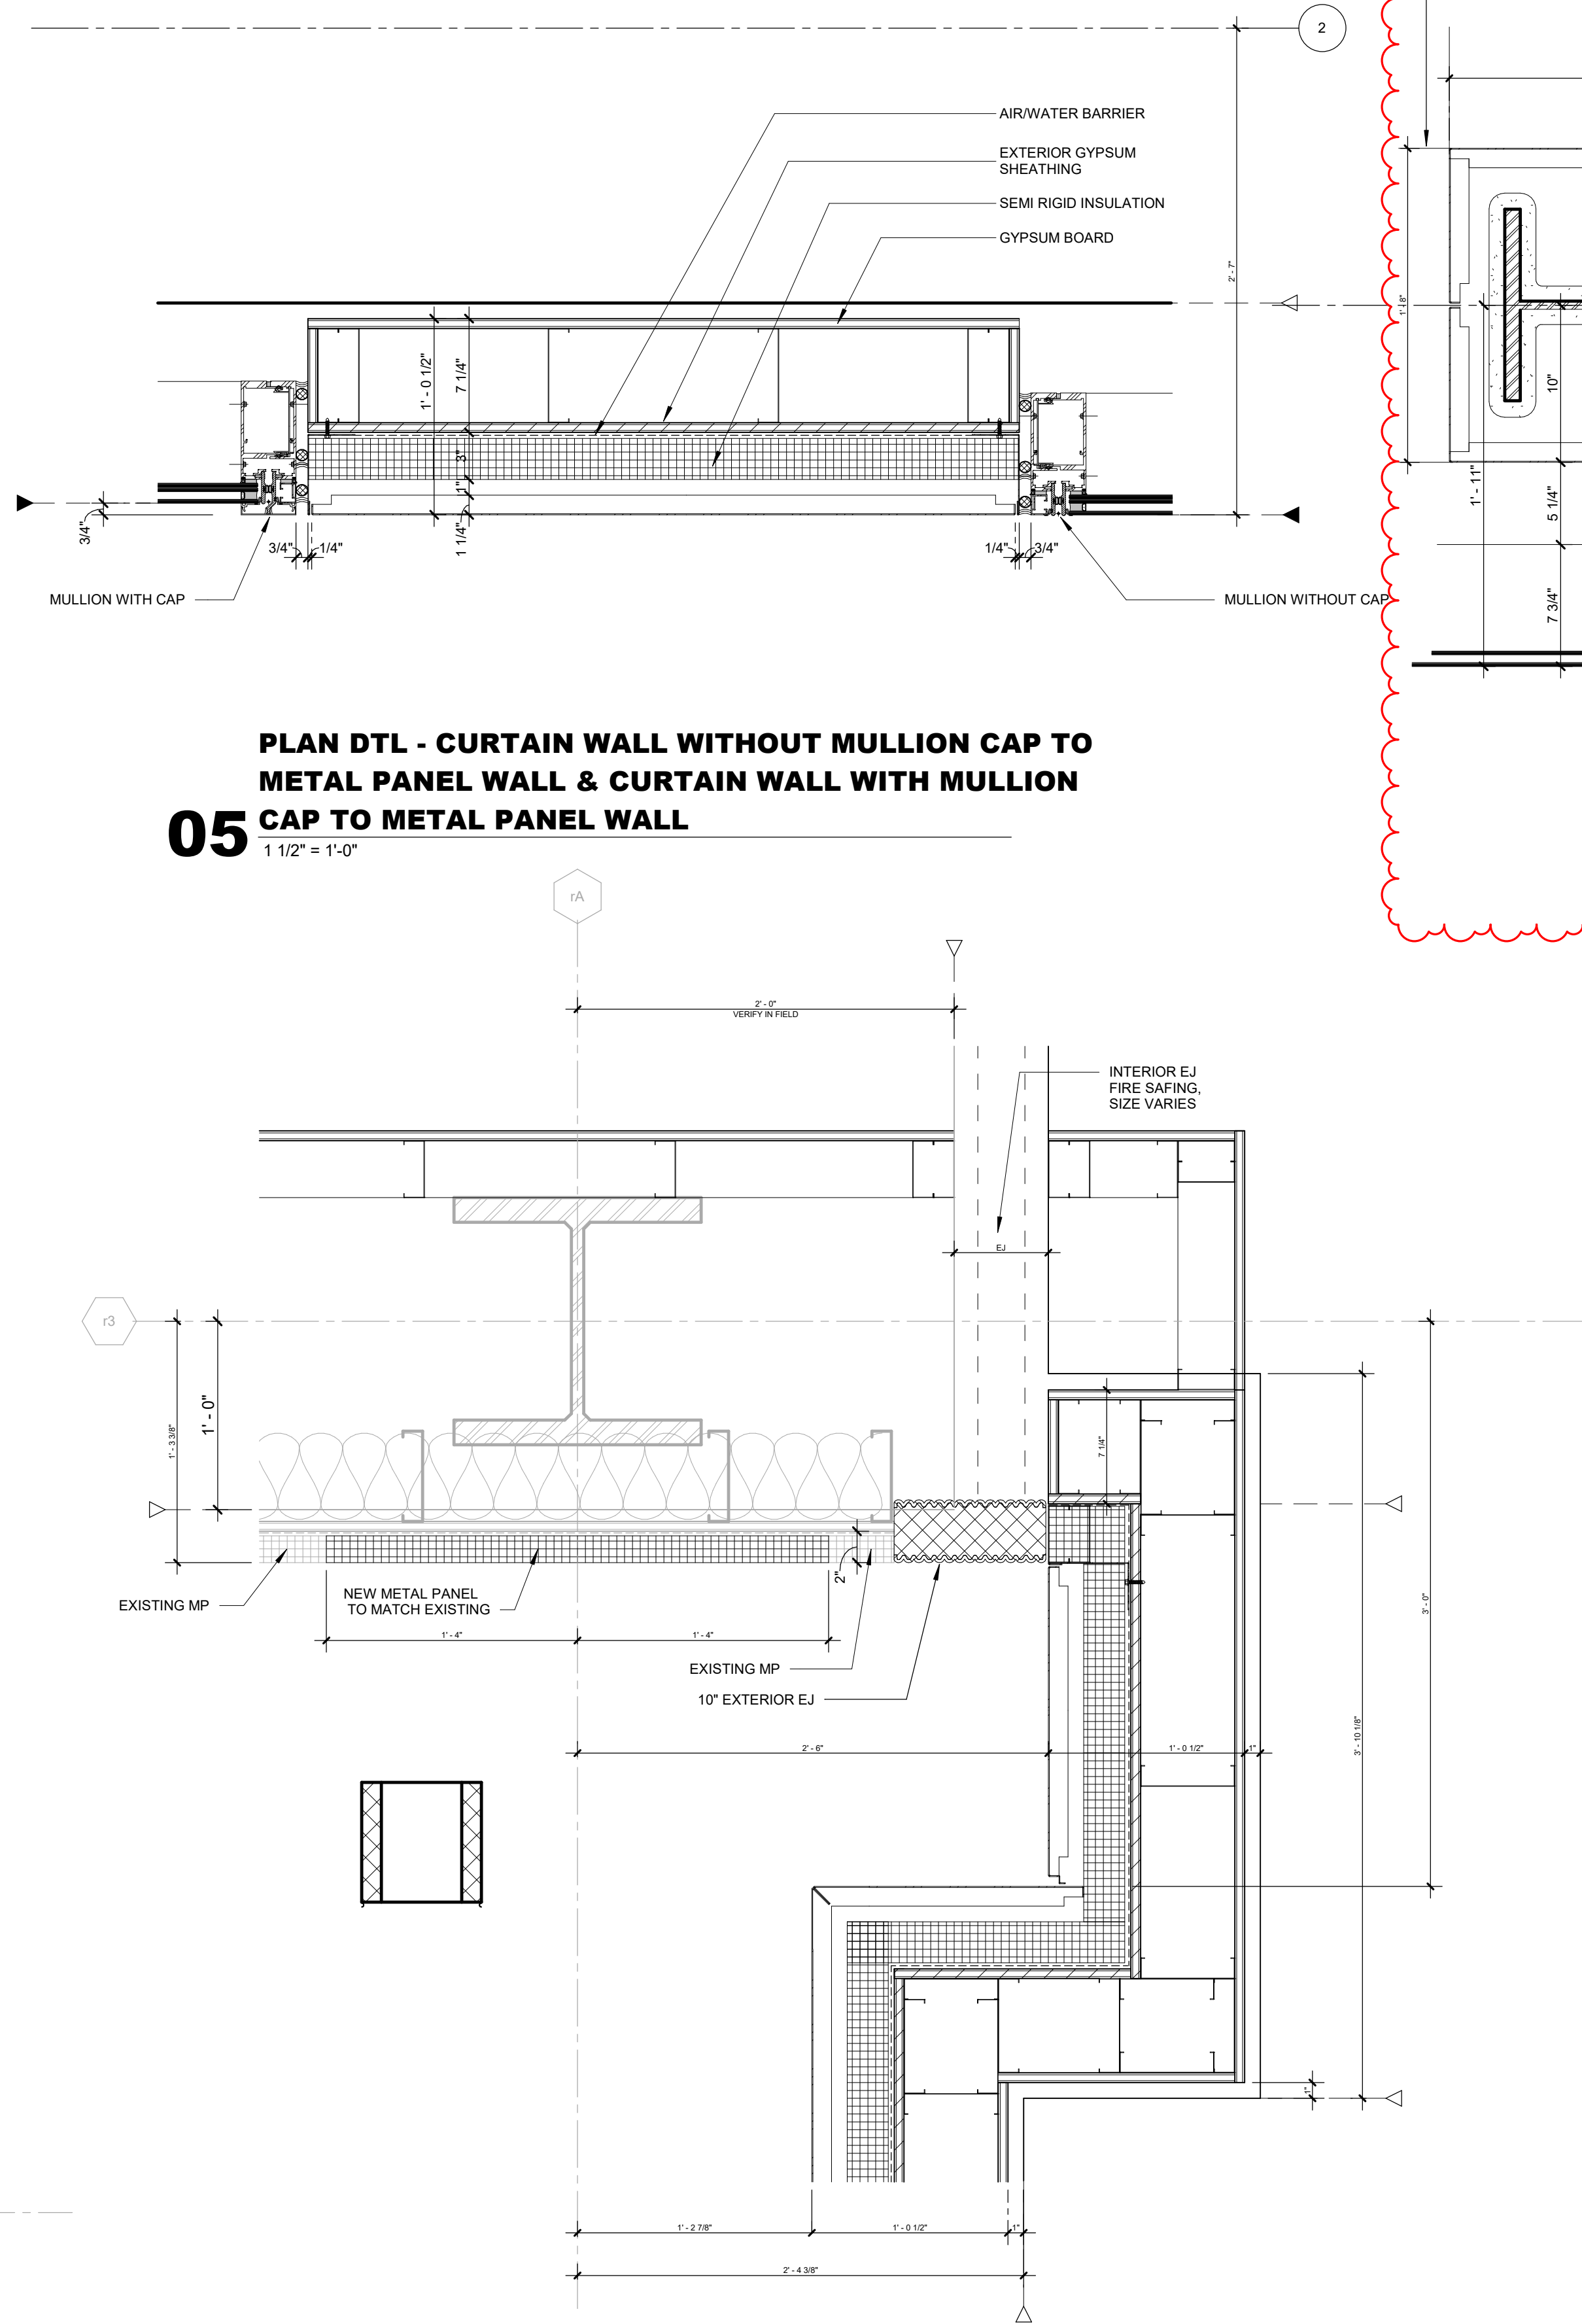


04 PLAN DETAIL - AT EXPANSION JOINT OF WEST TOWER A MEETS ROBERTS
1 1/2" = 1'-0"

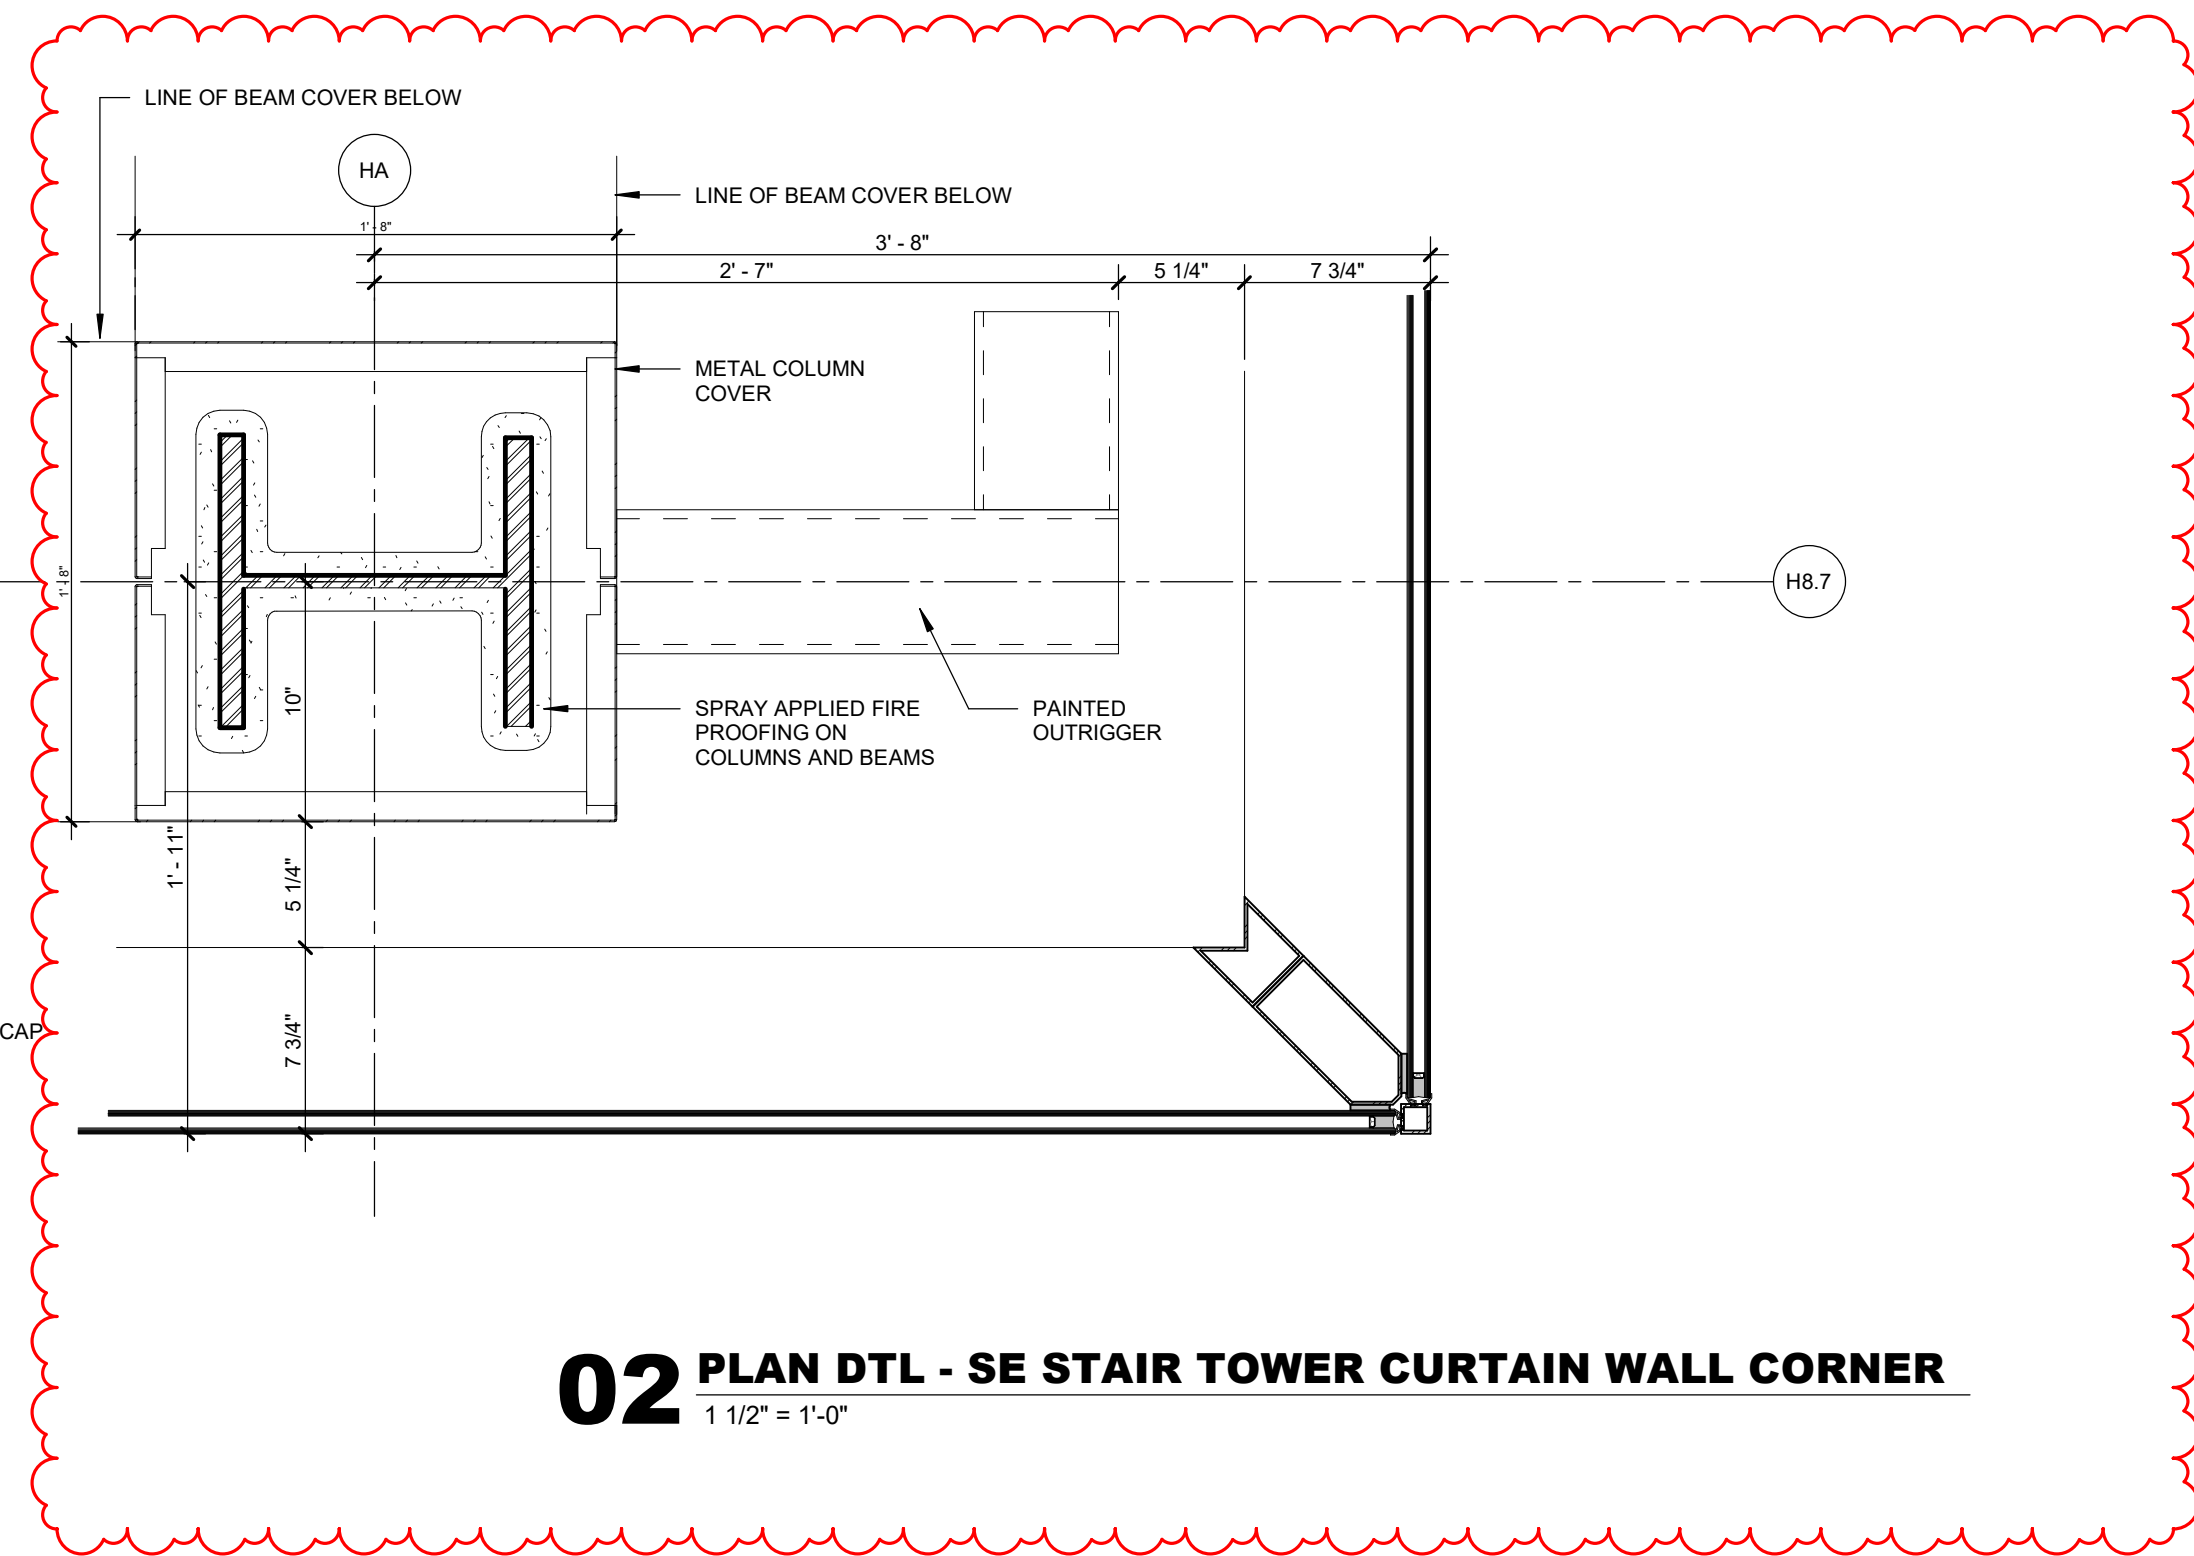

02 PLAN DTL - SE STAIR TOWER CURTAIN WALL CORNER
1 1/2" = 1'-0"

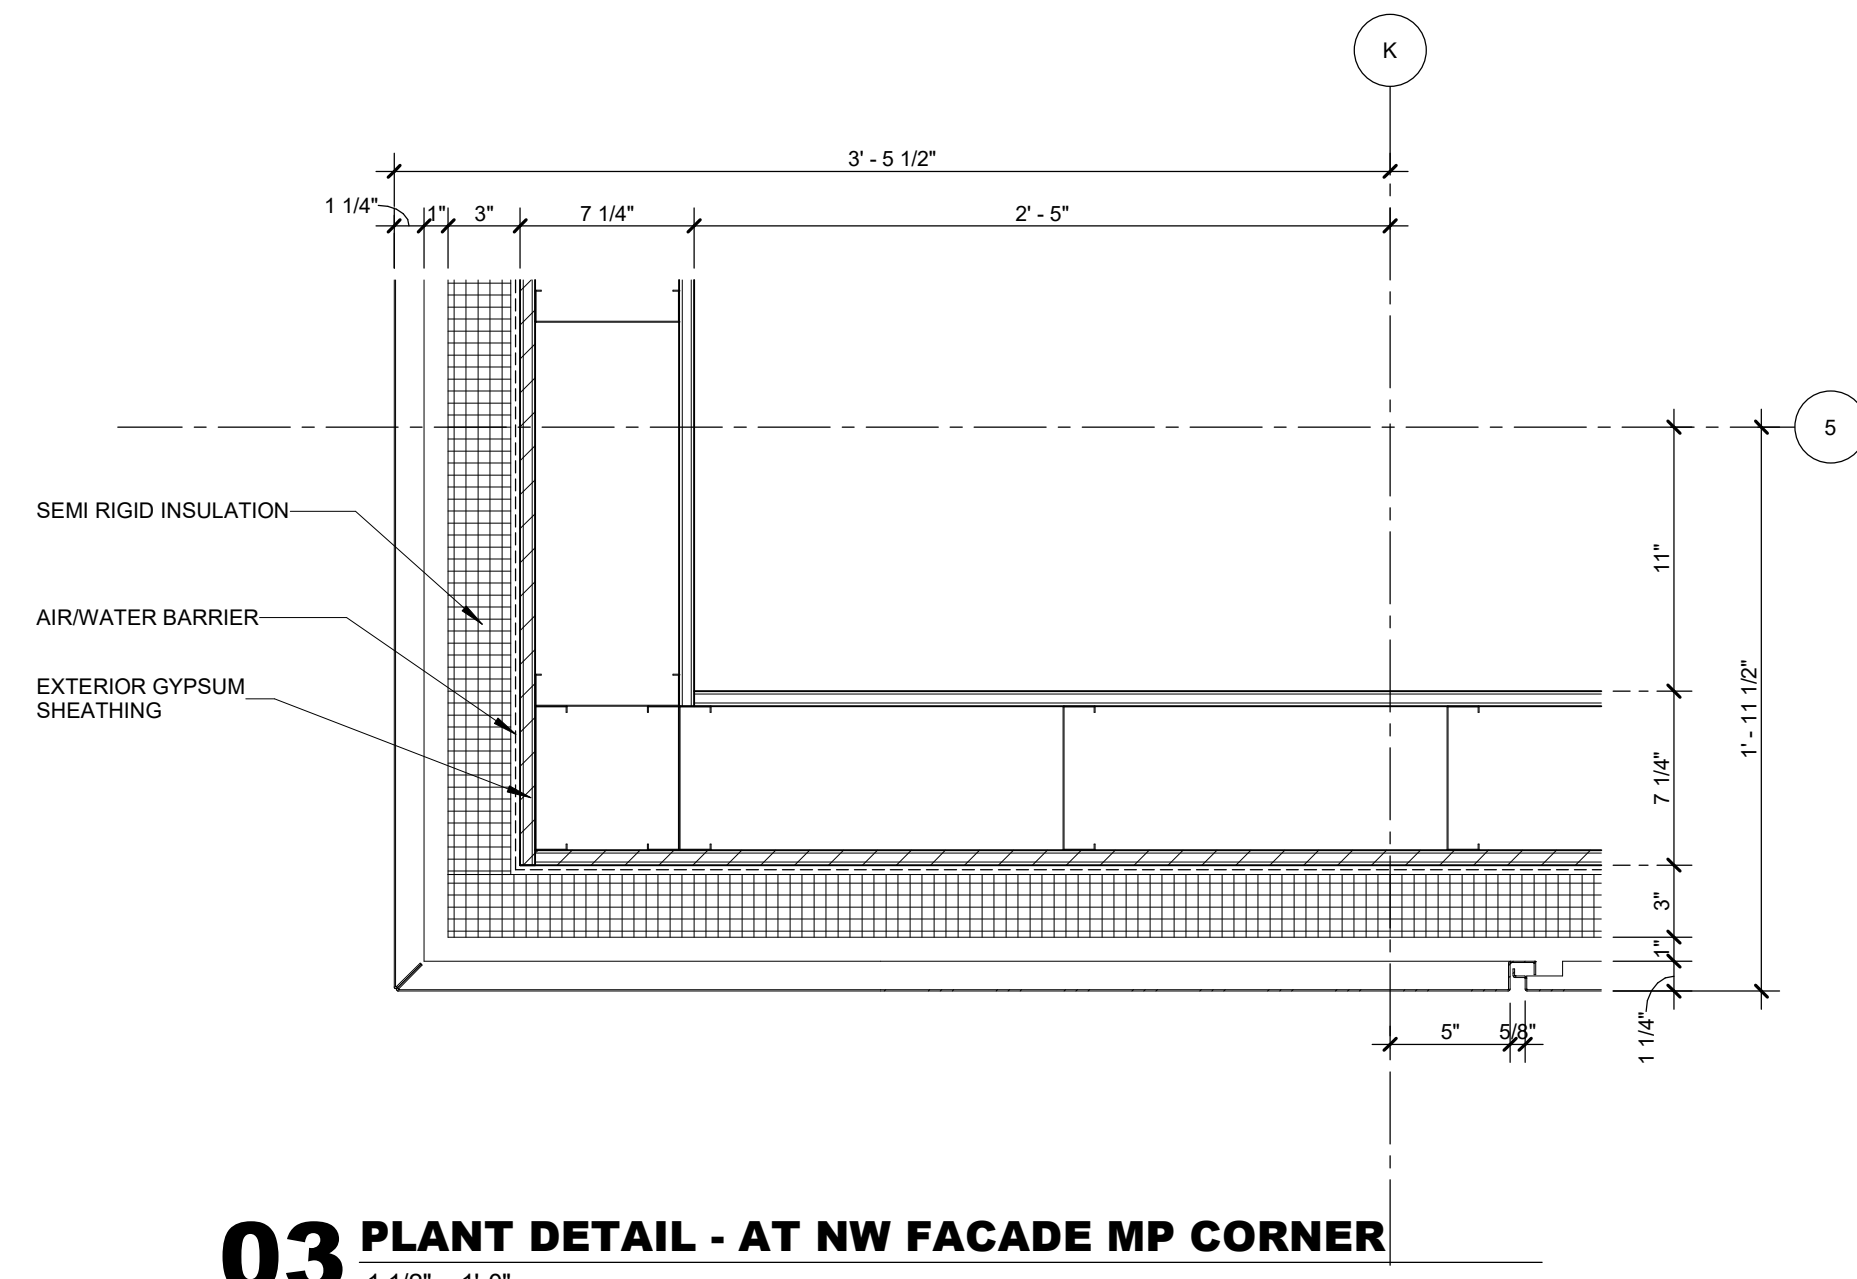

03 PLANT DETAIL - AT NW FACADE MP CORNER
1 1/2" = 1'-0"

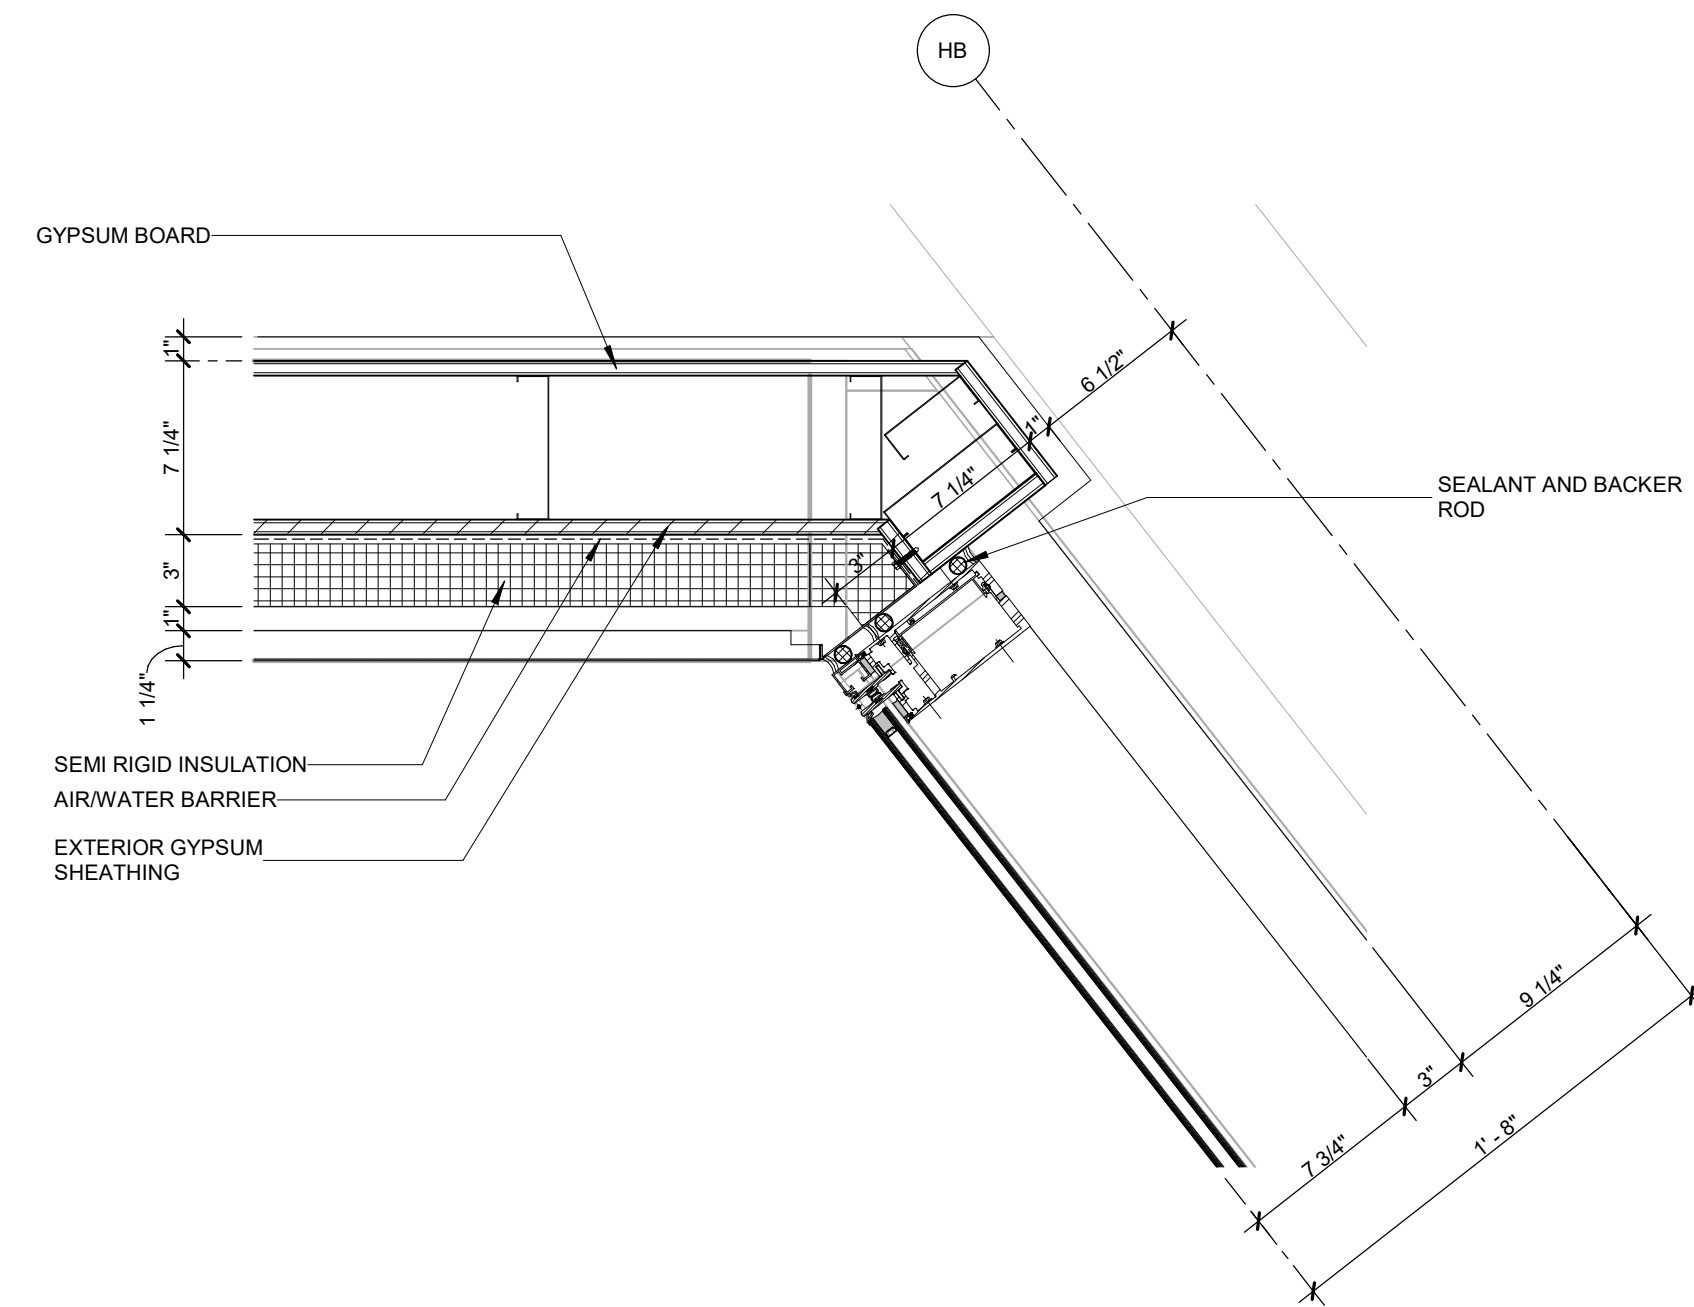

01 PLAN DTL - SE STAIR TOWER CURTAIN WALL TO SOUTH FACADE METAL PANEL WALL
1 1/2" = 1'-0"

RESERVE FOR DCA STAMP



ARCHITECT
HKS, P.C.
1250 I (EYE) STREET NW, SUITE 600
WASHINGTON, DC 20005
ASSOCIATE ARCHITECT / INTERIOR DESIGNER
ARRAY
1 WEST ELM STREET, SUITE 500
CONSHOHOCKEN, PA 19428
STRUCTURAL ENGINEER
O'DONNELL & NACCARATO
701 MARKET ST., #6000
PHILADELPHIA, PA 19106
MEP-FP / LOW VOLTAGE ENGINEER
BR+A CONSULTING ENGINEERS
2401 WALNUT ST SUITE 701
PHILADELPHIA, PA 19103
HIGHLAND ASSOCIATES
102 HIGHLAND AVE
CLARKS SUMMIT, PA 18411



OWNER
COOPER UNIVERSITY HEALTHCARE
1 COOPER PLAZA
CAMDEN, NJ 08103
PROJECT MANAGER
PURE PM
2026 RICHMOND STREET
PHILADELPHIA, PA 19134
CIVIL ENGINEER / LANDSCAPE
LANGAN
1818 MARKET STREET, SUITE 3300
PHILADELPHIA, PA 19103
SEAL & SINGATURE

KEY PLAN

REVISION	NO.	DESCRIPTION	DATE
1	BULLETIN #4		04/28/2025
	2	RFI 0416	11/14/2025

HKS PROJECT NUMBER
25695.100
DATE
10/15/2024
ISSUE
CORE & SHELL PERMIT SET
SHEET TITLE
EXTERIOR PLAN DETAILS


SHEET NO.

A7.32


BUILDING PERMIT NUMBER: 1111

© HKS, INC.


TITLE BLOCK VERSION: 20210830
MODEL: A:\models\Draws\25695.000_Cooper_Miller_Campus_Plan_2023\A_Cooper_TowerA_Enlarged_2023.rvt
PRINT DATE: 11/21/2025 3:29:55 PM
TEMPLATE VERSION: 23.0.3
© HKS, INC.

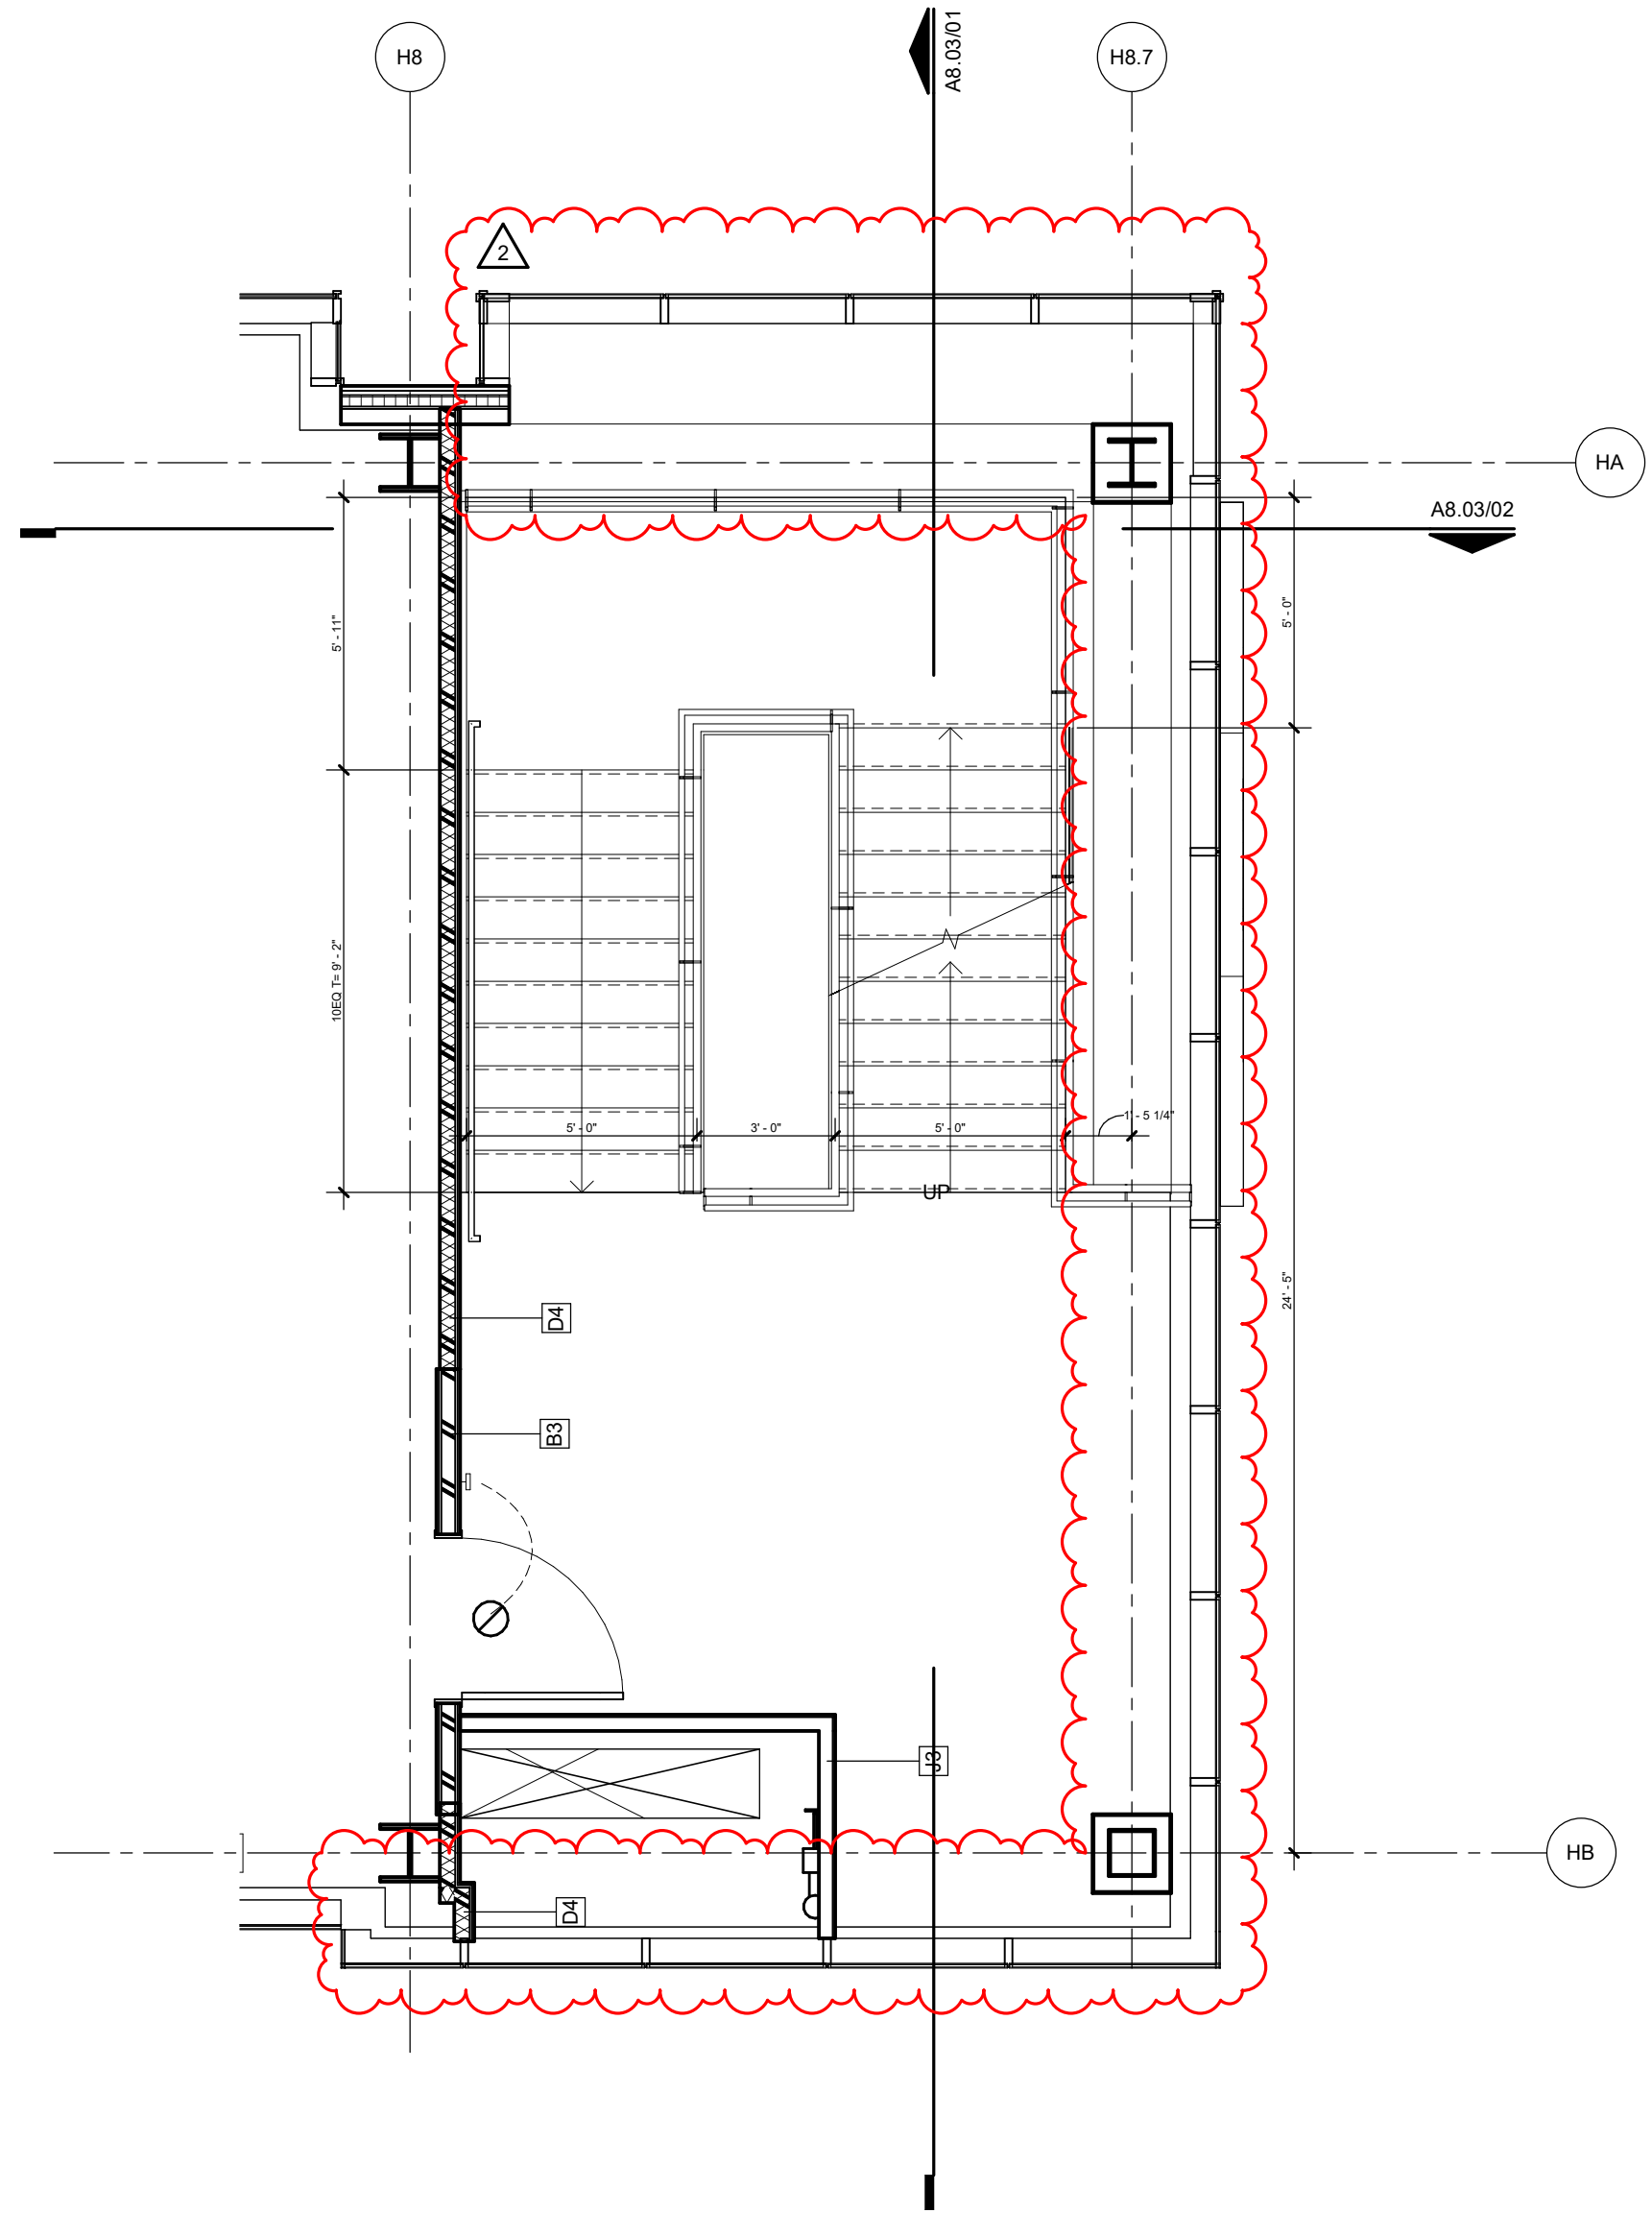


06 ENLARGED PLAN - ST02 - LEVEL 10
1/4" = 1'-0"

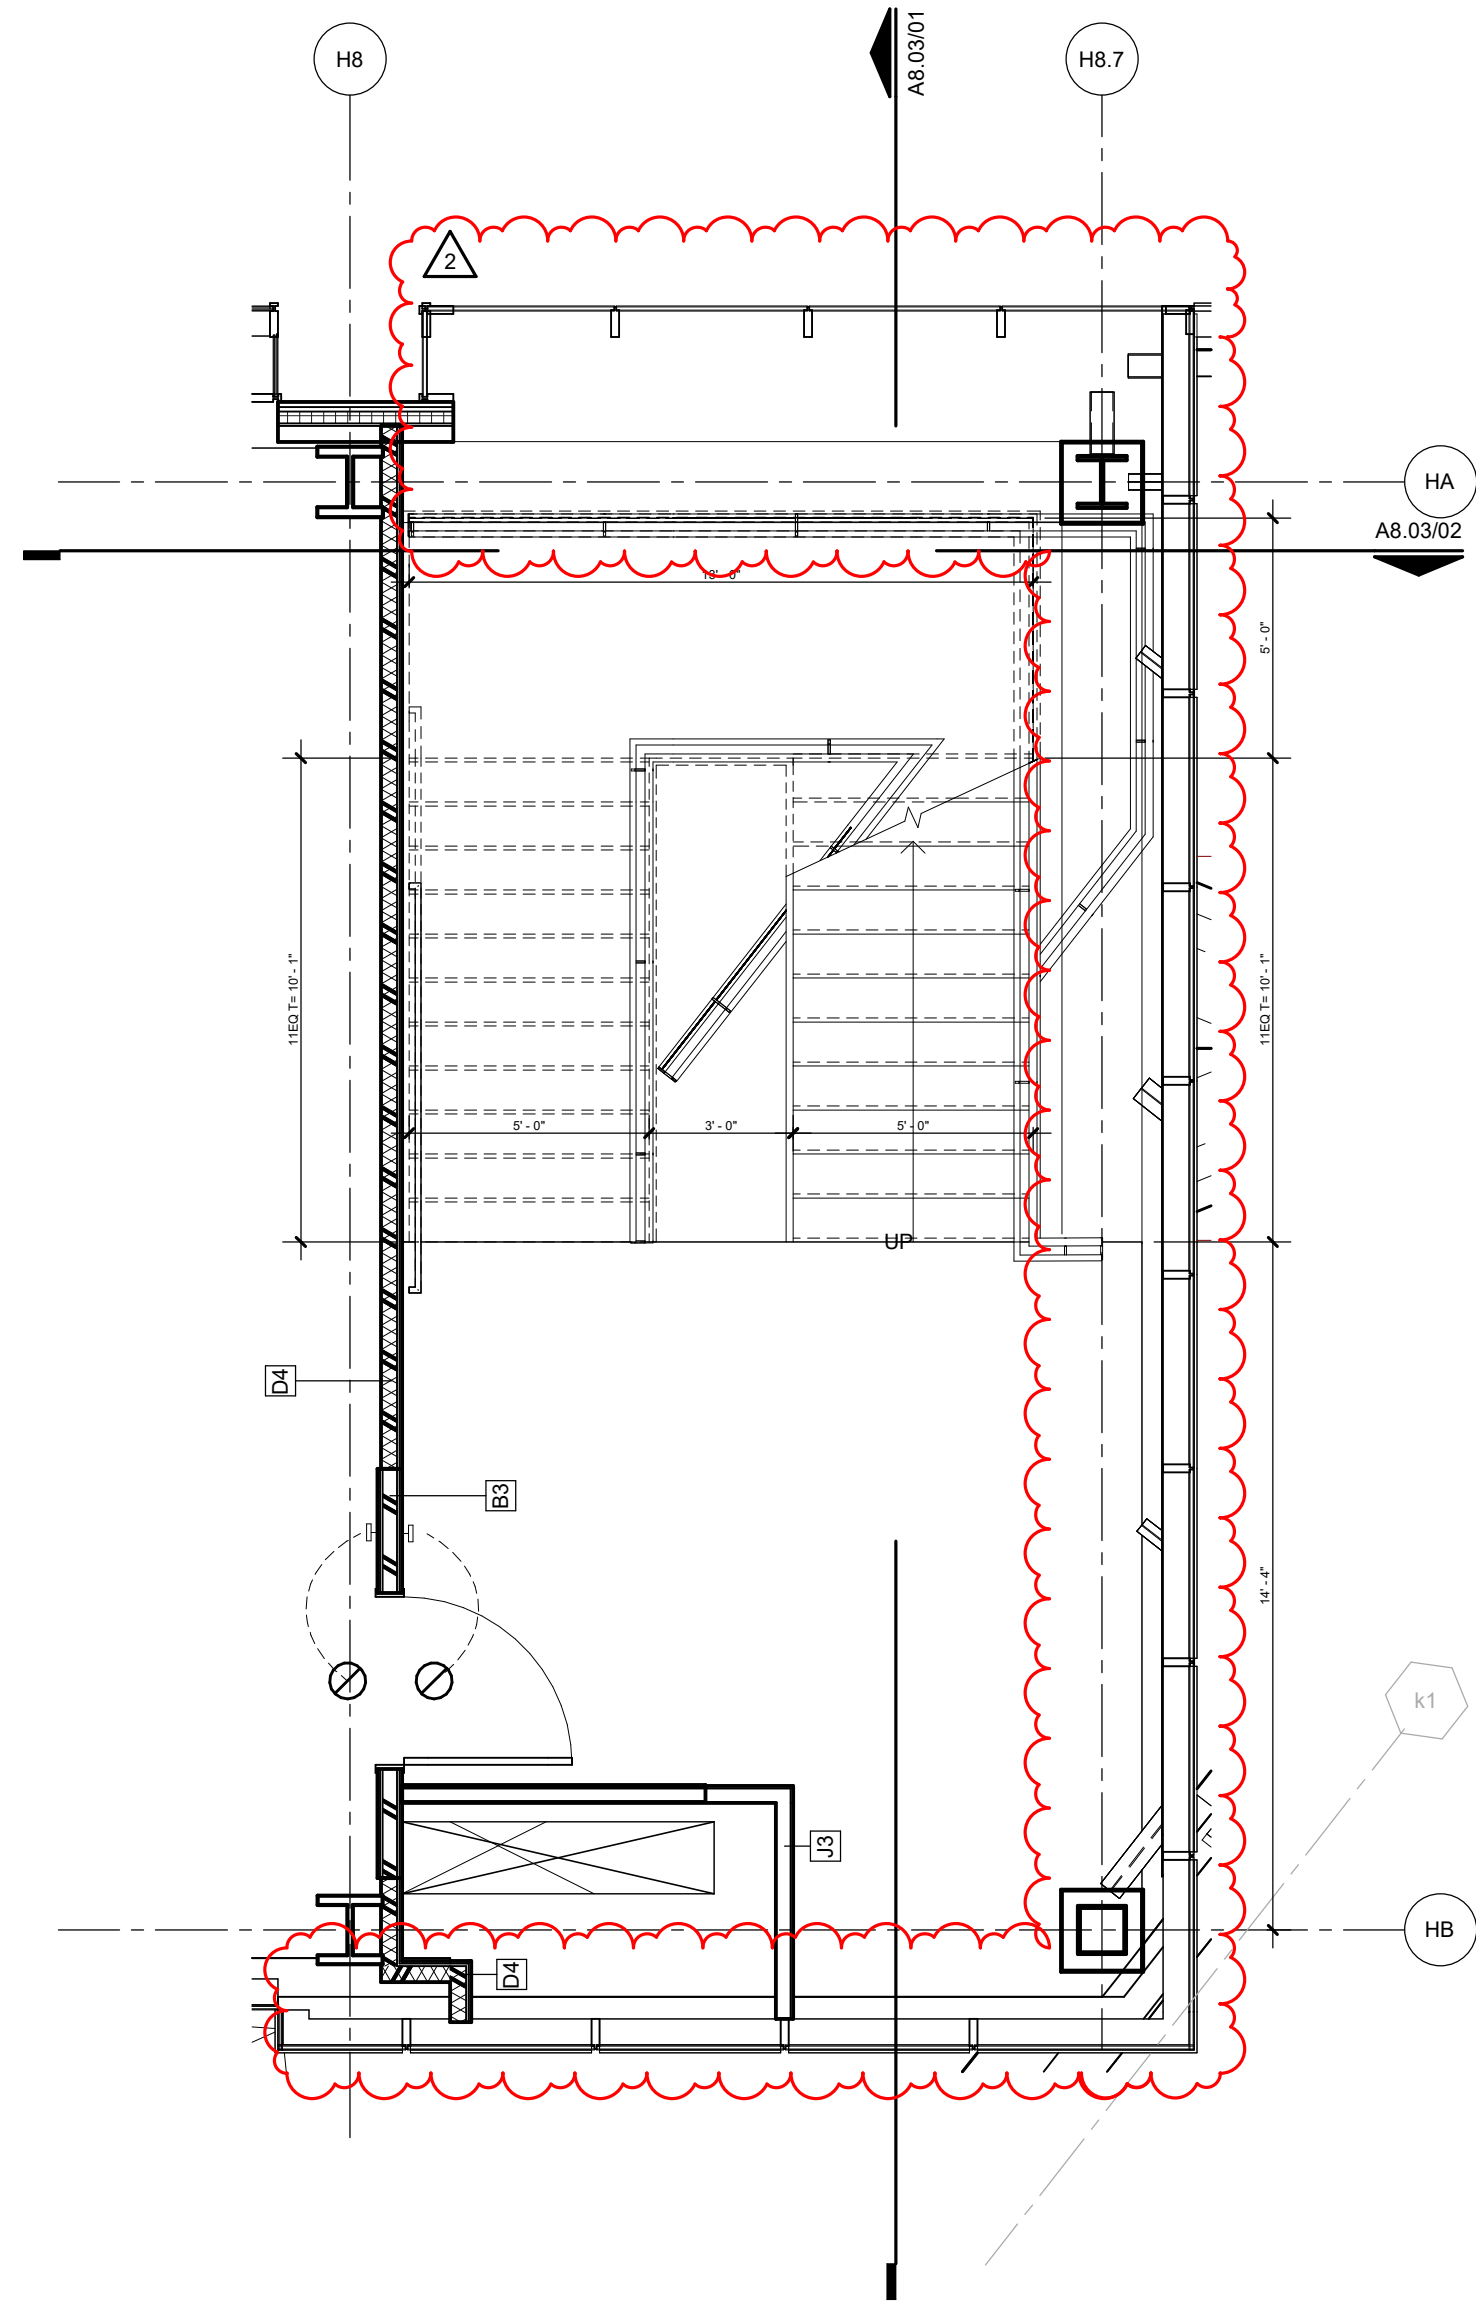


04 ENLARGED PLAN - ST02 - LEVEL 03
1/4" = 1'-0"

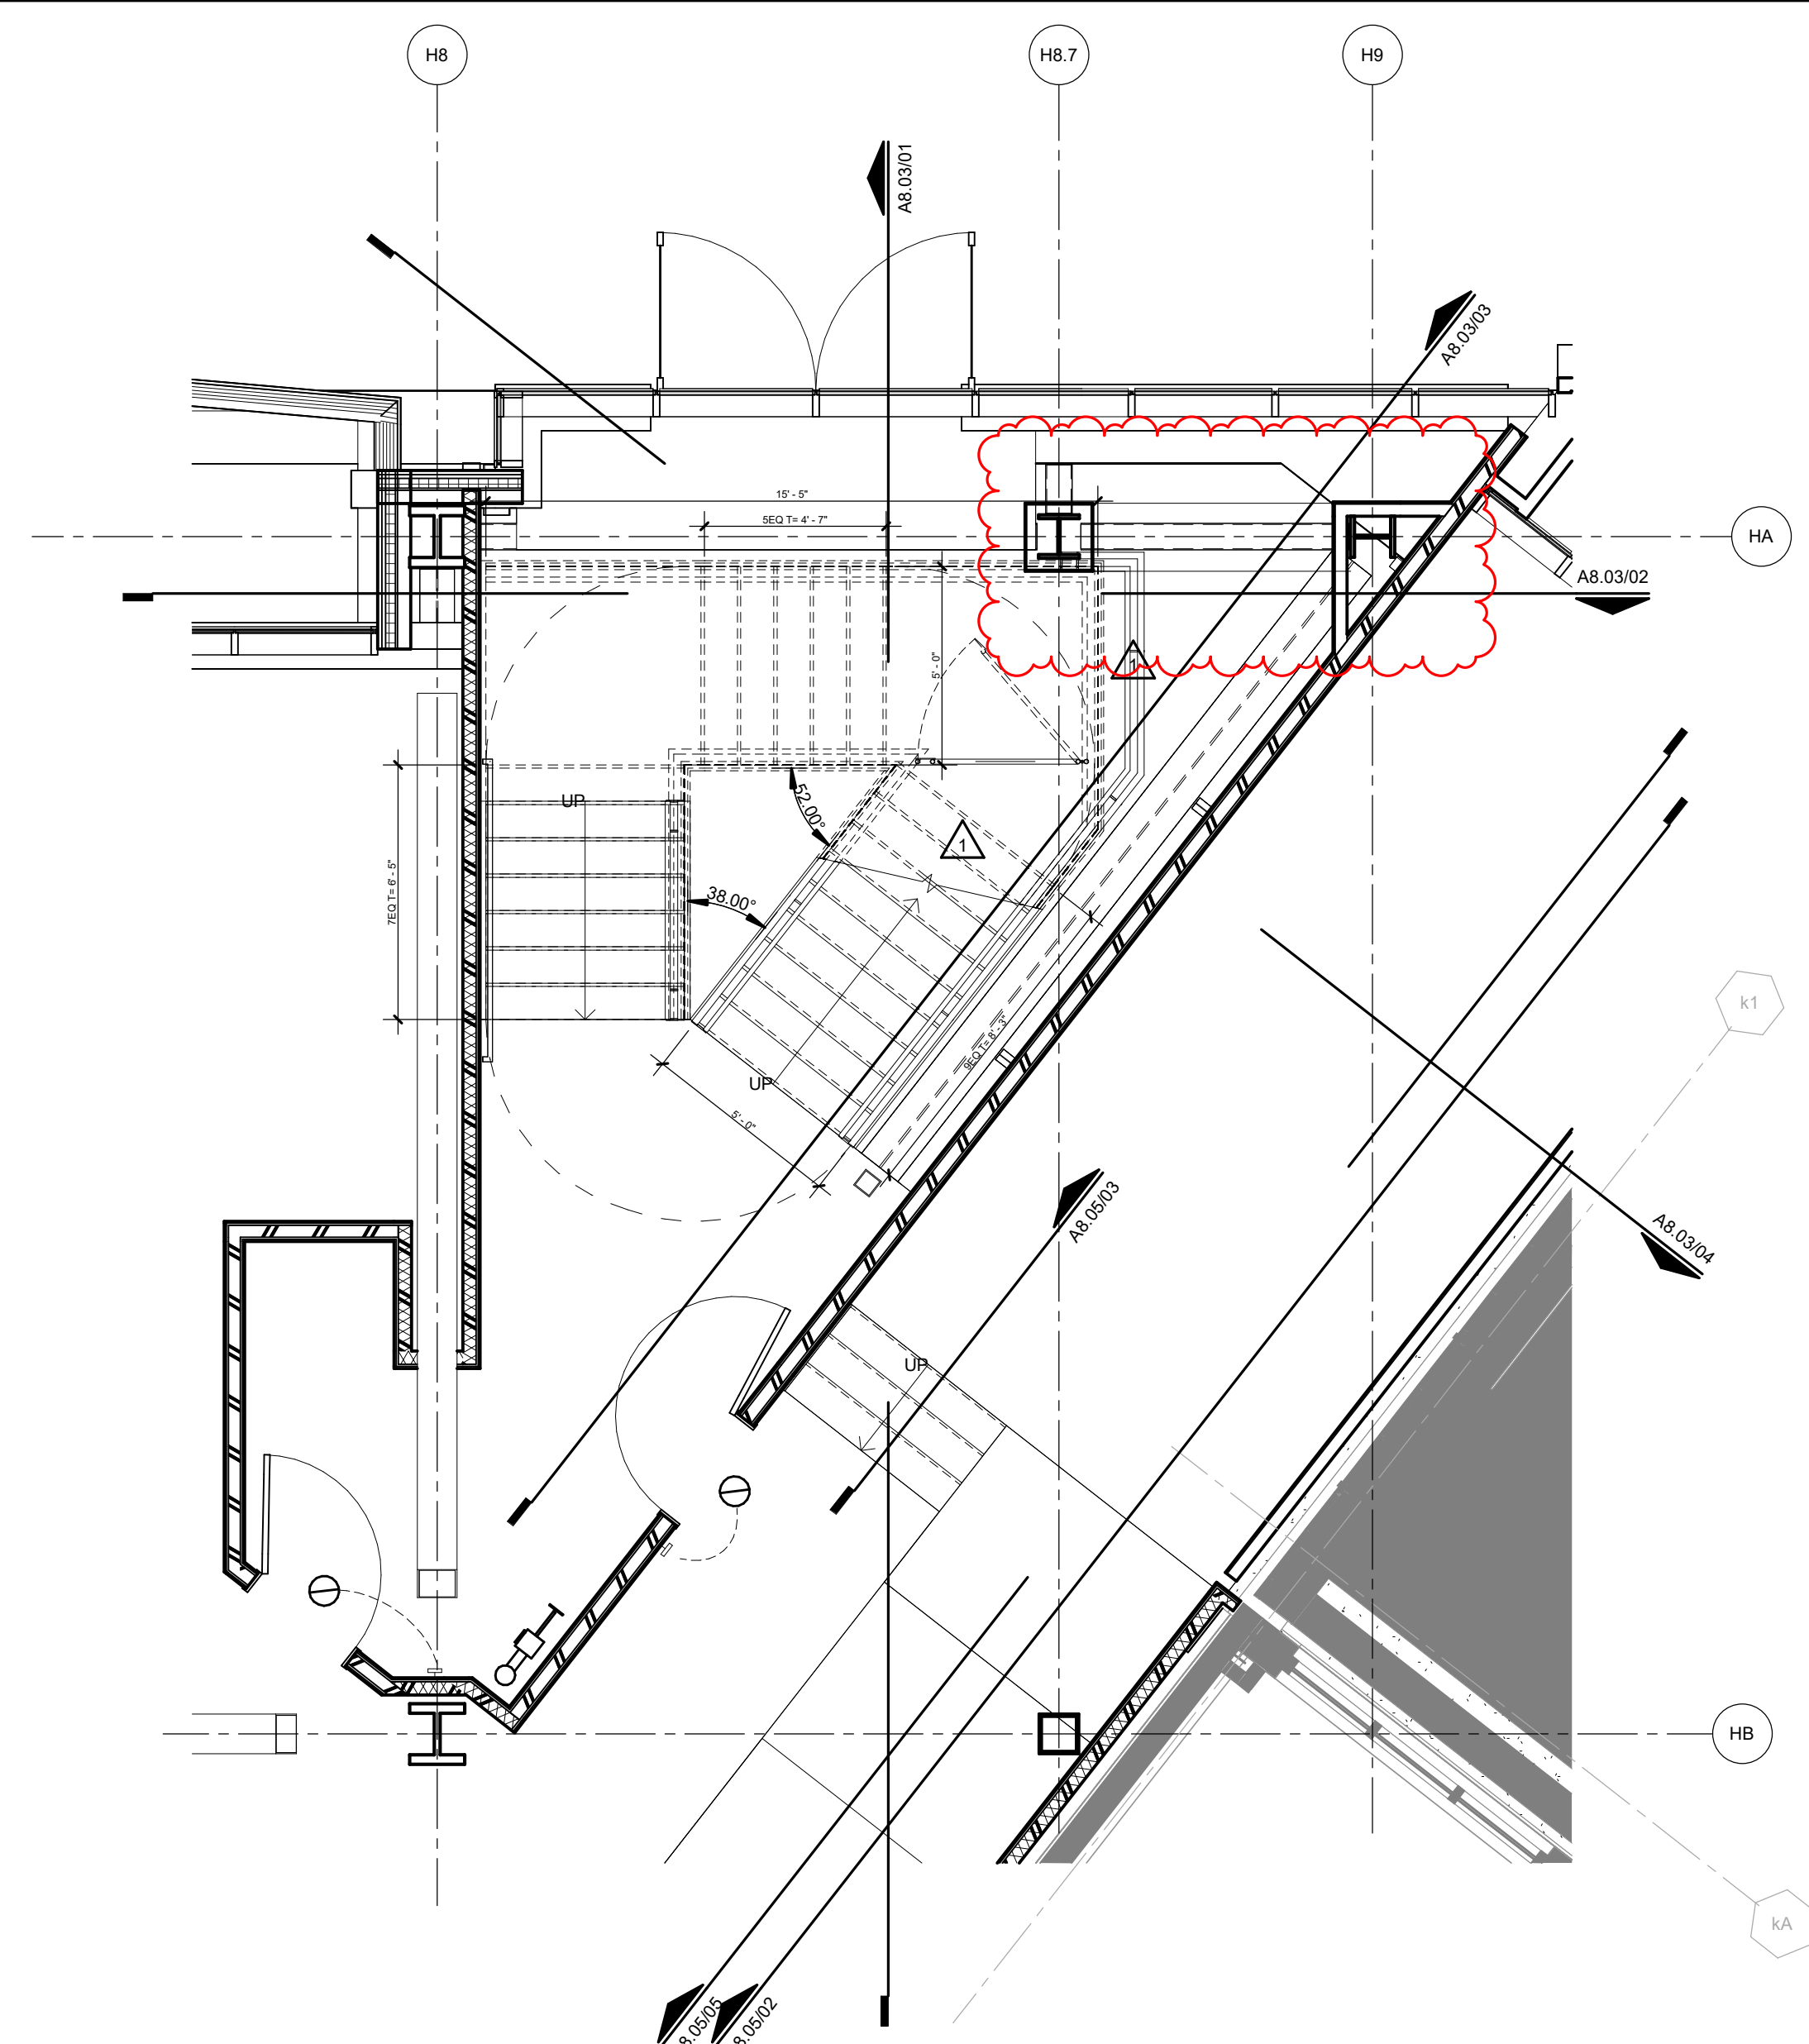


02 ENLARGED PLAN - ST02 - LEVEL 01
1/4" = 1'-0"

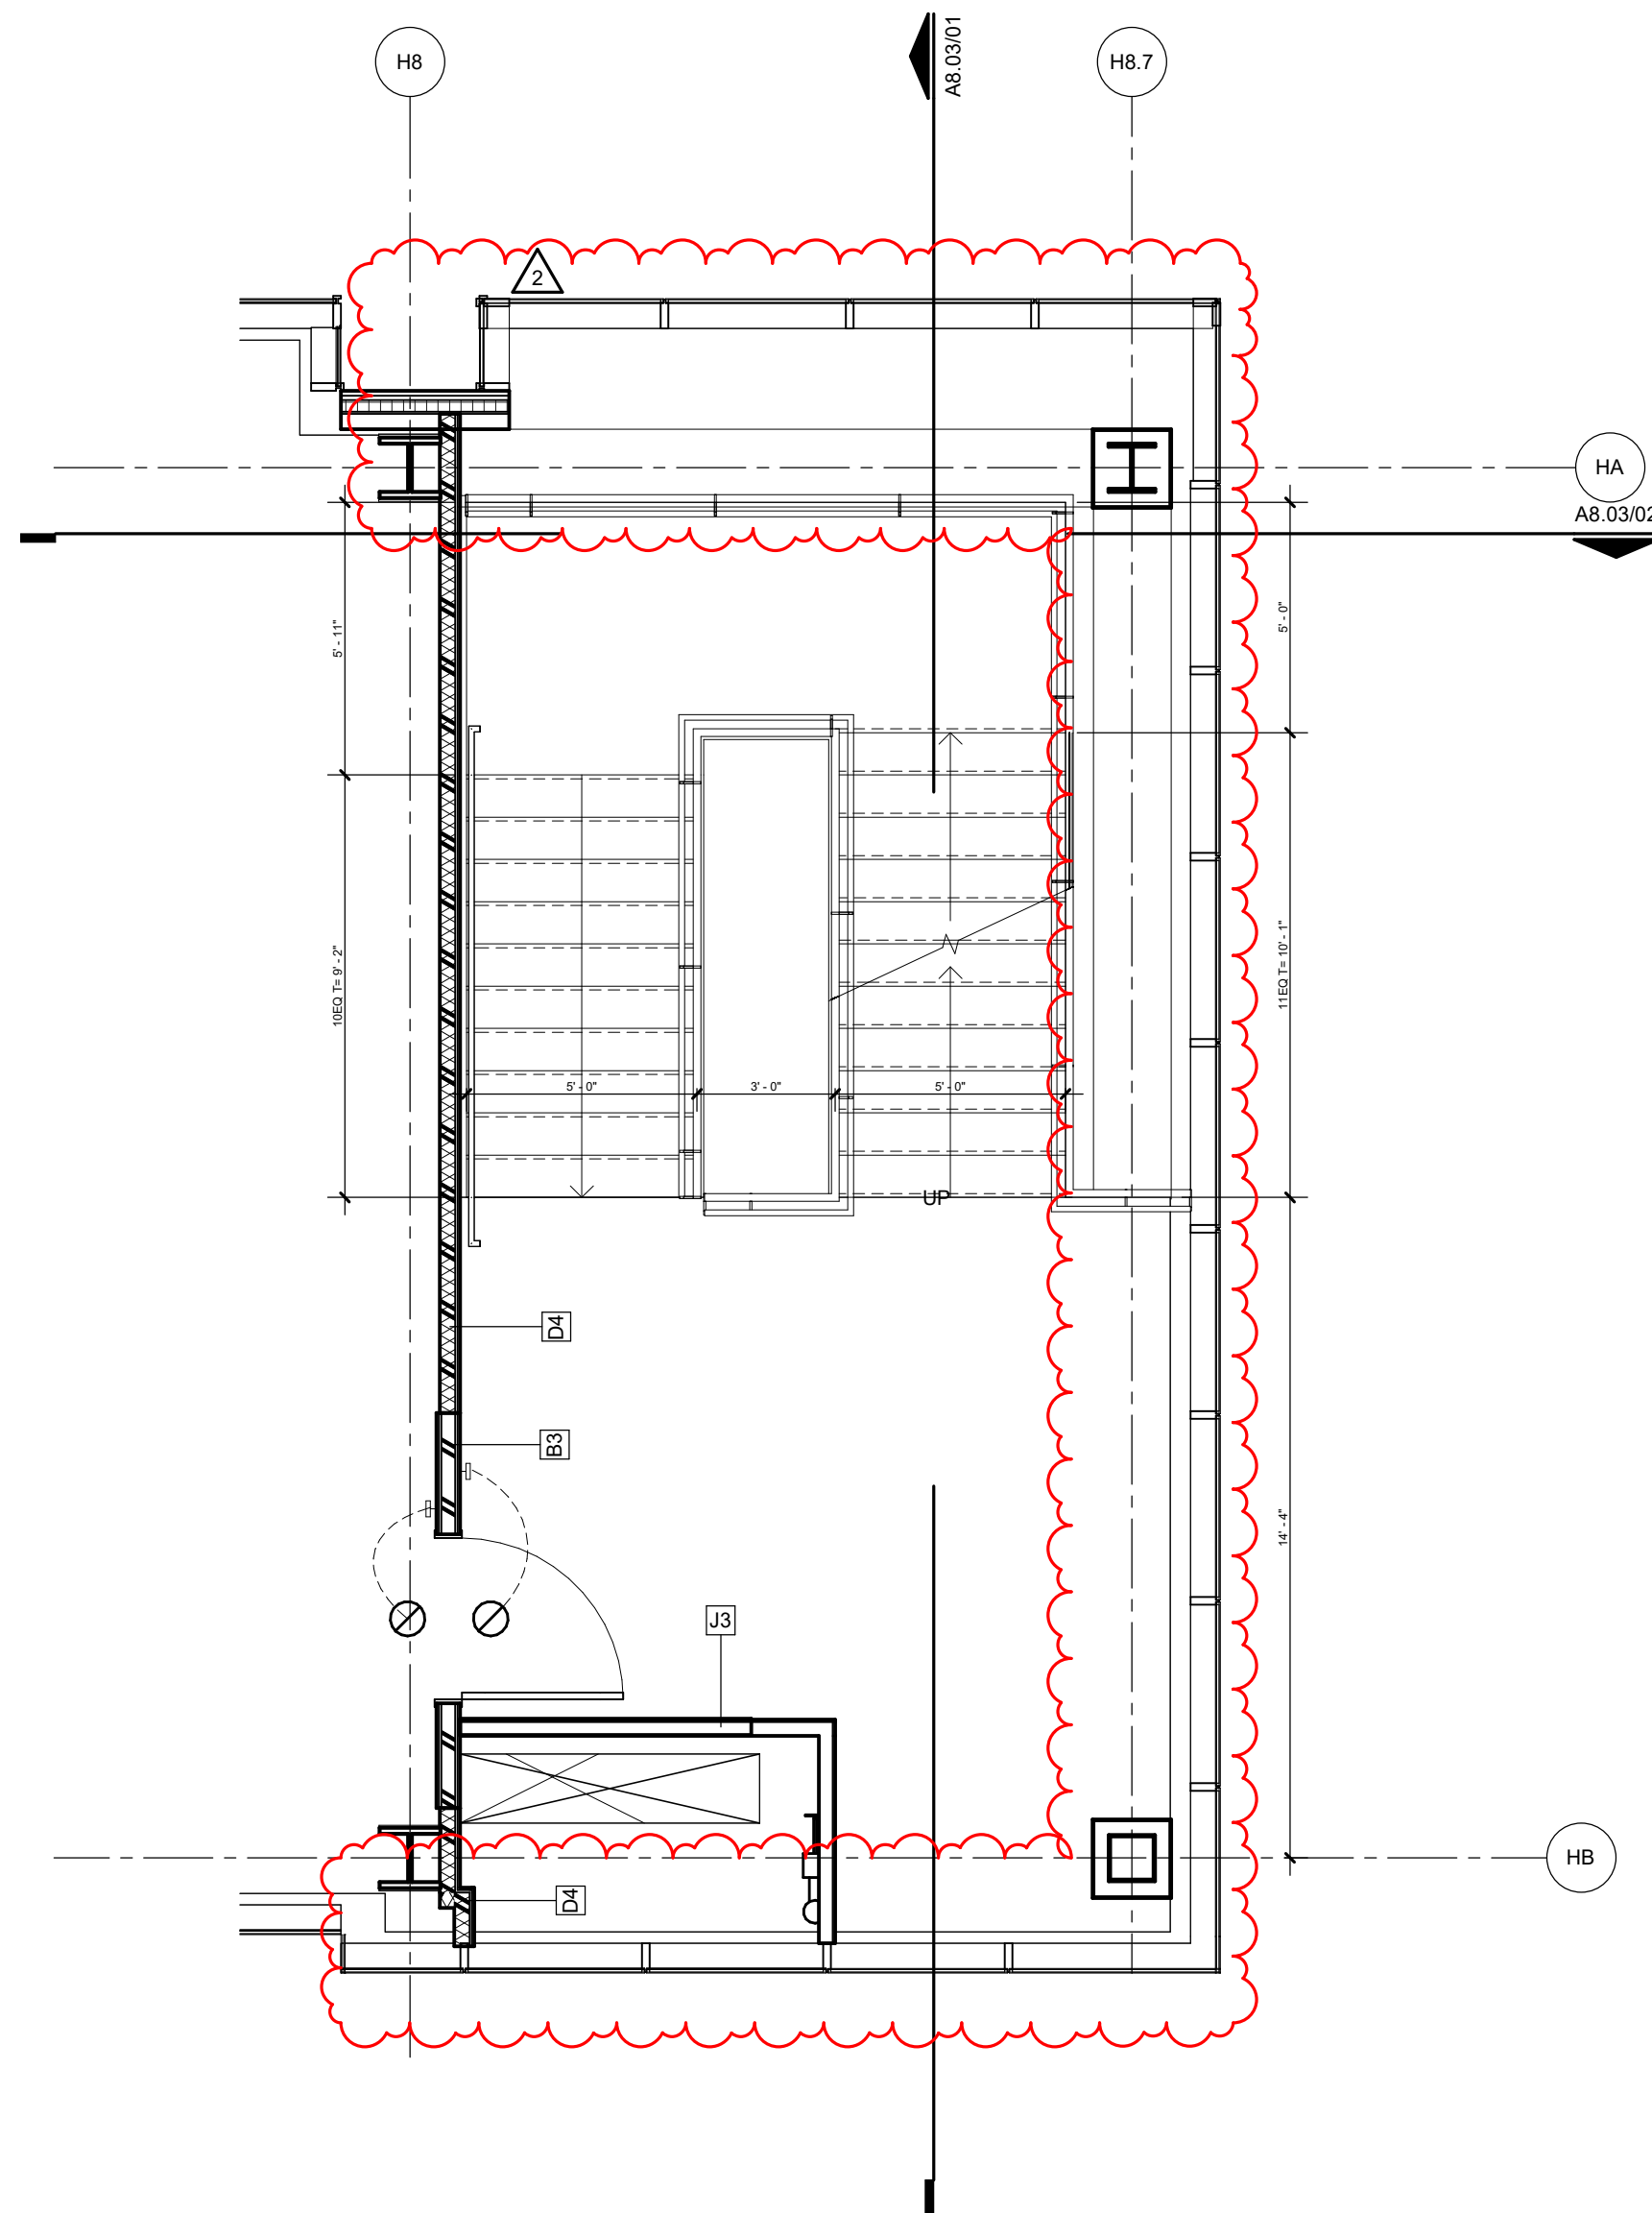

05 ENLARGED PLAN - ST02 - TYPICAL LEVEL 04-09
1/4" = 1'-0"

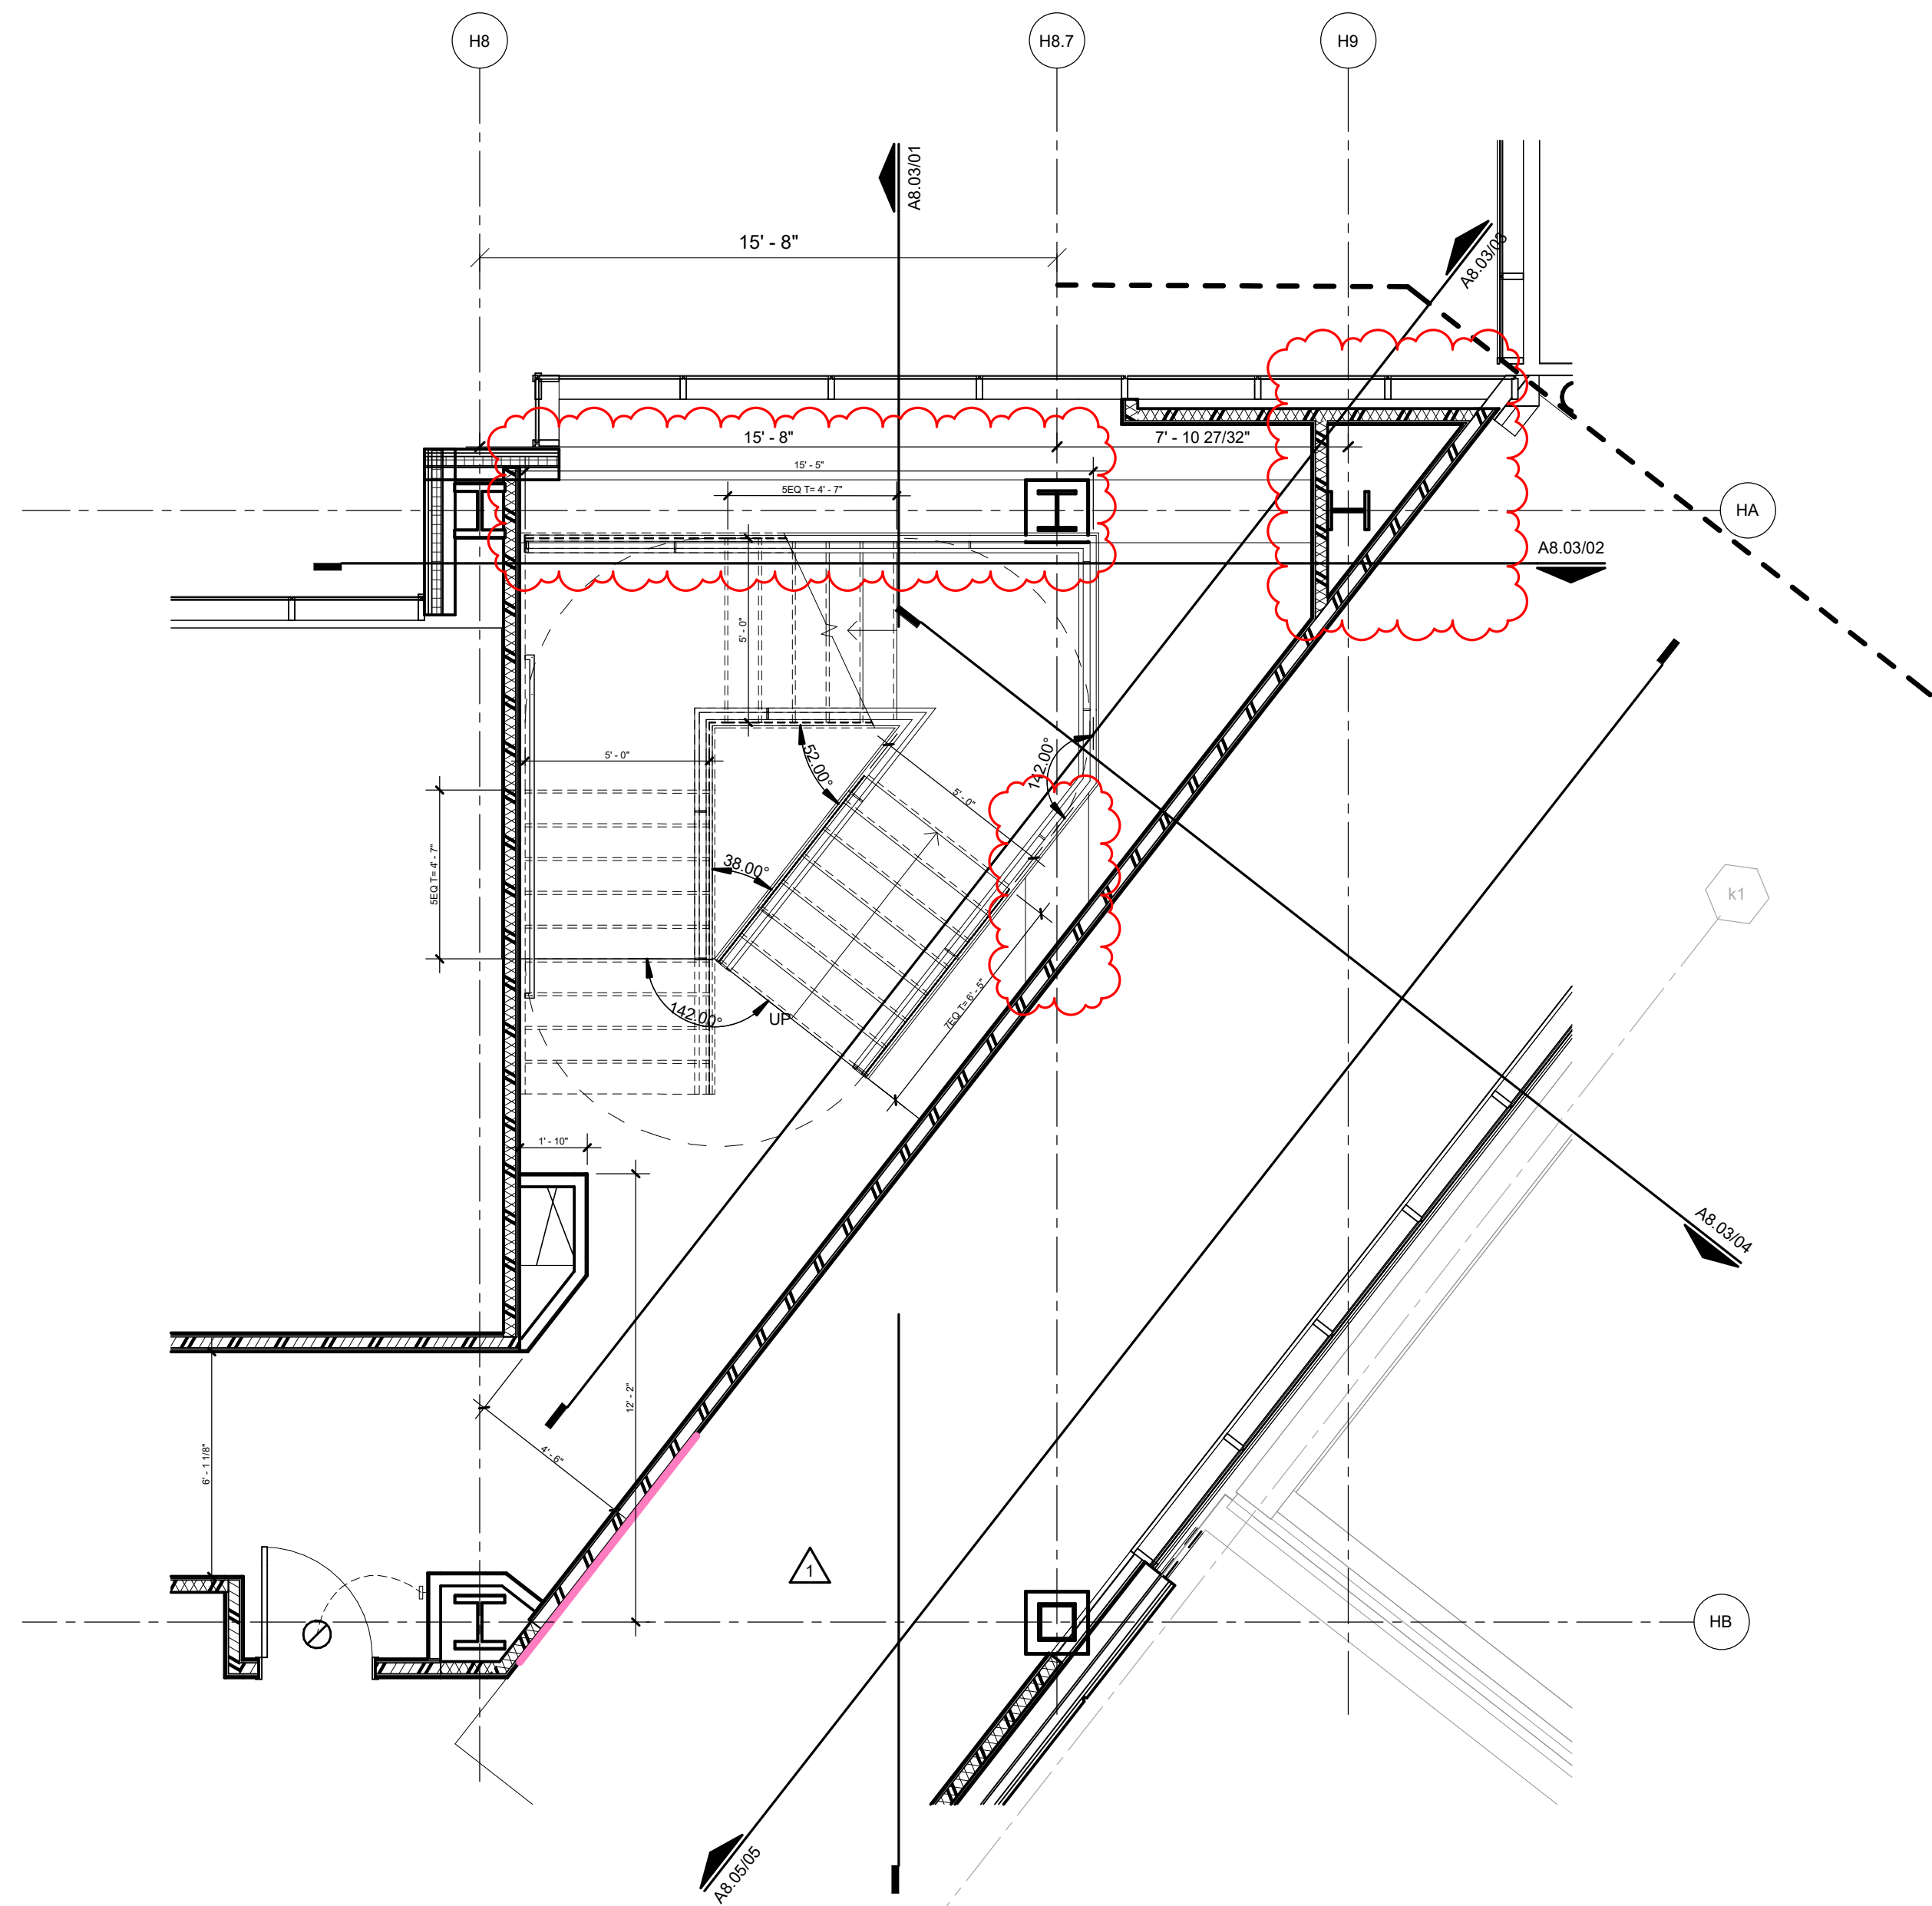

03 ENLARGED PLAN - ST02 - LEVEL 02
1/4" = 1'-0"

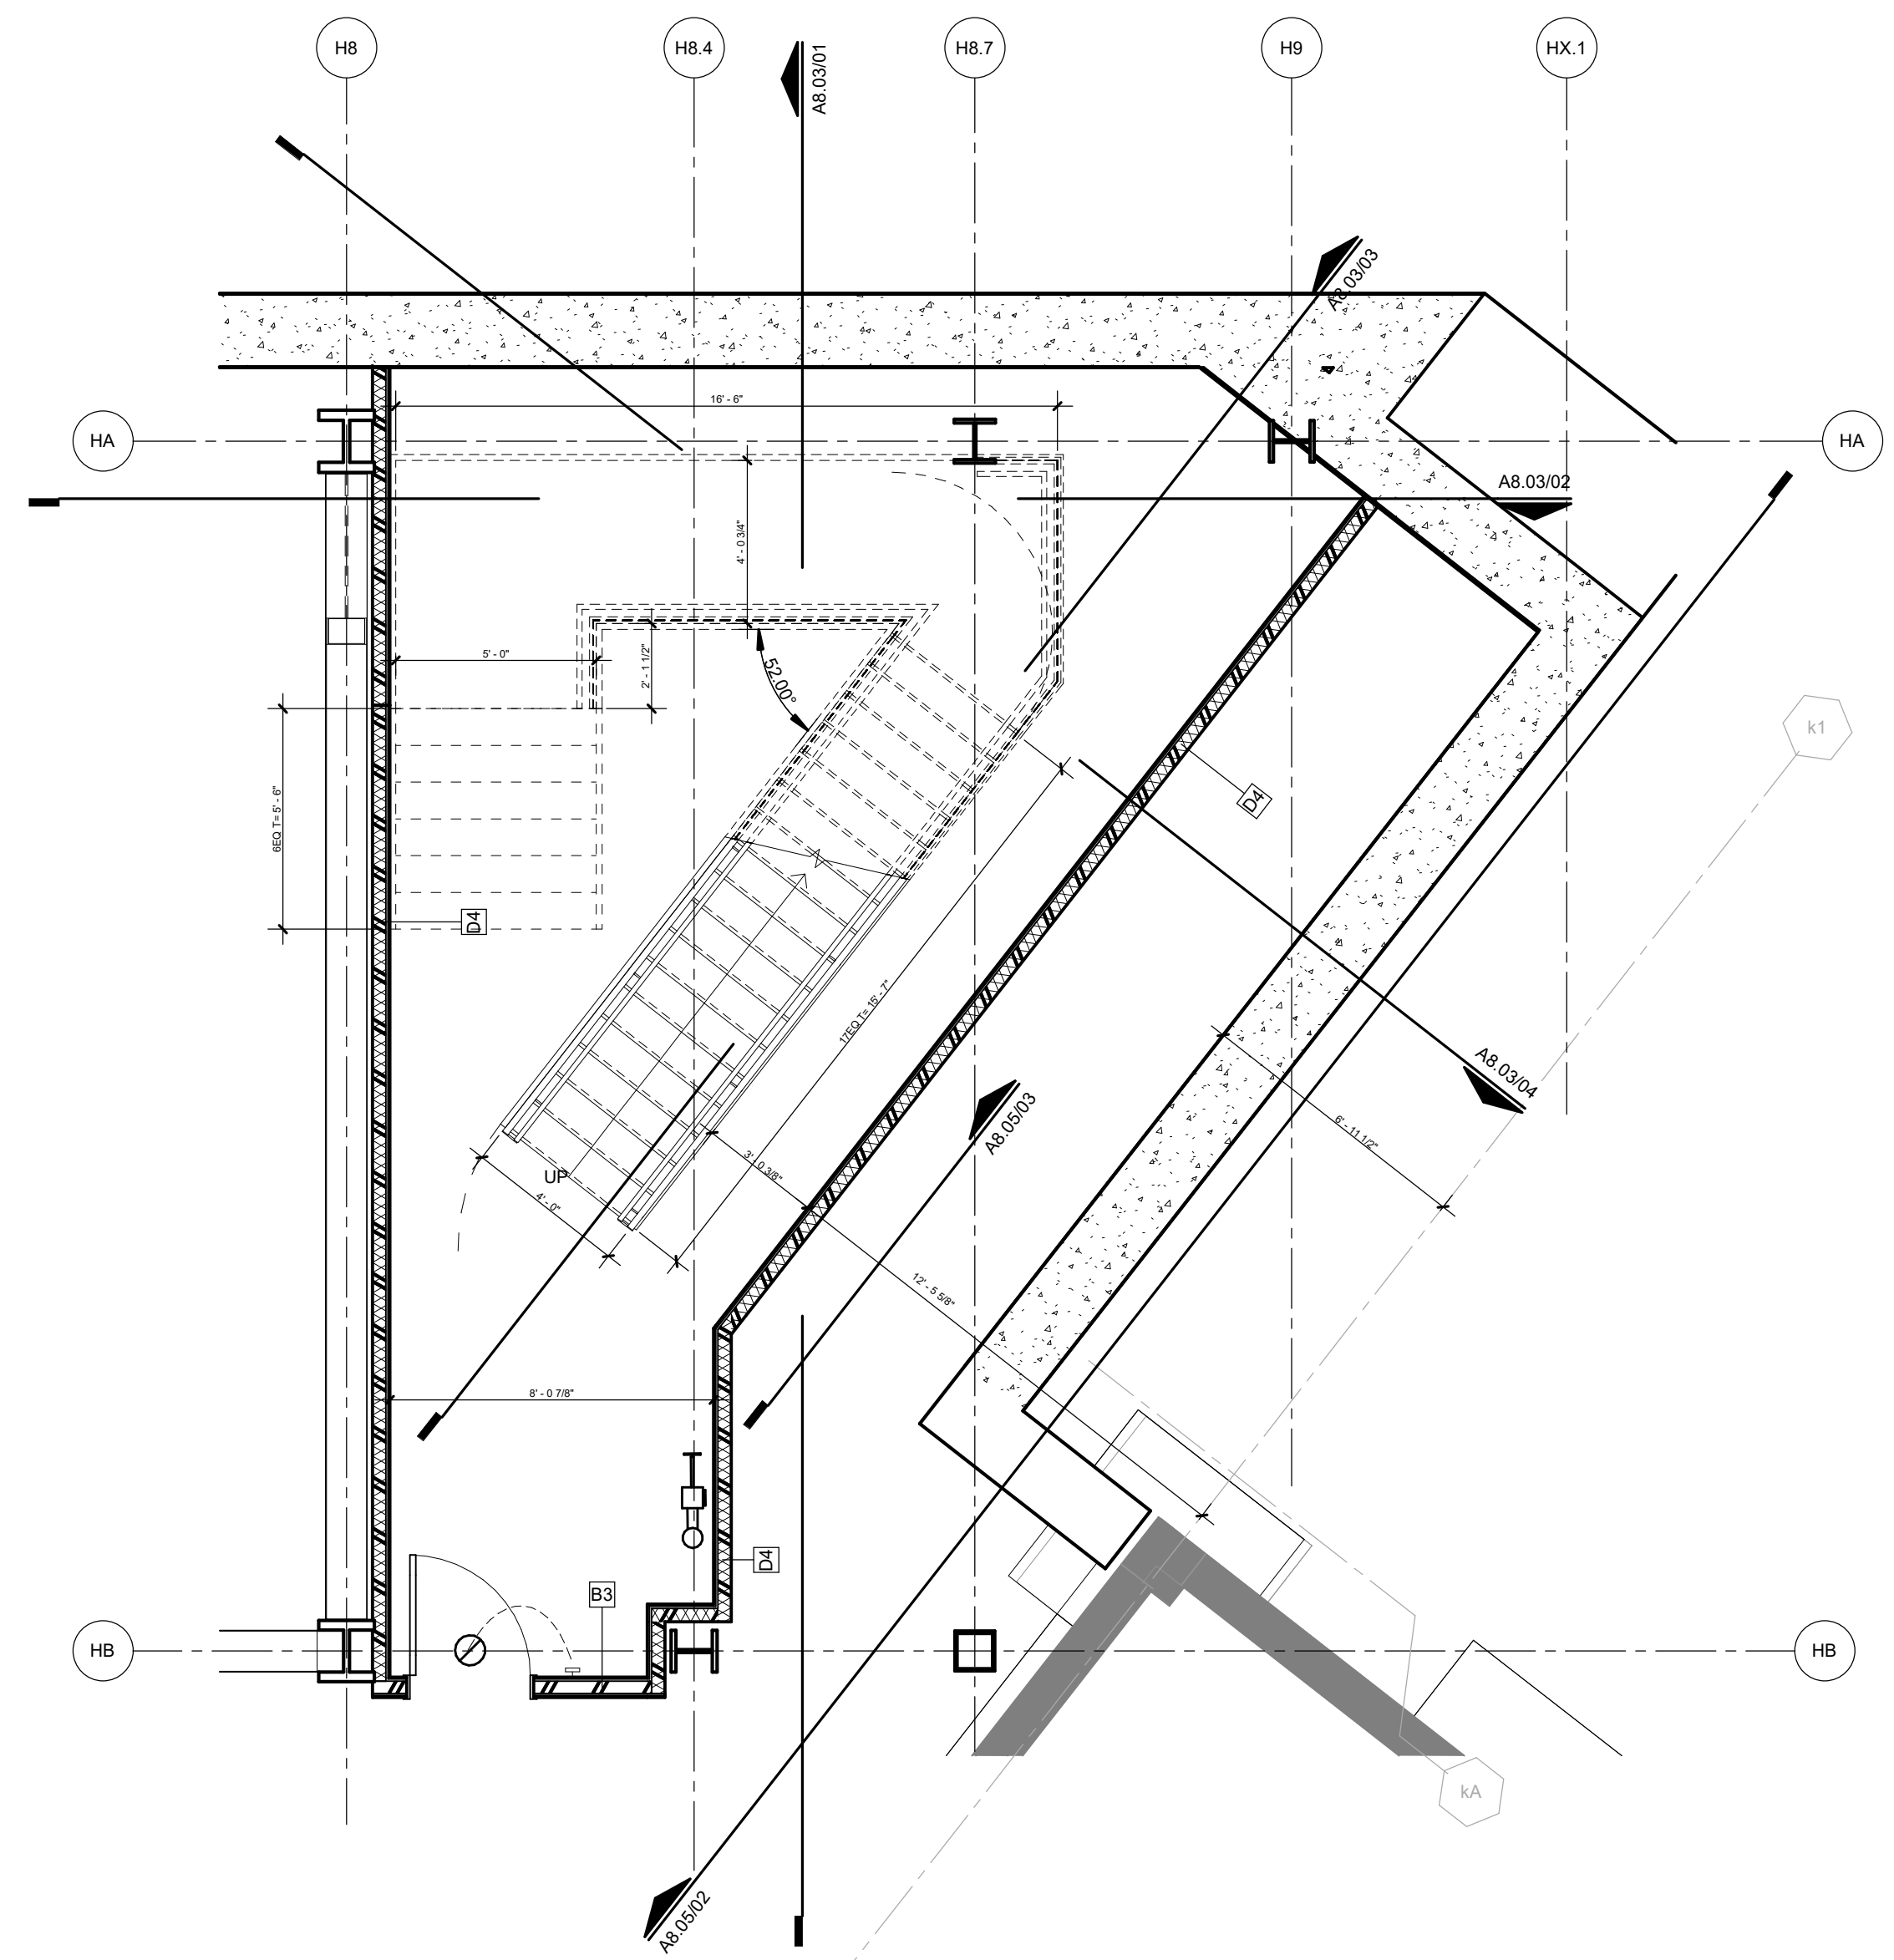

01 ENLARGED PLAN - LEVEL BASEMENT
1/4" = 1'-0"

RESERVE FOR DCA STAMP




ARCHITECT
HKS, P.C.
1250 I (EYE) STREET NW, SUITE 600
WASHINGTON, DC 20005
ASSOCIATE ARCHITECT / INTERIOR DESIGNER
ARRAY
1 WEST ELM STREET, SUITE 500
CONSHOHOCKEN, PA 19028
STRUCTURAL ENGINEER
O'DONNELL & NACCARATO
701 MARKET ST., #6000
PHILADELPHIA, PA 19106
MEP-FP / LOW VOLTAGE ENGINEER
BR+A CONSULTING ENGINEERS
2401 WALNUT ST SUITE 701
PHILADELPHIA, PA 19103
HIGHLAND ASSOCIATES
102 HIGHLAND AVE
CLARKS SUMMIT, PA 18411

Cooper University Health Care
COOPER UNIVERSITY HOSPITAL - TOWER A
PROJECT ADDRESS: 1 COOPER PLAZA, CAMDEN, NJ 08103

OWNER
COOPER UNIVERSITY HEALTHCARE
1 COOPER PLAZA
CAMDEN, NJ 08103
PROJECT MANAGER
PURE PM
2026 RICHMOND STREET
PHILADELPHIA, PA 19134
CIVIL ENGINEER / LANDSCAPE
LANGAN
1818 MARKET STREET, SUITE 3300
PHILADELPHIA, PA 19103
SEAL & SINGATURE

KEY PLAN

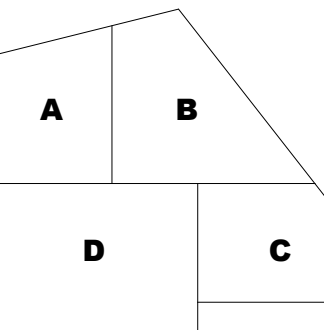


REVISION	NO.	DESCRIPTION	DATE
1	BULLETIN #2		01/23/2025
2	RFI 0416		11/14/2025


HKS PROJECT NUMBER
25695.100
DATE
10/15/2024
ISSUE
CORE & SHELL PERMIT SET
SHEET TITLE
STAIR PLANS AND SECTIONS

SHEET NO.


A8.02

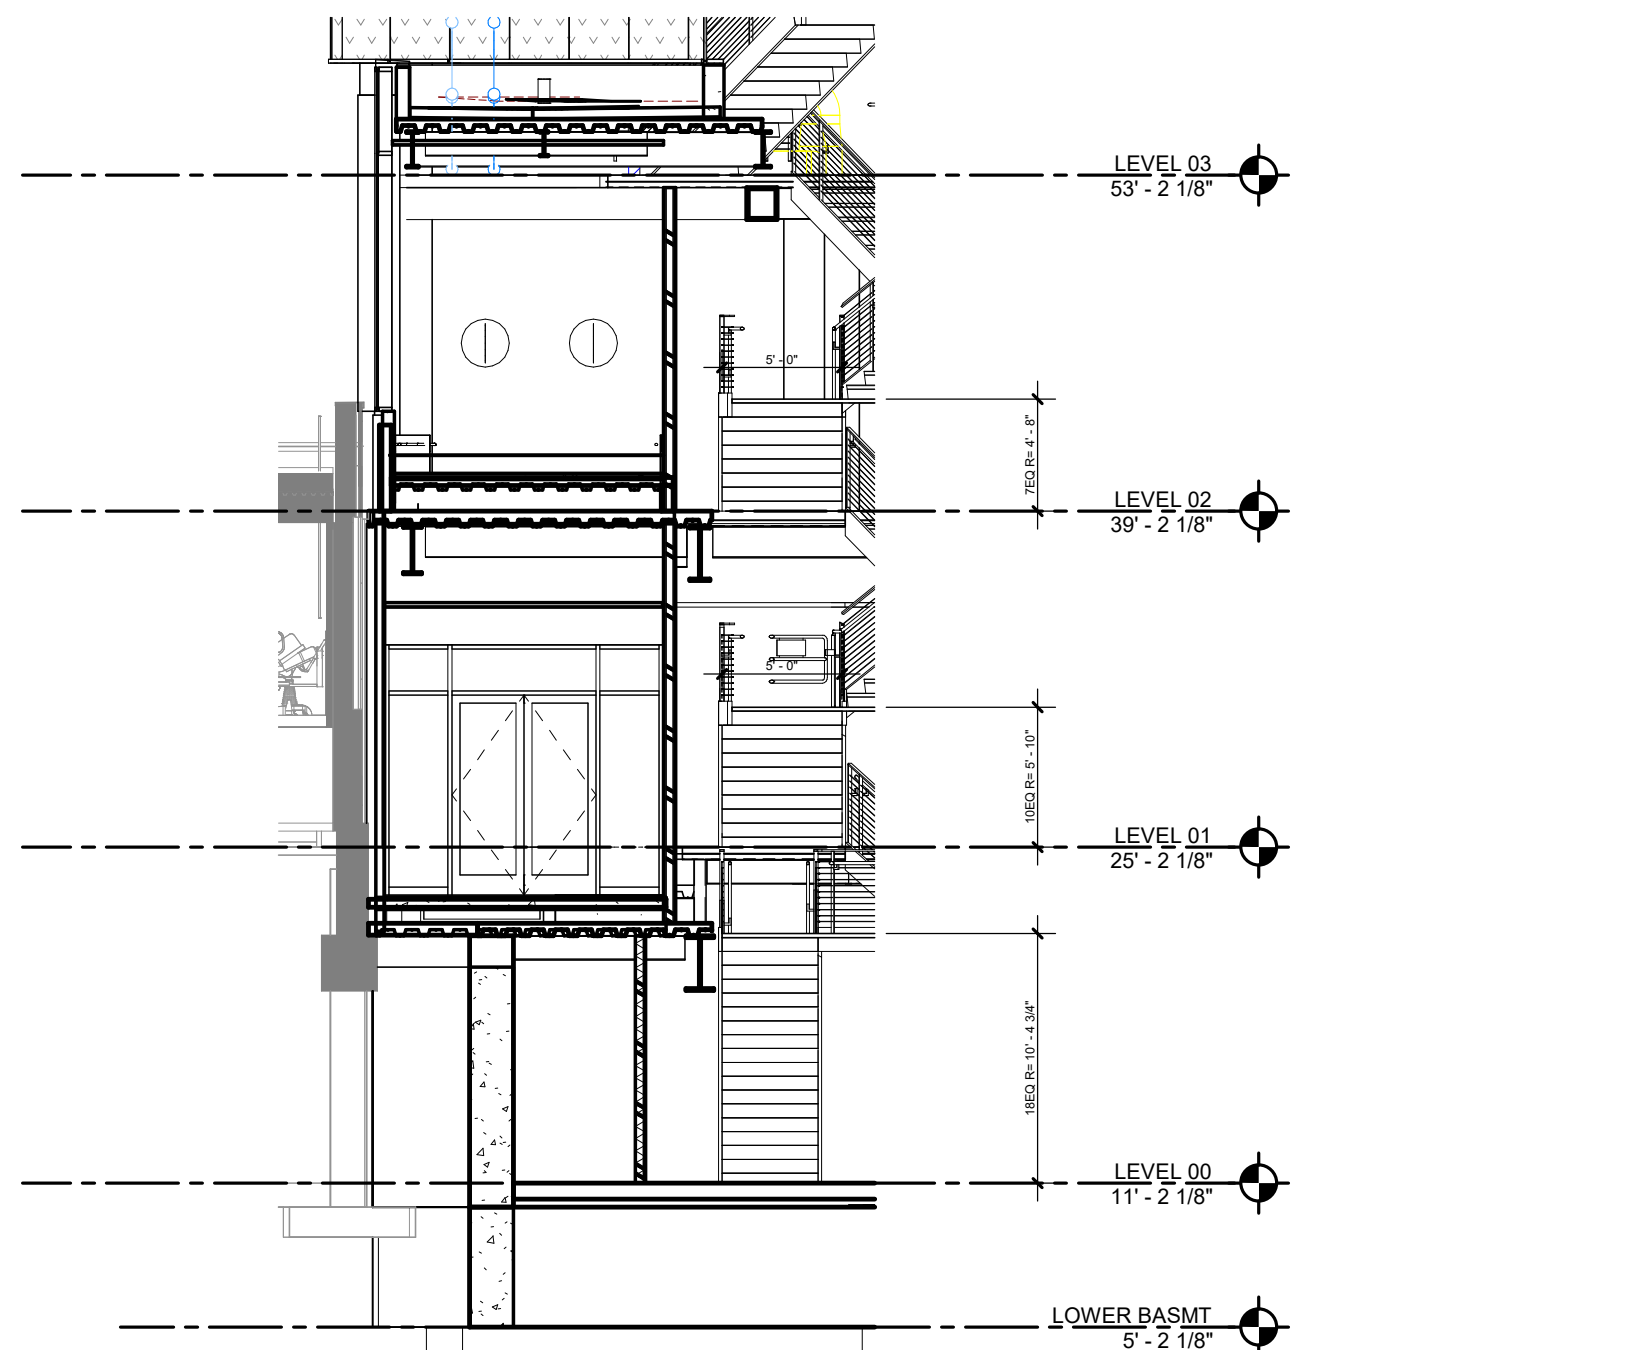


04 SE STAIR SECTION 04
1/8" = 1'-0"

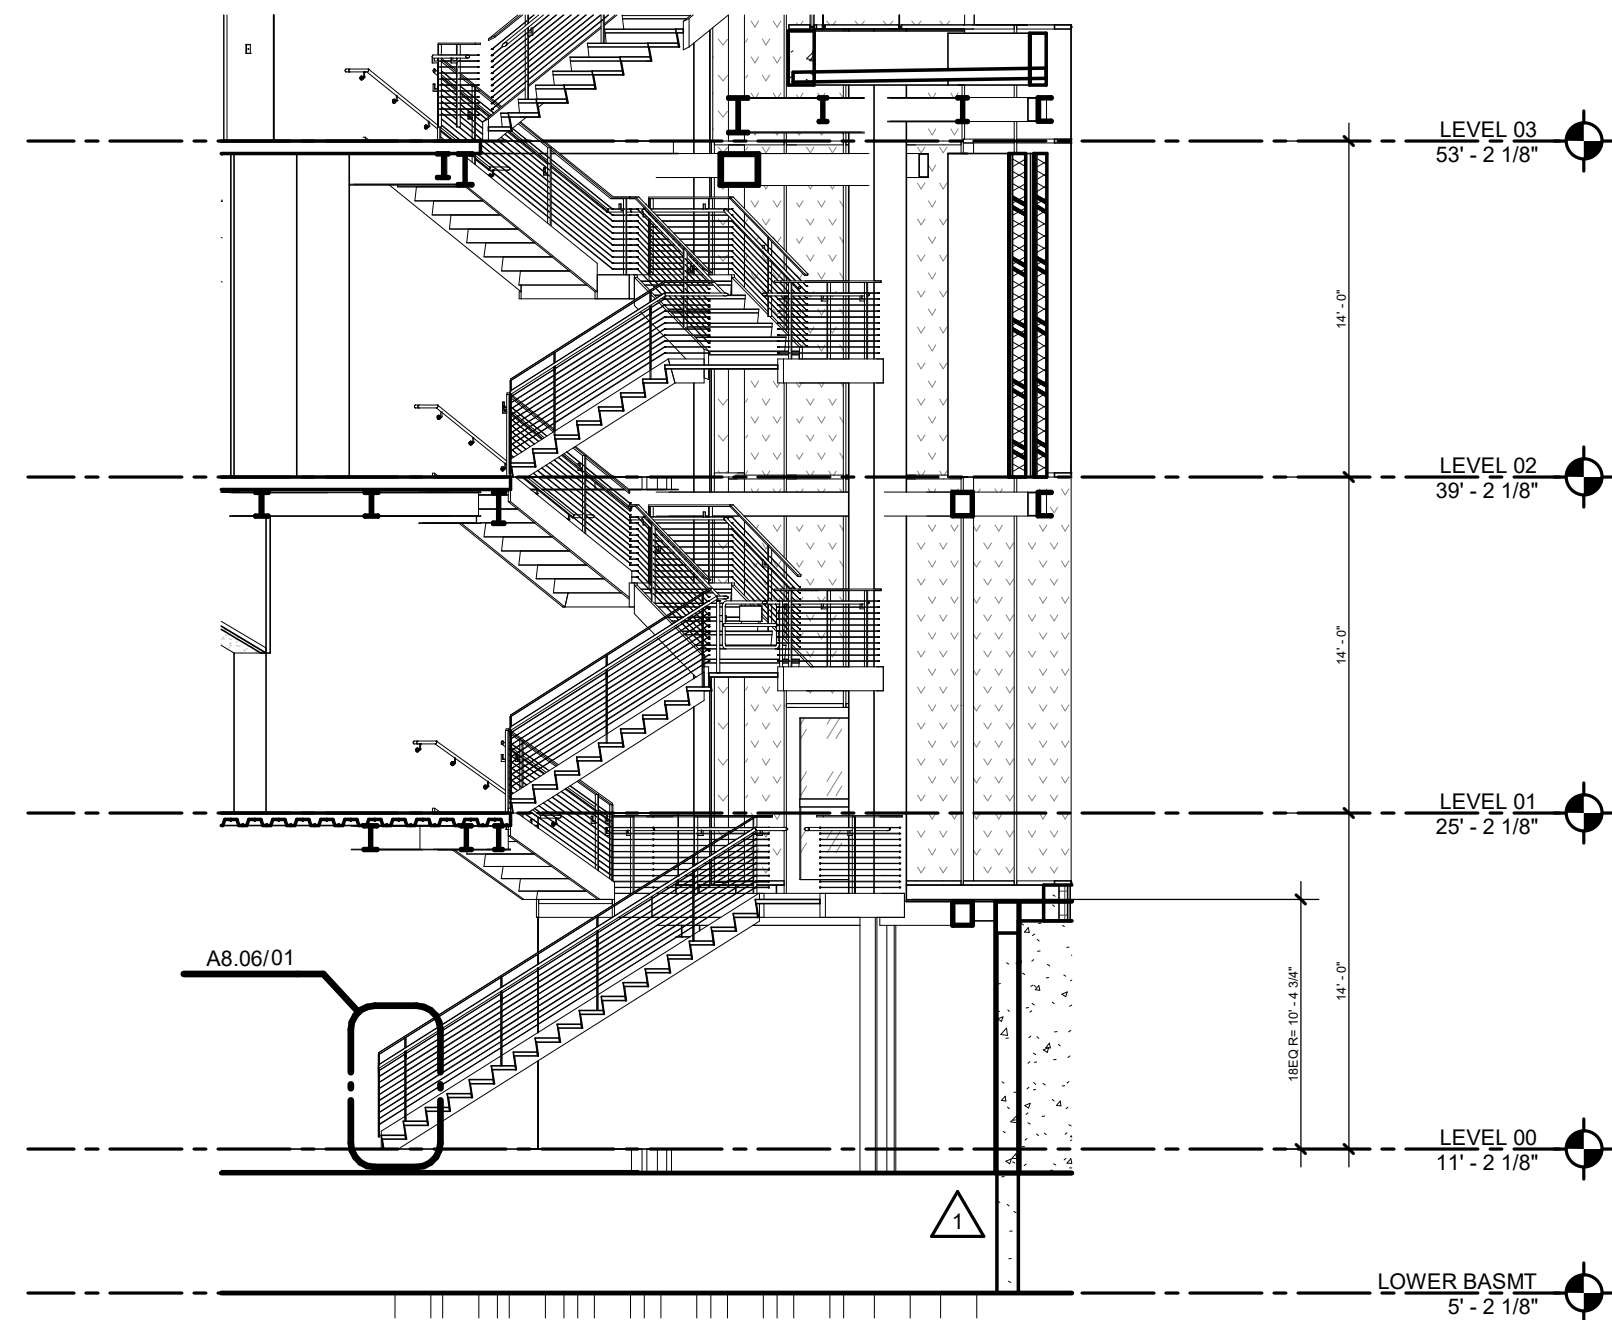

03 SE STAIR SECTION 03
1/8" = 1'-0"

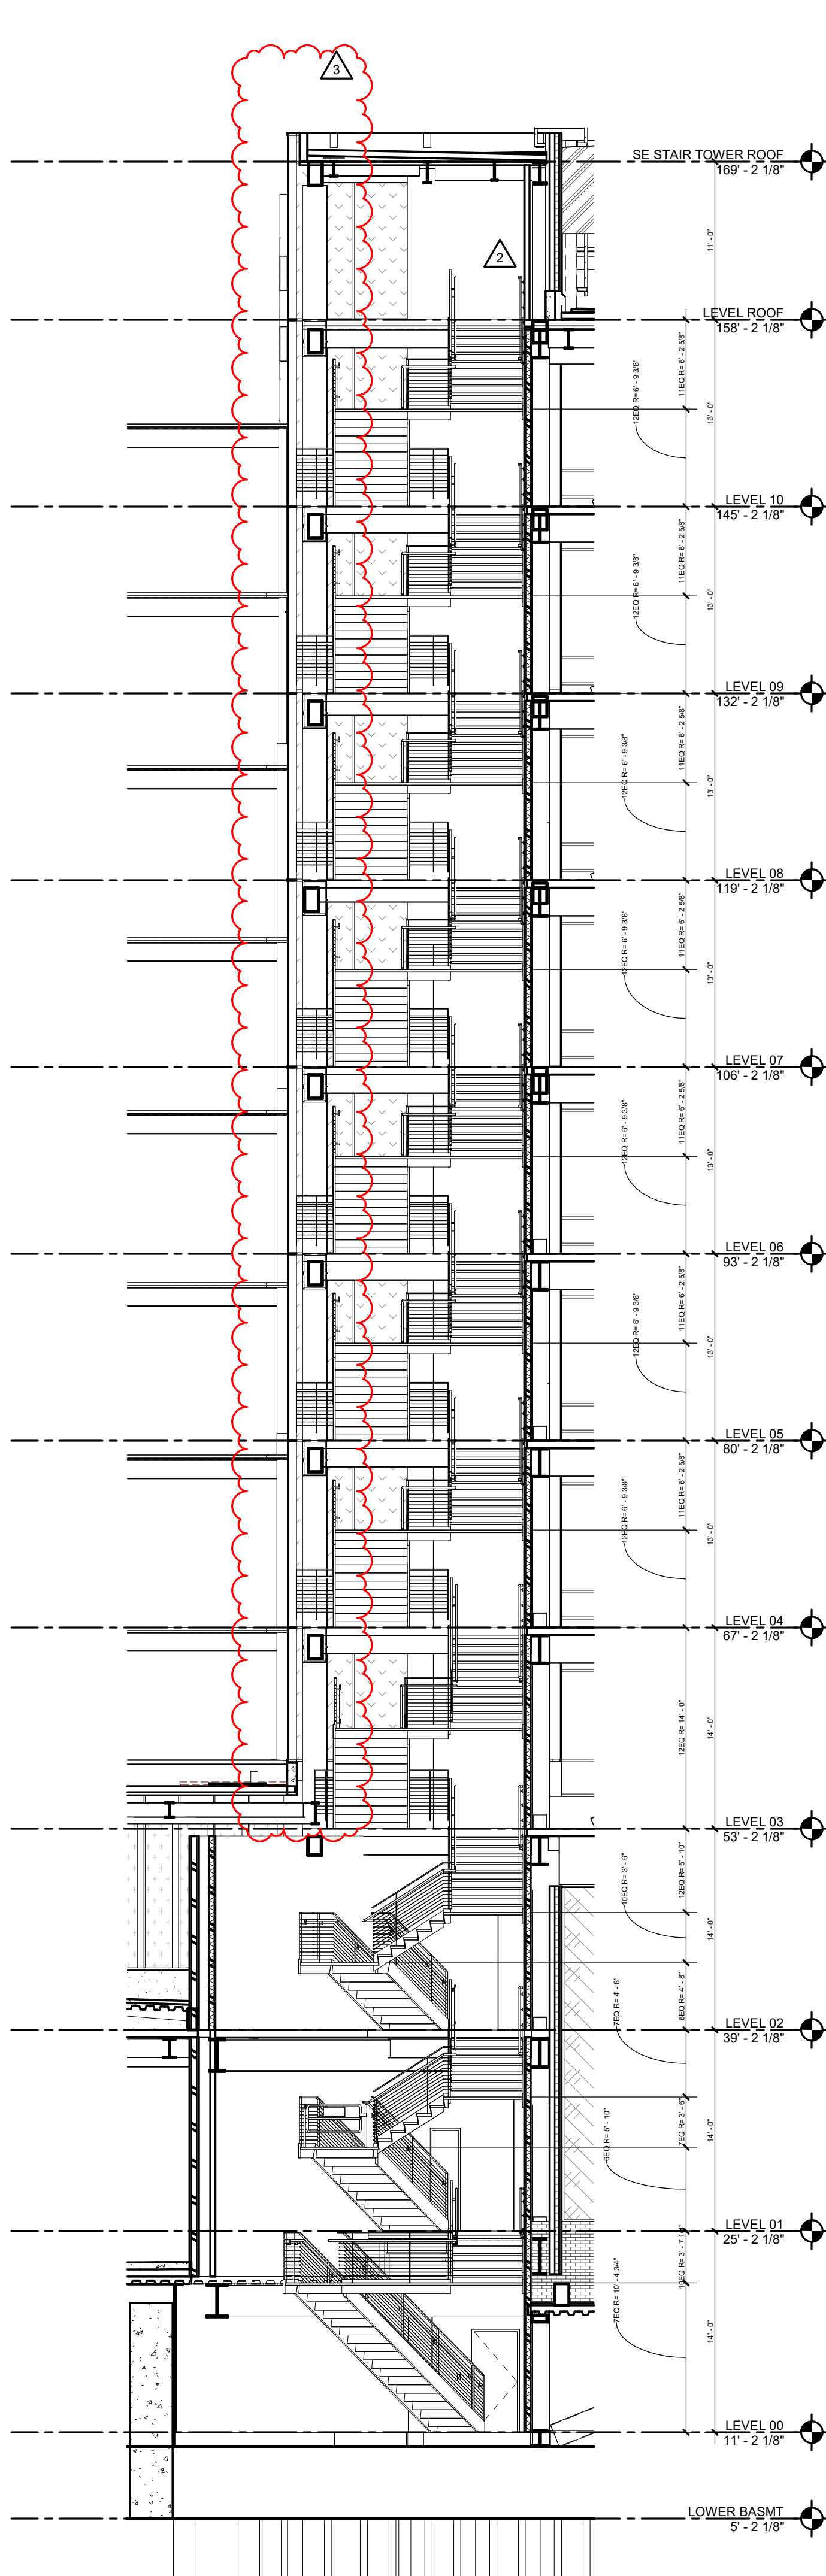

02 SE STAIR SECTION 02
1/8" = 1'-0"

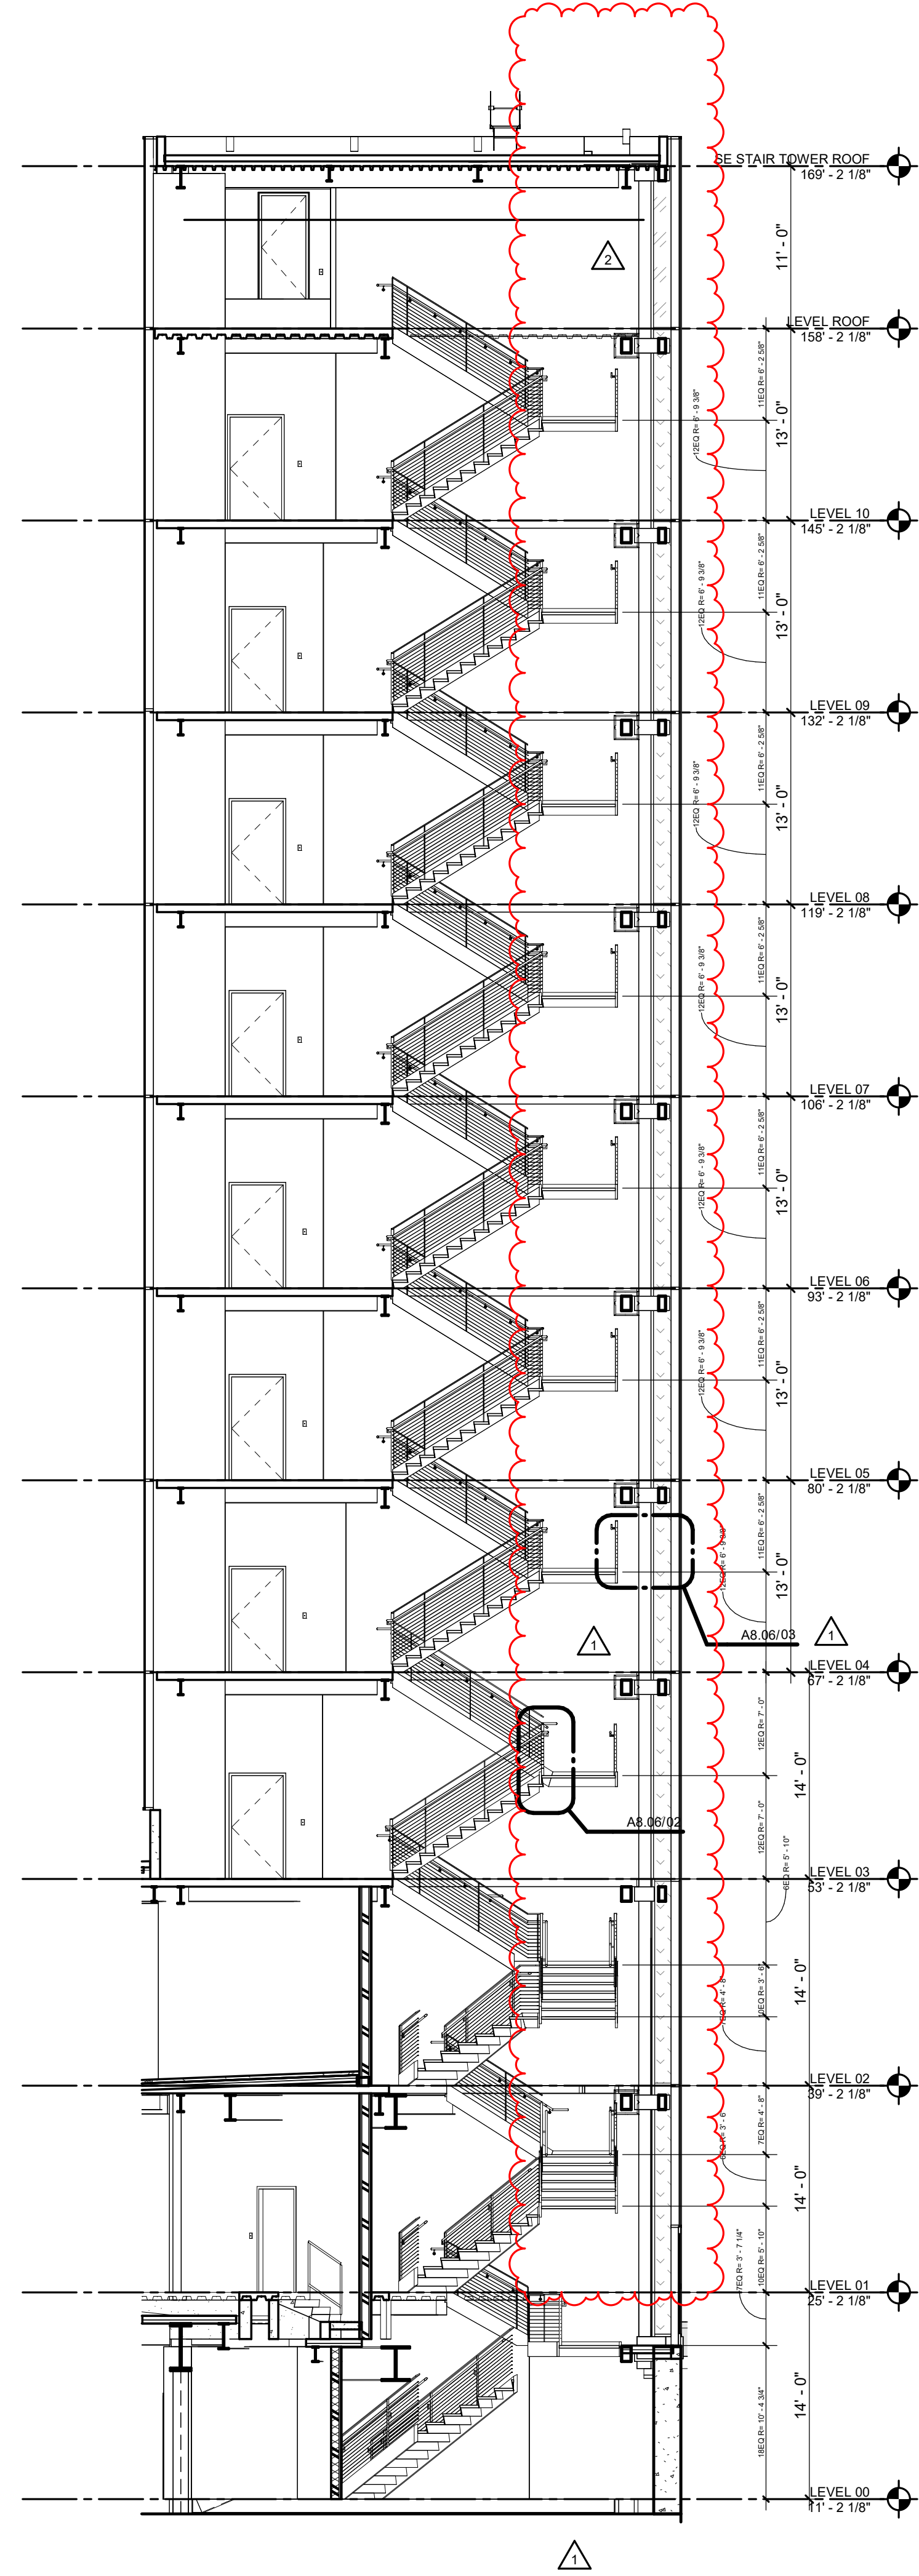

01 SE STAIR SECTION 01
1/8" = 1'-0"


RESERVE FOR DCA STAMP



ARCHITECT
HKS, P.C.
1250 I (EYE) STREET NW, SUITE 600
WASHINGTON, DC 20005
ASSOCIATE ARCHITECT / INTERIOR DESIGNER
ARRAY
1 WEST ELM STREET, SUITE 500
CONSHOHOCKEN, PA 19428
STRUCTURAL ENGINEER
O'DONNELL & NACCARATO
701 MARKET ST., #6000
PHILADELPHIA, PA 19106
MEP-FP / LOW VOLTAGE ENGINEER
BR-A CONSULTING ENGINEERS
2401 WALNUT ST SUITE 701
PHILADELPHIA, PA 19103
HIGHLAND ASSOCIATES
102 HIGHLAND AVE
CLARKS SUMMIT, PA 18411



OWNER
COOPER UNIVERSITY HEALTHCARE
1 COOPER PLAZA
CAMDEN, NJ 08103
PROJECT MANAGER
PURE PM
2026 RICHMOND STREET
PHILADELPHIA, PA 19134
CIVIL ENGINEER / LANDSCAPE
LANGAN
1818 MARKET STREET, SUITE 3300
PHILADELPHIA, PA 19103
SEAL & SINGATURE

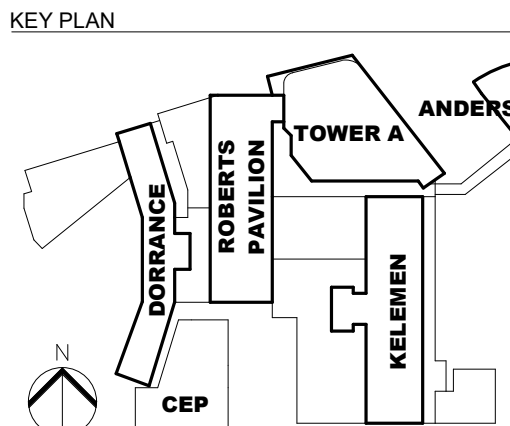

NO.	DESCRIPTION	DATE
1	BULLETIN #4	04/28/2025
2	RFI 0312	08/11/2025
3	RFI 0416	11/14/2025

HKS PROJECT NUMBER
25695.100
DATE
10/15/2024
ISSUE
CORE & SHELL PERMIT SET
SHEET TITLE
STAIR PLANS AND SECTIONS

SHEET NO.

A8.03

BUILDING PERMIT NUMBER: 1111